FL_PI10_01 - PLANTA GENERAL E IMPLANTACIÓN, ZONAS Y SUPERFICIES

Calle al norte: administración y servicios al personal al norte de la nave (croquis del usuario). Cada m² de la nave tiene código y nombre (verificado).

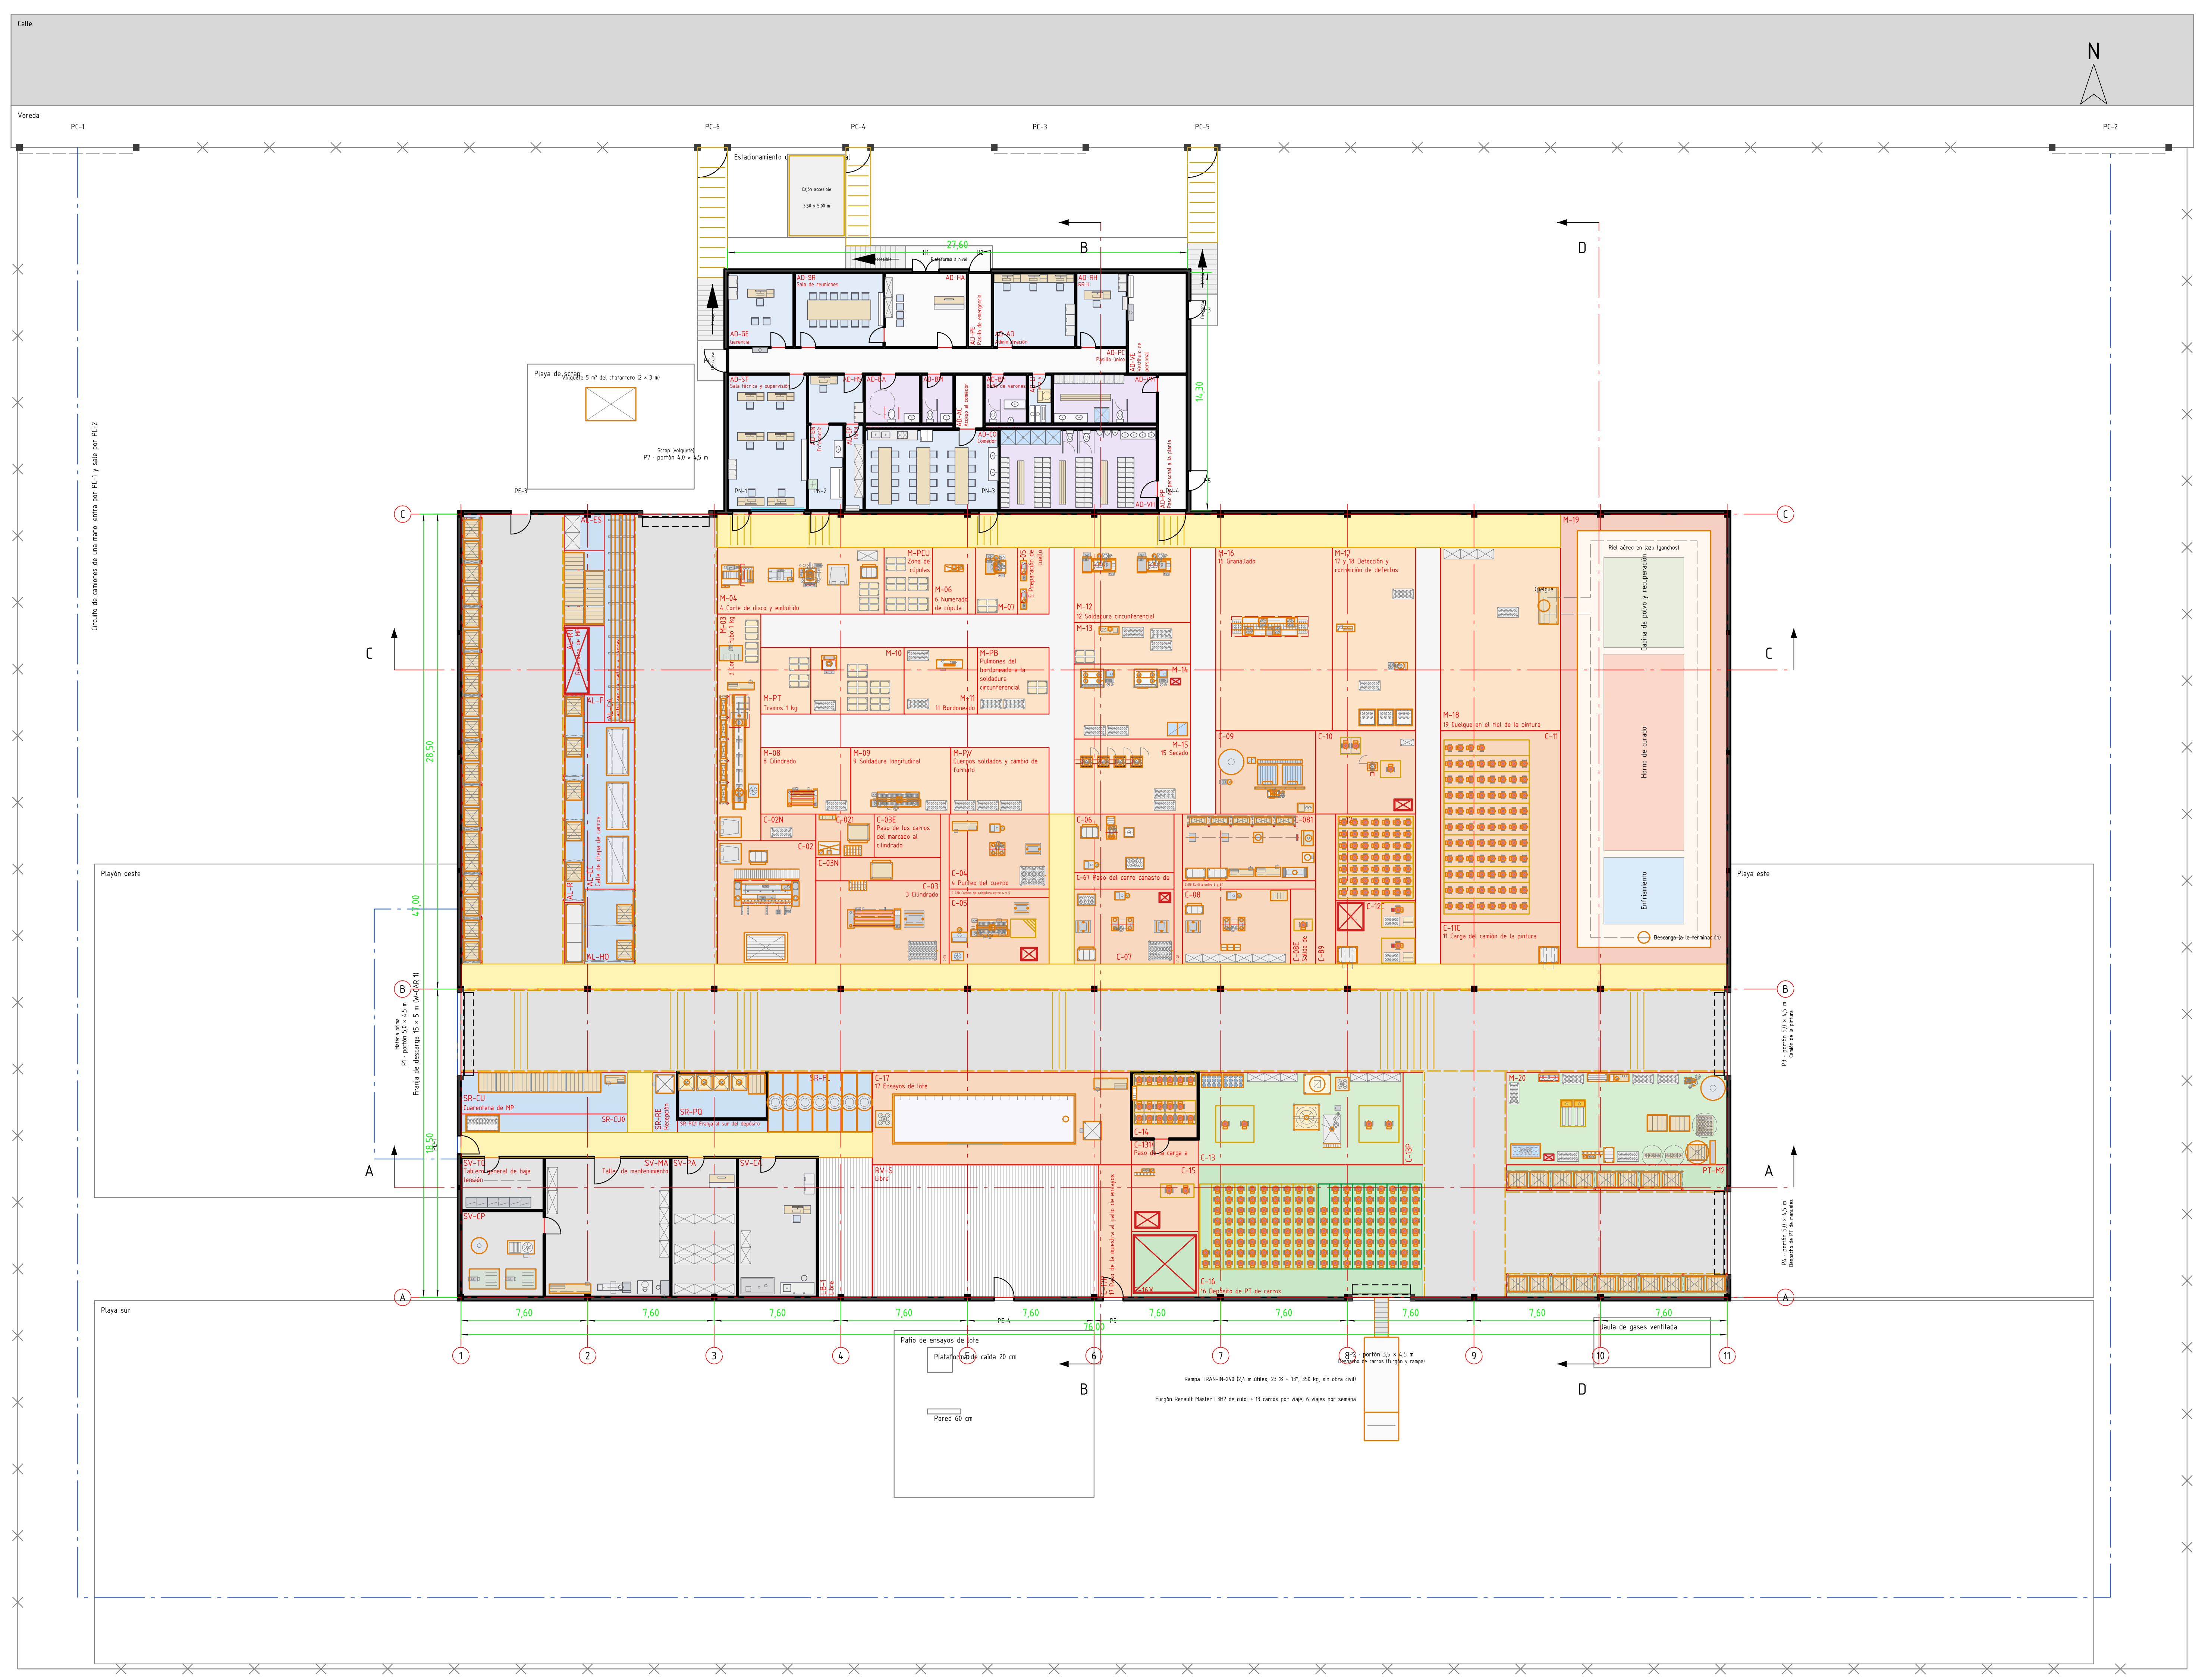

Zonas de la nave y del anexo (m² del plano y m² que pide la fuente)

Código	Zona	m²	Fuente
AL-R1	Rack selectivo R1, 4 niveles	29,7	-
AL-W	Franja del muro oeste	2,7	-
AL-AB	Estacionamiento de los carros de abastecimiento	4,4	-
AL-RC	Racks de carros	14,9	14,7
AL-RT	Retenidos de MP	10,0	6,0
AL-PV	Pilas de pallets vacíos	10,8	-
AL-ES	Estantería de cajas	5,3	-
AL-HO	Rack de chapas por espesor	13,5	-
AL-CC	Calle de chapa de carros	30,0	20,0
AL-F	Franja detrás del cantiléver	2,0	-
AL-CA	Cantiléver de caños y barras	22,5	-
SR-CU	Cuarentena de MP	25,0	25,0
SR-CU0	Jaula de tubos de gas y paso detrás de la cuarentena	11,0	-
SR-RE	Recepción	5,4	-
SR-PQ	Depósito de polvo químico y pintura en polvo	15,1	-
SR-PQ1	Franja al sur del depósito de polvo	4,3	-
SR-FL	Bobinas de fleje	22,7	22,0
M-04	4 Corte de disco y embutido	40,0	26,0
M-PCU	Zona de cúpulas	11,6	-
M-06	6 Numerado de cúpula	10,4	2,3
M-07	7 Soldadura del cuello a la cúpula	10,0	5,3
M-05	5 Preparación de cuello	7,6	4,5
M-03	3 Corte de tubo 1 kg	35,4	25,5
M-PT	Tramos 1 kg	12,0	-
M-10	10 Encastre de fondo y zona de fondos	22,4	3,6
M-11	11 Bordoneado	17,6	3,6
M-PB	Pulmones del bordoneado a la soldadura circunferencial	17,2	-
M-08	8 Cilindrado	21,6	7,3
M-09	9 Soldadura longitudinal	24,0	8,4
M-PV	Cuerpos soldados y cambio de formato	23,6	-
M-12	12 Soldadura circunferencial	31,5	17,5
M-13	13 Control de espesor	17,5	2,3
M-14	14 Prueba hidráulica	31,5	14,1
M-15	15 Secado	31,5	6,0
M-16	16 Granallado	77,0	27,4
M-17	17 y 18 Detección y corrección de defectos	55,0	9,2
M-18	19 Cuelgue en el riel de la pintura	79,2	-
M-19	19 Pintura en polvo + horno	270,0	270,0
C-13	13 Carga, armado y presurización de carros	68,3	60,0
C-13P	Paso de los carros pintados y de los cilindros a la carga y al depósito 16	6,7	-
M-20	20 a 25 Terminación de manuales	73,5	47,0
C-02	2 Corte de chapa	43,7	44,0
C-02N	Salida de desarrollos de la guillotina a manuales	5,3	-
C-021	2.1 Marcado del cuerpo	9,1	9,0
C-03	3 Cilindrado	37,5	35,0
C-03N	Paso de la mesa móvil del marcado al cilindrado	10,5	-
C-03E	Paso de los carros del marcado al cilindrado	10,4	-
C-05	5 Soldadura longitudinal	24,0	22,0
C-04	4 Punteo del cuerpo	27,0	27,0
C-45	Cortina de soldadura entre 3 y 4/5	4,5	-
C-45b	Cortina de soldadura entre 4 y 5	3,0	-
C-07	7 Armado y soldadura circunferencial	27,0	27,0
C-06	6 Soldadura de cupla en la cúpula	21,0	16,0

Código	Zona	m²	Fuente
C-67	Paso del carro canasto de cúpulas de 6 a 7	6,0	-
C-08	8 Soldadura de accesorios	29,2	29,0
C-081	8.1 Fabricación de accesorios	32,0	32,0
C-78	Cortina de soldadura entre 7 y 8	4,5	-
C-88	Cortina entre 8 y 8.1	4,0	-
C-08E	Salida de los carros sobre su juego provisorio	6,8	-
C-09	9 Prueba hidráulica de carros	30,0	22,0
C-10	10 Secado de carros y espera de los mojados	30,0	7,5
C-89	Paso de los carros del puesto 8 a la prueba hidráulica	10,8	-
C-12C	12 Recepción de pintados	18,2	-
C-12	12 Pulmón de pintados	25,0	24,5
C-11C	11 Carga del camión de la pintura	18,0	-
C-11	11 Pulmón de despacho a la pintura tercerizada	82,8	42,0
C-17	17 Ensayos de lote	86,3	70,0
C-1314	Paso de la carga a la sala de pérdidas, a los ensayos y al etiquetado	6,2	-
C-14	14 Sala del ensayo de pérdidas	16,0	14,2
C-17P	17 Paso de la muestra al patio de ensayos	15,9	-
C-15	15 Etiquetado e inspección final	16,0	9,0
C-16X	16 Rechazados	15,8	11,5
C-16	16 Depósito de PT de carros	107,3	72,0
PT-M	Depósito de PT unificado	17,9	-
PT-M2	Depósito de PT unificado	20,5	-
SV-CP	Sala de compresores y secador de aire	26,0	-
SV-TG	Tablero general de baja tensión	16,0	-
SV-MA	Taller de mantenimiento	63,8	-
SV-PA	Pañol de herramientas y repuestos	33,6	-
SV-CA	Laboratorio de control de calidad	40,3	-
LB-1	Libre	27,7	-
RV-S	Libre	107,7	-
AD-GE	Gerencia	18,0	-
AD-SR	Sala de reuniones	24,3	-
AD-HA	Hall de recepción y espera de visitas	22,5	-
AD-PE	Pasillo de emergencia	6,8	-
AD-AD	Administración	22,5	-
AD-RH	RRHH	14,0	-
AD-VE	Vestíbulo de personal	22,0	-
AD-PC	Pasillo único	38,4	-
AD-ST	Sala técnica y supervisión	39,4	-
AD-HS	Seguridad e Higiene	10,2	-
AD-EN	Enfermería	11,4	-
AD-EP	Pañol de EPP	6,2	-
AD-BA	Baño para personas con discapacidad	10,2	-
AD-BM	Baño de mujeres	6,0	-
AD-AC	Acceso al comedor	5,9	-
AD-BH	Baño de varones	7,8	-
AD-LI	Limpieza y termotanque	4,5	-
AD-VM	Vestuario y sanitarios de mujeres	18,9	-
AD-CO	Comedor	39,7	-
AD-VH	Vestuario y sanitarios de varones	46,5	-
AD-PP	Paso de personal a la planta	14,8	-
AD-PL1	Plenum sanitario	1,6	-
AD-PL2	Plenum sanitario	3,1	-

Portones de la nave y del predio

Portón	Uso	Ancho (m)
P1	Materia prima: del playón oeste al pasillo principal	5,0
P2	Despacho de carros: furgón Renault Master L3H2 y rampa TRAN-IN-240	3,5
P3	Camión de la pintura: carros secos (11) y pintados (12)	5,0
P4	Despacho de PT de manuales (pasillo de los racks)	5,0
P7	Scrap: del pasillo AL-A a la playa con volquete	4,0
PC-1	Entrada de camiones, 7,0 m (criterio: semirremolque)	7,0
PC-2	Salida de camiones, 7,0 m (circuito de una mano)	7,0
PC-3	Estacionamiento, 5,5 m	5,5
PC-4	Peatonal: visitas, gerencia y oficinas	1,5
PC-5	Peatonal: operarios (ingreso lateral este)	1,8
PC-6	Peatonal: supervisión, PCP, calidad y HyS (oeste)	1,8

Superficies por destino

Destino	m²	% de la nave
Almacén de MP y recepción	229,3	6,4
Manuales 1 a 10 kg	576,6	16,1
Pintura	270,0	7,6
Terminación de manuales	148,5	4,2
Carros 25 a 100 kg	660,6	18,5
Depósitos de producto terminado	161,5	4,5
Servicios técnicos (mantenimiento, calidad, aire, energía)	179,8	5,0
Libre / reserva	135,4	3,8
Pasillos y sendas	1.210,3	33,9
TOTAL NAVE (76,0 × 47,0 m)	3.572,0	100,0
Anexo de administración y servicios (27,6 × 14,3 m)	394,7	-

Referencias

🟦	Almacén de MP y recepción
🟧	Manuales 1 a 10 kg
🟥	Pintura
🟩	Terminación de manuales
🟧	Carros 25 a 100 kg
🟩	Depósitos de producto terminado
⬜	Servicios técnicos (mantenimiento, calidad, aire, energía)
🟦	Oficinas
🟪	Vestuarios y sanitarios
▨	Libre / reserva
⬜	Carril del autoelevador (5,0 m)
🟨	Senda peatonal demarcada
⬜	Pasillo de operarios y carros a mano

Criterios

Nave de 76,0 × 47,0 m, 10 vanos de 7,6 m; pórticos de 18,5 + 28,5 m con la fila de columnas en el borde norte del carril del autoelevador (ninguna columna dentro de un carril).
Pasillo principal: carril de 5,0 m (Heli CPCD50, W-CAR) + senda de 1,5 m con baranda y cruces.
Almacén con dos pasillos de 5,0 m (AL-A junto a las máquinas de corte, AL-B entre racks).
Portones de la nave: P1 MP 5,0 m (oeste, con la franja de descarga de 15 × 5 m y la cuarentena), P3 camión de la pintura 5,0 m y P4 PT de manuales 5,0 m (este), P2 despacho de carros 3,5 m con rampa y furgón (sur), P7 scrap 4,0 m (norte del almacén, playa con volquete); P5 patio de ensayos; PE emergencia.
Predio con cerco: PC-1 entrada y PC-2 salida de camiones (circuito de una mano), PC-3 estacionamiento y PC-4 a PC-6 accesos peatonales del croquis de oficinas. Cortes A-A a D-D en FL_PI10_06.
Carros: reglas del Word de carros con la demanda pico 2035 (X-CAR: 14 recipientes por día, 70 por semana): 84 en el pulmón de despacho, 49 pintados, 17 en la sala de pérdidas, 74 retenidos, 70 liberados y 23 rechazados. PT unificado de manuales y carros contra el muro sur, debajo de la terminación compartida (carga y presurización de manuales y carros), que queda debajo de la pintura, cruzando el pasillo; racks de manuales de 90 posiciones (70 de PT y 17 revendidos de X-ALM).
Prueba hidráulica y secado de carros al lado de los de manuales; granallado, detección y cuelgue arriba, en la fila de la cabina de la pintura (sin reservas). Lo que sobra de la nave queda en RV-S y LB-1.

	Fecha	Nombre
Dibujó	16/10/26	Claude Code
Revisó		
Aprobó		

Escala: 1:200
Método de proyección: ISO E
Unidades: Cotas en m
Formato: A0
Propietario: FLAMA S.A.
Denominación: Planta general e implantación
Layout 2035 v10 - zonas codificadas y áreas
Tipo de documento: Plano de planta
Reemplaza a / Reemplazado por: -
Material: -
Edición: 0
Fecha de emisión: 16/10/2026
Hoja: 1 / 6
Idioma: es
N° de plano: FL_PI10_01