FL_PI10_03 - CIRCULACIÓN, FLUJOS DE MATERIALES Y RECORRIDOS DEL PERSONAL

Carriles del autoelevador, sendas peatonales y pasillos de operarios con su ancho; flujo de MP, de semielaborado y de PT; hilos del personal desde los vestuarios.

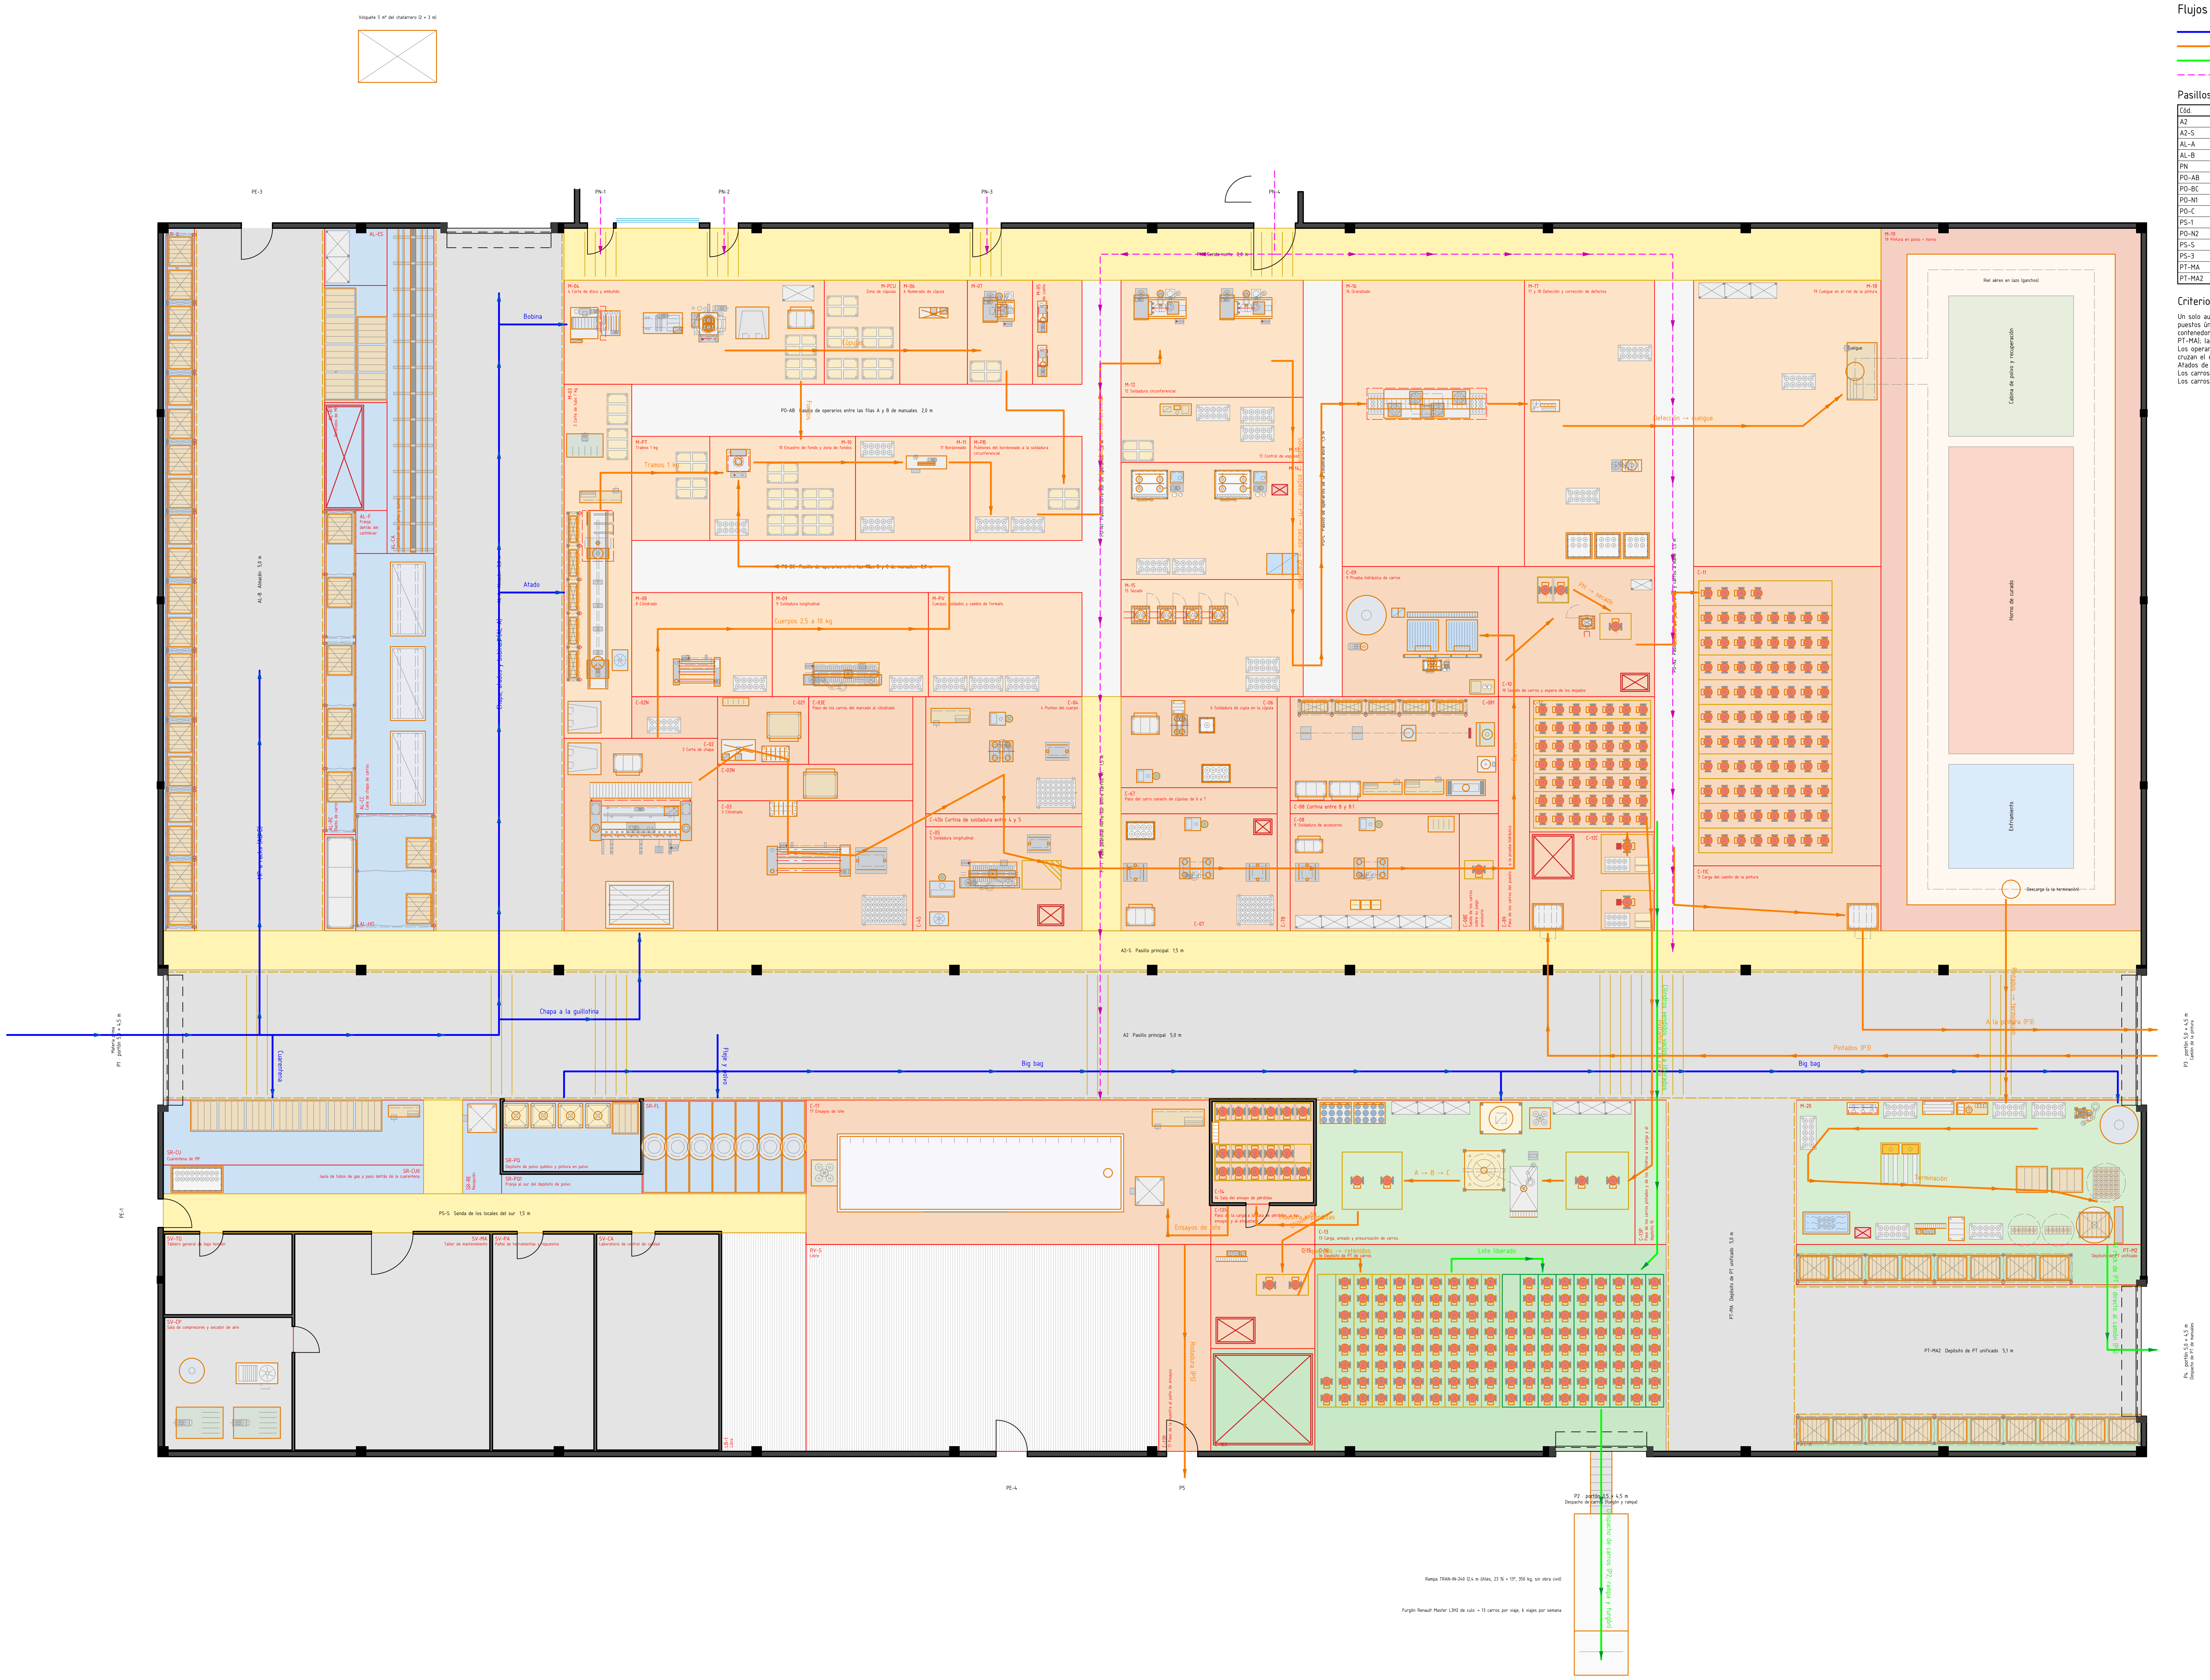
Volquete 5 m³ del chatarrero (2 × 3 m)
Materia prima
P1 · portón 5,0 × 4,5 m
Cuarentena
Chapa a la guillotina
Fleje y polvo
Big bag
Bobina
Atado
AL-HO
SR-CU
Cuarentena de MP
SR-CU0
Jaula de tubos de gas y paso detrás de la cuarentena
SR-RE
Recepción
SR-PQ
Depósito de polvo químico y pintura en polvo
SR-PQ1
Franja al sur del depósito de polvo
SR-FL
C-17
17 Ensayos de lote
C-07
C-78
C-08E
Salida de los carros sobre su juego provisorio
C-89
Paso de los carros del puesto
C-11C
11 Carga del camión de la pintura
Descarga (a la terminación)
A2-S Pasillo principal 1,5 m
A2 Pasillo principal 5,0 m
Cilindros vendidos vacíos a llenados
Pintados (P3)
A la pintura (P3)
Pintados → terminación
P3 · portón 5,0 × 4,5 m
Camión de la pintura
C-14
14 Sala del ensayo de pérdidas
A → B → C
M-20
Terminación
PT-MA2 Depósito de PT unificado 5,1 m
PT-MA Depósito de PT unificado

Referencias

- ▨ Carril del autoelevador (5,0 m)
- 🟨 Senda peatonal demarcada
- ☐ Pasillo de operarios y carros a mano

Flujos

- → MP: materia prima (azul)
- → SE: semielaborado (naranja)
- → PT: producto terminado (verde)
- - - → Hilos de personal (magenta)

Pasillos (m)

Cód.	Pasillo	Ancho	Largo	Uso
A2	Pasillo principal	5,0	76,0	Autoelevador
A2-S	Pasillo principal	1,5	76,0	Peatonal
AL-A	Almacén	5,0	27,0	Autoelevador
AL-B	Almacén	5,0	27,0	Autoelevador
PN	Senda norte	2,0	50,6	Peatonal
PO-AB	Pasillo de operarios entre las filas A y B de manua.	2,0	17,3	Operarios
PO-BC	Pasillo de operarios entre las filas B y C de manua.	2,0	17,3	Operarios
PO-N1	Pasillo norte-sur de operarios	1,5	16,0	Operarios
PO-C	Pasillo de operarios de la columna este	1,5	16,0	Operarios
PS-1	Paso peatonal norte-sur entre carros 4/5 y 6/7	1,5	9,0	Peatonal
PO-N2	Pasillo norte-sur de operarios y carros a mano	1,5	25,0	Operarios
PS-S	Senda de los locales del sur	1,5	24,7	Peatonal
PS-3	Paso peatonal de la senda sur al pasillo principal	1,5	3,6	Peatonal
PT-MA	Depósito de PT unificado	5,0	13,5	Autoelevador
PT-MA2	Depósito de PT unificado	5,1	13,2	Autoelevador

Criterios de circulación

Un solo autoelevador (Heli CPCD50, W-MAN y W-CAR): circula sólo por A2, AL-A y AL-B (5,0 m) y entra a los puestos únicamente donde la máquina mira al carril: mesa elevadora, cajón del atado, desbobinador, contenedores de scrap (a P7), big bags (terminación y carro 13), envolvedora y racks de PT (pasillo PT-MA); las tarimas de los carros 11 y 12 las lleva por el pasillo principal a P3.
Los operarios caminan por las sendas (amarillas) y por los pasillos de operarios de 1,5 a 2,0 m; cruzan el carril sólo por los cruces demarcados de la baranda.
Atados de 6 m: se mueven colgados de la pluma (W-MAN 1 y 2), a lo largo del pasillo.
Los carros de manuales (FCHP y de 12 cajones) se empujan a mano entre puestos pegados (W-MAN).
Los carros (extintores rodantes) ruedan sobre su juego provisorio desde el puesto 8 (W-CAR).

	Fecha	Nombre
Dibujó	16/10/26	Claude Code
Revisó		
Aprobó		

Escala
1:100

Método de proyección
ISO E

Unidades
Cotas en m

Formato
A0

Propietario
FLAMA S.A.

Denominación
Circulación y flujos
Layout 2035 v10 – pasillos, materiales y personas

Tipo de documento
Plano de circulación

Reemplaza a / Reemplazado por
-

Material
-

Edición
0

Fecha de emisión
16/10/2026

Hoja
3 / 6

Idioma
es

N° de plano
FL_PI10_03