
FL_PI10_05 – ADMINISTRACIÓN Y SERVICIOS AL PERSONAL (ANEXO NORTE)

Disposición y marcas del croquis del usuario (27,6 × 14,3 m, calle al norte, planta al sur): accesos, rampas, relojes, ventanillas, matafuegos, baranda con cruces y los 12 circuitos del personal.

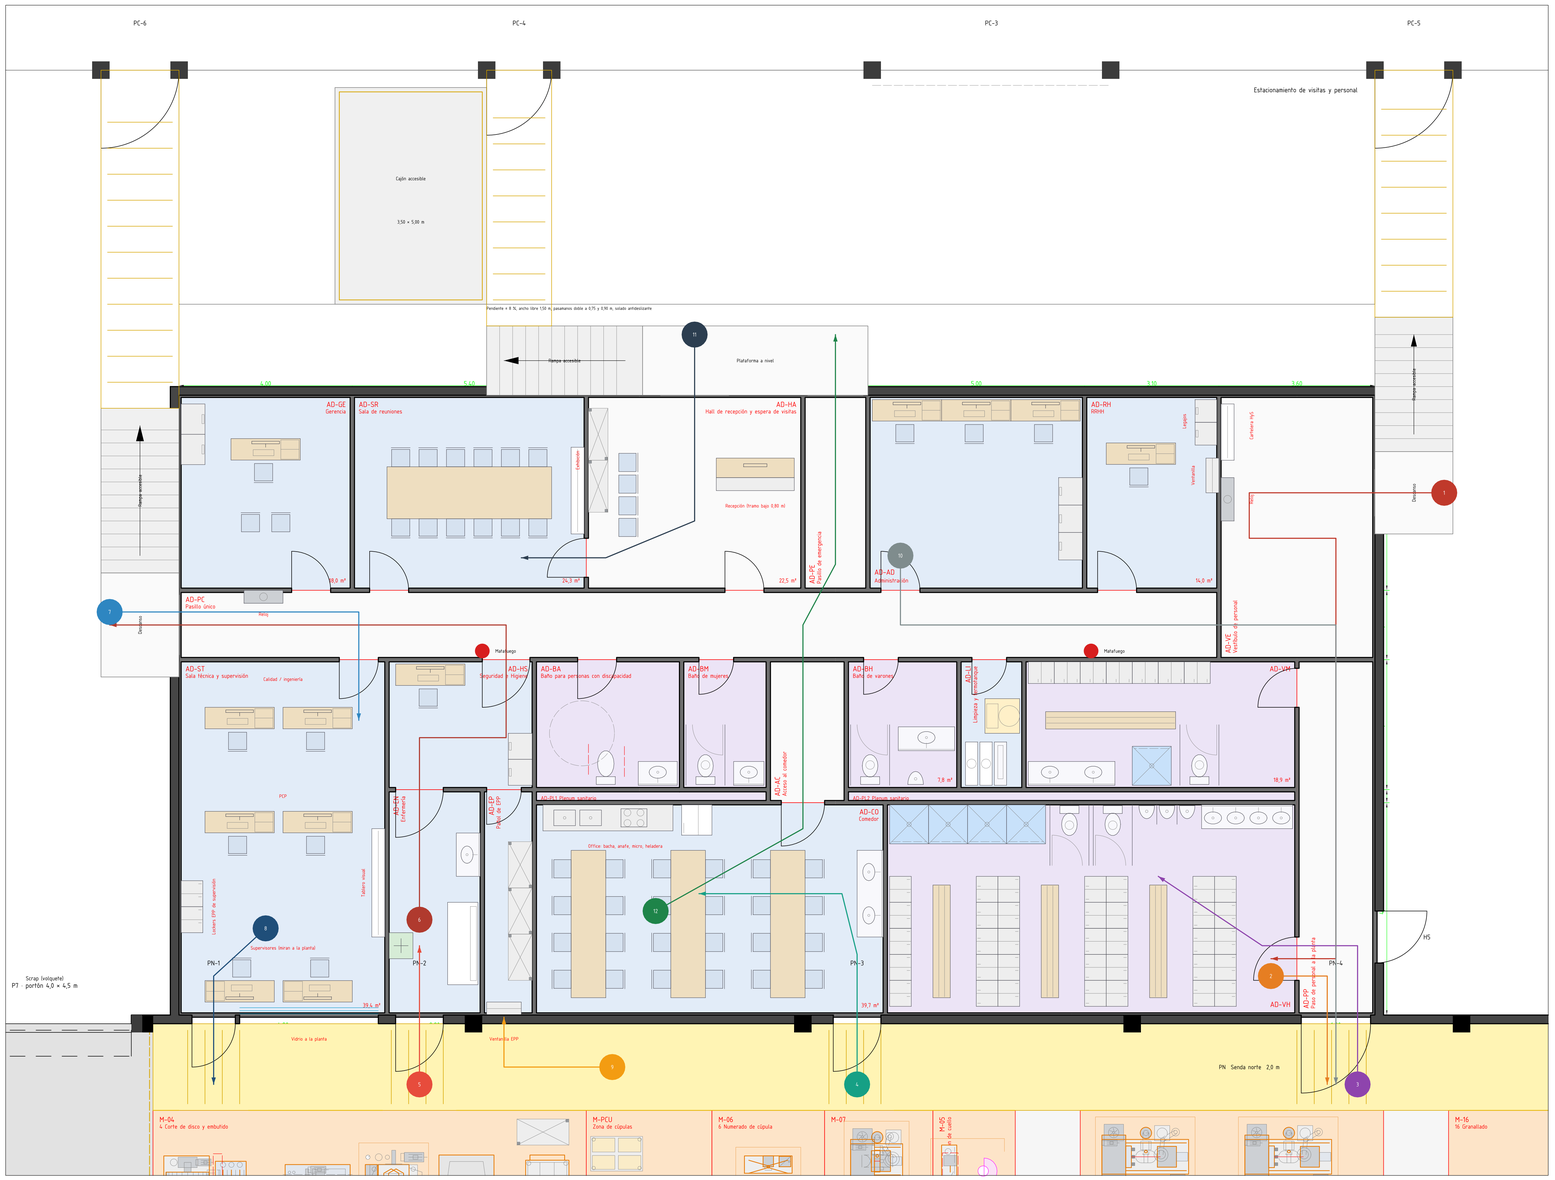

Circuitos del personal y distancias medidas sobre el plano, a eje de paso

N.º	Circuito (croquis del usuario)	Largo en el plano
1	Llegada del operario: ingreso lateral este → reloj → paso de personal → vestuario	≈ 19 m
2	Vestuario → planta (sale por el lado de la planta)	≈ 4 m
3	Baño durante el turno: planta → inodoro u orinal	≈ 8 m
4	Almuerzo: planta → cruce → lavamanos → comedor	≈ 8 m
5	Accidente: planta → cruce → enfermería (puerta de 1,10 m)	≈ 3 m
6	Ambulancia: enfermería → HyS → salida oeste	≈ 18 m
7	Llegada de supervisión, PCP y calidad: ingreso oeste → reloj → sala técnica	≈ 8 m
8	Supervisores → planta (puerta directa y cruce)	≈ 4 m
9	Retiro de EPP: senda → ventanilla del pañol	≈ 4 m
10	Oficinas → planta (ocasional): pasillo → paso de personal	≈ 22 m
11	Visitas, gerencia y oficinas: frente → hall → reuniones (no cruzan con operarios)	≈ 8 m
12	Evacuación central: comedor → acceso → pasillo de emergencia → calle	≈ 15 m

N

0 1 2 3 4 5 m

Escala gráfica 1:50

Dotación

Dotación 2035: sin recargas	Personas	Fuente
Turno mañana: operarios de producción	30	X-DT Dotación: 46 − 16 de recargas
Turno mañana: encargado de turno	1	X-DT Servicios y Oficinas fila 35
Turno mañana: oficina (jefe de planta, calidad, ventas y cobranzas, compras, PCP)	5	X-DT Filas 21 a 26, sin «atención de recargas»
Turno tarde: operarios de producción	6	X-DT Dotación fila 104
Turno tarde: encargado y administrativo	2	X-DT Filas 27 y 39
Turno más numeroso (mañana): 32 varones y 4 mujeres	36	10 % de mujeres, redondeado arriba (X-DT)
Personal de planta en los dos turnos (armarios): 34 varones y 4 mujeres	38	Operarios + encargados

Sanitarios y vestuarios (Dec. 351/79 art. 49, fórmulas X-DT)

Vestuarios de planta y comedor	Pide H	Hay H	Pide M	Hay M
Inodoros	2	2	1	1
Orinales	3	3	–	–
Lavabos	4	4	1	2
Duchas	3	4	1	1
Armarios dobles	34	35	4	7
Lugares del comedor (2 tandas)	18	24		

Además: baño accesible (Ley 24.314) y baños de mujeres y de varones de oficinas, del croquis.
Accesos separados (croquis): visitas, gerencia y oficinas por el hall (H1, rampa norte y plataforma a nivel, cajón accesible de 3,50 × 5,00 m); operarios por el vestíbulo lateral este (H3, rampa, reloj) → vestuarios → paso de personal → planta (PN-4); supervisión, PCP, calidad y HyS por el ingreso oeste (H4, rampa y reloj). Sala técnica (PN-1), enfermería (PN-2, 1,10 m) y comedor (PN-3) con puerta directa a la senda norte; pañol de EPP y RRHH con ventanilla. Pasillo de emergencia de 1,5 m a la calle (H2) y salida del paso de personal (HS); las puertas exteriores abren hacia afuera. Dos matafuegos en el pasillo único. Senda norte con baranda y cruces pintados frente a cada puerta a la planta. Plenum sanitario único.
Rampas: pendiente ≤ 8 %, ancho libre 1,50 m, pasamanos doble a 0,75 y 0,90 m, solado antideslizante. Portones del predio PC-4 a PC-6: accesos peatonales del croquis.

	Fecha	Nombre
Dibujó	16/10/26	Claude Code
Revisó		
Aprobó		

Escala: 1:50 · Método de proyección: ISO E · Unidades: Cotas en m · Formato: A0

Preparado: FLAMA S.A.

Denominación: Administración y servicios al personal

Layout 2035 v10 – croquis del usuario y dotación de la X-DT

Tipo de documento: Plano de detalle

Reemplaza a / Reemplazado por: –

Material: –

Edición: 0 · Fecha de emisión: 16/10/2026

Hoja: 5 / 6 · Idioma: es

N.º de plano: FL_PI10_05