


FL PI_05 - SERVICIOS AL PERSONAL, OFICINAS Y APOYO A LA LÍNEA

Todo en planta baja (sin entrepiso). Circuito del personal, vestuarios con 1 locker por empleado y sanitarios (Dec. 351/79 arts. 49-50), accesibilidad (Ley 24.314), supervisor y PCP sobre la línea.


DETALLE 1 - SERVICIOS Y ADMINISTRACIÓN - 1:50

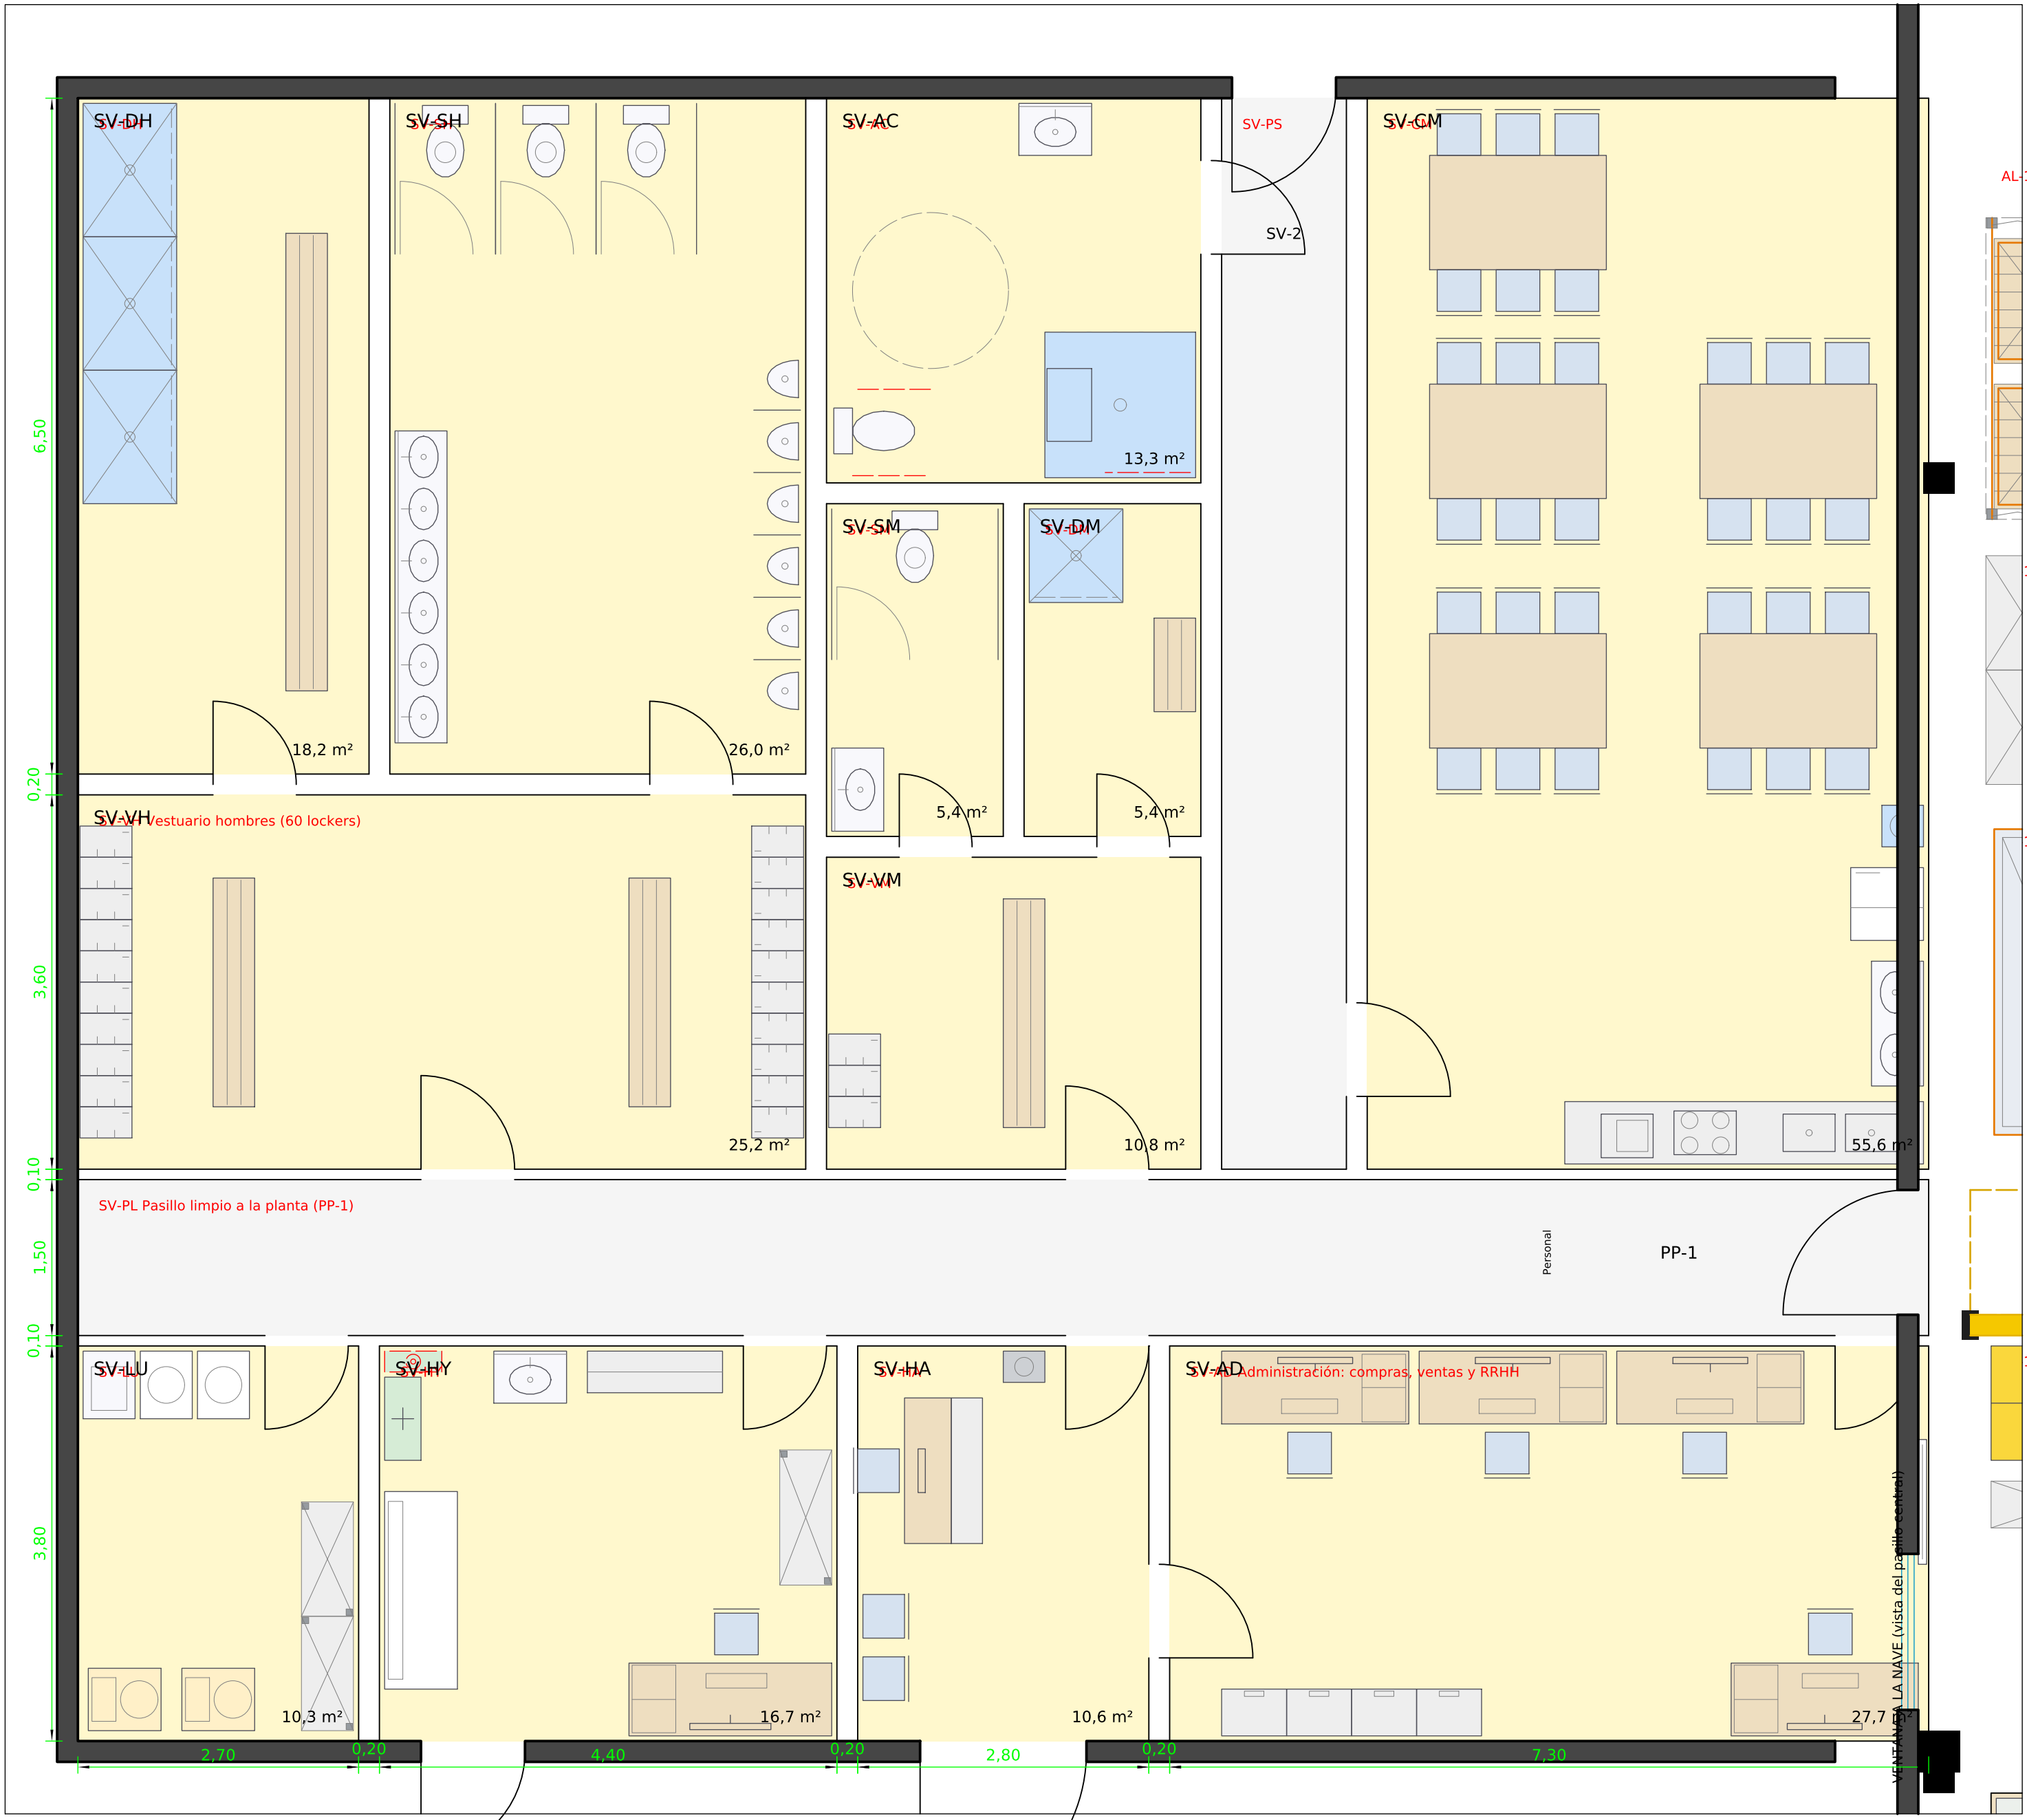


Locales de servicios, administración y apoyo a la línea

Local	m²	Equipoamiento / criterio
SV-U Utilitarios de limpieza	10.3	Fletera de lavado, carrete, máquina de piso y artículos de limpieza (ex)
SV-Mr Higiene y seguridad, medicina laboral, p	16.7	Una sola persona: escritorio, camilla, botiquín y lavabo; entrega de E
SV-VH Hall, recepción y fichado	10.6	Reloj biométrico y tablero de novedades al paso; alfileres a vidrio y p
SV-AD Administración, compras, ventas y RRHH	27.4	4 puestos (compras 1, ventas 2, RRHH 1) y archivo; ventana a la nave a
SV-VH Vestuario hombres (60 lockers)	25.2	1 locker por empleado; 2 bloques de 10 columnas x 3 filas = 60 lockers en
SV-DH Duchas hombres	18.2	3 duchas sobre la misma pared (art. 49-55 m en el turno mañana con ch
SV-SM Inodoros, mingitorios y lavabos hombres	26.0	3 inodoros en la pared norte, 6 mingitorios en la pared este y 6 lavab
SV-MM Vestuario mujeres (9 lockers)	10.8	3 bloques de 3 columnas x 3 filas = 9 lockers (7 en 2023) e baño
SV-DM Inodoro y lavabo mujeres	5.4	Art. de 6 M por turno => 1 inodoro y 1 lavabo
SV-OM Duchas mujeres	5.4	1 ducha, separada del inodoro
SV-AC Sanitario accesible con ducha	13.3	Inodoro con 0.80 m libre lateral; lavabo, ducha a nivel con asiento re
SV-CA Comedor (36 plazas) y office	35.6	3 mesas de 6 m de la puerta; office con bache y lavamanos sobre la
SN-M Sanitarios hombres (planta)	14.4	2 inodoros (pared norte); 2 mingitorios (pared este) y 2 lavabos (pare
SN-M Sanitario mujeres (planta)	7.2	1 inodoro y lavabo
MT Taller de mantenimiento	16.8	Mantenimiento preventivo: bancos, torno, aguilera, soldadora móvil
PR-L Paño de mantenimiento y de línea	17.3	Pegado al taller: repuestos críticos, herramienta del preventivo, cons
Q Laboratorio de calidad	14.0	Mezcladora, espesor por ultrasonido, adherencia y espesor de pintura
DE Cuarentena y muestras retenidas	18.4	Alta con lavab; roles rechazados y un cilindro testigo por lote (IRAM
SUP Supervisor de planta	13.8	Oficina propia del encargado de turno; con ventana a la línea y al pas
PCP Planificación y control de la producción	18.4	Separada del supervisor; 2 puestos y tablero de programación con venta
SC Compresores y colectores de gases de soldad	49.3	Área libre de la vó más el ex paño; colector de Alcal 21 y colector d


DETALLE 2 - FILA CENTRAL: MANTENIMIENTO, PAÑOL, CALIDAD, SUPERVISOR Y PCP - 1:50

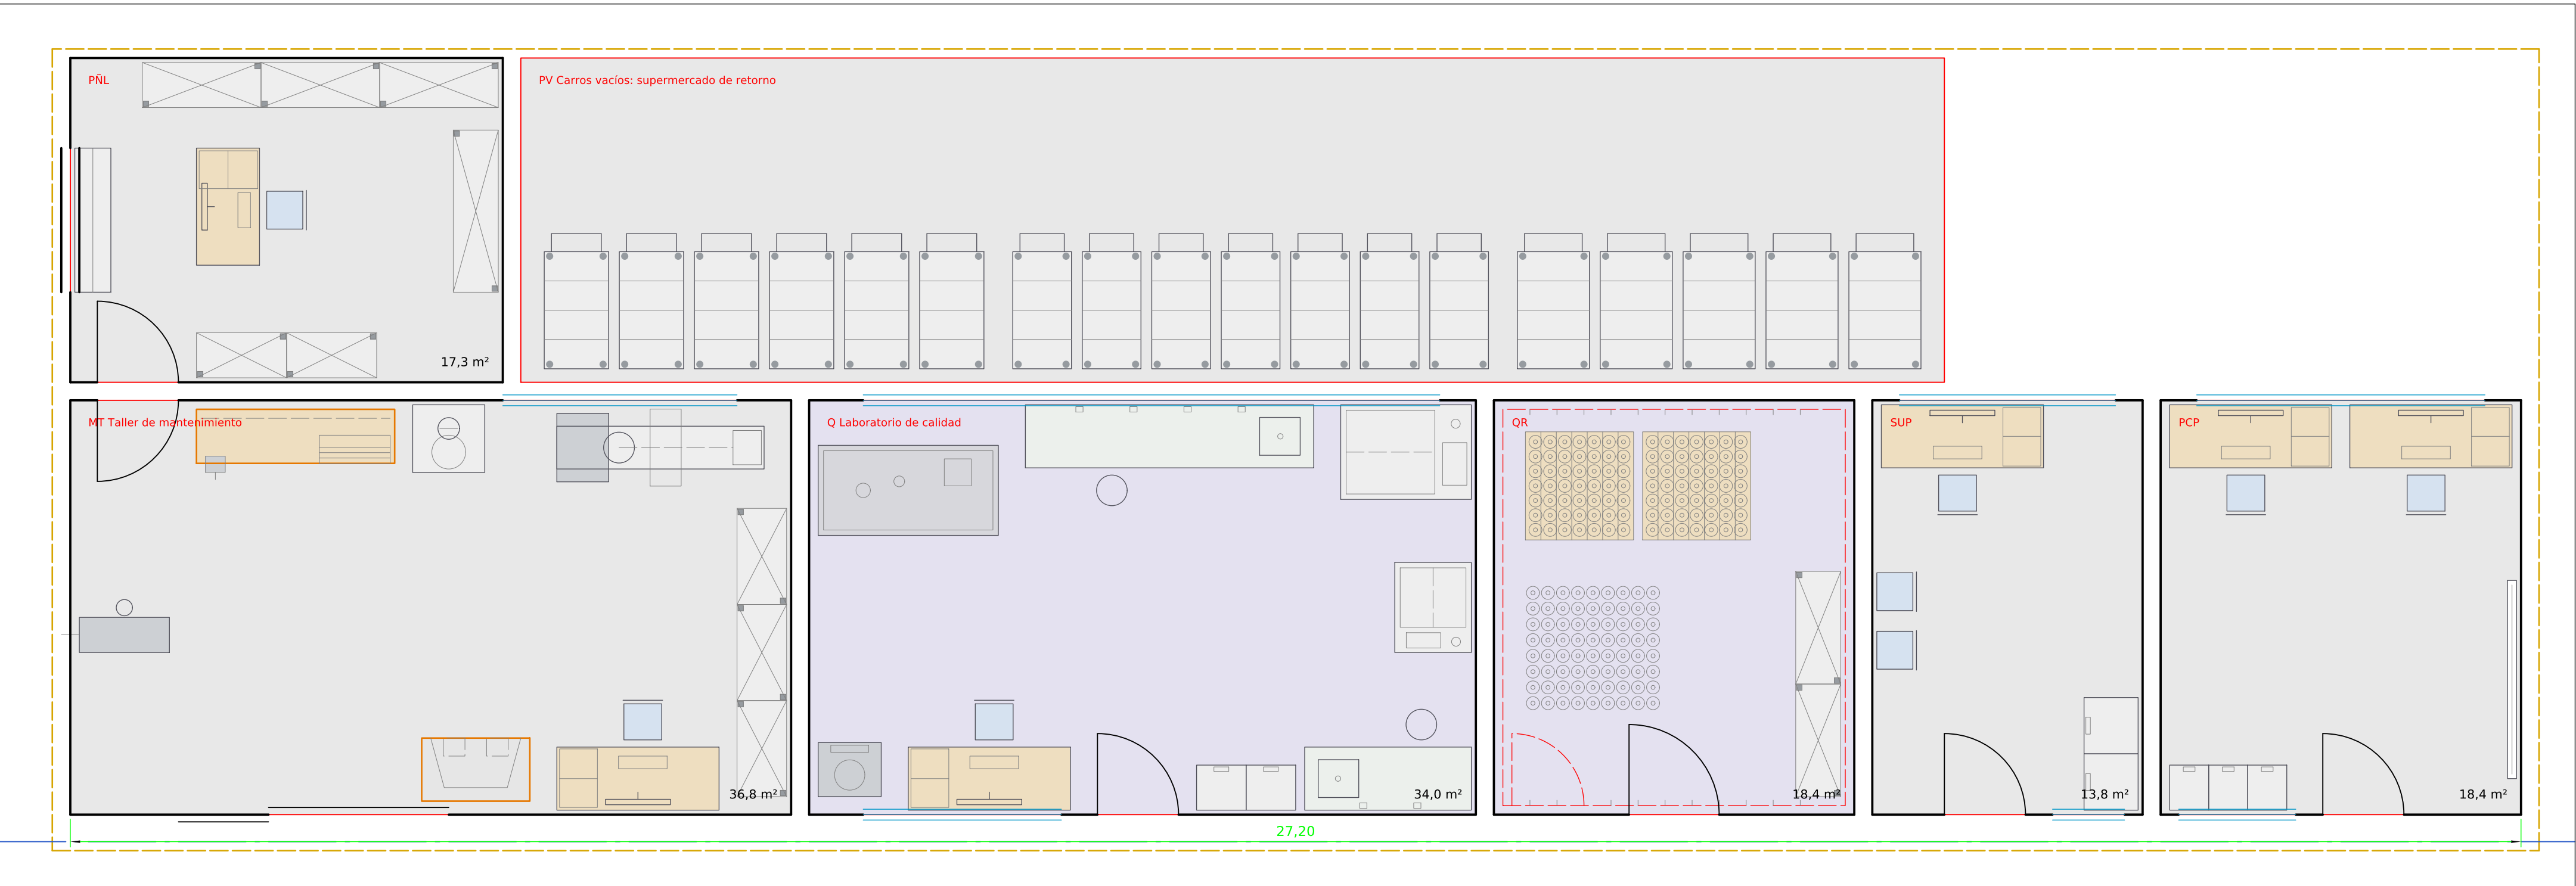

DETALLE 3 - SANITARIOS DE PLANTA (H Y M) - 1:50

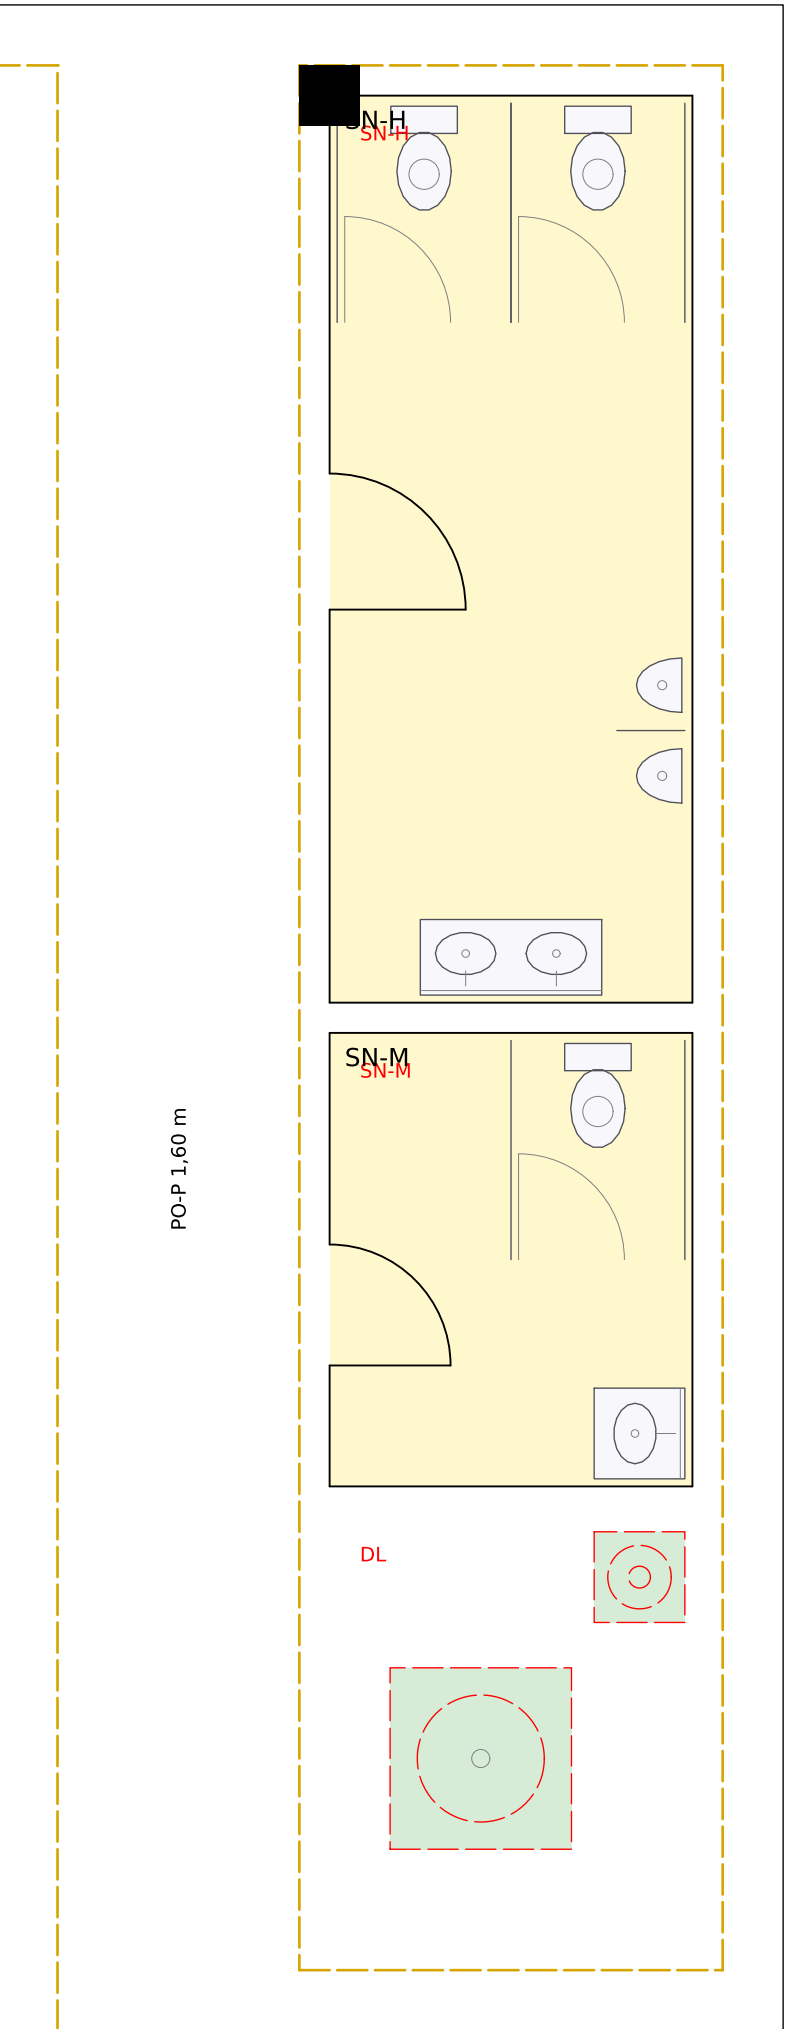

DETALLE 4 - COMPRESORES Y COLECTORES DE GASES DE SOLDADURA - 1:50

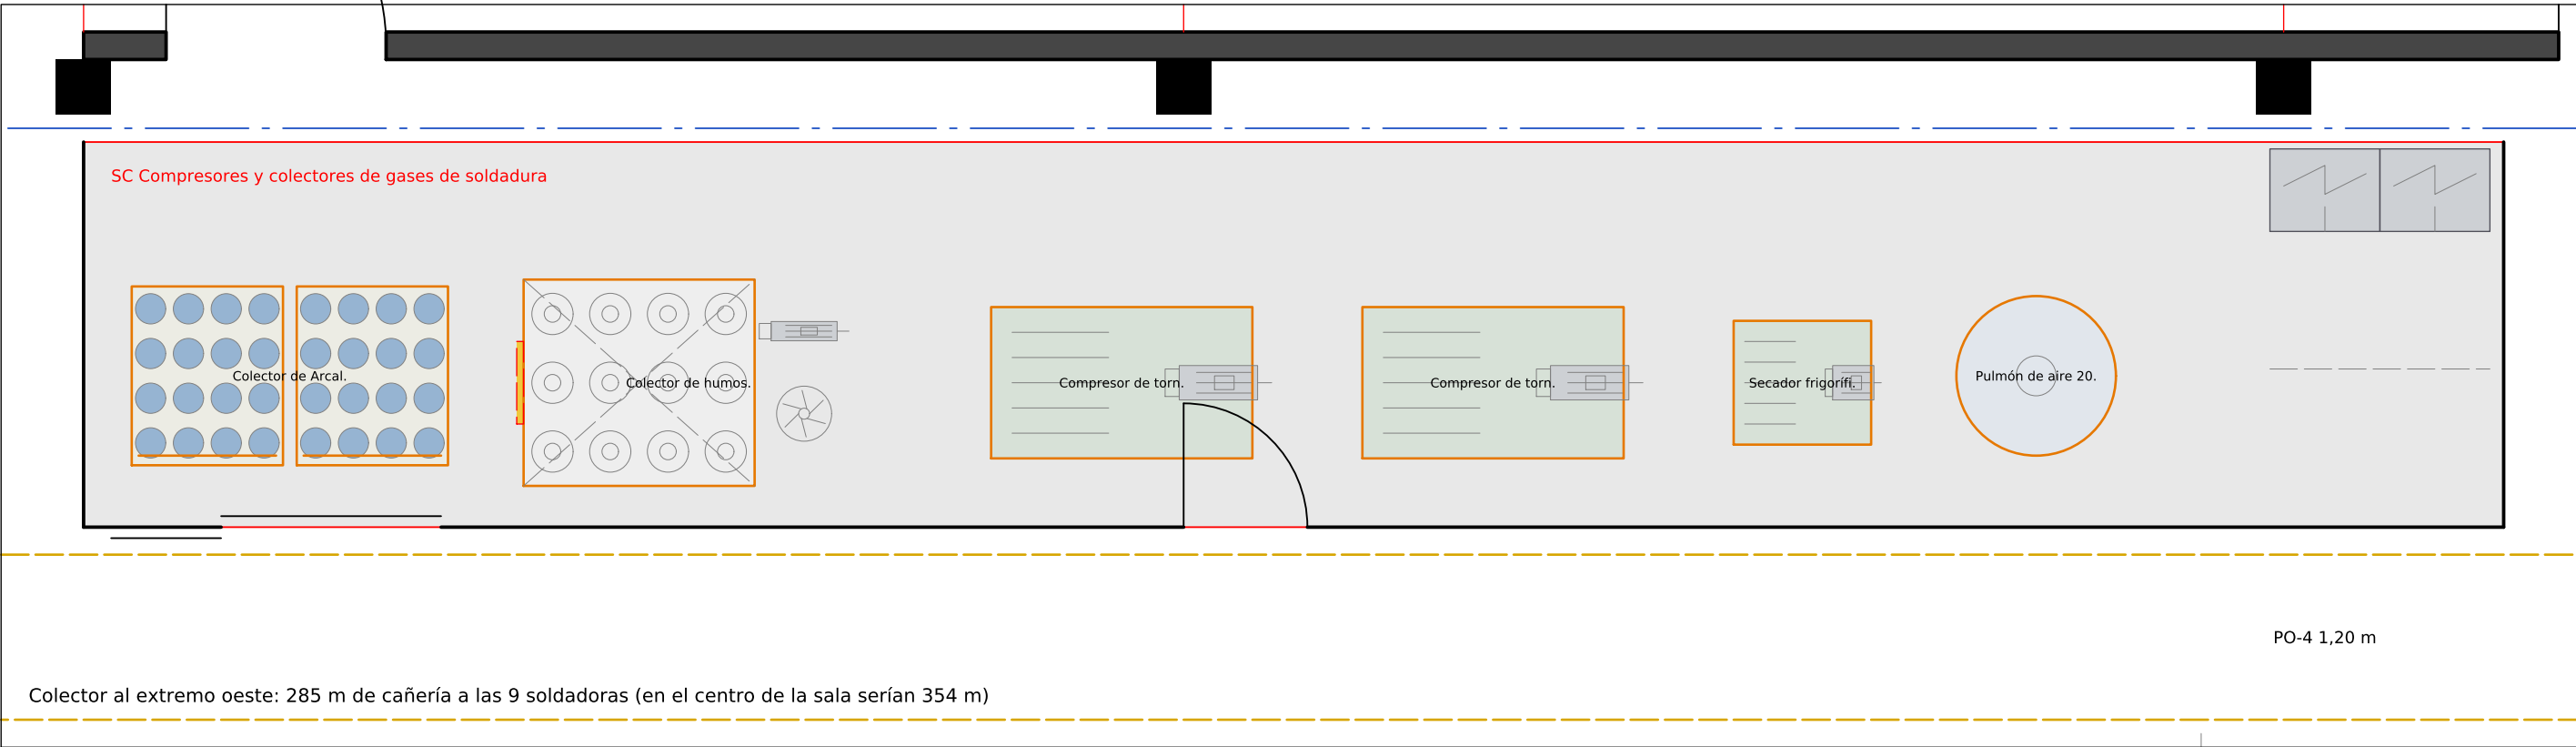

Circuito y criterios

- ① Ingreso por SV-1 (camino peatonal desde G4 y la garita); fichado en el hall.
- ② Pasillo limpio; al sur limpieza, higiene y seguridad (con EPP y primeros auxilios), hall y administración; al norte vestuarios, sanitario accesible y comedor.
- ③ Vestuario: 1 locker por empleado (bloques de 10 columnas x 3 filas). Duchas en su propio local, separadas de inodoros y mingitorios; todo sólo desde el vestuario.
- ④ Duchas, inodoros, mingitorios y lavabos: cada grupo alineado sobre una misma pared húmeda.
- ⑤ Sanitario accesible con ducha a nivel donde estaba limpieza; se entra por el pasillo PS, que termina en la salida de emergencia SV-2.
- ⑥ Comedor: el office (bacha y lavamanos sobre la misma pared) junto a la puerta; las mesas al fondo.
- ⑦ Administración (compras, ventas, RRHH) contra la nave; ventana a lo largo del pasillo central y PP-1 a 6 m.
- ⑧ Supervisor en oficina propia y PCP separado; los dos con ventana a la línea; mantenimiento con su paño pegado; calidad y cuarentena (con muestras y archivo) juntas.

	Fecha	Nombre	Propietario	Reemplaza a / Reemplazado por
Dibujó	03/10/26	Claude Code	FLAMA S.A.	-
Revisó			Denominación	Material
Aprobó				Mampostería / estructura metálica
Escala	1:50	Método de proyección	Servicios, oficinas y apoyo	Edición
Unidades	03/10/26	ISO E	central (mantenimiento, calidad, supervisor, PCP),	0
Cotas en m	A0	Plano de detalle	FL_PI_05	03/10/2026