


Nave 88 x 44 m, servicios al personal, recargas y sala técnica, con cada máquina, puesto, pulmón, mueble y artefacto a escala. Cotas en metros. Ejes 1 a 12 cada 8,00 m y A-B-C



IMPLANTACIÓN GENERAL - 1:500

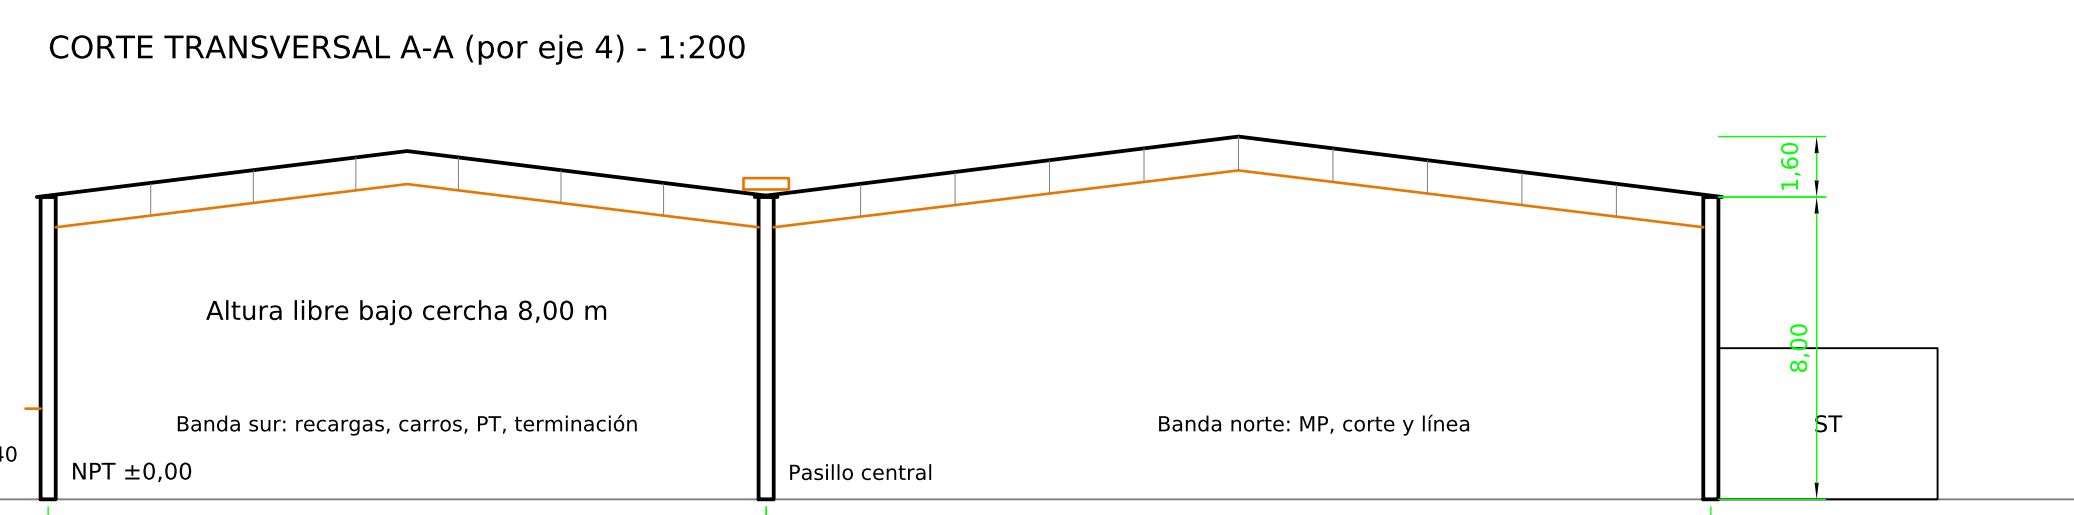

Nota: pólitos móviles de dos laces (19,40 y 24,60 m) cada 8 m; altura libre 8,00 m; zócalo de bloque 2,40 m y chapa; anexas de rampastería. Pisos de hormigón liso con demarcación IRAM 10005; sanitarios con revestimiento hasta 2,10 m (Dcc. 351/79 cap. 5).