


FL_PI_04 - PLANO FORMAL NORMALIZADO - HOJA 1: IMPLANTACIÓN GENERAL

Parque Industrial Villa de Luján, Gral. Heredia 3220, Sarandí (Avellaneda). Escala 1:200. Cotas en metros. Norte arriba.

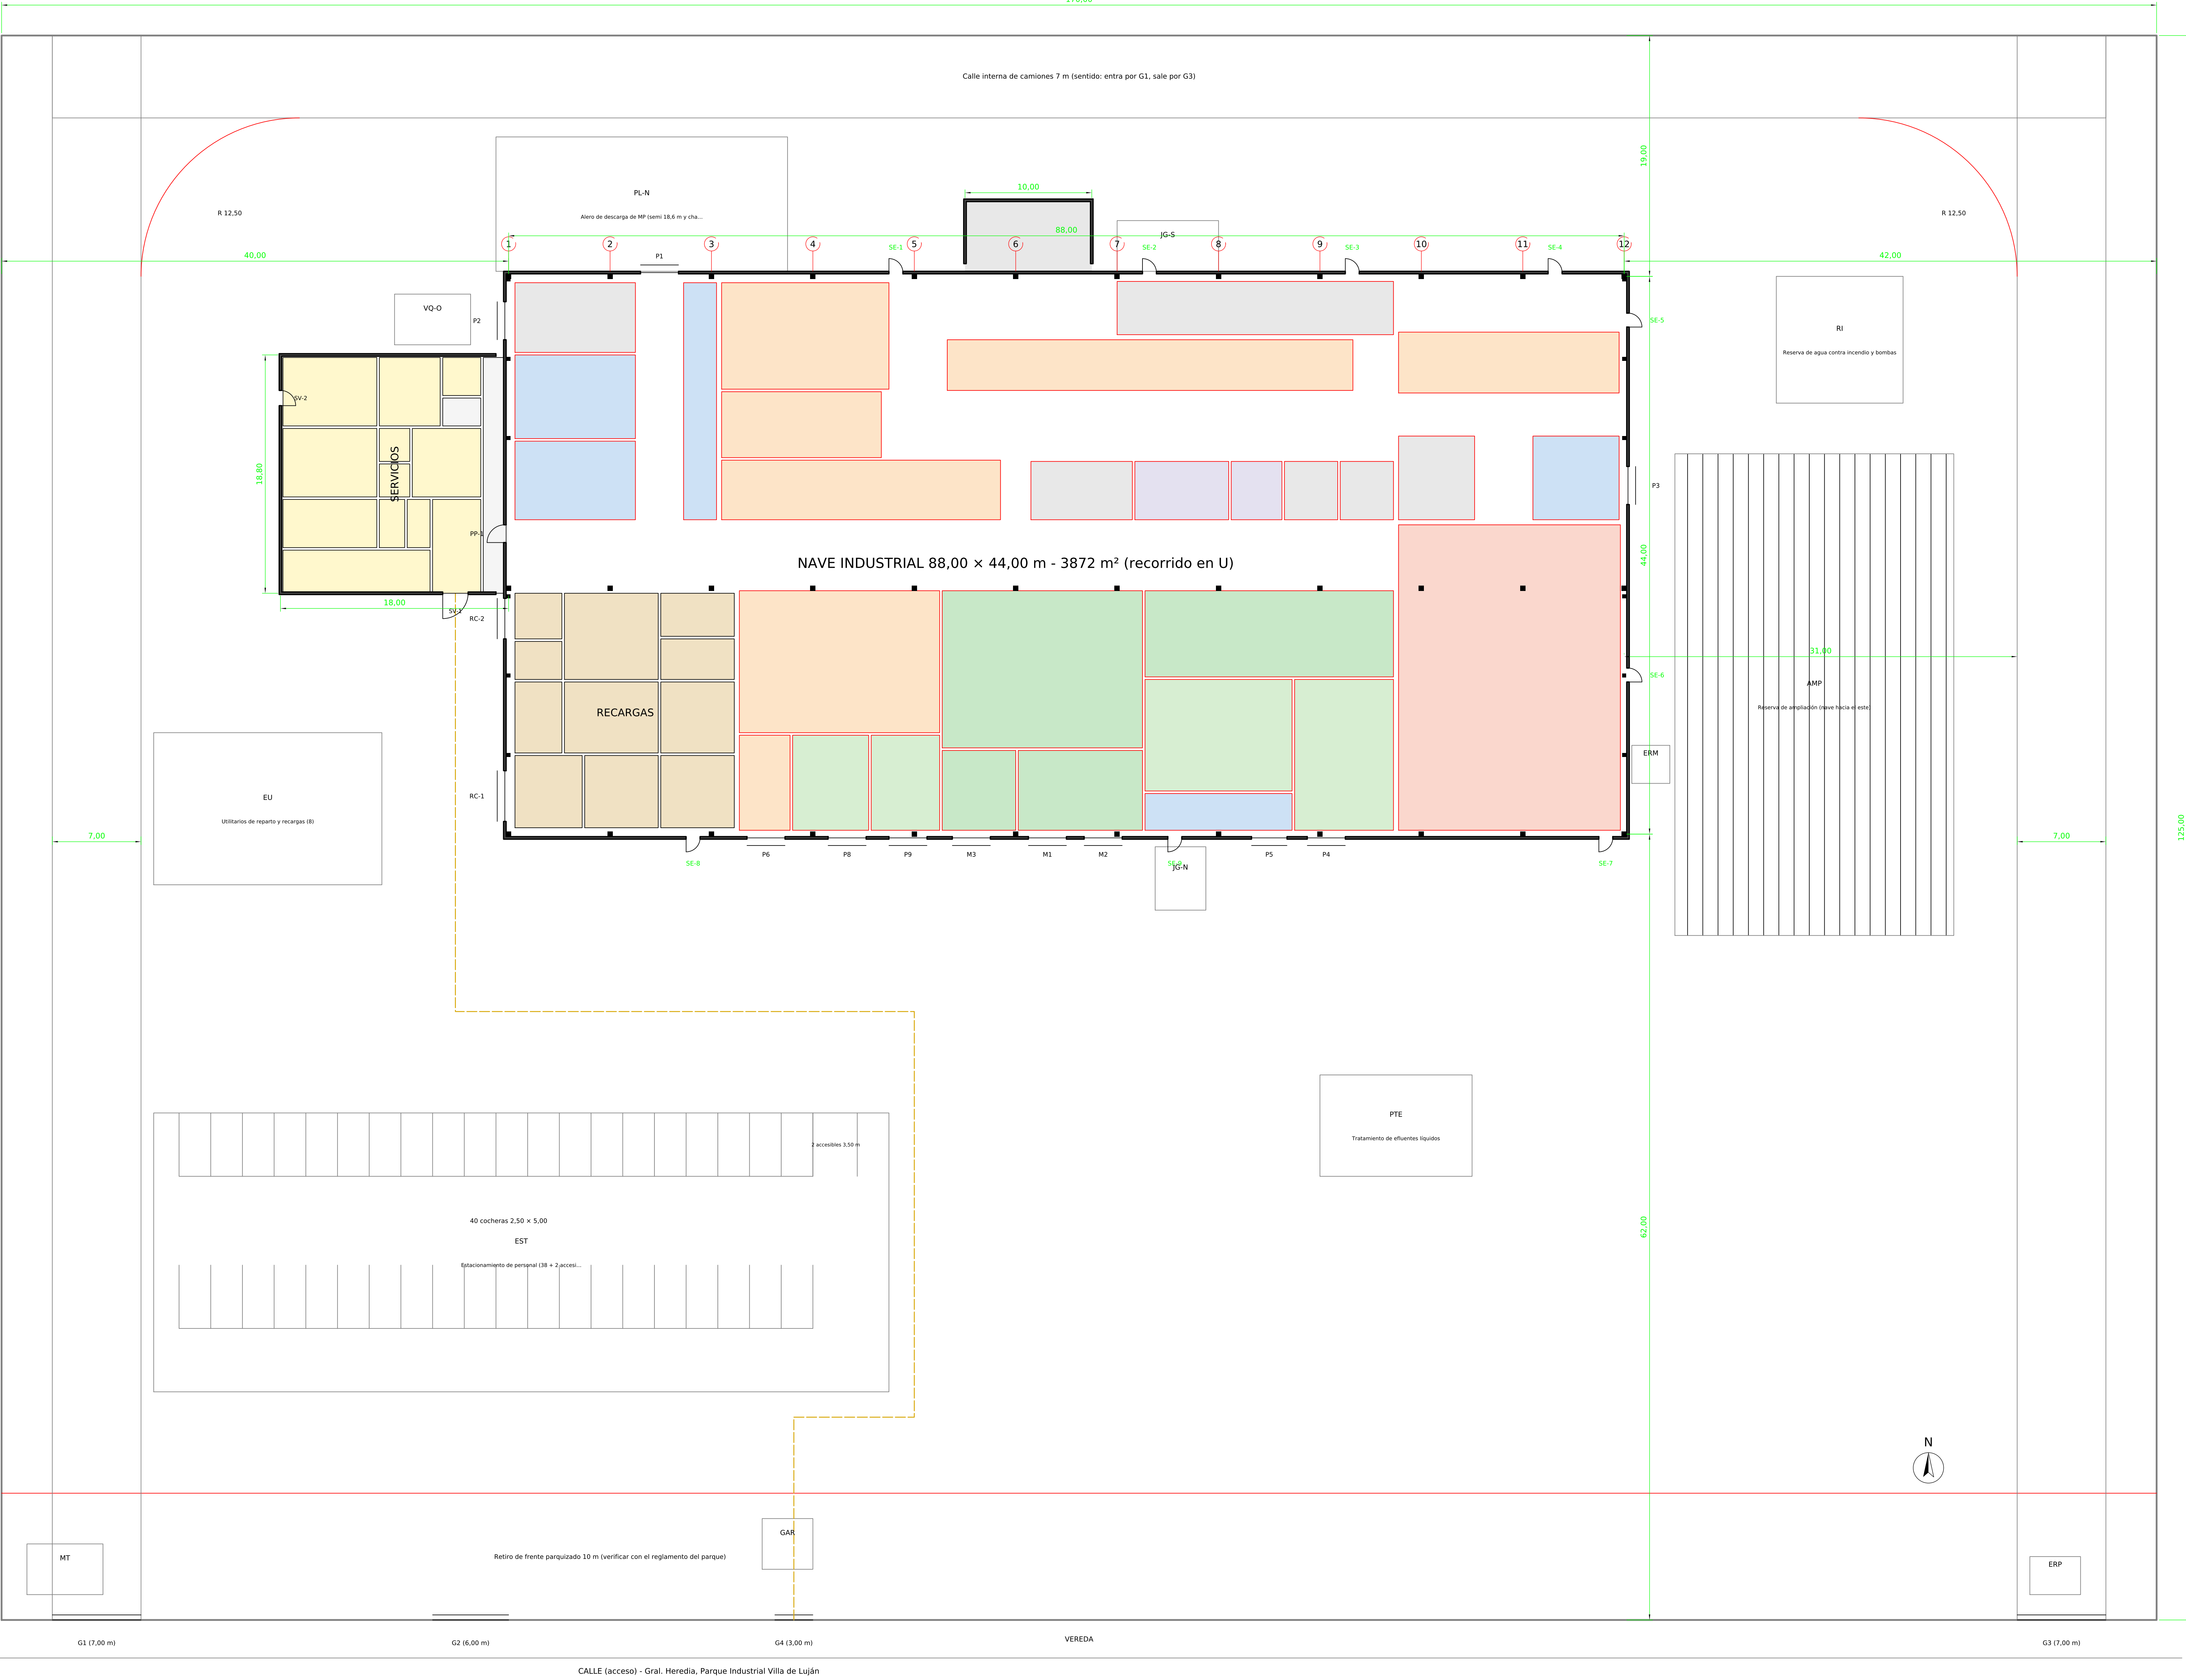

Cuadro de superficies

Concepto	m²	%
Terreno 170,00 × 125,00	21.250	100,0
Nave industrial 88,00 × 44,00	3.872	18,2
Incluye recargas (ángulo 50°)	335	
Servicios al personal y oficinas	338	1,6
Sala técnica norte	58	0,3
Alero de descarga de MP (norte)	244	1,1
Superficie cubierta total	4.512	21,2
FOS = cubierta / terreno		0,21
Reserva de ampliación (este)	836	

FOS, FOT, retiros y altura máxima: verificar con el reglamento del parque industrial y el código de Avellaneda (Ley 13.744 de parques industriales PBA, habilitación Ley 11.459).


Referencias de exteriores

Código	Elemento exterior
PL-N	Alero de descarga de MP (semi 18,6 m y chasis)
VQ-O	Volquete 6 m³ (scrap)
JG-S	Jaula de gases de soldadura (Ar/CO₂)
ERM	Regulación de gas de hornos
JG-N	Jaula de N₂ y CO₂ (manifold)
RI	Reserva de agua contra incendio y bombas
AMP	Reserva de ampliación (nave hacia el este)
PTE	Tratamiento de efluentes líquidos
EST	Estacionamiento de personal (38 + 2 accesibles)
EU	Utilitarios de reparto y recargas (8)
GAR	Garita y control de acceso
MT	Celda de medición de media tensión
ERP	Estación reductora de gas
G1	Portón de camiones de MP, scrap y pintor (entrada)
G2	Portón de autos del personal
G3	Portón de camiones de PT y carros (salida)
G4	Ingreso peatonal con garita

Circulación de camiones en anillo de un sentido (G1 -> oeste -> norte -> este -> G3); los camiones de MP descargan en la playa norte o en la bahía interior oeste y los de PT en los muelles sur sin cruzarse. Autos y peatones entran por el frente, separados de los camiones. Radio de giro exterior del semi: 12,50 m. Pavimento de hormigón en calles, playas y patios; veredas perimetrales de 1,20 m. Naves: pórticos metálicos de dos luces (19,40 y 24,60 m) cada 8 m, columnas centrales en el eje B, al borde del pasillo central; altura libre bajo cerca 8,00 m; cerramiento de zócalo de bloque de 2,40 m y chapa; cubierta de chapa con aislación y lucernarios; anexos de mampostería.

	Fecha	Nombre	Propietario	Reemplaza a / Reemplazado por
Dibujó	02/10/26	Claude Code	FLAMA S.A.	-
Revisó			Denominación	Materia
Aprobó			Implantación general	Estructura metálica
Escala	1:200	Método de proyección		Edición
Unidades	Cotas en m	Formato	A0	Fecha de emisión
				02/10/2026
				Hoja
				1 / 4
				es
				Nº de plano
				FL_PI_04


Escala 1:100. Cotas en metros. Ejes estructurales 1 a 12 cada 8,00 m y A-B-C (luzes de 19,40 y 24,60 m, columnas centrales en el eje B).

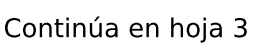

Referencias: cada equipo se dibuja en planta a escala con sus partes (bastidor, rodillos, mordazas, motores, tableros), resguardos en rojo y operario en su puesto (magenta); en trazos, partes elevadas; óvalo = código del equipo; círculo rojo = barrido de pluma; líneas amarillas = demarcación de pasillos (IRAM 10005); cebra = senda peatonal; punto rojo numerado = extintor ABC 10 kg (IRAM 3517-2, recorrido ≤ 20 m); flecha verde = salida de emergencia 1,10 m con barril antipánico.

FL PI_04 - PLANO FORMAL NORMALIZADO - HOJA 3: PLANTA DE LA NAVE, SECTOR ESTE (x = 42 a 104 m)

Escala 1:100. Cotas en metros. Ejes estructurales 1 a 12 cada 8,00 m y A-B-C (lucos de 19,40 y 24,60 m, columnas centrales en el eje B).

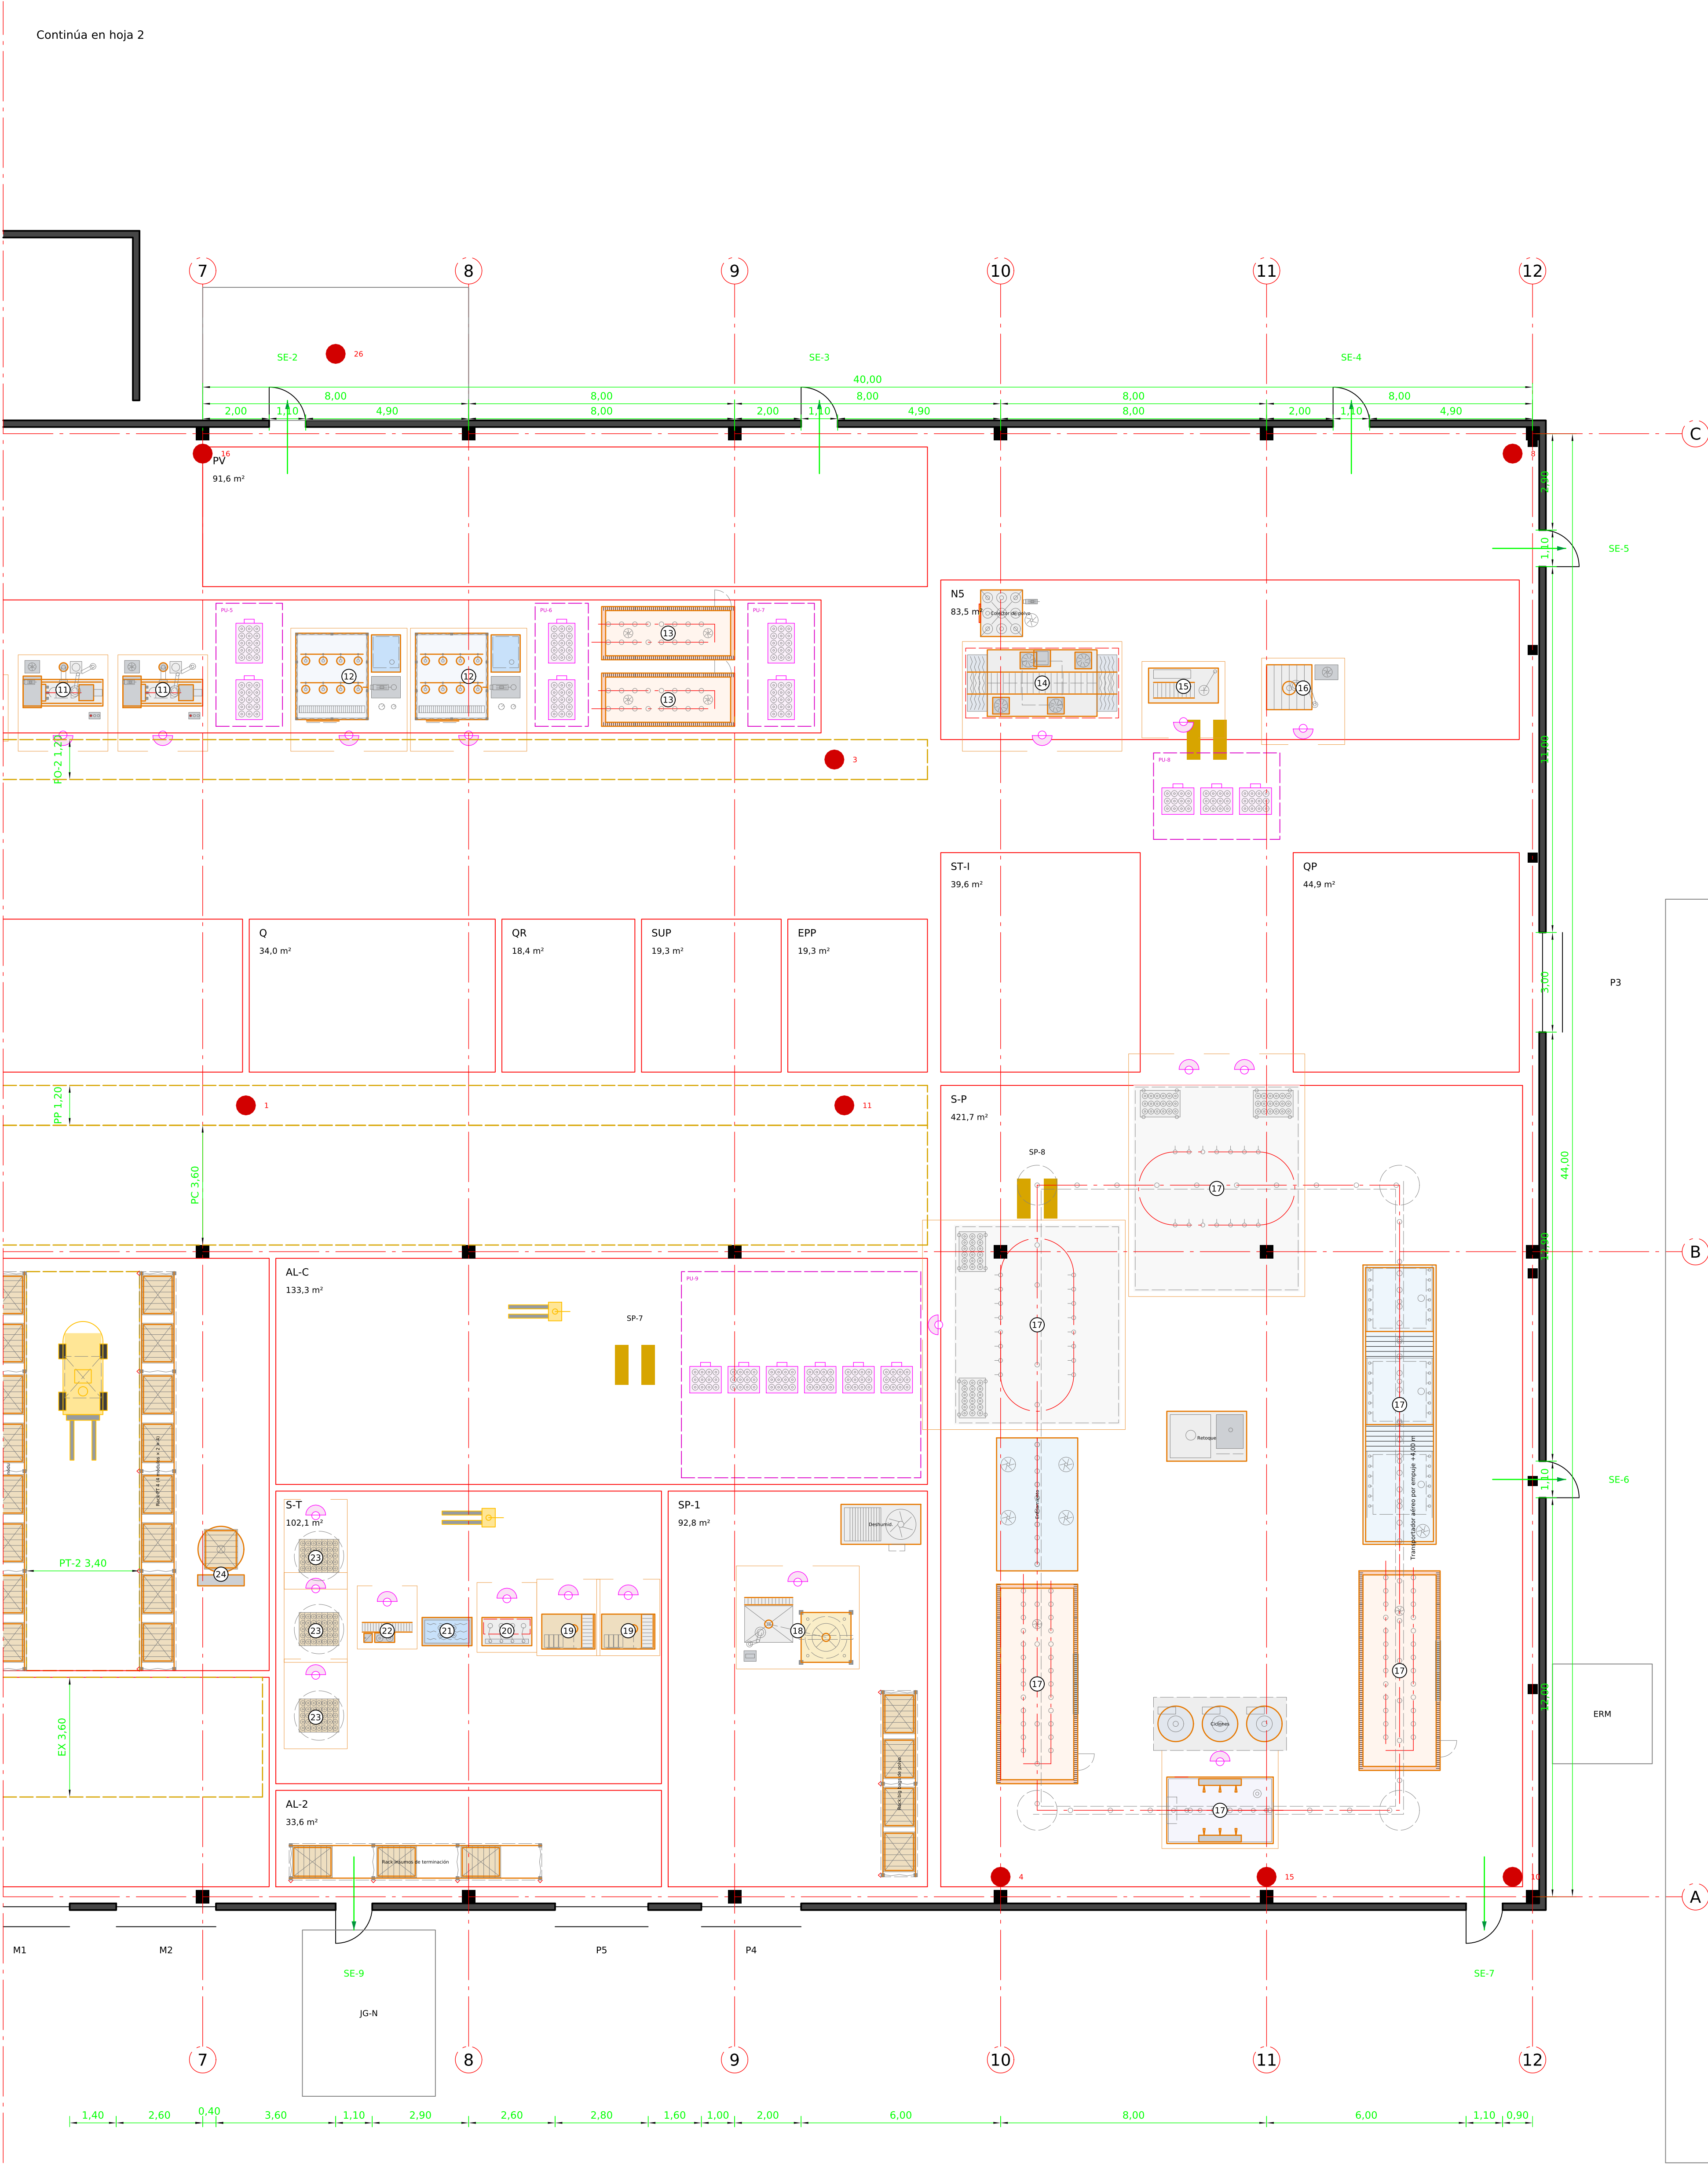


FL_PI_04 - PLANO FORMAL NORMALIZADO - HOJA 4: SERVICIOS, SANITARIOS Y CORTE

Planta del bloque de servicios 1:50; sanitario accesible 1:20; corte transversal de la nave 1:100. Cotas en metros.

BLOQUE DE SERVICIOS AL PERSONAL Y OFICINAS - 1:50



Inodoro a 0,45-0,50 m de altura; eje a 0,45 m del muro con barra fija; espacio lateral libre $\geq$ 0,80 m del lado de transferencia con barra rebatible; lavatorio sin pie a 0,80-0,85 m; espejo inclinado; puerta de 0,90 m que abre hacia afuera; accionamiento de canilla por palanca; timbre de emergencia.

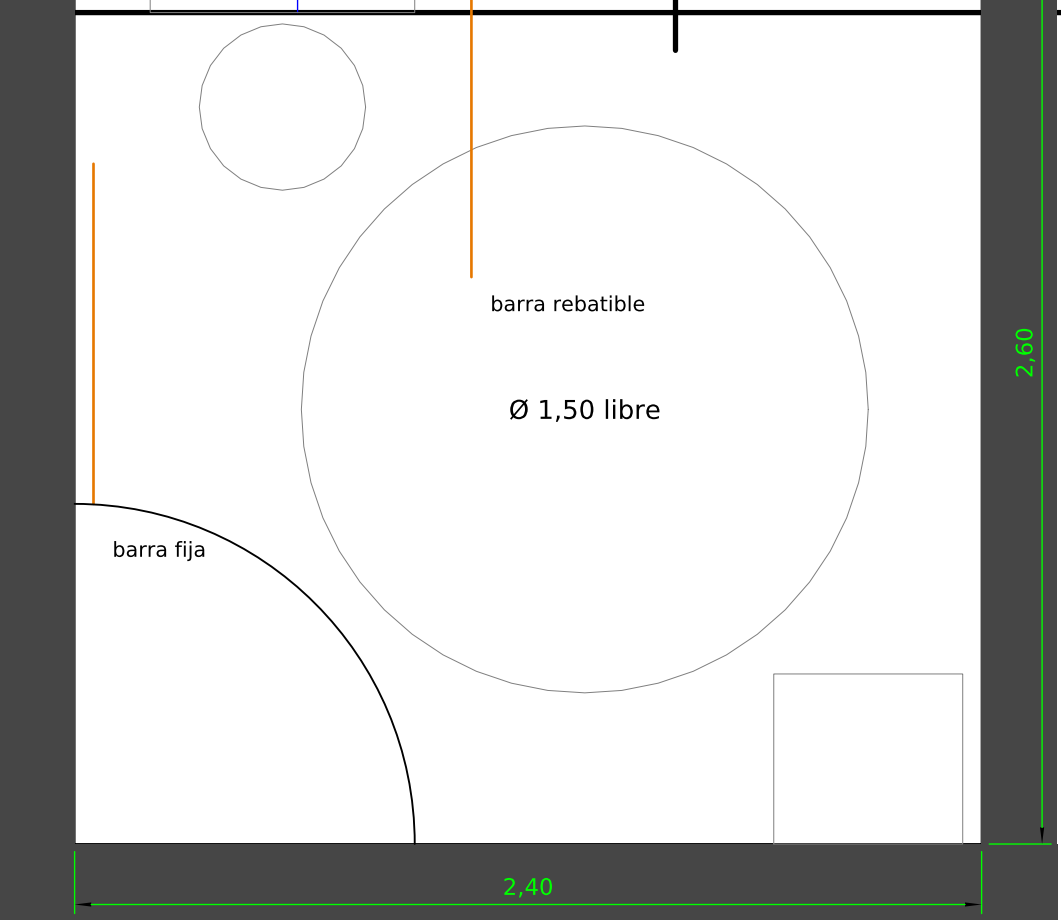


Locales de servicios y recargas

Local	m²	Equipamiento
SV-VH Vestuario hombres (62 armarios)	40,0	
SV-SH Sanitarios y duchas hombres	29,8	1 Inodoros, 6 mingitorios, 6 lavabos, 4 duchas
SV-LI Limpieza	9,0	
SV-PS Paso a planta	6,6	
SV-WH Vestuario y sanitarios mujeres (14 armarios)	40,0	2 Inodoros, 2 lavabos, 2 duchas
SV-AC Sanitario accesible	6,2	Círculo libre Ø 1,50 m, barras, inodoro con 0,80 m libre later
SV-LA Lactario	6,2	Buena práctica (Ley 26.873)
SV-PA Primeros auxilios	29,2	
SV-CO Pasillo	33,5	
SV-HA Hall, recepción y fichado	28,1	
SV-OF Oficinas (6 puestos)	28,1	
SV-JP Jefatura de planta	7,6	
SV-RE Reuniones	6,8	
SV-CH Comedor 30 plazas y office	39,4	
RC-RE Recepción, clasificación y recibidos	30,2	Clasificación en 4 colas: polvo, CO ₂ , agente limpio y líquidos
RC-DE Desarme y lavado	33,1	
RC-OC Descarga y ensayo de funcionamiento	33,1	Sala con extracción y recuperación de polvo
RC-PI-PIH con jaula, secado y Puffer	32,5	
RC-PV Recinto de polvo (IH $\leq$ 70 %)	41,4	Carga ABC, BC y D, 8 renovaciones por hora; sin estufas
RC-SA-CD y agente limpio	20,7	Trasvaseador y balanza
RC-IR Inutilizados y residuos	33,1	
RC-OP Despacho y equipos para entregar	33,3	
RC-EN Embalaje, presentación, peso, hermeticidad y retoque	50,3	
RC-LO Líquidos	18,6	Agua, AFFF y clase K
RC-RP Etiquetado y fisa de intercambio	19,7	

Pisos lavables y antideslizantes; revestimiento sanitario hasta 2,30 m; ventilación natural o mecánica; agua caliente y fría en duchas y lavabos (Dec. 351/79 cap. 3); altura mínima de locales 3,00 m; separación por sexo con acceso independiente; vestuarios contiguos a los sanitarios (art. 50). Paso a planta PP-1, directo al pasillo central de personal.

CORTE TRANSVERSAL A-A (por eje 4) - 1:100

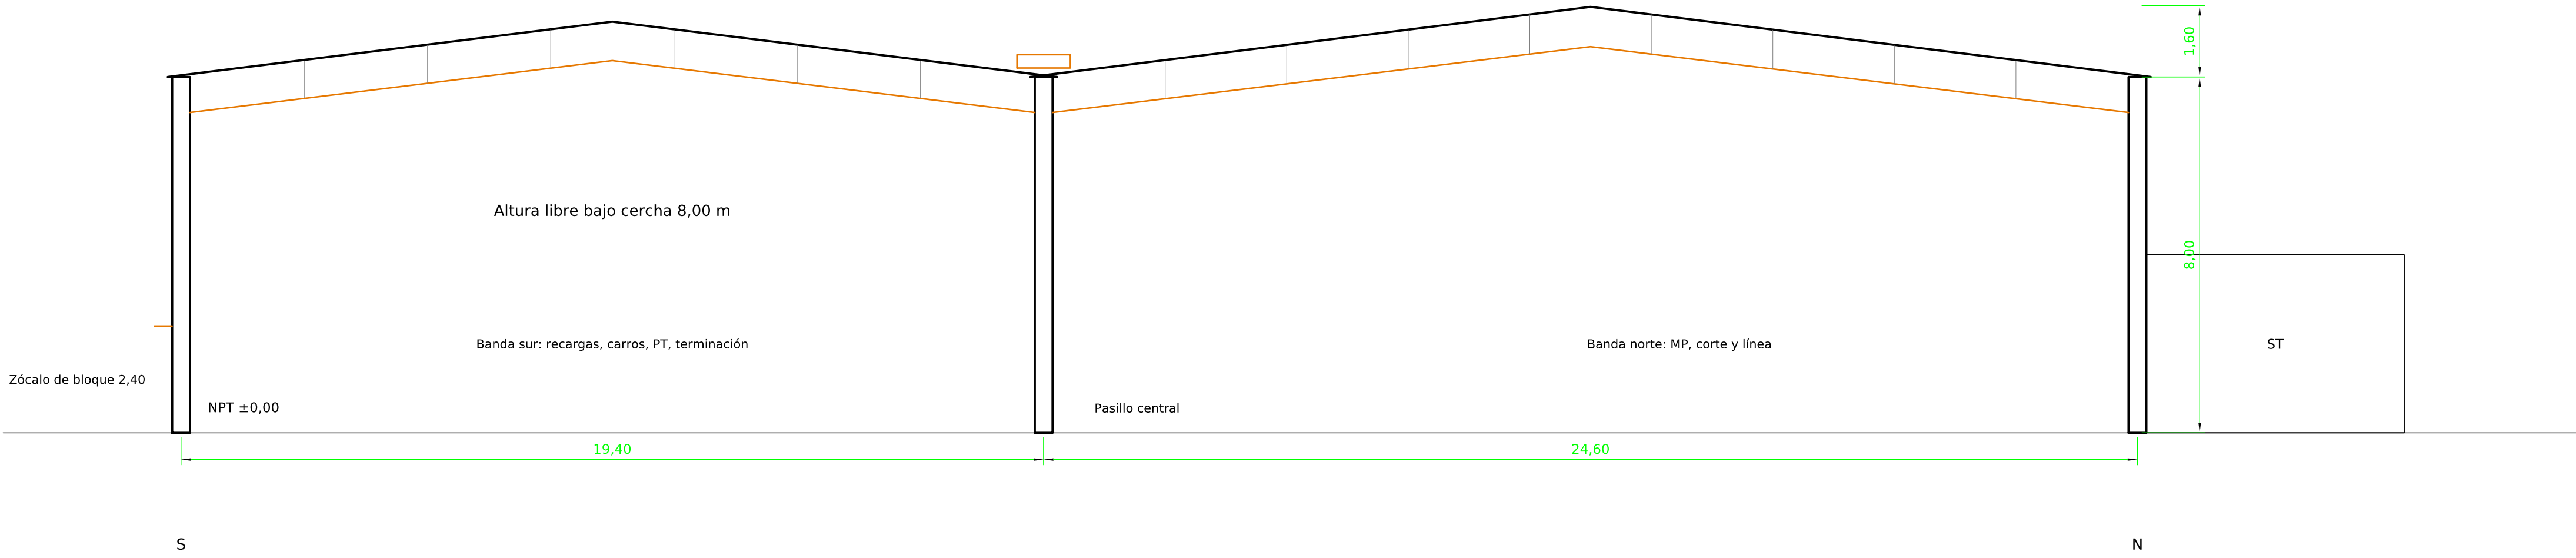

	Fecha	Nombre	Propietario		Reemplaza a / Reemplazado por	
Dibujó	02/10/26	Claude Code	FLAMA S.A.			
Revisó			Denominación	Mampostería / estructura metálica		
Aprobó						
Escala	Método de proyección		Fecha de emisión			
1:50			02/10/2026			
Unidades	Formato		Hoja			
Cotas en m	A0		Planta 1:50, sanitarios accesible 1:20, corte 1:100		4 / 4 es	
			Tipo de documento		Nº de plano	
			Plano de detalle		FL_PI_04	