


FL_PI_02 - FLUJO DE OPERACIONES Y PROCESOS POR SECCIÓN

Planta Industrial FLAMA S.A. - Parque Industrial Villa de Luján, Sarandí (Avellaneda) - dimensionada al año 10 (2035). Escala 1:200. Norte arriba; la calle de acceso está al sur.

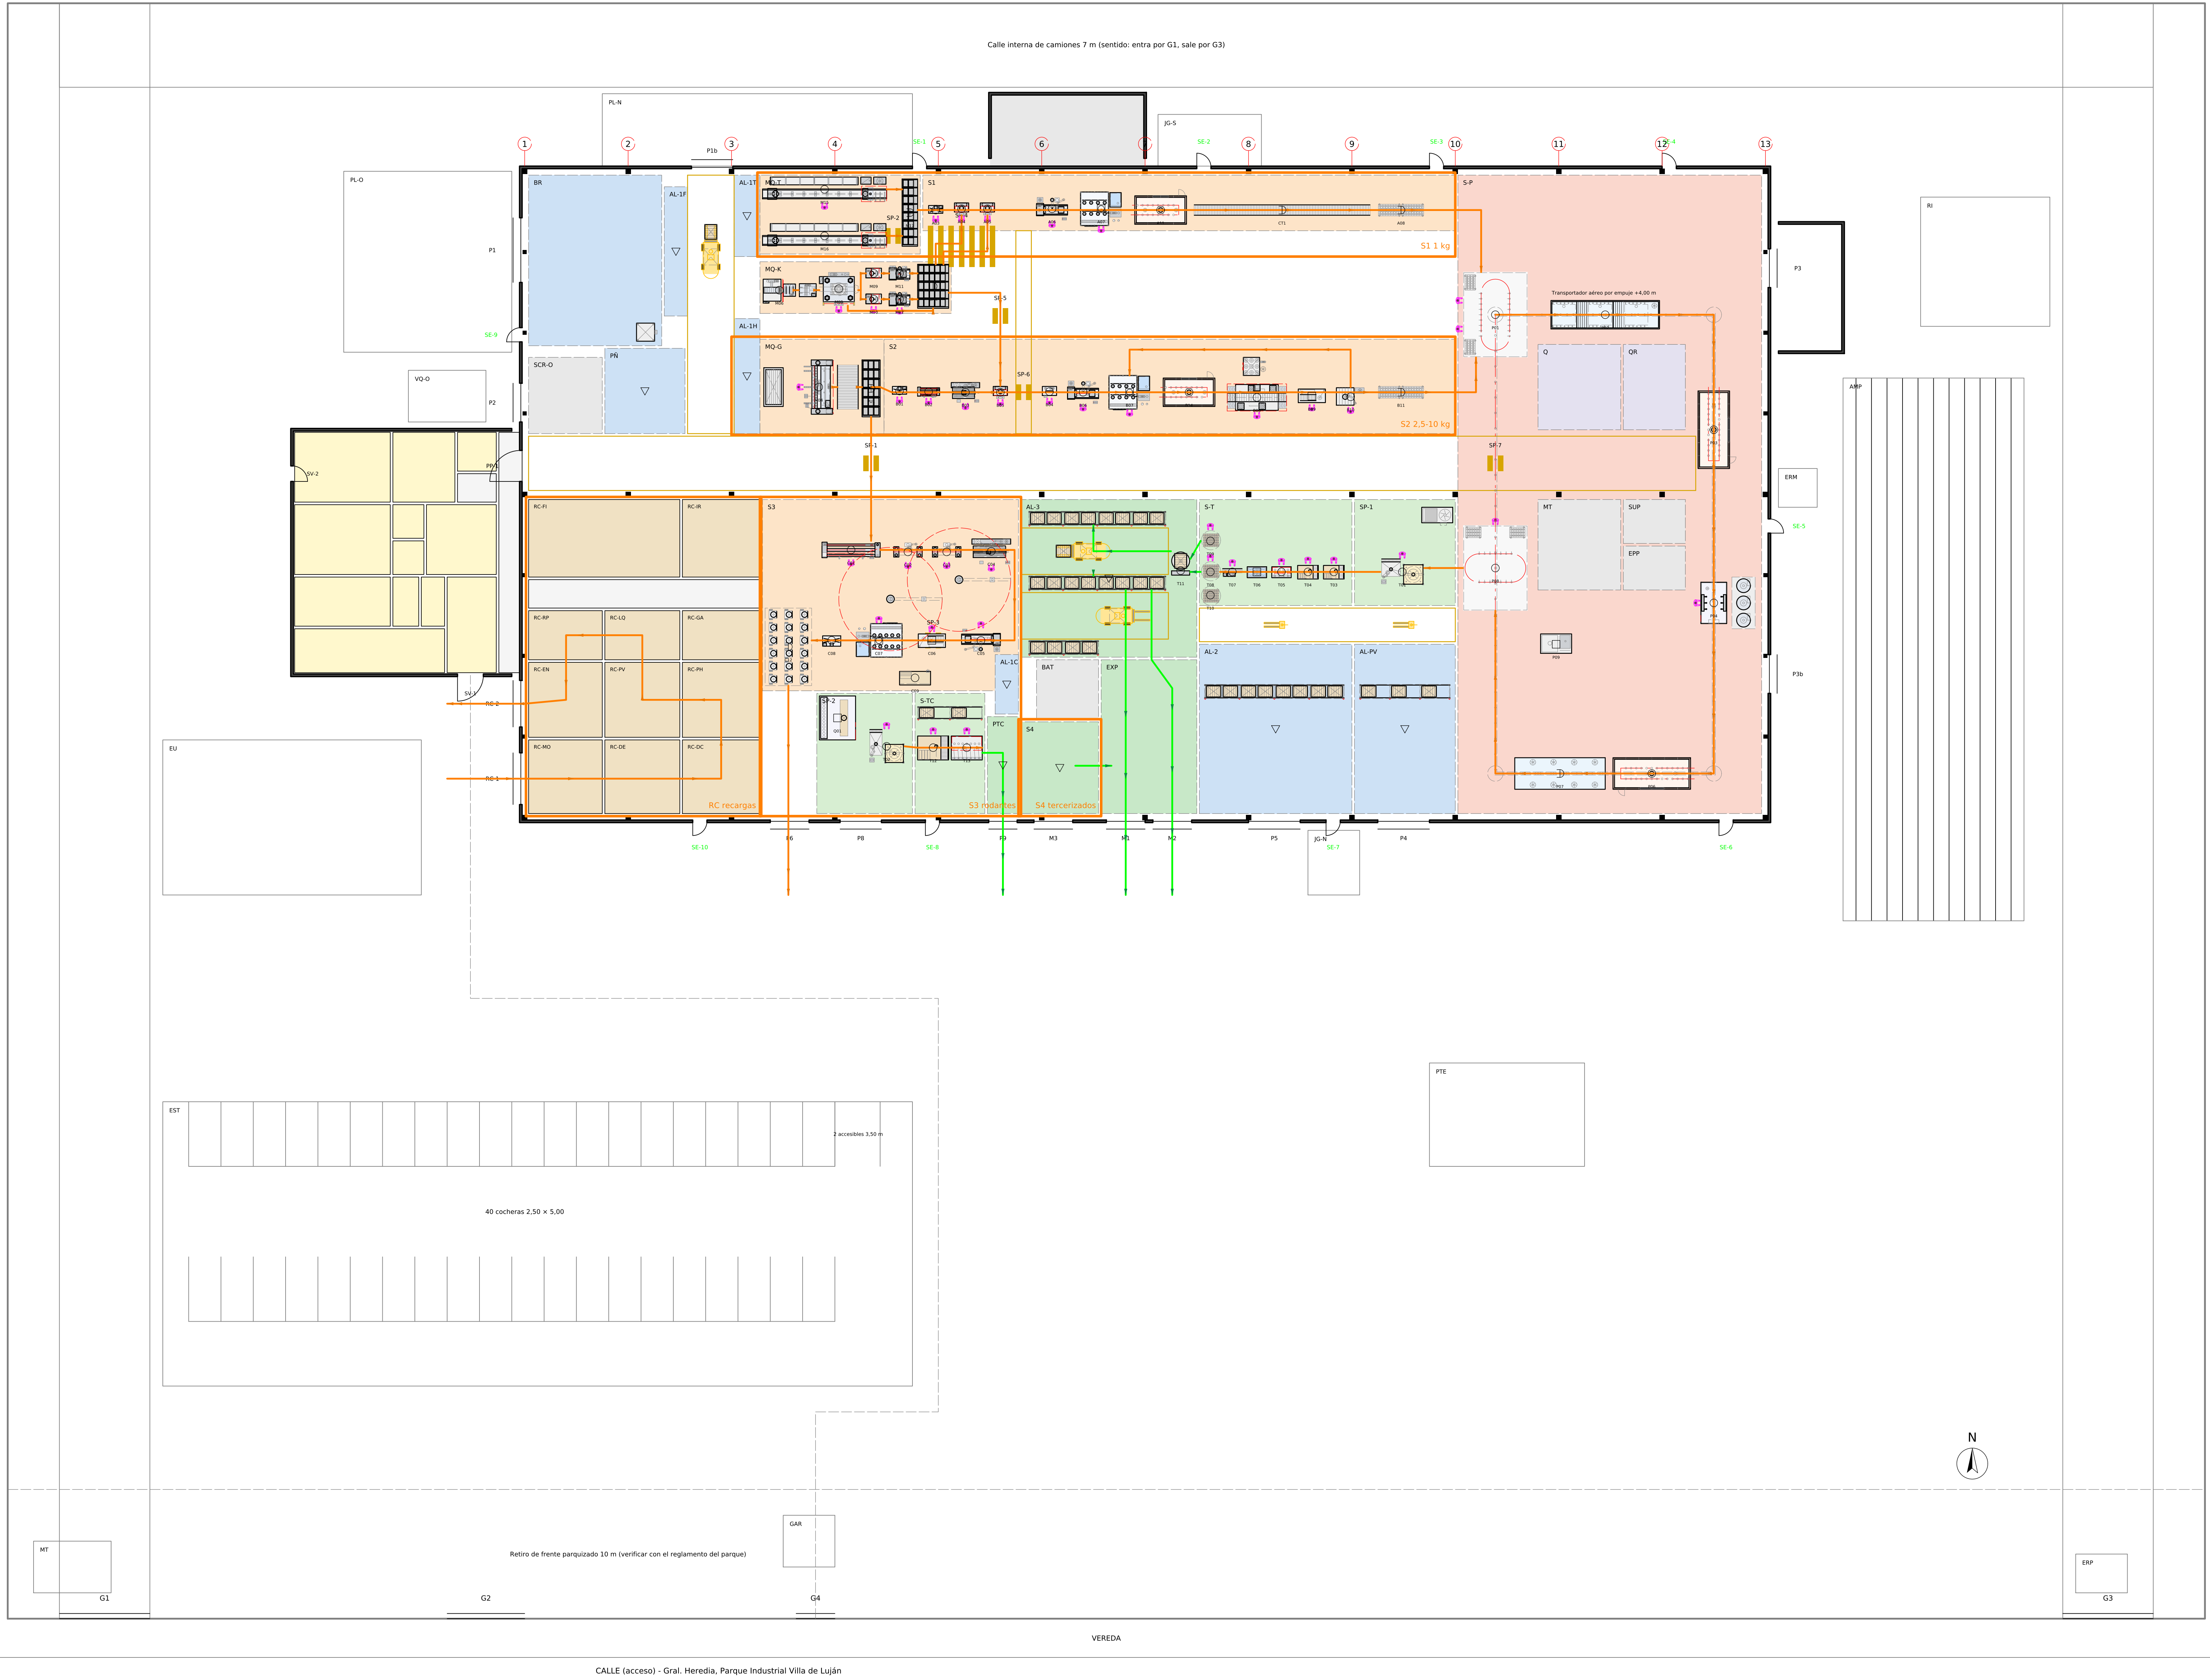

Simbolos (ASME)

- Operación
- Inspección / control
- Operación e inspección combinadas
- Transporte (tren logístico, autoelevador, carro)
- Demora: pulmón o supermercado
- Almacenamiento

S1 - Matafeugos ABC 1 kg (fabricados)

Paso	Dónde
✓ Corte en cartón	AL-17
✓ Corte de caño láser	M15/M16
✓ Pulmon	M17
✓ Numerado	A03
✓ Encastre de fondo	A04
✓ Encastre de cupla con cuello	A05
✓ Soldadura circunferencial	A06
✓ Prueba hidraulica 100 %	A07
✓ Secado	A11
✓ Transportador de rodillos	CT1
✓ Pulmón a pintura	A08
✓ Pretratamiento	P02
✓ Secado	P03
✓ Pintura en polvo	P04
✓ Pulverizado	P06
✓ Espesor y adherencia	P09
✓ Carga de polvo	T01
✓ Ensamblaje	T03/T04
✓ Presurización con N2	T05
✓ Hermeticidad	T06
✓ Etiquetado	T07
✓ Embalaje y palletizado	T08/T09
✓ Envolado	T11
✓ Almacen de PT	AL-3
✓ Expedición	M1/M2

O16 - I2 - Q11 - T2 - D2 - A2

S3 - Matafeugos ABC rodantes 25 / 50 / 70 ...

Paso	Dónde
✓ Hojes LAC	AL-1H
✓ Corte de cuerpo	M04
✓ Pulmon	P01
✓ Cilindrado 4 rodillos	C01
✓ Punteo, refuerzo y estructura	C02/C03
✓ Soldadura longitudinal	C04
✓ Soldadura circ. (casquetes AL-1C)	C05
✓ Inspección de costuras	C06
✓ Prueba hidraulica 4,0 MPa	C07
✓ Marcado	C08
✓ Tapera de retro	C12
✓ Pintura tercerizada (P6 -> P8)	-
✓ Carga de polvo	T02
✓ Armado de ruedas y manguera	T12
✓ Presurización y etiquetado	T13
✓ Camas terminadas	PTC
✓ Expedición	P9

O9 - I1 - Q11 - T2 - D2 - A2

Flujos

- SE: semielaborado (naranja)
- Tren logístico de un sentido (SE)
- PT: producto terminado (verde)

Secciones: S1 1 kg fabricado; S2 manuales 2,5-10 kg; S3 rodantes 25-100 kg; S4 tercerizados revendidos (con transformación); RC: recargas (servicio, ala propia). Pintura y terminación son comunes a S3 y S4; los carros se pintan alviera. El 1 kg no se registra.

S2 - Matafeugos ABC 2,5 / 5 / 10 kg

Paso	Dónde
✓ Hojes LAC	AL-1H
✓ Corte de cuerpo	M04
✓ Pulmon	P01
✓ Numerado	B01
✓ Cilindrado	B02
✓ Soldadura longitudinal	B03
✓ Encastre de fondo y cupula	B05
✓ Bordonado	B04
✓ Soldadura circunferencial	B06
✓ Prueba hidraulica 100 %	B07
✓ Secado	B14
✓ Granallado	B08
✓ Detección de defectos	B09
✓ Corrección (cuello a P10)	B10
✓ Pulmón a pintura	B11
✓ Pintura (igual que S1)	P02-P06
✓ Terminación (igual que S1)	T03-T11
✓ Almacen de PT	AL-3
✓ Expedición	M1/M2

O4 - I0 - Q10 - T1 - D1 - A1

Paso	Dónde
✓ Hojes LAC	AL-1H
✓ Corte de cuerpo	M04
✓ Pulmon	P01
✓ Numerado	B01
✓ Cilindrado	B02
✓ Soldadura longitudinal	B03
✓ Encastre de fondo y cupula	B05
✓ Bordonado	B04
✓ Soldadura circunferencial	B06
✓ Prueba hidraulica 100 %	B07
✓ Secado	B14
✓ Granallado	B08
✓ Detección de defectos	B09
✓ Corrección (cuello a P10)	B10
✓ Pulmón a pintura	B11
✓ Pintura (igual que S1)	P02-P06
✓ Terminación (igual que S1)	T03-T11
✓ Almacen de PT	AL-3
✓ Expedición	M1/M2

O12 - I1 - Q11 - T1 - D2 - A2

S4 - Tercerizados revendidos (CO2, agua, A...

Paso	Dónde
✓ Recepción	M3
✓ Control de recepción y sello IRAM	S4
✓ Stock	S4
✓ Expedición con el pedido	M1/M2

O0 - I1 - Q10 - T2 - D0 - A1

RC - Recargas (servicio)

Paso	Dónde
✓ Recepción	RC-1
✓ Clasificación en 4 celas	RC-MO
✓ Desarme	RC-DE
✓ Descarga y ensayo de funcionamiento	RC-DC
✓ PH: lavado y secado	RC-PH
✓ Recarga por familia	RC-PV/GALO
✓ Ensamblaje y presurización	RC-EN
✓ Pneo y hermeticidad	RC-EN
✓ Retoque y etiquetado	RC-RP
✓ Para entregar	RC-EN
✓ Despacho	RC-2

O4 - I2 - Q12 - T2 - D0 - A1

Fecha	Nombre	Propietario	Reemplaza a / Reemplazado por
02/10/2026	Claude Code	FLAMA S.A.	-
Revisó		Denominación	Material
Aprobó			
Escala	Método de proyección	Flujo de operaciones	
1:200	ISO E	Secuencia de operaciones por sección - año 10	
Unidades	Formato	Diagrama de proceso	
Cotas en m	A0	FL_PI_02	