# FL_PI10_01 - PLANTA GENERAL E IMPLANTACIÓN, ZONAS Y SUPERFICIES

Calle al norte: administración y servicios al personal al norte de la nave (croquis del usuario). Cada m² de la nave tiene código y nombre (verificado).

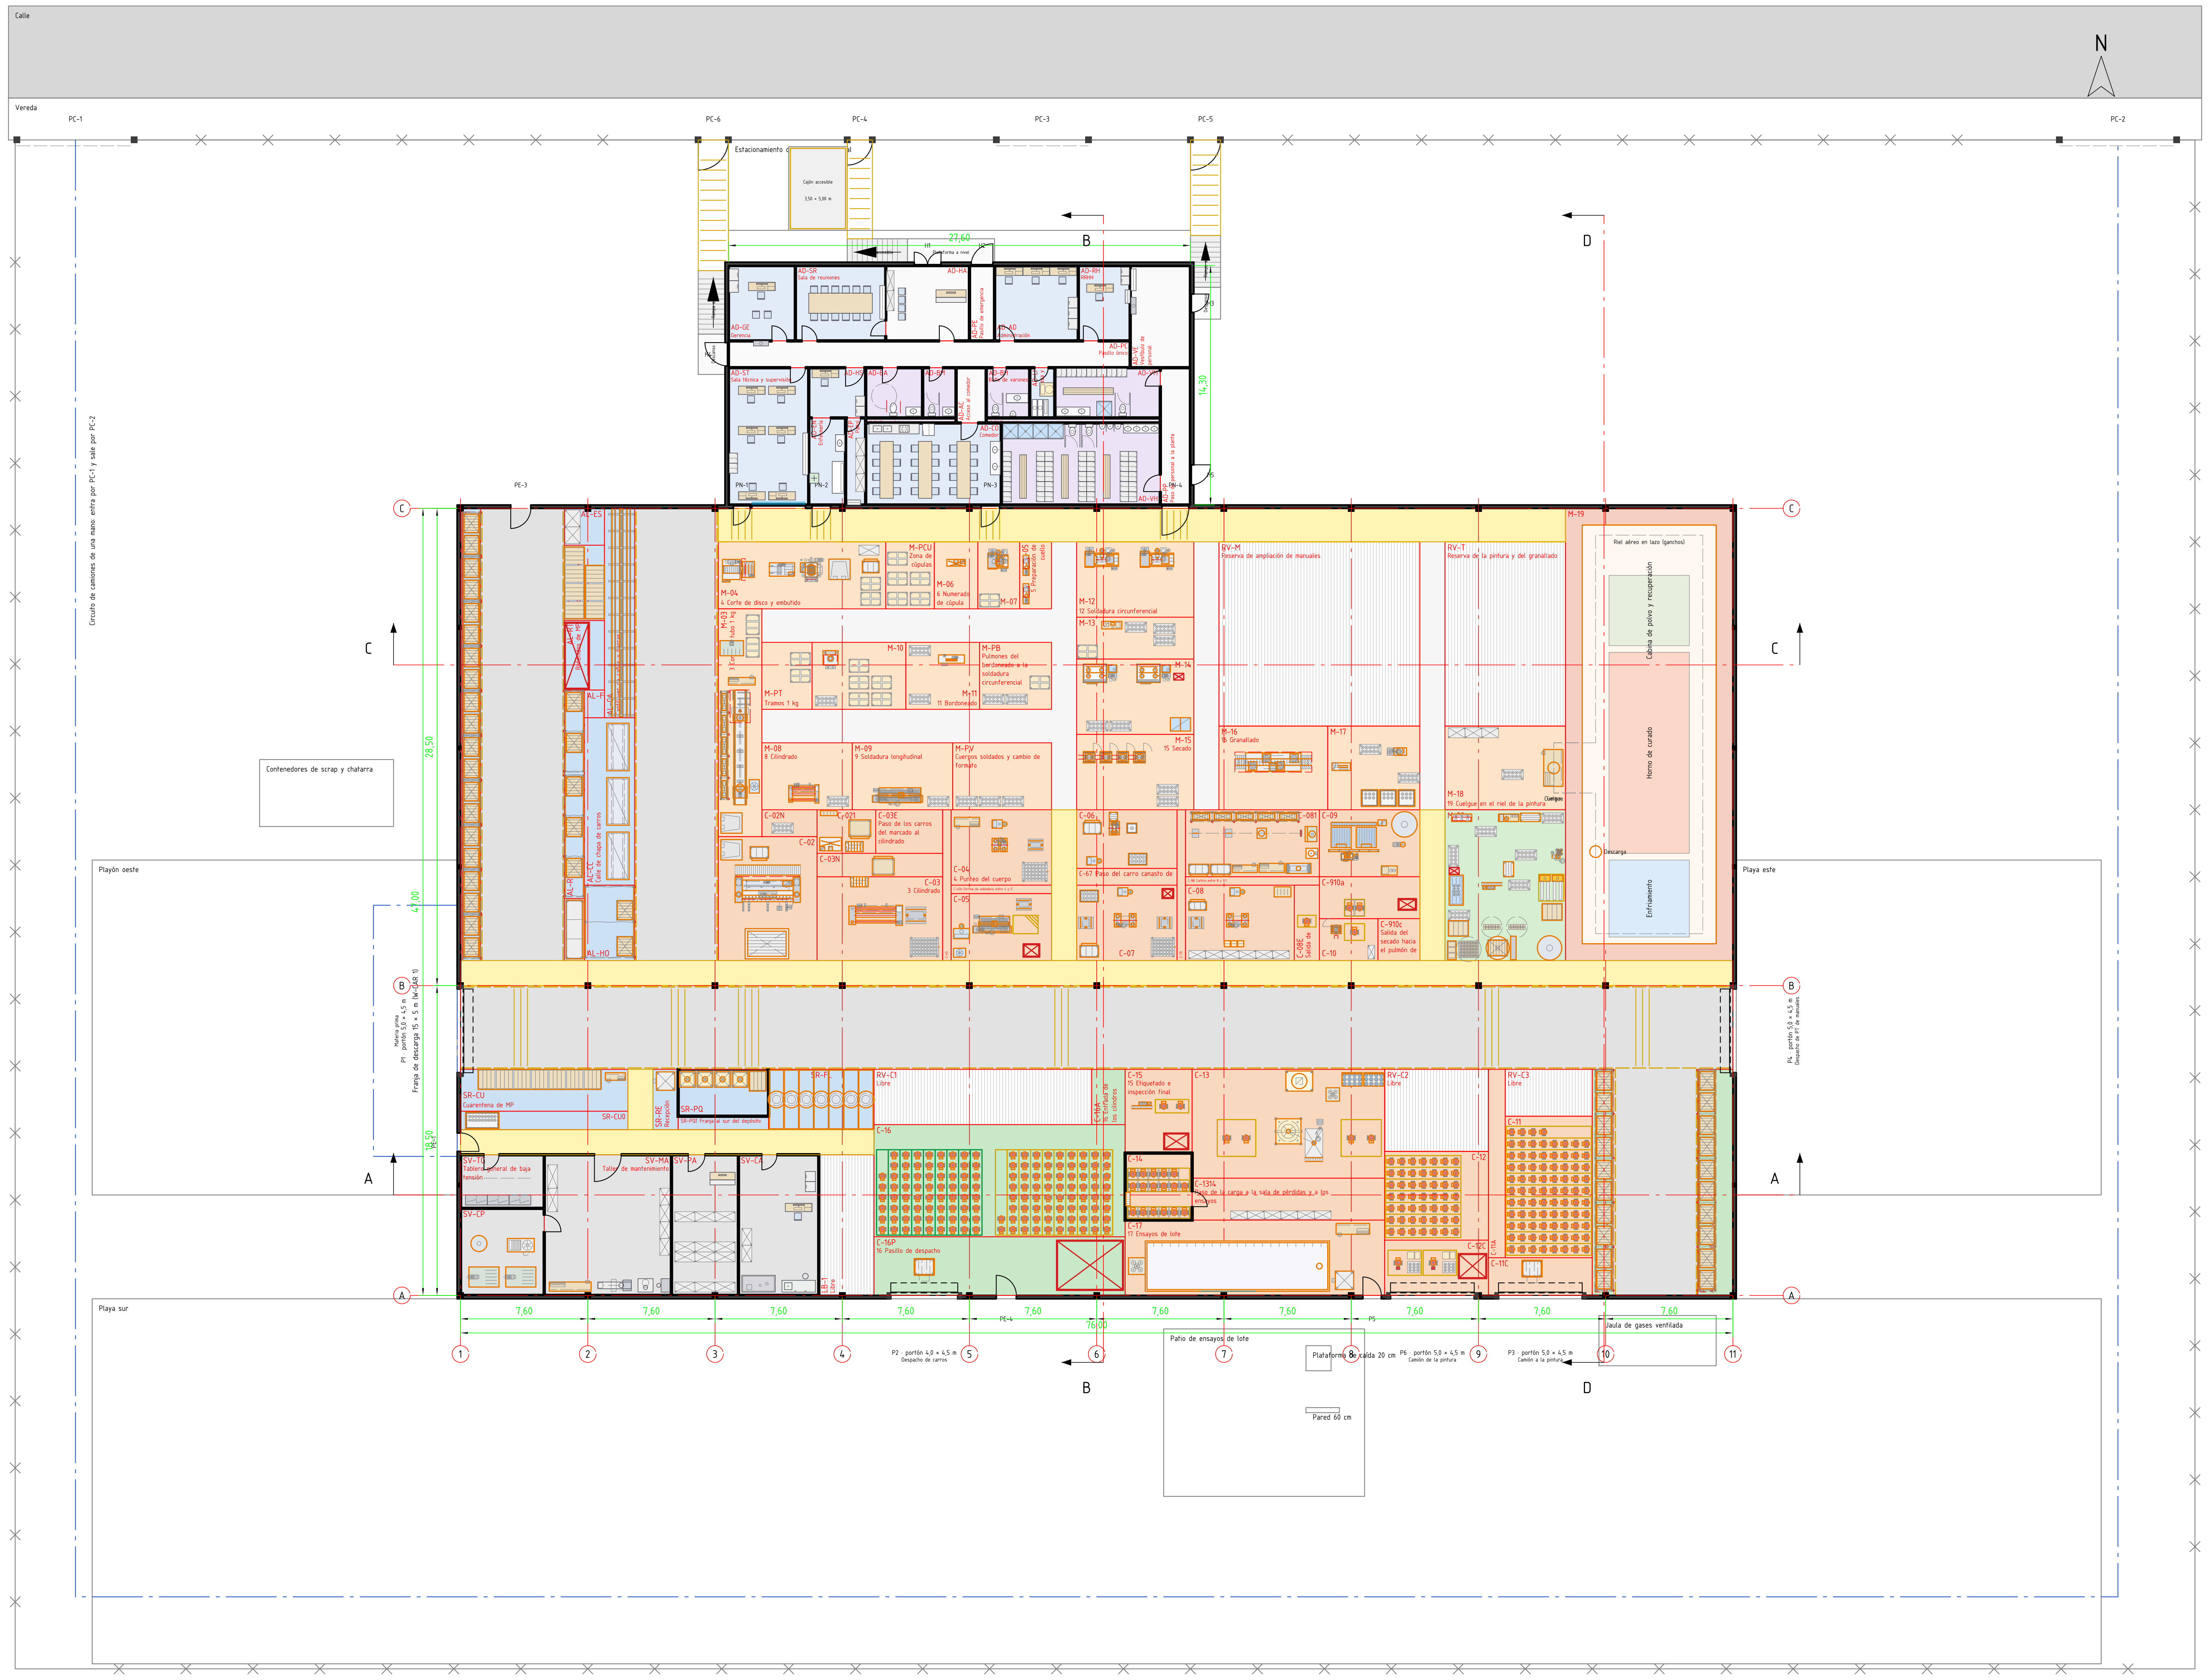

## Zonas de la nave y del anexo (m² del plano y m² que pide la fuente)

| Código | Zona | m² | Fuente |
|---|---|---|---|
| AL-R1 | Rack selectivo R1, 4 niveles | 29,7 | - |
| AL-W | Franja del muro oeste | 2,7 | - |
| AL-AB | Estacionamiento de los carros de abastecimiento | 4,4 | - |
| AL-RC | Racks de carros | 14,9 | 14,7 |
| AL-RT | Retenidos de MP | 10,0 | 6,0 |
| AL-PV | Pilas de pallets vacíos | 10,8 | - |
| AL-ES | Estantería de cajas | 5,3 | - |
| AL-HO | Rack de chapas por espesor | 13,5 | - |
| AL-CC | Calle de chapa de carros | 30,0 | 20,0 |
| AL-F | Franja detrás del cantiléver | 2,0 | - |
| AL-CA | Cantiléver de caños y barras | 22,5 | - |
| SR-CU | Cuarentena de MP | 25,0 | 25,0 |
| SR-CU0 | Jaula de tubos de gas y paso detrás de la cuarentena | 11,0 | - |
| SR-RE | Recepción | 5,4 | - |
| SR-PQ | Depósito de polvo químico y pintura en polvo | 15,1 | - |
| SR-PQ1 | Franja al sur del depósito de polvo | 4,3 | - |
| SR-FL | Bobinas de fleje | 22,7 | 22,0 |
| M-04 | 4 Corte de disco y embutido | 40,0 | 26,0 |
| M-PCU | Zona de cúpulas | 11,6 | - |
| M-06 | 6 Numerado de cúpula | 10,4 | 2,3 |
| M-07 | 7 Soldadura del cuello a la cúpula | 10,0 | 5,3 |
| M-05 | 5 Preparación de cuello | 7,6 | 4,5 |
| M-03 | 3 Corte de tubo 1 kg | 35,4 | 25,5 |
| M-PT | Tramos 1 kg | 12,0 | - |
| M-10 | 10 Encastre de fondo y zona de fondos | 22,4 | 3,6 |
| M-11 | 11 Bordoneado | 17,6 | 3,6 |
| M-PB | Pulmones del bordoneado a la soldadura circunferencial | 17,2 | - |
| M-08 | 8 Cilindrado | 21,6 | 7,3 |
| M-09 | 9 Soldadura longitudinal | 24,0 | 8,4 |
| M-PV | Cuerpos soldados y cambio de formato | 23,6 | - |
| M-12 | 12 Soldadura circunferencial | 31,5 | 17,5 |
| M-13 | 13 Control de espesor | 17,5 | 2,3 |
| M-14 | 14 Prueba hidráulica | 31,5 | 14,1 |
| M-15 | 15 Secado | 31,5 | 6,0 |
| M-16 | 16 Granallado | 32,5 | 27,4 |
| M-17 | 17 y 18 Detección y corrección de defectos | 27,5 | 9,2 |
| M-18 | 19 Cuelgue en el riel de la pintura | 36,0 | - |
| M-19 | 19 Pintura en polvo + horno | 270,0 | 270,0 |
| M-20 | 20 a 25 Terminación | 64,8 | 47,0 |
| C-02 | 2 Corte de chapa | 43,7 | 44,0 |
| C-02N | Salida de desarrollos de la guillotina a manuales | 5,3 | - |
| C-021 | 2.1 Marcado del cuerpo | 9,1 | 9,0 |
| C-03 | 3 Cilindrado | 37,5 | 35,0 |
| C-03N | Paso de la mesa móvil del marcado al cilindrado | 10,5 | - |
| C-03E | Paso de los carros del marcado al cilindrado | 10,4 | - |
| C-05 | 5 Soldadura longitudinal | 24,0 | 22,0 |
| C-04 | 4 Punteo del cuerpo | 27,0 | 27,0 |
| C-45 | Cortina de soldadura entre 3 y 4/5 | 4,5 | - |
| C-45b | Cortina de soldadura entre 4 y 5 | 3,0 | - |
| C-07 | 7 Armado y soldadura circunferencial | 27,0 | 27,0 |
| C-06 | 6 Soldadura de cupla en la cúpula | 21,0 | 16,0 |
| C-67 | Paso del carro canasto de cúpulas de 6 a 7 | 6,0 | - |
| C-08 | 8 Soldadura de accesorios | 29,2 | 29,0 |
| C-081 | 8.1 Fabricación de accesorios | 32,0 | 32,0 |
| C-78 | Cortina de soldadura entre 7 y 8 | 4,5 | - |

| Código | Zona | m² | Fuente |
|---|---|---|---|
| C-88 | Cortina entre 8 y 8.1 | 4,0 | - |
| C-08E | Salida de los carros sobre su juego provisorio | 6,8 | - |
| C-10 | 10 Secado | 8,8 | 7,5 |
| C-09 | 9 Prueba hidráulica | 24,0 | 22,0 |
| C-910a | Paso de la prueba hidráulica al secado | 15,0 | - |
| C-910c | Salida del secado hacia el pulmón de despacho | 6,2 | - |
| C-17 | 17 Ensayos de lote | 69,8 | 70,0 |
| C-14 | 14 Sala del ensayo de pérdidas | 16,0 | 14,2 |
| C-15 | 15 Etiquetado e inspección final | 20,0 | 9,0 |
| C-13 | 13 Carga, armado y presurización | 74,8 | 60,0 |
| C-1314 | Paso de la carga a la sala de pérdidas y a los ensayos | 28,8 | - |
| C-12 | 12 Pulmón de pintados | 32,9 | 24,5 |
| C-12C | 12 Recepción de pintados | 20,5 | - |
| C-11A | 11 Pasillo de los carros a la puerta | 11,2 | - |
| C-11 | 11 Pulmón de despacho a la pintura tercerizada | 43,9 | 42,0 |
| C-11C | 11 Carga del camión de la pintura | 13,9 | - |
| C-16 | 16 Depósito de PT de carros | 100,5 | 72,0 |
| C-16A | 16 Entrada de los cilindros pintados desde el pasillo principal | 6,6 | - |
| C-16P | 16 Pasillo de despacho | 52,5 | 11,5 |
| PT-M | Almacén de PT de manuales | 17,5 | - |
| PT-M2 | Almacén de PT de manuales | 28,4 | - |
| SV-CP | Sala de compresores y secador de aire | 26,0 | - |
| SV-TG | Tablero general de baja tensión | 16,0 | - |
| SV-MA | Taller de mantenimiento | 63,8 | - |
| SV-PA | Pañol de herramientas y repuestos | 33,6 | - |
| SV-CA | Laboratorio de control de calidad | 40,3 | - |
| LB-1 | Libre | 27,7 | - |
| RV-M | Reserva de ampliación de manuales | 132,0 | - |
| RV-T | Reserva de la pintura y del granallado | 79,2 | - |
| RV-C1 | Libre | 42,9 | - |
| RV-C2 | Libre | 30,4 | - |
| RV-C3 | Libre | 14,6 | - |
| AD-GE | Gerencia | 18,0 | - |
| AD-SR | Sala de reuniones | 24,3 | - |
| AD-HA | Hall de recepción y espera de visitas | 22,5 | - |
| AD-PE | Pasillo de emergencia | 6,8 | - |
| AD-AD | Administración | 22,5 | - |
| AD-RH | RRHH | 14,0 | - |
| AD-VE | Vestíbulo de personal | 22,0 | - |
| AD-PC | Pasillo único | 38,4 | - |
| AD-ST | Sala técnica y supervisión | 39,4 | - |
| AD-HS | Seguridad e Higiene | 10,2 | - |
| AD-EN | Enfermería | 11,4 | - |
| AD-EP | Pañol de EPP | 6,2 | - |
| AD-BA | Baño para personas con discapacidad | 10,2 | - |
| AD-BM | Baño de mujeres | 6,0 | - |
| AD-AC | Acceso al comedor | 5,9 | - |
| AD-BH | Baño de varones | 7,8 | - |
| AD-LI | Limpieza y termotanque | 4,5 | - |
| AD-VM | Vestuario y sanitarios de mujeres | 18,9 | - |
| AD-CO | Comedor | 39,7 | - |
| AD-VH | Vestuario y sanitarios de varones | 46,5 | - |
| AD-PP | Paso de personal a la planta | 14,8 | - |
| AD-PL1 | Plenum sanitario | 1,6 | - |
| AD-PL2 | Plenum sanitario | 3,1 | - |

## Portones de la nave y del predio

| Portón | Uso | Ancho (m) |
|---|---|---|
| P1 | Materia prima: del playón oeste al pasillo principal | 5,0 |
| P2 | Despacho de carros (depósito 16, liberados) | 4,0 |
| P3 | Carga del camión a la pintura tercerizada (puesto 11) | 5,0 |
| P6 | Descarga de los carros pintados (puesto 12) | 5,0 |
| P4 | Playa este: despacho de PT de manuales (al final del pasillo) | 5,0 |
| PC-1 | Entrada de camiones, 7,0 m (criterio: semirremolque) | 7,0 |
| PC-2 | Salida de camiones, 7,0 m (circuito de una mano) | 7,0 |
| PC-3 | Estacionamiento, 5,5 m | 5,5 |
| PC-4 | Peatonal: visitas, gerencia y oficinas | 1,5 |
| PC-5 | Peatonal: operarios (ingreso lateral este) | 1,8 |
| PC-6 | Peatonal: supervisión, PCP, calidad y HyS (oeste) | 1,8 |

## Superficies por destino

| Destino | m² | % de la nave |
|---|---|---|
| Almacén de MP y recepción | 229,3 | 6,4 |
| Manuales 1 a 10 kg | 461,4 | 12,9 |
| Pintura | 270,0 | 7,6 |
| Terminación de manuales | 64,8 | 1,8 |
| Carros 25 a 100 kg | 691,1 | 19,3 |
| Depósitos de producto terminado | 205,5 | 5,8 |
| Servicios técnicos (mantenimiento, calidad, aire, energía) | 179,8 | 5,0 |
| Libre / reserva | 326,8 | 9,1 |
| Pasillos y sendas | 1.143,4 | 32,0 |
| TOTAL NAVE (76,0 × 47,0 m) | 3.572,0 | 100,0 |
| Anexo de administración y servicios (27,6 × 14,3 m) | 394,7 | - |

## Referencias

| | |
|---|---|
| 🟦 | Almacén de MP y recepción |
| 🟧 | Manuales 1 a 10 kg |
| 🟥 | Pintura |
| 🟩 | Terminación de manuales |
| 🟧 | Carros 25 a 100 kg |
| 🟩 | Depósitos de producto terminado |
| ⬜ | Servicios técnicos (mantenimiento, calidad, aire, energía) |
| 🟦 | Oficinas |
| 🟪 | Vestuarios y sanitarios |
| ▨ | Libre / reserva |
| ⬜ | Carril del autoelevador (5,0 m) |
| 🟨 | Senda peatonal demarcada |
| ⬜ | Pasillo de operarios y carros a mano |

## Criterios

Nave de 76,0 × 47,0 m, 10 vanos de 7,6 m; pórticos de 18,5 + 28,5 m con la fila de columnas en el borde norte del carril del autoelevador (ninguna columna dentro de un carril).
Pasillo principal: carril de 5,0 m (Heli CPCD50, W-CAR) + senda de 1,5 m con baranda y cruces.
Almacén con dos pasillos de 5,0 m (AL-A junto a las máquinas de corte, AL-B entre racks).
Portones de la nave (croquis de circuitos de carros): P1 MP 5,0 m (oeste, con la franja de descarga de 15 × 5 m y la cuarentena pegada), P4 PT de manuales 5,0 m (este), P2 despacho de carros 4,0 m, P3 camión a la pintura 5,0 m y P6 regreso de los pintados 5,0 m (sur); P5 patio de ensayos; PE de emergencia.
Predio con cerco: PC-1 entrada y PC-2 salida de camiones (circuito de una mano), PC-3 estacionamiento y PC-4 a PC-6 accesos peatonales del croquis de oficinas. Cortes A-A a D-D en FL_PI10_06.
Carros: reglas del Word de carros con la demanda pico 2035 (X-CAR: 14 recipientes por día, 70 por semana): 84 en el pulmón de despacho, 49 pintados, 17 en la sala de pérdidas, 74 retenidos, 70 liberados y 23 rechazados; lo que no se usa queda libre (RV-C1 a C3). PT de manuales en racks (W-MAN): 100 posiciones de pallet (70 de PT y 17 revendidos de X-ALM). Almacén de MP por secciones de X-ALM.
Reservas (RV y LB): lugar para la máquina siguiente de los puestos de manuales al 92-97 % en 2035 (X-MAN) y el espacio libre del croquis. El largo de la nave lo fijan la fila de carros más la terminación y la pintura (norte) y los puestos 11 a 17 de carros más el PT (sur).

| | Fecha | Nombre |
|---|---|---|
| Dibujó | 15/10/26 | Claude Code |
| Revisó | | |
| Aprobó | | |

Escala: 1:200
Método de proyección: ISO E
Unidades: Cotas en m
Formato: A0
Propietario: FLAMA S.A.
Denominación: Planta general e implantación
Layout 2035 v10 - zonas codificadas y áreas
Tipo de documento: Plano de planta
Reemplaza a / Reemplazado por: -
Material: -
Edición: 0
Fecha de emisión: 15/10/2026
Hoja: 1 / 6
Idioma: es
N° de plano: FL_PI10_01