
FL_PI10_03 – CIRCULACIÓN, FLUJOS DE MATERIALES Y RECORRIDOS DEL PERSONAL

Carriles del autoelevador, sendas peatonales y pasillos de operarios con su ancho; flujo de MP, de semielaborado y de PT; hilos del personal desde los vestuarios.

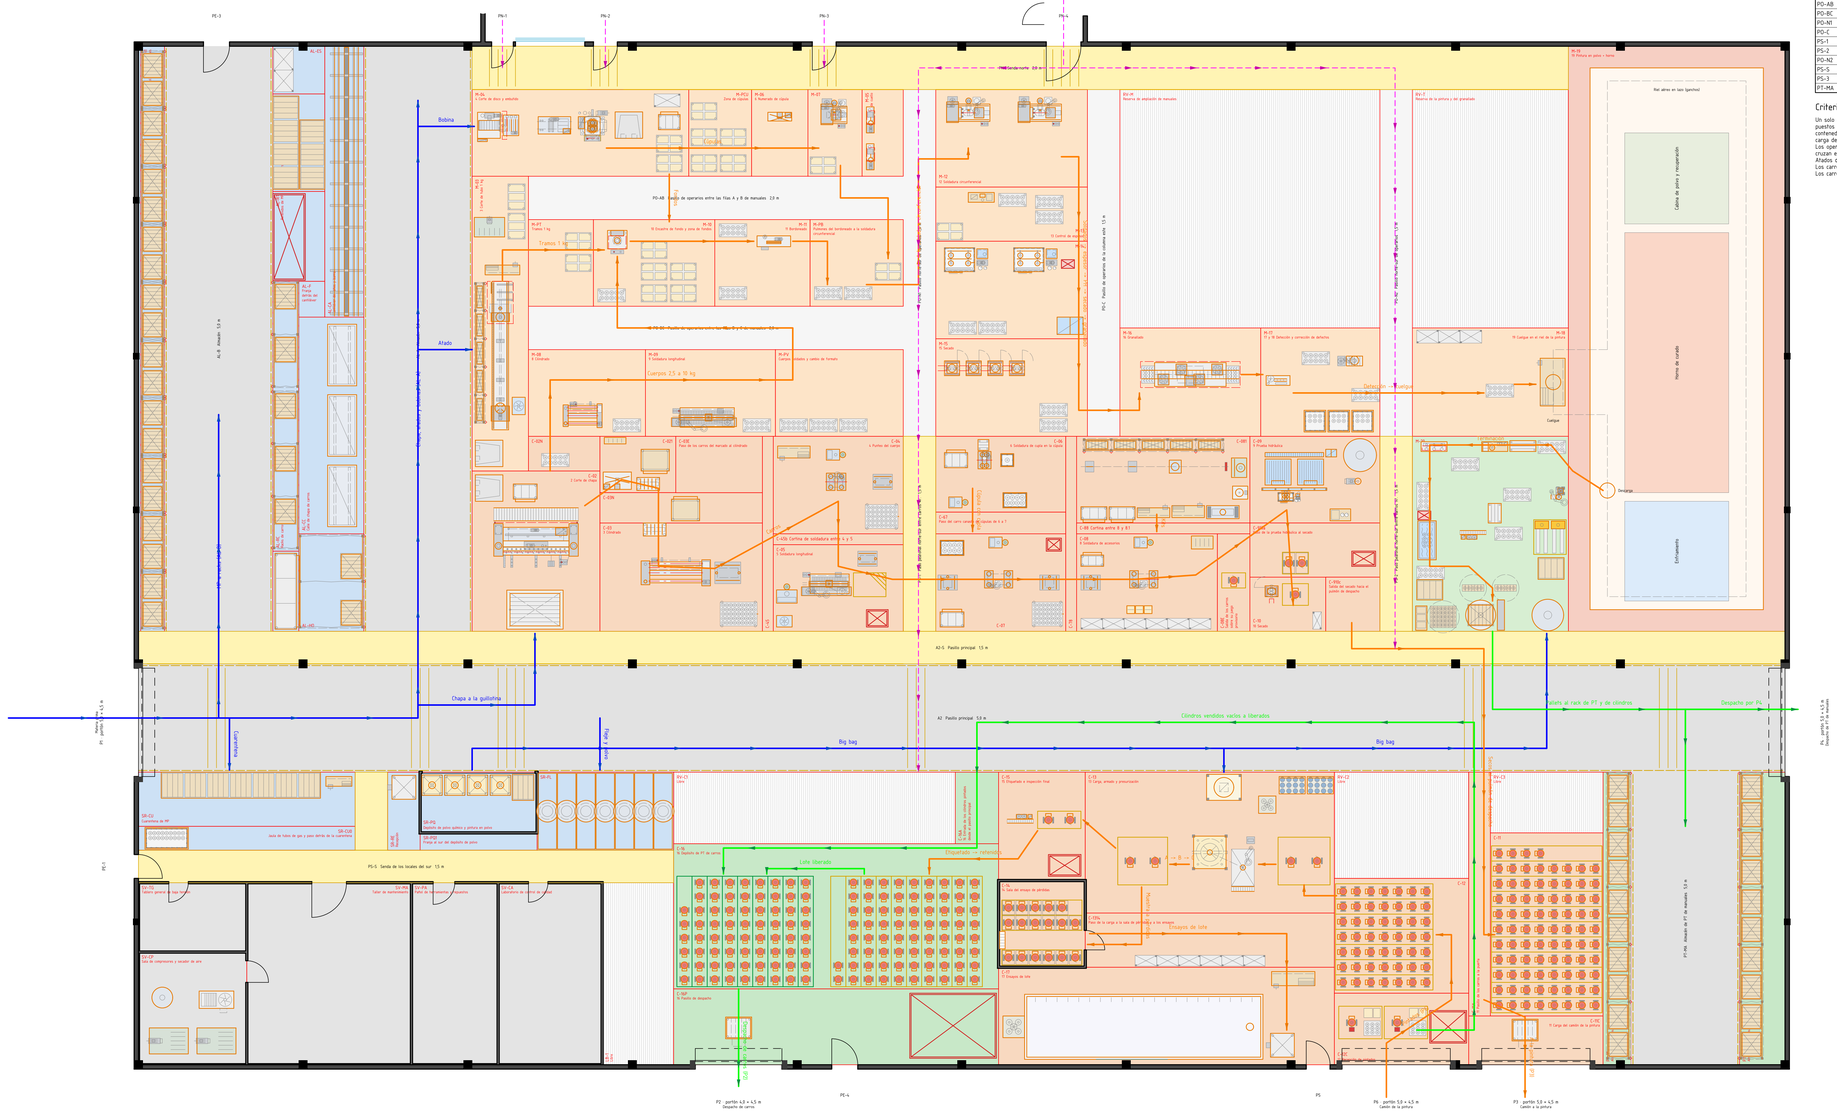

Referencias

- Carril del autoelevador (5,0 m)
- Senda peatonal demarcada
- Pasillo de operarios y carros a mano

Flujos

- MP: materia prima (azul)
- SE: semielaborado (naranja)
- PT: producto terminado (verde)
- Hilos de personal (magenta)

Pasillos (m)

Cód.	Pasillo	Ancho	Largo	Uso
A2	Pasillo principal	5,0	76,0	Autoelevador
A2-S	Pasillo principal	1,5	76,0	Peatonal
AL-A	Almacén	5,0	27,0	Autoelevador
AL-B	Almacén	5,0	27,0	Autoelevador
PN	Senda norte	2,0	50,6	Peatonal
PO-AB	Pasillo de operarios entre las filas A y B de manual	2,0	17,3	Operarios
PO-BC	Pasillo de operarios entre las filas B y C de manual	2,0	17,3	Operarios
PO-M1	Pasillo norte–sur de operarios	1,5	16,0	Operarios
PO-C	Pasillo de operarios de la columna este	1,5	16,0	Operarios
PS-1	Paso peatonal norte–sur entre carros 4/5 y 6/7	1,5	9,0	Peatonal
PS-2	Paso peatonal norte–sur entre carros 9/10 y la tarima	1,5	9,0	Peatonal
PO-N2	Pasillo norte–sur de operarios	1,5	16,0	Operarios
PS-S	Senda de los locales del sur	1,5	24,7	Peatonal
PS-3	Paso peatonal de la senda sur al pasillo principal	1,5	3,6	Peatonal
PT-MA	Almacén de PT de manuales	5,0	13,5	Autoelevador

Criterios de circulación

Un solo autoelevador (Heli CPCD50, W-MAN y W-CAR) circula sólo por A2, AL-A y AL-B (5,0 m) y entra a los puestos únicamente donde la máquina mira al carril: mesa elevadora, cajón del atado, desbobinador, contenedores de scrap, big bags (fermineación y carro 13), envolvedora y calles de PT; las tarimas de carga de los carros (P2, P3 y P6) las toma desde la playa sur.
Los operarios caminan por las sendas (amarillas) y por los pasillos de operarios de 1,5 a 2,0 m; cruzan el carril sólo por los cruces demarcados de la barandilla.
Atados de 6 m se mueven colgados de la pluma (W-MAN 1 y 2), a lo largo del pasillo.
Los carros de manuales (PCHP y de 12 cajones) se empujan a mano entre puestos pegados (W-MAN).
Los carros lavahirores rodarán/ruedan sobre su piego provisorio desde el puesto B (W-CAR).

	Fecha	Nombre
Dibujó	15/10/26	Claude Code
Revisó		
Aprobó		

Escala	1:100
Método de proyección	ISO E
Unidades	Cotas en m
Formato	A0

Propietario: FLAMA S.A.

Denominación: Circulación y flujos

Layout 2035 v10 – pasillos, materiales y personas

Tipo de documento: Plano de circulación

Reemplaza a / Reemplazado por	–
Material	–
Edición	0
Fecha de emisión	15/10/2026
Hoja	3 / 6
Idioma	es
N° de plano	FL_PI10_03