
FL_PI_03 - PERSONAL, EVACUACIÓN Y SEÑALIZACIÓN

Planta industrial FLAMA S.A. - Parque Industrial Villa de Luján, Sarandí (Avellaneda) - dimensionada al año 10 (2035). Escala 1:200. Norte arriba; la calle de acceso está al sur.

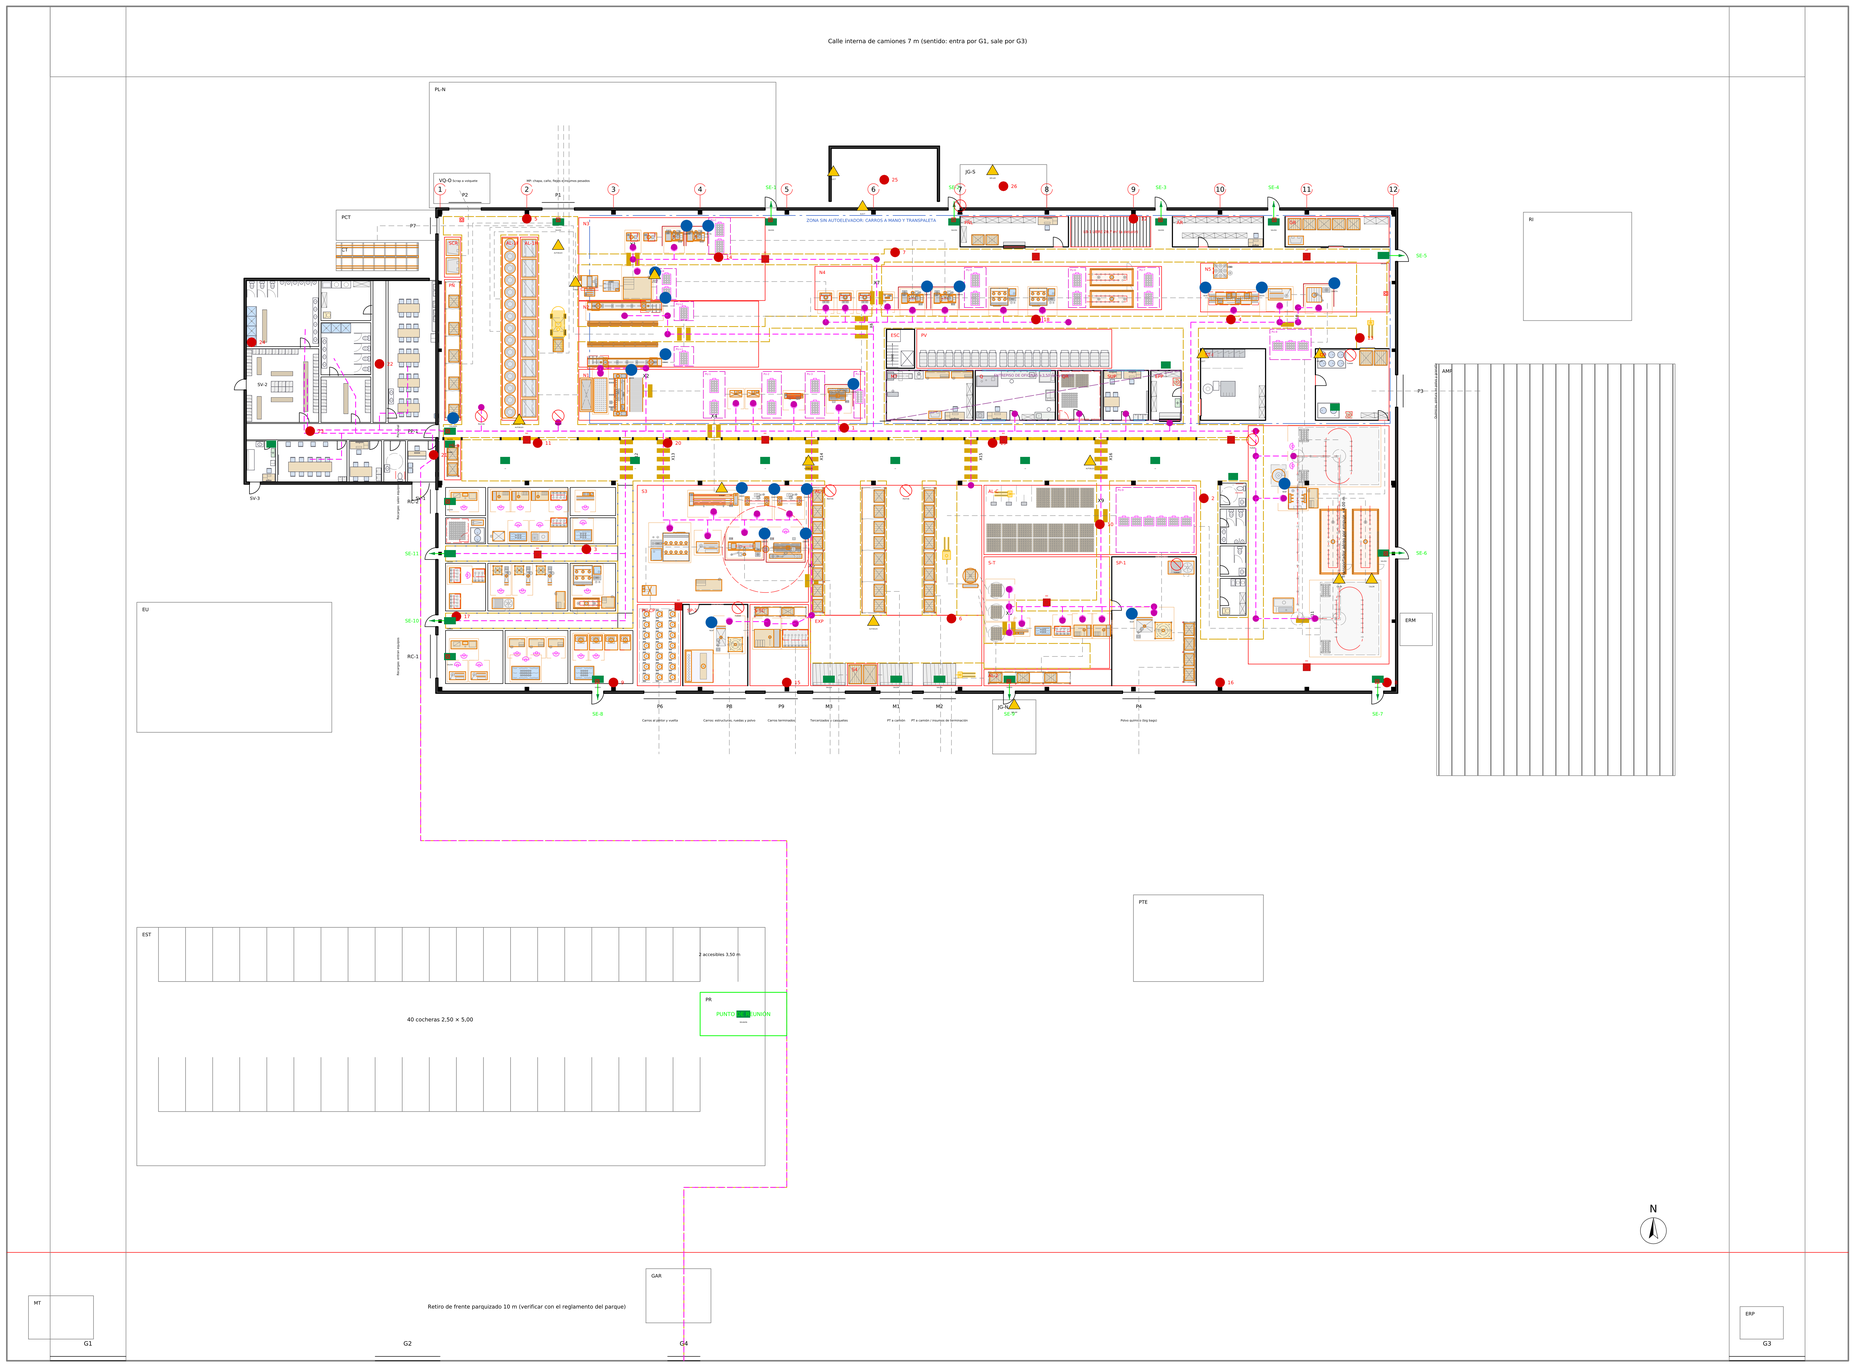

Referencias

Hilo de personal (DIR) y puesto de trabajo

X1..: senda peatonal (cebra) donde un hilo cruza un flujo

Punto rojo numerado: extintor ABC 10 kg · BIE: boca de incendio equipada · □: pulsador de alarma

Señales (IRAM 10005-1: formas y colores de seguridad)

- Advertencia · ATRAP: Riesgo de atrapamiento / cargas suspendidas
- Advertencia · AUTOELEV: Circulación de autoelevadores
- Advertencia · CALOR: Superficie caliente (hornos)
- Advertencia · ELECT: Riesgo eléctrico
- Advertencia · INFLAM: Inflamables / gases a presión
- Obligación · CALZADO: Calzado de seguridad y ropa de trabajo (ingreso a planta)
- Obligación · CARETA: Careta fotosensible y guantes
- Obligación · OIDOS: Protección auditiva
- Obligación · RESP: Respirador P2
- Prohibición · FUMAR: Prohibido fumar y llama abierta
- Prohibición · PEATON: Prohibido el paso de peatones (calle de autoelevador)
- Salvamento y evacuación · +: Primeros auxilios / lavaojos
- Salvamento y evacuación · →: Recorrido de evacuación
- Salvamento y evacuación · PLANO: Plano de evacuación (ingreso PP-1)
- Salvamento y evacuación · REUNIÓN: Punto de reunión
- Salvamento y evacuación · SALIDA: Salida

Evacuación y protección contra incendio

Medios de escape (Dec. 351/79 anexo VII)	Valor
Recorrido máximo real a una salida (grilla 0,5 m, tabiques y equipos)	31,9 m ≤ 40
Ocupación (16 m² por persona en la nave)	242 personas
Unidades de ancho de salida / ancho mínimo	3 / 1,55 m
Salidas de emergencia de 1,10 m con barral antipánico	11
Extintores ABC 10 kg (1 cada 200 m², recorrido ≤ 20 m)	26
Bocas de incendio equipadas / pulsadores de alarma	11 / 14
Sanitarios accesibles (servicios, planta y entrepiso)	3

Longitud de los hilos

Hilo (grupo de puestos)	Desde PP-1 (m)
Almacén de MP y corte (N1)	44
Láseres, cúpulas, unión y PH (N2-N4)	35
Granallado, defectos y pintura (N5, S-P)	52
Terminación, calidad y expedición	48
Línea de carros (S3)	58
Recargas (RC)	34

Sanitarios de vestuarios (art. 49): 55 H y 6 M

Artefacto	H req.	H proy.	M req.	M proy.
Inodoros	3	3	1	4
Lavabos	6	6	1	4
Orinales	6	6	0	0
Duchas	3	4	1	3
Armarios (art. 50)	56	60	7	20

Además: núcleo sanitario de planta (este) con 2 inodoros, 2 mingitorios, 2 lavabos H, 1 inodoro M, sanitario accesible y sala de limpieza, a < 25 m de pintura, terminación y PT. Cada operario tiene 1,0 m libre detrás de su puesto: ninguna calle ni material ajeno pasa por su espalda (verificado). Mamparas ignífugas en todos los puestos de soldadura.

	Fecha	Nombre
Dibujó	03/10/26	Claude Code
Revisó		
Aprobó		

Escala	1:200
Método de proyección	ISO E
Unidades	Cotas en m
Formato	A0
Propietario	FLAMA S.A.
Denominación	Personal y seguridad
	DIR medios de escape, protección contra incendio, IRAM 10005
Tipo de documento	Plano de seguridad e higiene
Reemplaza a / Reemplazado por	-
Material	-
Edición	0
Fecha de emisión	03/10/2026
Hoja	1 / 1
Idioma	es
N° de plano	FL_PI_03