FL_PI_01 - PLANO GENERAL FORMAL NORMALIZADO: PLANTA ACOTADA 1:100

Nave 88 × 44 m, servicios al personal, recargas y sala técnica, con cada máquina, puesto, pulmón, mueble y artefacto a escala. Cotas en metros. Ejes 1 a 12 cada 8,00 m y A-B-C.

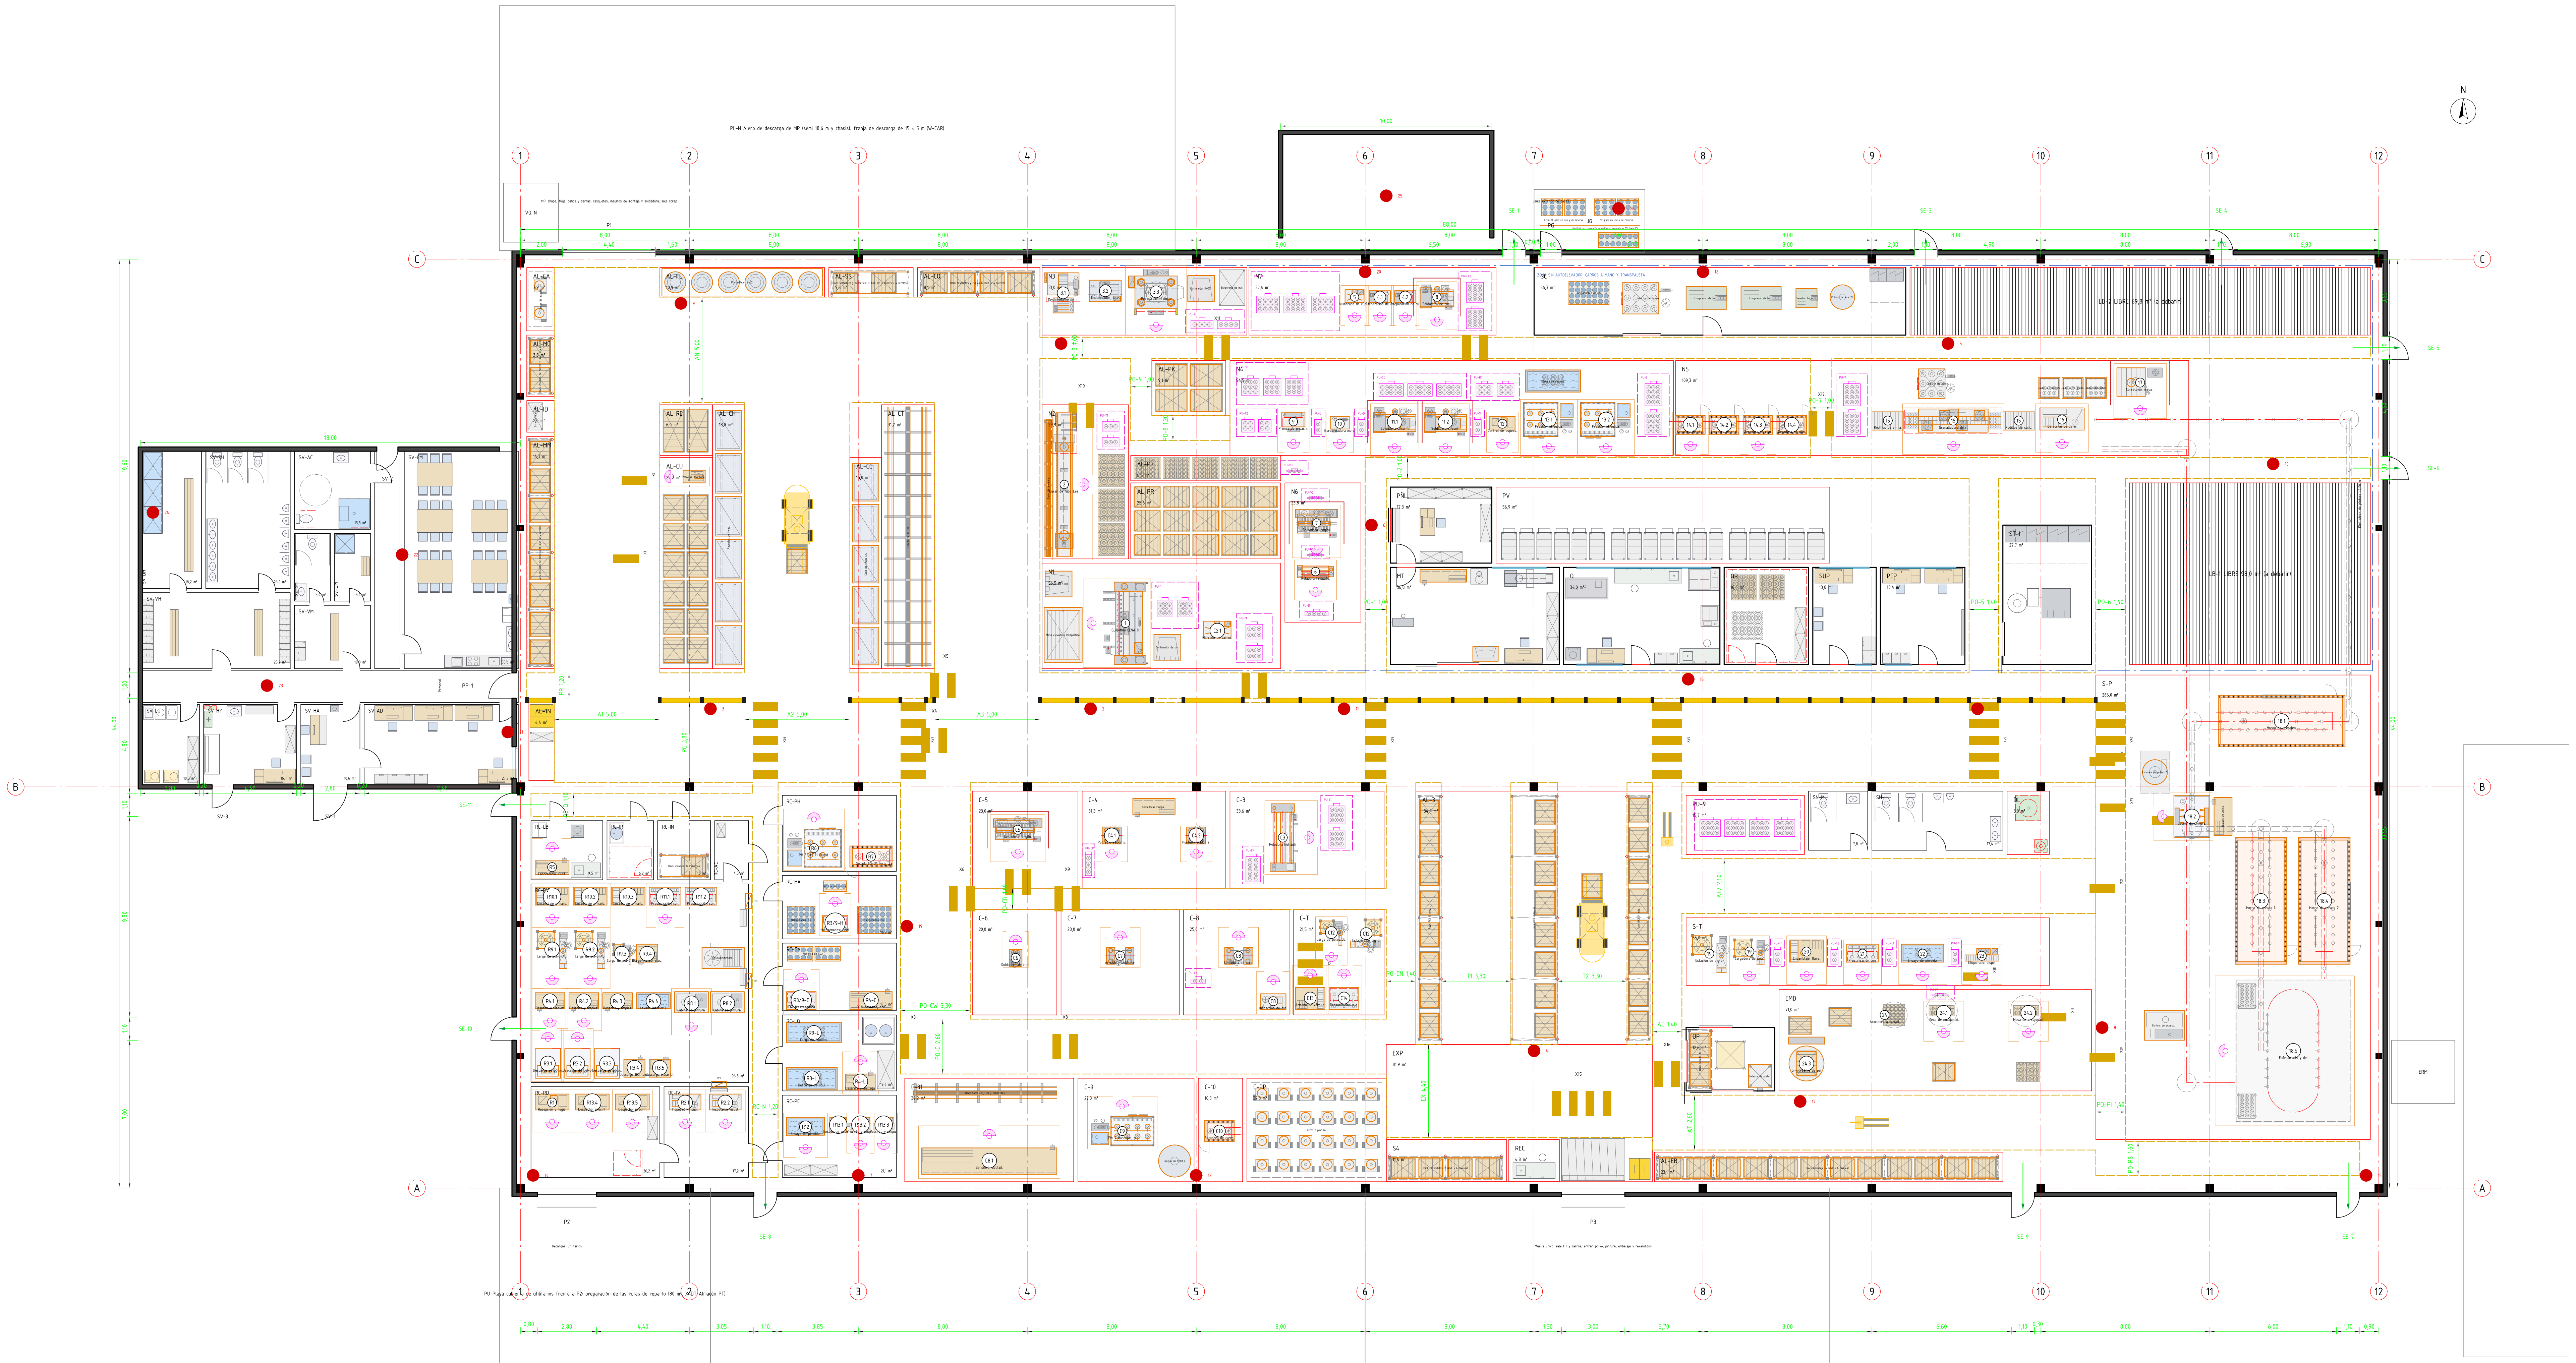

Equipos: medida (cotización o criterio de diseño) y superficie de Guerchet (m²)

Paso	Cód.	Equipo	Medida m	Fuente de la medida	Op.	Ss	St
-	RMM	Rack de insumos de montaje (4 mód. × 4 niv	1,15 × 10,80	X-ALM: 32 posiciones de pallet 1,2 × 1,0	-	12,4	16,9
-	EID	Estantería de identificación (5 niveles)	0,70 × 1,30	X-ALM: estantería de cajas	-	0,9	1,2
-	RMC	Rack de insumos de carros (1 mód. × 4 nive	1,15 × 2,70	X-ALM: 8 posiciones	-	3,1	4,2
-	CAB	Carros de abastecimiento (2)	1,10 × 2,60	W-CAR tabla 5: 3 × 1 m	-	2,9	3,9
-	MI1	Mesa de inspección de recepción (micrómetr	1,20 × 0,60	W-MAN y W-CAR: mesa 1,2 × 0,6	1	0,7	2,0
-	HJ1	Paquetes de hojas LAF (5 posiciones × 2 al	1,40 × 12,20	X-ALM: 7 lugares de 1,22 × 2,44 a 1,5 × 3,0	-	17,1	23,3
-	RF1	Porta-flejes de 3 niveles (24 cunas)	7,60 × 1,30	X-ALM 21 rollos; porta-flejes de MP Opción D	-	9,9	13,5
-	RSS	Rack de soldadura y superficie (1 mód. de	3,70 × 1,15	X-ALM: 12 posiciones	-	4,3	5,8
-	HJ2	Calle de chapa LAC de carros (3 posiciones	1,40 × 9,70	W-CAR: 3 posiciones de 3,0 × 1,5 m	-	13,6	18,5
-	CT1	Cantiléver de caños y barras (3 niveles)	2,30 × 12,30	X-ALM: caño de 6 m + 0,4 m por extremo	-	28,3	38,6
-	RCQ	Rack de casquetes y cuplas (2 mód. × 4 niv	5,40 × 1,15	X-ALM: 11 posiciones	-	6,2	8,5
-	BP1	Balanza de plataforma 1,20 × 1,20 m, 1.500	1,20 × 1,20	W-MAN y W-CAR: balanza de plataforma compartid	-	1,4	2,0
-	M02	Mesa elevadora de tijera 3 t (compartida)	1,80 × 2,60	W-MAN y W-CAR: 2,6 × 1,8 m	-	4,7	6,4
1	M04	Guillotina CENA 8 × 3200 (compartida)	2,10 × 3,90	W-CAR: ≈ 3,9 × 2,1 m (a confirmar con Cena)	1	8,2	22,3
-	SCG	Contenedor de scrap 1.000 L con volcador	1,47 × 1,42	W-CAR: 1470 × 1420 mm detrás de la guillotina,	-	2,1	2,8
C2.1	MK1	Marcado de carros: mesa 1,4 × 1,0 y marcad	1,40 × 1,00	W-CAR 2.1: lo atiende el operario de corte	-	1,4	1,9
-	CJ1	Cajón de alimentación 0,5 × 0,5 × 6,5 m (a	0,50 × 6,50	W-MAN: el autoelevador deja el atado y se desf	-	3,2	4,4
2	M16	Láser de tubo Leapion 1,5 kW con chiller	0,80 × 6,85	Cotiz. Leapion; W-MAN: recorrido útil 6150 mm	1	5,5	14,9
-	SCL	Contenedor 1.000 L de recortes del láser	1,47 × 1,42	W-MAN: junto a la máquina, lo vacía el autoele	-	2,1	2,8
6	B02	Roladora Firesafer FS-RM01	1,70 × 0,80	W-MAN: trifásica 380 V, 4 kW (huella de catálo	1	1,4	3,7
7	B03	Soldadora longitudinal Firesafer (MAG)	2,00 × 1,40	Cotiz. Firesafer; W-MAN	1	2,8	7,6
3.1	M06	Desbobinador de eje horizontal con carro p	1,80 × 2,00	W-MAN: rollo parado, cargado con el espolón de	-	3,6	4,9
3.2	M07	Enderezador, lubricante y alimentador serv	1,60 × 1,20	Cotiz. Cena PRE-1 (Drive)	-	1,9	2,6
3.3	M08	Prensa embutidora Sangiacomo	2,60 × 2,20	W-MAN: corta el disco y embute en el mismo gol	1	5,7	15,6
-	SCP	Contenedor 1.000 L del esqueleto (sobre ru	1,47 × 1,42	W-MAN: el cortador trocea el esqueleto al cont	-	2,1	2,8
-	EM	Estantería de matrices (8 juegos) y carro	1,20 × 1,70	W-MAN: 8 juegos, al lado de la prensa	-	2,0	2,8
5	M10	Numerado de cúpula: micropercusión Pannier	1,00 × 0,80	W-MAN: marcadora de columna sobre banco	1	0,8	2,2
4.1	M09a	Preparación de cuello: prensa de muesca Pa	1,00 × 0,80	W-MAN: prensa de banco neumática 3.500 kg	1	0,8	2,2
4.2	M09b	Preparación de cuello: prensa de muesca Pa	1,00 × 0,80	W-MAN: prensa de banco neumática 3.500 kg	1	0,8	2,2
8	M11	Soldadura de cuello Firesafer FS-HFM1	1,60 × 1,20	Cotiz. Firesafer FS-HFM1 (plato divisor)	1	1,9	5,2
9	E09	Prensa de encastre Del Fabro 30 t	1,20 × 1,00	W-MAN: prensa hidráulica motorizada, matriz po	1	1,2	3,3
10	B04	Bordoneadora motorizada Pilman SWM-400	1,00 × 0,80	Cotiz. Pilman / Bendmak SWM-400	1	0,8	2,2
11.1	A06	Soldadora circunferencial Firesafer	2,00 × 1,40	W-MAN: cúpula y fondo a la vez, MAG 350 A	1	2,8	7,6
11.2	B06	Soldadora circunferencial Firesafer	2,00 × 1,40	W-MAN: cúpula y fondo a la vez, MAG 350 A	1	2,8	7,6
12	Q01	Control de espesor: mesa y ultrasonido Mel	1,20 × 0,80	W-MAN: mesa al costado de la salida	1	1,0	2,6
13.1	A07	Prueba hidráulica Firesafer FS-JD12A	2,40 × 1,60	Cotiz. Firesafer FS-JD12A (huella de catálogo)	1	3,8	10,5
13.2	B07	Prueba hidráulica Firesafer FS-JD12A	2,40 × 1,60	Cotiz. Firesafer FS-JD12A (huella de catálogo)	1	3,8	10,5
-	DEC	Cámara de decantación y separador de aceit	2,60 × 1,20	W-MAN: compartidos con el ensayo de pérdidas;	-	3,1	4,3
14.1	B14a	Secadora de cilindros (boquilla en el cuel	1,40 × 0,90	W-MAN: secadora Yukon; D gabinete de 4 boquill	1	1,3	3,4
14.2	B14b	Secadora de cilindros (boquilla en el cuel	1,40 × 0,90	W-MAN: secadora Yukon; D gabinete de 4 boquill	-	1,3	1,7
14.3	B14c	Secadora de cilindros (boquilla en el cuel	1,40 × 0,90	W-MAN: secadora Yukon; D gabinete de 4 boquill	1	1,3	3,4
14.4	B14d	Secadora de cilindros (boquilla en el cuel	1,40 × 0,90	W-MAN: secadora Yukon; D gabinete de 4 boquill	-	1,3	1,7
15	RIN	Rodillos de entrada de la granalladora	1,50 × 0,90	W-MAN: los cilindros entran acostados	-	1,3	1,8
15	B08	Granalladora de rodillos AirBlast G-100	4,50 × 1,30	Cotiz. Airblast G-100 4500 × 1300	1	5,8	16,0
-	B13	Colector de polvo de la granalladora	1,80 × 1,40	colector de cartuchos del G-100	-	2,5	3,4
15	ROUT	Rodillos de salida y boquilla de soplado	1,50 × 0,90	W-MAN: soplado del polvo a la salida	-	1,3	1,8
16	B09	Detección de defectos: mesa iluminada	2,20 × 1,20	W-MAN: a continuación de los rodillos de salid	1	2,6	7,2
-	J1	Jaula «a corregir»	1,00 × 1,00	W-MAN: tres jaulas al lado del puesto	-	1,0	1,4
-	J2	Jaula «a re-granallar»	1,00 × 1,00	W-MAN	-	1,0	1,4
-	J3	Jaula «descarte»	1,00 × 1,00	W-MAN	-	1,0	1,4
17	B10	Corrección: mesa y cabina de amolado con e	2,20 × 1,50	W-MAN: amoladora 115 mm, machos y calibres	1	3,3	9,0
18.1	P01	Horno de precalentamiento (túnel a gas)	6,00 × 2,44	W-MAN: saca la humedad antes de la cabina; hue	-	14,6	20,0
18.2	P04	Cabina de pintura 2 × 1,5 m y reciprocador	1,70 × 2,00	Cotiz. Electricolor	1	3,4	9,3
-	P05	Ciclones de recuperación de polvo (2)	1,40 × 2,00	Cotiz. Electricolor	-	2,8	3,8
-	P02	Equipos de aplicación y tolvas EC40-200D	1,00 × 1,80	Cotiz. Electricolor	-	1,8	2,5
18.3	P03	Horno de curado 180-220 °C	2,44 × 6,00	Cotiz. Electricolor 6 × 2,44 m; W-MAN 15 a 20	-	14,6	20,0
18.4	P06	Horno de curado 2 (en paralelo para el pic	2,44 × 6,00	Cotiz. Electricolor 6 × 2,44 m	-	14,6	20,0
18.5	P08	Enfriamiento y descarga: separa vacíos y t	5,50 × 6,80	Cotiz. Electricolor; W-MAN: el flujo se divide	1	37,4	102,0
-	P09	Control de espesor de película y adherenci	2,00 × 1,40	W-MAN: por muestreo, con registro de temperatu	-	2,8	3,8
-	RKP	Rack pesado de big bags y pallets de pintu	1,10 × 2,80	X-ALM: big bags de 1 t y pallets, 11 posicione	-	3,1	4,2
19	BB1	Estación de big bag (ABC 60) con transport	1,80 × 1,80	W-MAN: bastidor con polipasto y transferencia	-	3,2	4,4
19	T01	Cargadora de polvo por vacío Yukon M-00012	1,60 × 1,20	Cotiz. Yukon M-000121; W-MAN	1	1,9	5,2
20	T03	Ensamblaje: llave dinamométrica y estante	1,60 × 1,20	W-MAN: puesto manual	1	1,9	5,2
21	T05	Presurización con N2: pinza Yukon M-000150	1,50 × 1,00	Cotiz. Yukon M-000150; N2 por cañería del pack	1	1,5	4,1
22	T06	Ensayo de pérdidas: tanque de inmersión y	2,00 × 1,00	W-MAN: 6 matafuegos por tanda, 100 mm de agua	1	2,0	5,5
23	T07	Etiquetado: dispensador, posicionador e im	1,60 × 0,80	W-MAN: etiqueta preimpresa + n° de serie y fec	1	1,3	3,5
24.3	T11	Envolvedora de pallets EDOS PS5	1,80 × 1,80	Cotiz. EDOS PS5 (plato Ø1,65 m + columna)	-	3,2	4,4
24	AC1	Armadora automática de cajas (caja del 1 k	2,40 × 1,20	W-MAN: al inicio de las mesas de encajonado (a	-	2,9	3,9
24.1	T09	Mesa de encajonado: terminados	1,60 × 0,80	W-MAN y X-MAN (embalaje 2): al final de la ter	1	1,3	3,5
24.2	T08	Mesa de encajonado: cilindros vacíos	1,60 × 0,80	W-MAN: al lado de la descarga de pintura	1	1,3	3,5
-	RKE	Rack de embalaje (6 mód. × 4 niveles)	16,20 × 1,10	X-ALM: 48 posiciones de cajas plegadas, film y	-	17,8	24,3
-	RK1	Rack RK1 (4 mód. × 5 niveles)	1,10 × 11,60	4 módulos de 2,7 m × 5 niveles (pallet 1,2 × 1	-	12,8	17,4
-	RK2	Rack RK2 doble (4 mód. × 2 × 5 por cara)	2,20 × 11,60	4 módulos de 2,7 m, doble fondo × 5 niveles	-	25,5	34,8
-	RK3	Rack RK3 (4 mód. × 5 niveles)	1,10 × 11,60	4 módulos de 2,7 m × 5 niveles	-	12,8	17,4
-	RKR	Rack de revendidos (2 mód. × 4 niveles)	5,40 × 1,10	X-ALM: 17 posiciones	-	5,9	8,1
C3	C01	Roladora hidráulica CNC W12 8 × 1500	1,40 × 3,20	W-CAR: ≈ 3,2 × 1,4 m (a confirmar)	1	4,5	12,2
C4.1	C02a	Punteo: virador sobre base fija	1,20 × 0,60	W-CAR: 1,2 × 0,6 con 1 m libre en cada boca	1	0,7	2,0
C4.2	C02b	Punteo: virador sobre base fija	1,20 × 0,60	W-CAR; X-DT 2035: 2 puestos	1	0,7	2,0
-	C02s	Soldadoras Pampa 300 y banco con morsa (co	2,00 × 0,90	W-CAR: soldadora 0,9 × 0,5 y banco 1,5 × 0,7	-	1,8	2,5
C5	C04	Soldadora longitudinal ZH-1300 con mesa	2,30 × 1,14	W-CAR: 2,30 × 1,14 m; fuente MIG-350IX y chill	1	2,6	7,2
C6	C06	Soldadura de cupla: mesa Müller con posici	0,90 × 0,60	W-CAR: ≈ 0,9 × 0,6 m	1	0,5	1,5
C7	C05	Armado y soldadura circ.: virador con tope	1,60 × 0,80	W-CAR: ≈ 1,6 × 0,8 m, 1 m libre en cada punta	1	1,3	3,5
C8	C08	Soldadura de accesorios: virador	1,60 × 0,80	W-CAR: ≈ 1,6 × 0,8 m	1	1,3	3,5
C8	C09	Inspección de costuras (mesa)	1,30 × 0,90	X-DT: inspección de costuras int. y ext.	1	1,2	3,2
C12	BB2	Estación de big bag (ABC 90) con transport	1,50 × 1,50	igual a la de manuales (W-MAN)	-	2,2	3,1
C12	T02	Carga de polvo de carros 25 a 100 kg	1,20 × 1,20	carga por vacío con balanza	1	1,4	3,9
C13	T12	Armado de válvula, manguera y tobera	1,40 × 1,20	banco de armado	1	1,7	4,6
C14	T13	Presurización y etiquetado de carros	1,40 × 1,20	banco de presurización + etiquetado	1	1,7	4,6
-	C81r	Rack de barras (6,5 m) y caballetes	6,80 × 1,00	W-CAR 8.1: 6,5 × 0,6 + caballetes 6,8 × 0,6	-	6,8	9,3
C8.1	C81	Sensitiva, dobladora, taladro, prensa 20 t	6,40 × 1,40	W-CAR 8.1: ≈ 8,0 × 4,0 m	1	9,0	24,4
C9	C07	PH: 2 bandejas, pantalla y Yukon M-000200	3,00 × 1,40	Cotiz. Yukon M-000200; W-CAR tabla del puesto	1	4,2	11,5
-	C07t	Tanque de 1.000 L con bomba y filtros (cir	1,56 × 1,56	W-CAR: Rotoplas Ø1,56 m	-	2,4	3,3
C10	C10	Secadora de carros (aire caliente por la c	1,40 × 1,00	secado con boquilla en la cupla	-	1,4	1,9
-	C12	Carros a pintura (6) y carros terminados	6,20 × 4,50	W-CAR: 6 carros 1,1 × 2,2; X-DT 32 m² de carro	-	27,9	38,0
-	CG1	Reguladores de Arcal 21 y N2 (de la jaula	2,00 × 1,20	W-MAN: pack con manifold y cañería a los puest	-	2,4	3,3
-	CH1	Colector de humos de soldadura (filtro de	2,40 × 1,50	colector de cartuchos 6000 m³/h	-	3,6	4,9
-	CP1	Compresor de tornillo 30 kW	1,90 × 1,10	compresor de tornillo 30 kW (1,9 × 1,1)	-	2,1	2,9
-	CP2	Compresor de tornillo 30 kW (reserva)	1,90 × 1,10	compresor de tornillo 30 kW (1,9 × 1,1)	-	2,1	2,9
-	SEC	Secador frigorífico y filtros	1,00 × 0,90	secador para 5 m³/min	-	0,9	1,2
-	TQ1	Pulmón de aire 2000 L	1,20 × 1,20	tanque vertical Ø 1,2 m	-	1,4	2,0
R1	R01	Recepción y registro (escáner y balanza)	1,60 × 0,90	X-DT Análisis Recargas 2035; W-REC	1	-	-
R13.4	R17a	Despacho: precinto, remito y carga	1,60 × 0,90	X-DT Análisis Recargas 2035; W-REC	1	-	-
R13.5	R17b	Despacho: precinto, remito y carga	1,60 × 0,90	X-DT Análisis Recargas 2035; W-REC	1	-	-
R2.1	R19a	Inspección visual (pesa el CO2 y el haloge	1,60 × 0,90	X-DT Análisis Recargas 2035; W-REC	1	-	-
R2.2	R19b	Inspección visual	1,60 × 0,90	X-DT Análisis Recargas 2035; W-REC	1	-	-
R3.1	R02a	Descarga de polvo ABC FS-SDP-1 (recuperaci	1,20 × 1,40	X-DT Análisis Recargas 2035; W-REC	1	-	-
R3.2	R02b	Descarga de polvo ABC FS-SDP-1 (recuperaci	1,20 × 1,40	X-DT Análisis Recargas 2035; W-REC	1	-	-
R3.3	R02c	Descarga de polvo ABC FS-SDP-1 (recuperaci	1,20 × 1,40	X-DT Análisis Recargas 2035; W-REC	-	-	-
R3.4	R02d	Descarga BC: tambor Yukon M-000030 exclusi	1,00 × 1,00	X-DT Análisis Recargas 2035; W-REC	-	-	-
R3.5	R02e	Descarga clase D: recipiente exclusivo	1,00 × 1,00	X-DT Análisis Recargas 2035; W-REC	-	-	-
R4.1	R04a	Desarme y limpieza: morsa neumática FS-PC	1,40 × 0,90	X-DT Análisis Recargas 2035; W-REC	1	-	-
R4.2	R04b	Desarme y limpieza: morsa neumática FS-PC	1,40 × 0,90	X-DT Análisis Recargas 2035; W-REC	1	-	-
R4.3	R04c	Desarme y limpieza: morsa neumática FS-PC	1,40 × 0,90	X-DT Análisis Recargas 2035; W-REC	-	-	-
R4.4	R05	Lavado interior (si va a PH)	1,60 × 0,90	X-DT Análisis Recargas 2035; W-REC	-	-	-
R8.1	R20a	Cabina de pintura de retoque con extracció	1,60 × 1,10	X-DT Análisis Recargas 2035; W-REC	1	-	-
R8.2	R20b	Cabina de pintura de retoque con extracció	1,60 × 1,10	X-DT Análisis Recargas 2035; W-REC	-	-	-
R9.1	R09a	Carga de polvo ABC por vacío FS-ZR01	1,60 × 1,80	X-DT Análisis Recargas 2035; W-REC	1	-	-
R9.2	R09b	Carga de polvo ABC por vacío FS-ZR01	1,60 × 1,80	X-DT Análisis Recargas 2035; W-REC	1	-	-
R9.3	R09c	Carga de polvo BC (cargadora portátil excl	1,00 × 1,00	X-DT Análisis Recargas 2035; W-REC	-	-	-
R9.4	R16	Carga manual clase D (embudo)	1,00 × 1,00	X-DT Análisis Recargas 2035; W-REC	-	-	-
-	R18	Deshumidificador y filtro de la extracción	2,00 × 1,00	X-DT Análisis Recargas 2035; W-REC	-	-	-
R10.1	R10a	Ensamblaje y marbete: morsa FS-MC	1,60 × 1,00	X-DT Análisis Recargas 2035; W-REC	1	-	-
R10.2	R10b	Ensamblaje y marbete: morsa FS-MC	1,60 × 1,00	X-DT Análisis Recargas 2035; W-REC	1	-	-
R10.3	R10c	Ensamblaje y marbete: morsa FS-MC	1,60 × 1,00	X-DT Análisis Recargas 2035; W-REC	-	-	-
R11.1	R11a	Presurización con N2 FS-N2C (pinza)	1,50 × 1,00	X-DT Análisis Recargas 2035; W-REC	1	-	-
R11.2	R11b	Presurización con N2 FS-N2C (pinza)	1,50 × 1,00	X-DT Análisis Recargas 2035; W-REC	-	-	-
R5	R23	Laboratorio: Puffer (IRAM 3672) y mufla	1,60 × 0,80	X-DT Análisis Recargas 2035; W-REC	1	-	-
-	RRI	Rack de insumos de recargas	2,30 × 1,10	X-DT Análisis Recargas 2035; W-REC	-	2,5	3,5
R12	R12	Ensayo de pérdidas: tanque de inmersión	1,80 × 1,00	X-DT Análisis Recargas 2035; W-REC	1	-	-
R13.1	R22	Ensayo de peso (balanza de precisión)	0,90 × 0,80	X-DT Análisis Recargas 2035; W-REC	-	-	-
R13.2	R21a	Precinto y etiquetado (oblea IRAM, marbete	1,00 × 0,80	X-DT Análisis Recargas 2035; W-REC	1	-	-
R13.3	R21b	Precinto y etiquetado (oblea IRAM, marbete	1,00 × 0,80	X-DT Análisis Recargas 2035; W-REC	1	-	-
R3-L	R26	Descarga de líquidos: IBC 1.000 L (AFFF) y	2,40 × 1,20	X-DT Análisis Recargas 2035; W-REC	-	-	-
R4-L	R25	Desarme y enjuague con boroscopio	1,40 × 0,90	X-DT Análisis Recargas 2035; W-REC	1	-	-
R9-L	R14	Carga de líquidos: premezcla 600 L, bomba	2,60 × 1,10	X-DT Análisis Recargas 2035; W-REC	-	-	-
R3/9-C	R24	CO2: trasvasadora 103/D1 (recupera y carga	1,40 × 1,00	X-DT Análisis Recargas 2035; W-REC	1	-	-
-	R24m	Manifold de CO2: cilindro de suministro y	2,60 × 0,80	X-DT Análisis Recargas 2035; W-REC	-	-	-
R4-C	R13	CO2: desarme, boroscopio, espesores, balan	2,00 × 1,00	X-DT Análisis Recargas 2035; W-REC	-	-	-
-	R27o	Halogenados: cilindros de origen (suminist	1,40 × 1,40	X-DT Análisis Recargas 2035; W-REC	-	-	-
R3/9-H	R27	Halogenados: unidad THB/BP (recupera y car	1,20 × 0,90	X-DT Análisis Recargas 2035; W-REC	1	-	-
-	R27n	N2 o argón con regulador (presurizar)	1,20 × 0,60	X-DT Análisis Recargas 2035; W-REC	-	-	-
-	R27d	Halogenados: cilindros de destino (recuper	1,70 × 1,40	X-DT Análisis Recargas 2035; W-REC	-	-	-
R6	R07	PH FS-HPT1 (3 estaciones, apto CO2) con ja	2,60 × 1,80	X-DT Análisis Recargas 2035; W-REC	1	-	-
R7	R08	Secado FS-D4 (4 cabezales) y cámara de ins	2,00 × 1,00	X-DT Análisis Recargas 2035; W-REC	-	-	-

Guerchet por sector: St = Ss + Sg + Se, k = 0,36

Sector	St Guerchet	Dibujado	Holgura
AL-3	70	134	65
AL-CA	4	4	-0
AL-CC	19	15	-4
AL-CH	23	19	-5
AL-CQ	8	8	-0
AL-CT	39	31	-7
AL-CU	2	25	23
AL-EB	24	23	-1
AL-FL	13	11	-3
AL-ID	1	2	1
AL-MC	4	4	-0
AL-MM	17	14	-3
AL-SS	6	6	-0
C-10	2	10	8
C-3	12	34	21
C-4	6	31	25
C-5	7	23	16
C-6	1	20	19
C-7	3	28	25
C-8	7	25	18
C-81	34	39	5
C-9	15	27	12
C-PP	38	32	-6
C-T	16	21	5
DP	6	13	6
EMB	15	71	56
N1	33	56	23
N2	22	30	8
N3	29	31	2
N4	49	94	46
N5	54	109	56
N6	11	24	12
N7	12	37	26
S-P	181	286	105
S-T	28	55	27
S4	8	11	3
SC	17	56	39

Sg = Ss × N (lados de operación); Se = k (Ss + Sg), k = h móviles / (2 h fijos) = 1,65 / (2 × 2,27). La holgura incluye pulmones, calles y estanterías: donde es grande (N2, N3, AL-3, S-T) queda espacio liberado por las medidas reales de las cotizaciones, para debatir (achicar la nave o reservar ampliación).

Locales y su equipamiento (ningún local vacío)

Local	m²	Equipamiento / función
SV-LU Utilitarios de limpieza	10,3	Pileta de lavado, carros, máquina de piso y artículos de limpieza
SV-HY Higiene y seguridad, medicina laboral,	16,7	Una sola persona: escritorio, camilla, botiquín y lavabo; entrega de EPP por ventani
SV-HA Hall, recepción y fichado	10,6	Reloj biométrico y tablero de novedades al paso; atiende a visitas y proveedores
SV-AD Administración: compras, ventas y RRHH	27,7	4 puestos (compras 1, ventas 2, RRHH 1) y archivo; ventana a la nave a lo largo del
SV-VH Vestuario hombres (60 lockers)	25,2	1 locker por empleado: 2 bloques de 10 columnas × 3 filas = 60 (56 en 2035) y bancos
SV-DH Duchas hombres	18,2	3 duchas sobre la misma pared (art. 49: 55 H en el turno mañana con choferes), banco
SV-SH Inodoros, mingitorios y lavabos hombre	26,0	3 inodoros en la pared norte, 6 mingitorios en la pared este y 6 lavabos en la pared
SV-VM Vestuario mujeres (9 lockers)	10,8	1 bloque de 3 columnas × 3 filas = 9 lockers (7 en 2035) y banco
SV-SM Inodoro y lavabo mujeres	5,4	Art. 49: 6 M por turno -> 1 inodoro y 1 lavabo
SV-DM Ducha mujeres	5,4	1 ducha, separada del inodoro
SV-AC Sanitario accesible con ducha	13,3	Inodoro con 0,80 m libre lateral, lavabo, ducha a nivel con asiento rebatible y barr
SV-CM Comedor (30 plazas) y office	55,6	5 mesas de 6 lejos de la puerta; office con bacha y lavamanos sobre la misma pared;
SN-H Sanitarios hombres (planta)	17,4	2 inodoros y 2 mingitorios (pared norte) y 2 lavabos (pared este)
SN-M Sanitario mujeres (planta)	7,8	1 inodoro y lavabo
RC-RD Recepción, registro y despacho (portón	26,2	Zona general: recepción y registro, despacho (X-DT 2), flota de intercambio y jaulas
RC-IV Inspección visual (zona general)	17,2	2 puestos (X-DT); pasaplatos 1 al recinto de polvo
RC-PV Recinto de polvo químico (HR ≤ 70 %)	96,8	W-REC: descarga, desarme y limpieza, pintura (cabina), carga, ensamblaje y marbete,
RC-LB Laboratorio de polvo y calidad de reca	9,5	Fuera de línea: Puffer y mufla (W-REC 5); patrones con calibración vigente (IRAM 351
RC-IR Inutilización y disposición final	6,2	Fuera de línea (W-REC 14): jaula NO APTO, tambores de residuo; comprobante de cada r
RC-IN Insumos de recargas	7,0	Dimensionamiento_Almacenes_MP_v5: 10 posiciones, 9,6 m² netos: agente limpio, AFFF,
RC-AC Antecámara del recinto de polvo	4,5	W-REC: dos puertas con cierre automático; EPP del recinto
RC-PE Pérdidas, peso, precinto y etiquetado	21,1	Zona general (W-REC 12 y 13): tanque de inmersión, balanza y 2 puestos de etiquetado
RC-LQ Líquidos: agua, AFFF y clase K	19,4	W-REC: fuera del recinto; IBC 1.000 L (AFFF) y tanque 600 L (agua) con tubo buzo y v
RC-GA CO2: recuperación, desarme y carga	17,3	W-REC: trasvasadora 103/D1 con manifold (cilindro de suministro y de recuperación, n
RC-HA Halogenados: circuito cerrado	16,2	W-REC (diagrama de gases): THB/BP al centro; origen a la entrada (extintor, recupera
RC-PH Prueba hidráulica, secado y cámara	19,4	Zona general (W-REC 6 y 7): pasa al recinto por el pasaplatos 3
AL-CU Cuarentena de MP (compartida manuales	25,0	W-MAN y W-CAR tabla 5: 10 × 2,5 m, demarcada en amarillo: 7 pallets, mesa de inspecc
AL-RE Retenidos de MP (no conforme)	6,0	W-CAR tabla 5: 4 × 1,5 m demarcados en rojo, 3 pallets; se reclama al proveedor
AL-1N Gasoil e insumos del autoelevador de M	4,4	Armario de inflamables y estante; el Heli CPCD50 diésel (W-MAN) se estaciona al fina
MT Taller de mantenimiento	36,8	Mantenimiento preventivo: bancos, torno, agujereadora, soldadora móvil; entra la tra
PÑL Pañol de mantenimiento y de línea	17,3	Pegado al taller: repuestos críticos, herramental del preventivo, consumibles de sol
Q Laboratorio de calidad	34,0	Metrología, ensayo de rotura (1 cilindro por lote, W-MAN), adherencia y espesor de p
QR Cuarentena de producto y muestras retenid	18,4	Jaula con llave: lotes rechazados y un cilindro testigo por lote (IRAM 3517 / 3523)
SUP Supervisor de planta	13,8	Oficina propia del encargado de turno, con ventana a la línea y al pasillo central
PCP Planificación y control de la producción	18,4	Separada del supervisor: 2 puestos y tablero de programación con ventana a la línea
PV Supermercado de carros vacíos	56,9	Carros FCHP20505 y de estantes de 12 cajones de reserva y para el cambio de formato
SC Compresores y colector de humos	56,3	Reguladores de Arcal 21 y N2 que vienen de la jaula exterior (puerta PG), colector d
ST-I Tableros y compresor de la cabina	27,7	Tablero de la línea este y compresor sin aceite dedicado a la cabina de pintura
DL Ducha de emergencia y lavaojos	6,0	A menos de 10 s de la carga de polvo, de la presurización y de la descarga de pintur
REC Recepción del muelle: mesa de control	4,8	Remito contra orden de compra y muestra del lote de polvo al laboratorio (humedad) a

IMPLANTACIÓN GENERAL - 1:500

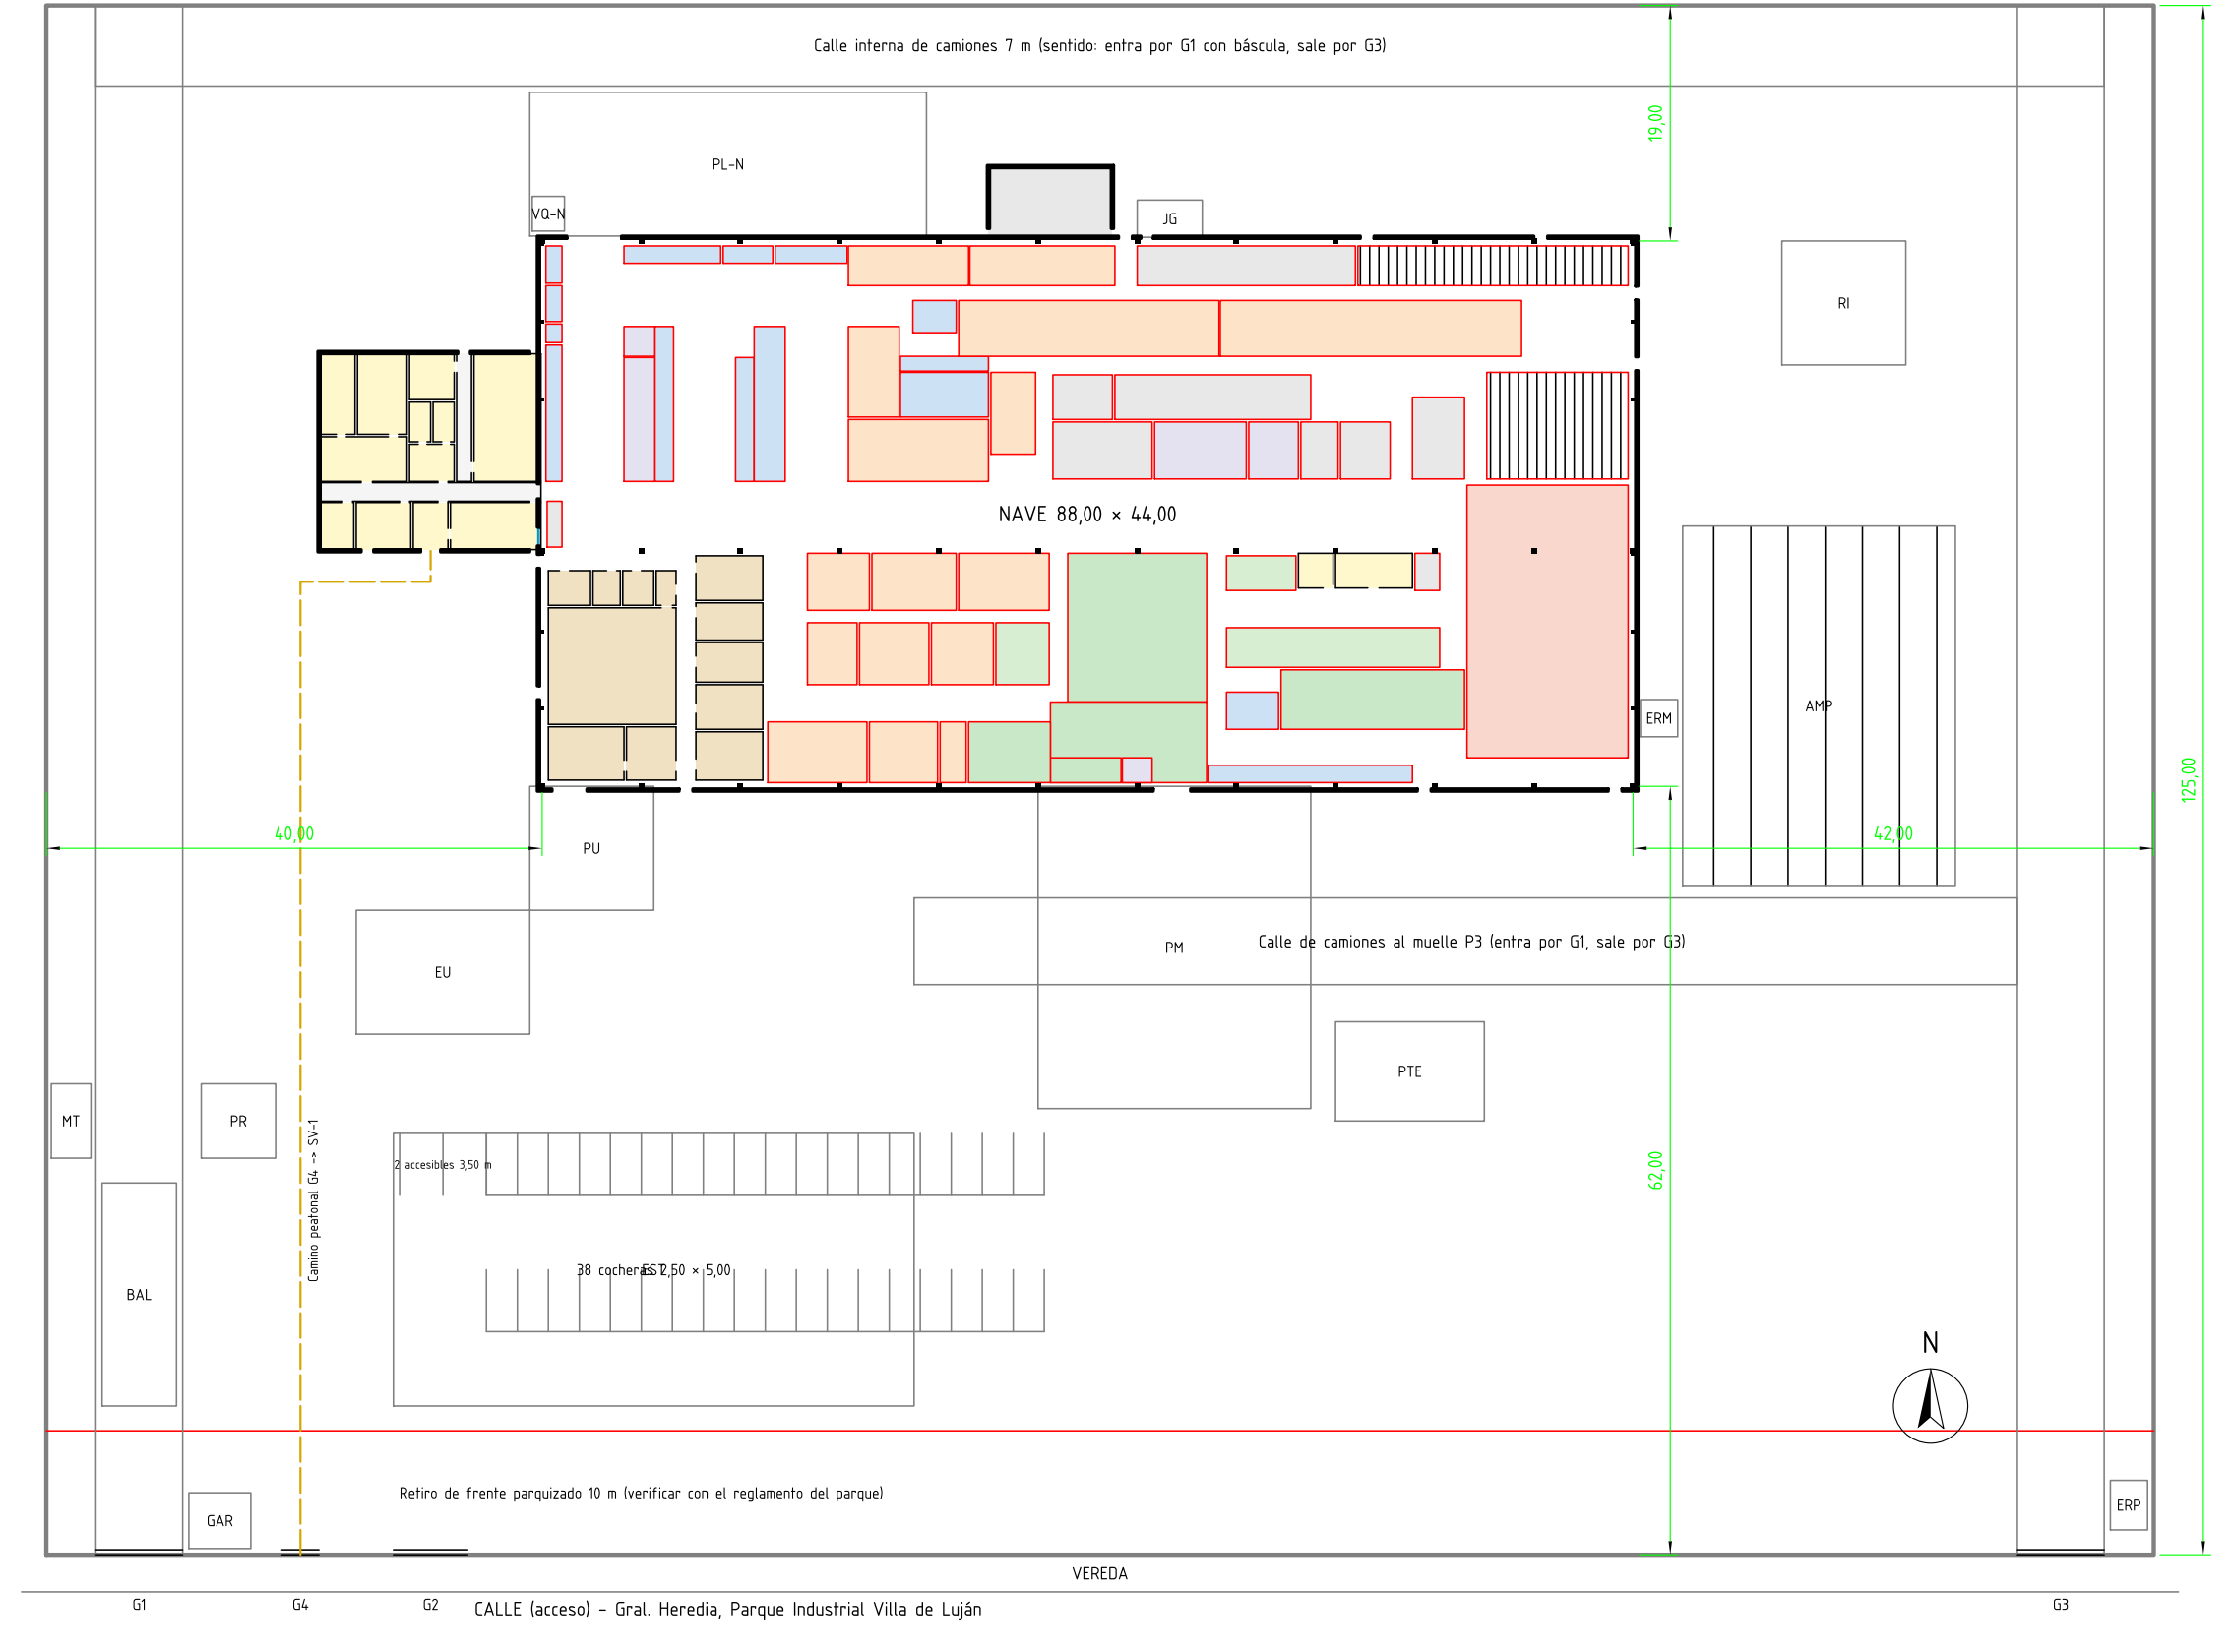
NAVE 88,00 × 44,00
38 cocheras 2,50 × 5,00
2 accesibles 3,50 m
Camino peatonal G4 -> SV-1
Retiro de frente parquizado 10 m (verificar con el reglamento del parque)
VEREDA
G1
G4
G2
G3
CALLE (acceso) - Gral. Heredia, Parque Industrial Villa de Luján
MT
PR
BAL
GAR
ERP
N
62,00

CORTE TRANSVERSAL A-A (por eje 4) - 1:200

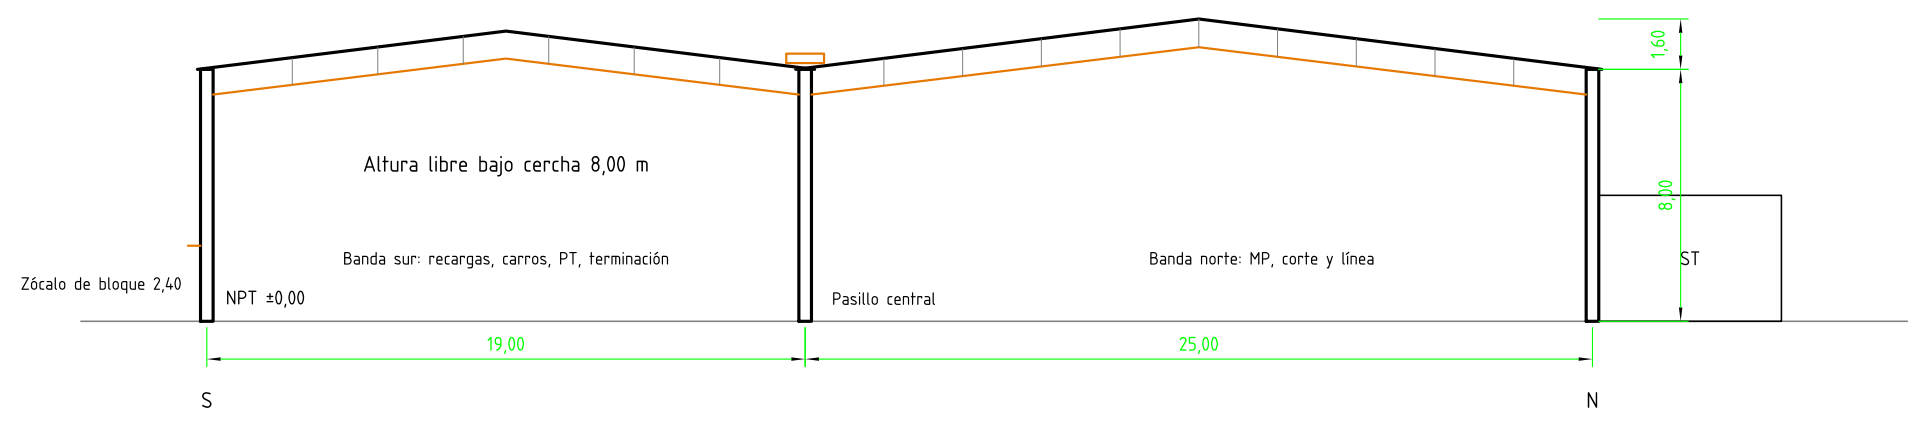
Altura libre bajo cercha 8,00 m
Banda sur: recargas, carros, PT, terminación
Banda norte: MP, corte y línea
Zócalo de bloque 2,40
NPT ±0,00
Pasillo central
19,00
S
N

Cuadro de superficies

Concepto	m²	%
Terreno 170,00 × 125,00	21.250	100,0
Nave industrial 88,00 × 44,00	3.872	18,2
incluye recargas (ángulo SO)	327	
Servicios al personal y oficinas	288	1,4
Sala técnica norte	58	0,3
Alero de descarga de MP	371	1,7
Superficie cubierta total	4.589	21,6
FOS = cubierta / terreno		0,22

Nave: pórticos metálicos de dos luces (19,40 y 24,60 m) cada 8 m; altura libre 8,00 m; zócalo de bloque 2,40 m y chapa; anexos de mampostería. Pisos de hormigón llaneado con demarcación IRAM 10005; sanitarios con revestimiento hasta 2,10 m (Dec. 351/79 cap. 5).

	Fecha	Nombre
Dibujó	14/10/26	Claude Code
Revisó		
Aprobó		

Escala: 1:100

Método de proyección: ISO E

Unidades: Cotas en m

Formato: 2A0

Propietario: FLAMA S.A.

Denominación:
Plano formal:
planta general acotada
Nave, servicios y recargas con equipos y mobiliario; implantación y corte

Tipo de documento: Plano de planta

Reemplaza a / Reemplazado por: -

Material: Estructura metálica / mampostería

Edición: 0

Fecha de emisión: 14/10/2026

Hoja: 1 / 1

Idioma: es

N° de plano: FL_PI_01