
FL_PI_03 – PERSONAL, EVACUACIÓN Y SEÑALIZACIÓN

Planta industrial FLAMA S.A. – Parque Industrial Villa de Luján, Sarandí (Avellaneda) – dimensionada al año 10 (2035). Escala 1:200. Norte arriba; la calle de acceso está al sur.

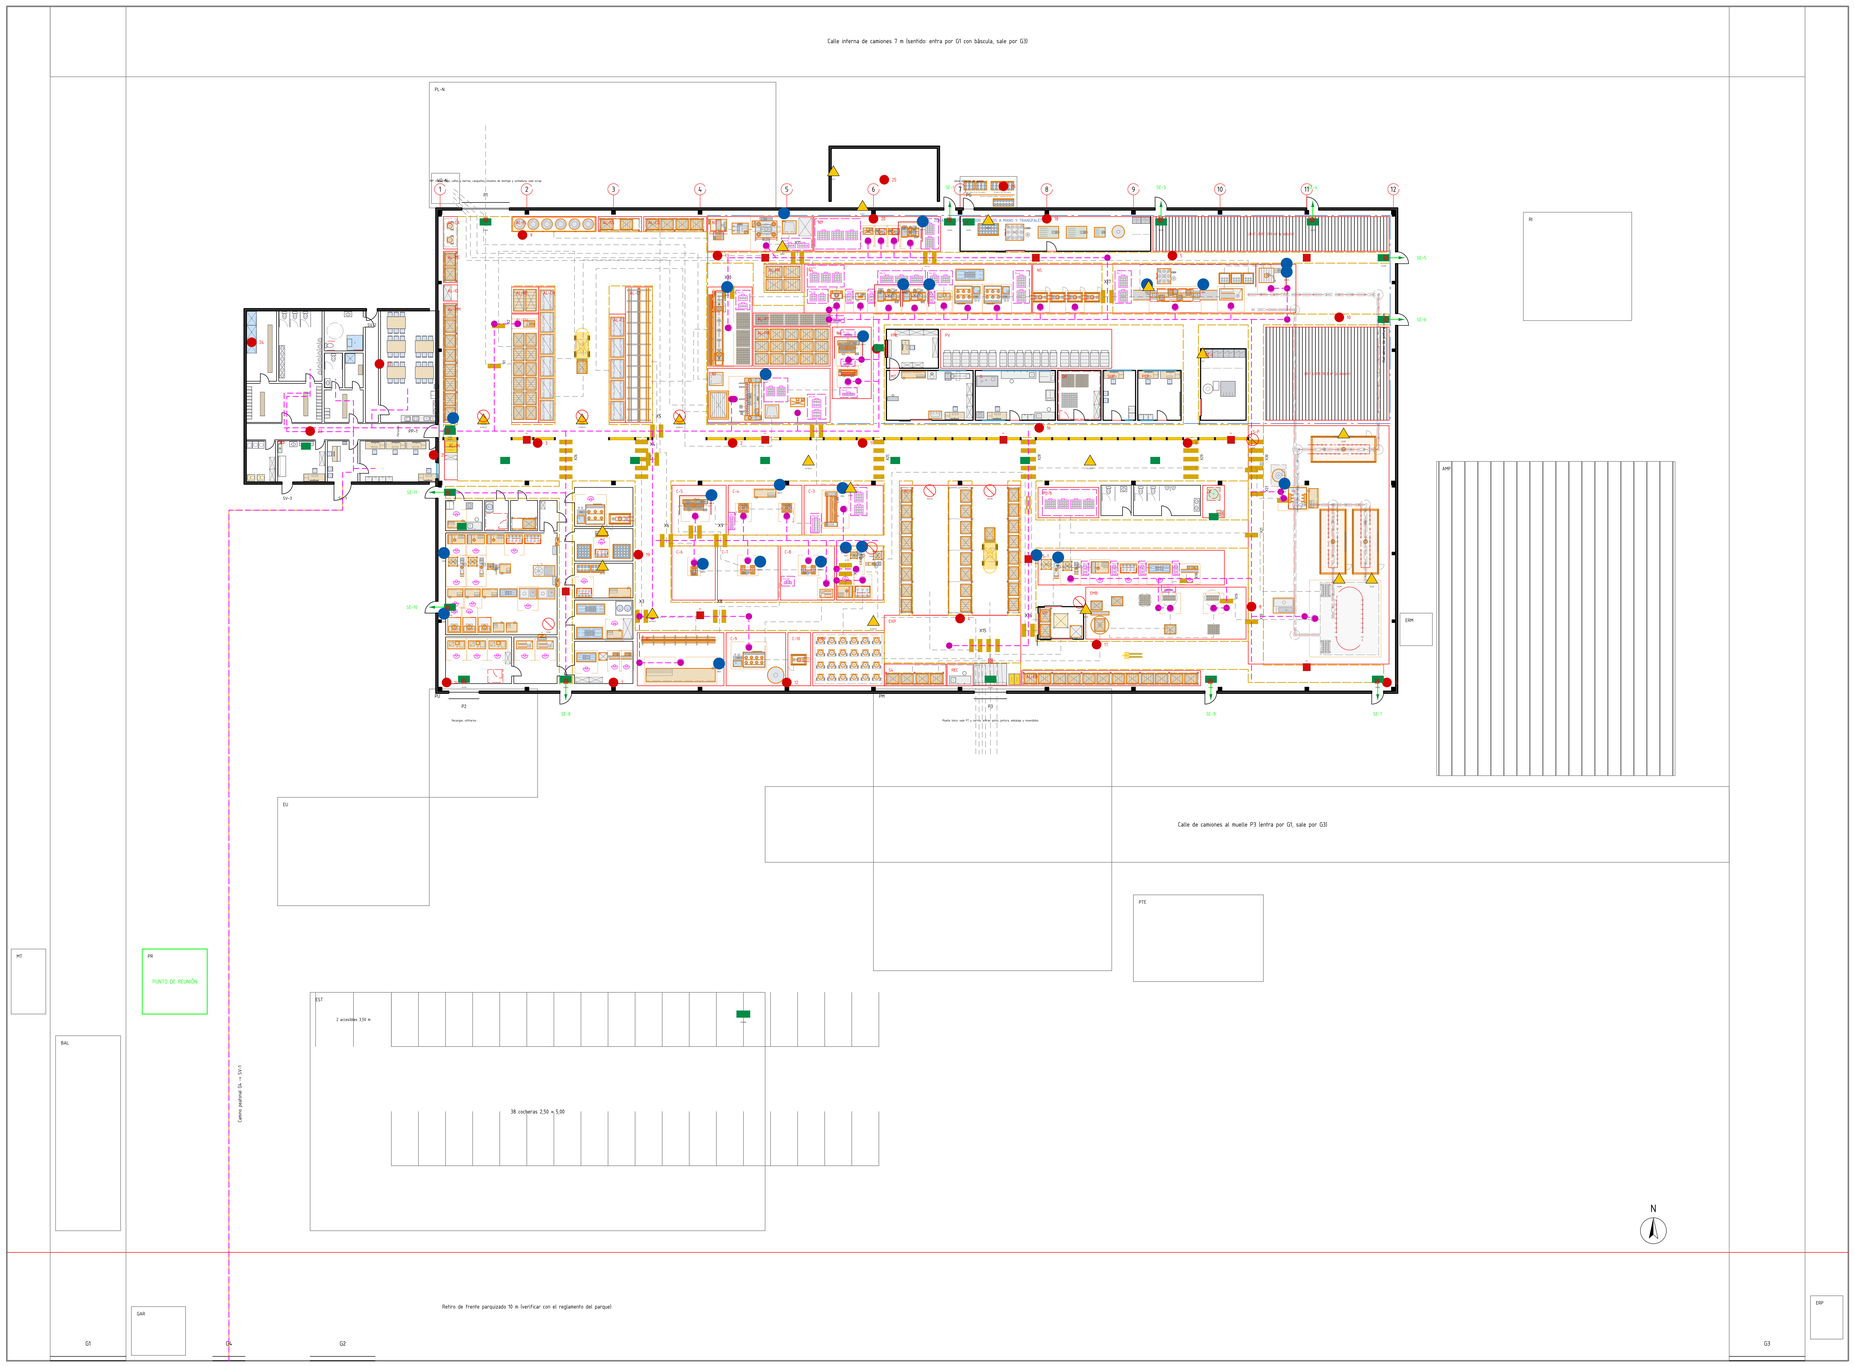

Referencias

Hilo de personal (DIR) y puesto de trabajo

X1…: senda peatonal (cebral donde un hilo cruza un flujo

Punto rojo numerado: extintor ABC 10 kg · BIE: boca de incendio equipada · PU: pulsador de alarma

Señales (IRAM 10005-1: formas y colores de seguridad)

Advertencia · ATRAP: Riesgo de atrapamiento / cargas suspendidas
Advertencia · AUTOELEV: Circulación de autoelevadores
Advertencia · CALOR: Superficie caliente (hornos)
Advertencia · ELECT: Riesgo eléctrico
Advertencia · INFLAM: Gases a presión
Obligación · CALZADO: Calzado de seguridad y ropa de trabajo (ingreso a planta)
Obligación · CARETA: Careta fotosensible y guantes
Obligación · OIDOS: Protección auditiva
Obligación · RESP: Respirador P2
Prohibición · FUMAR: Prohibido fumar y llama abierta
Prohibición · PEATON: Prohibido el paso de peatones (calle de autoelevador)
Salvamento y evacuación · +: Primeros auxilios / lavaojos
Salvamento y evacuación · ←: Recorrido de evacuación
Salvamento y evacuación · PLANO: Plano de evacuación (ingreso PP–1)
Salvamento y evacuación · REUNIÓN: Punto de reunión
Salvamento y evacuación · SALIDA: Salida

Evacuación y protección contra incendio

	Valor
Medios de escape (Dec. 351/79 anexo VIII)	
Recorrido máximo real a una salida (grilla 0,5 m, tabiques y equipos)	36,9 m ≤ 40
Ocupación (16 m² por persona en la nave)	242 personas
Unidades de ancho de salida / ancho mínimo	3 / 1,55 m
Salidas de emergencia de 1,10 m con barral antipánico	10
Extintores ABC 10 kg (1 cada 200 m², recorrido ≤ 20 m)	26
Bocas de incendio equipadas / pulsadores de alarma	11 / 54
Sanitario accesible con ducha (bloque de servicios)	1

Longitud de los hilos

Hilo (grupo de puestos)	Desde PP–1 (m)
Recepción, corte de chapa y marcado (N1)	46
Cuerpo, unión y PH (N4, N6)	33
Secado, granallado y deflexión (N5)	37
Láser, embutido y ceja de cuello (N2, N3, N7)	41
Pintura, terminación y embalaje	40
PT y expedición	27
Línea de carros (S3)	40
Recargas (RC)	34

Sanitarios de vestuarios (art. 49): 55 H y 6 M

Artefacto	H req.	H proy.	M req.	M proy.
Inodoros	3	3	1	1
Lavabos	6	6	1	1
Orinales	6	6	0	0
Duchas	3	3	1	1
Armarios (art. 50)	56	60	7	9

Además: sanitarios de planta (banda sur, calle ATZ) de hombres (2 inodoros, 2 mingitorios, 2 lavabos) y de mujeres (1 + 1, a + 25 m de pintura, terminación, embalaje y PT; Lockers: 1 por empleado. Cada operario tiene 1,5 m libre detrás de su puesto: ninguna calle ni material ajeno pasa por su espalda (verificado). Mamparas ignífugas en todos los puestos de soldadura.

	Fecha	Nombre
Dibujó	14/10/26	Claude Code
Revisó		
Aprobó		

Escala	1:200
Método de proyección	ISO E
Unidades	Cotas en m
Formato	A0
Propietario	FLAMA S.A.
Denominación	Personal y seguridad
	DIR, medios de escape, protección contra incendio, IRAM 10005
Tipo de documento	Plano de seguridad e higiene
Reemplaza a / Reemplazado por	–
Material	–
Edición	0
Fecha de emisión	14/10/2026
Hoja	1 / 1
Idioma	es
N° de plano	FL_PI_03