
FL_PI10_01 – PLANTA GENERAL E IMPLANTACIÓN, ZONAS Y SUPERFICIES

Calle al norte: administración y servicios al personal al norte de la nave (croquis del usuario). Cada m² de la nave tiene código y nombre (verificado).

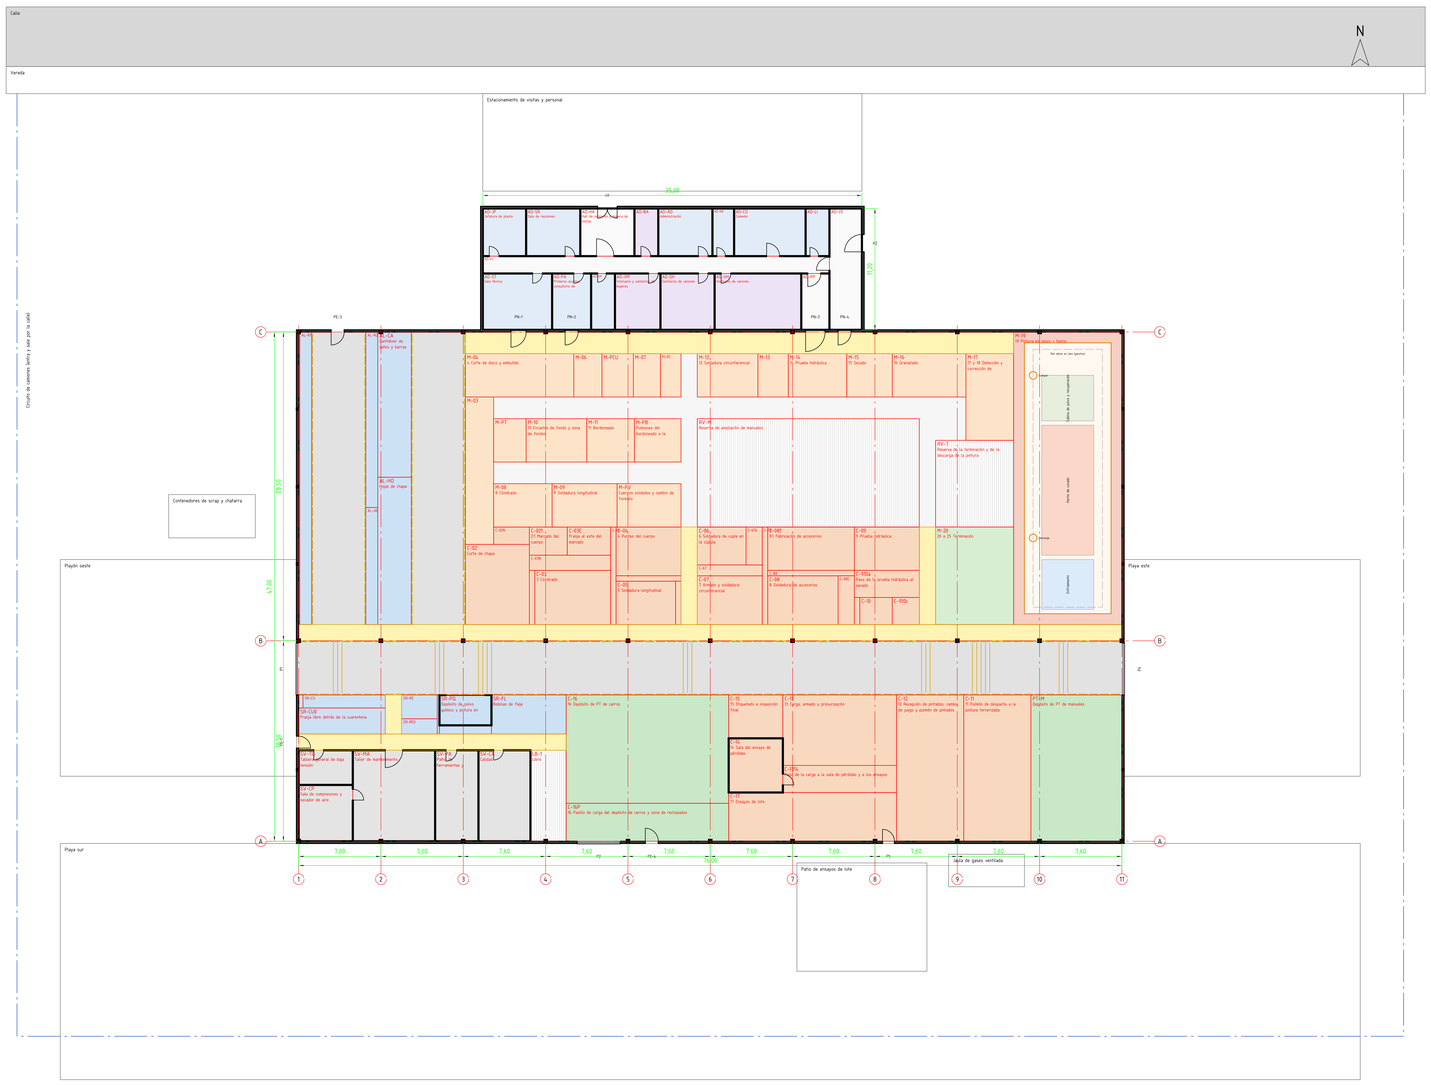

Zonas de la nave y del anexo (m² del plano y m² que pide la fuente)

Código	Zona	m²	Fuente
AL-R1	Rack selectivo R1, 4 niveles	29,7	–
AL-W	Franja del muro oeste	2,7	–
AL-R2	Rack selectivo R2, 4 niveles	17,8	–
AL-AB	Carros de abastecimiento, identificación y retenidos de MP	11,9	–
AL-HO	Hojas de chapa	42,2	26,5
AL-CA	Cantilever de caños y barras	41,5	–
SR-CU	Cuarentena de MP	9,1	8,4
SR-CU0	Franja libre detrás de la cuarentena	19,2	–
SR-CU1	Franja del muro oeste junto a la cuarentena	0,5	–
SR-RE	Recepción	7,3	6,8
SR-RE0	Franja detrás de la recepción	4,6	–
SR-PQ	Depósito de polvo químico y pintura en polvo	13,4	12,6
SR-PQ0	Franjas junto al depósito de polvo	0,7	–
SR-PQ1	Franja al sur del depósito de polvo	3,8	–
SR-FL	Bobinas de flejje	24,8	25,2
M-04	4 Corte de disco y embutido	40,0	26,0
M-06	6 Numerado de cúpula	10,4	2,3
M-PCU	Zona de cúpulas	11,6	–
M-07	7 Soldadura del cuello a la cúpula	10,0	5,3
M-05	5 Preparación de cuello	7,6	4,5
M-03	3 Corte de tubo 1 kg	35,4	25,5
M-PT	Tramos 1 kg	12,0	–
M-10	10 Encastre de fondo y zona de fondos	22,4	3,6
M-11	11 Bordoneado	17,6	3,6
M-PB	Pulmones del bordoneado a la soldadura circunferencial	17,2	–
M-08	8 Cilindrado	21,6	7,3
M-09	9 Soldadura longitudinal	24,0	8,4
M-PV	Cuerpos soldados y cambio de formato	23,6	–
M-12	12 Soldadura circunferencial	22,4	17,5
M-13	13 Control de espesor	11,2	2,3
M-14	14 Prueba hidráulica	21,6	14,1
M-15	15 Secado	16,8	6,0
M-16	16 Granallado	27,2	27,4
M-17	17 y 18 Detección y corrección de defectos: cuelgue en la pintura	35,2	9,2
M-19	19 Pintura en polvo + horno	270,0	270,0
M-20	20 a 25 Terminación	64,8	47,0
C-02	Corte de chapa	43,7	44,0
C-02N	Salida de desarrollos de la guillotina a manuales	5,3	–
C-021	2.1 Marcado del cuerpo	9,1	9,0
C-03	3 Cilindrado	35,0	35,0
C-03N	Paso de la mesa móvil del marcado al cilindrado	10,5	–
C-03W	Franja entre el corte y el cilindrado	2,5	–
C-03E	Franja al este del marcado	10,4	–
C-05	5 Soldadura longitudinal	22,0	22,0
C-04	4 Punteo del cuerpo	27,0	27,0
C-45	Separaciones del bloque 4/5	4,5	–
C-45D	Separación entre 4 y 5	3,0	–
C-45c	Franja al este de la soldadura longitudinal	2,0	–
C-07	7 Armado y soldadura circunferencial	27,0	27,0

Código	Zona	m²	Fuente
C-06	6 Soldadura de cupla en la cúpula	15,8	16,0
C-67	Pulmón de cúpulas con cupla	6,0	–
C-67b	Franja al este de la cupla	5,2	–
C-08	8 Soldadura de accesorios	29,2	29,0
C-081	8.1 Fabricación de accesorios	32,0	32,0
C-T8	Separaciones entre 7 y 8	4,5	–
C-88	Separación entre 8 y 8.1	4,0	–
C-08E	Franja al este de la soldadura de accesorios	6,8	–
C-10	10 Secado	7,5	7,5
C-09	9 Prueba hidráulica	24,0	22,0
C-910a	Paso de la prueba hidráulica al secado	15,0	–
C-910b	Franja junto al secado	1,2	–
C-910c	Salida del secado hacia el pulmón de despacho	6,2	–
C-17	17 Ensayos de lote	69,8	70,0
C-14	14 Sala del ensayo de pérdidas	25,0	25,0
C-15	15 Etiquetado e inspección final	20,0	9,0
C-13	13 Carga, armado y presurización	68,2	60,0
C-131L	Paso de la carga a la sala de pérdidas y a los ensayos	26,2	–
C-12	12 Recepción de pintados, cambio de juego y pulmón de pintados	83,7	79,0
C-11	11 Pulmón de despacho a la pintura herrerizada	83,7	70,0
C-16	16 Depósito de PT de carros	150,0	150,0
C-16P	16 Pasillo de carga del depósito de carros y zona de rechazados	52,5	50,0
PT-M	Depósito de PT de manuales	113,4	84,0
SV-CP	Sala de compresores y secador de aire	26,0	–
SV-TG	Tablero general de baja tensión	16,0	–
SV-MA	Taller de mantenimiento	63,8	–
SV-PA	Pañol de herramientas y repuestos	33,6	–
SV-CA	Calidad	40,3	–
LB-1	Libre	27,7	–
RV-M	Reserva de ampliación de manuales	295,0	–
RV-T	Reserva de la terminación y de la descarga de la pintura	57,6	–
AD-ST	Sala técnica	33,3	–
AD-PA	Primeros auxilios; consultorio de medicina laboral y de higiene y seguridad	18,7	–
AD-EP	Pañol de EPP	11,4	–
AD-VM	Vestuario y sanitarios de mujeres	21,8	–
AD-SH	Sanitarios de varones	26,0	–
AD-VH	Vestuario de varones	45,6	–
AD-PP	Paso de personal a la planta	13,5	–
AD-VE	Vestíbulo de ingreso del personal	33,6	–
AD-PE	Pasillo de la administración	51,2	–
AD-JP	Jefatura de planta	17,6	–
AD-SR	Sala de reuniones	22,0	–
AD-HA	Hall de recepción y espera de visitas	22,0	–
AD-BA	Baño accesible	9,7	–
AD-AD	Administración	22,0	–
AD-AR	Archivo	8,8	–
AD-CO	Comedor	29,0	–
AD-LI	Limpieza y hermotanque	9,7	–

Superficies por destino

Destino	m²	% de la nave
Almacén de MP y recepción	229,3	6,4
Manuales 1 a 10 kg	387,8	10,9
Pintura	270,0	7,6
Terminación de manuales	64,8	1,8
Carros 25 a 100 kg	736,1	20,6
Depósitos de producto terminado	315,9	8,8
Servicios técnicos (mantenimiento, calidad, aire, energía)	171,8	5,0
Libre / reserva	290,3	8,1
Pasillos y sendas	1.098,0	30,7
TOTAL NAVE (76,0 × 47,0 m)	3.572,0	100,0
Anexo de administración y servicios (35,0 × 11,2 m)	392,0	–

Referencias

- Almacén de MP y recepción
- Manuales 1 a 10 kg
- Pintura
- Terminación de manuales
- Carros 25 a 100 kg
- Depósitos de producto terminado
- Servicios técnicos (mantenimiento, calidad, aire, energía)
- Oficinas
- Vestuarios y sanitarios
- Libre / reserva
- Carril del autoelevador (5,0 m)
- Senda peatonal demarcada
- Pasillo de operarios y carros a mano

Criterios

Nave de 76,0 × 47,0 m, 10 vanos de 7,6 m, pórticos de 18,5 + 28,5 m con la fila de columnas en el borde norte del carril del autoelevador (ninguna columna dentro de un carril). Pasillo principal: carril de 5,0 m (Heli CPC050, W-CAR) + senda de 1,5 m con baranda y cruces. Almacén con dos pasillos de 5,0 m (AL-A junto a las máquinas de corte, AL-B entre racks). Puertas: P1 MP (oeste), P4 despacho de PT de manuales y camión de pintura de carros (este, al final del pasillo principal: W-CAR 11 «más» el de la planta»), P2 despacho de carros (sur), P5 paño de ensayos; salidas de emergencia PE y puertas PN entre la administración y la planta. Reservas (RV y LB): lugar para la máquina siguiente de los puestos de manuales al 92-97 % en 2035 (X-MAN) y el espacio libre del croquis. El largo de la nave lo fijan la fila de carros más la terminación y la pintura (norte) y los puestos 11 a 17 de carros más el PT (sur).

	Fecha	Nombre
Dibujó	15/10/26	Claude Code
Revisó		
Aprobó		

Escala	1:200
Método de proyección	ISO E
Unidades	Cotas en m
Formato	A0

Propietario	FLAMA S.A.
Denominación	Planta general e implantación
	Layout 2035 v10 – zonas codificadas y áreas
Tipo de documento	Plano de planta
Reemplaza a / Reemplazado por	–
Material	–
Edición	0
Fecha de edición	15/10/2026
Hoja	1 / 5
Idioma	es
N.º de plano	FL_PI10_01