# FL_PI10_02 - PUESTOS Y EQUIPOS (MANUALES, CARROS, PINTURA, TERMINACIÓN Y ALMACENES)

Máquina de cada puesto según X-MAN y W-CAR; medida de la tabla de áreas v10 (cotización > ET > Word > criterio). Operario dibujado al frente con 0,95 m libres (verificado).

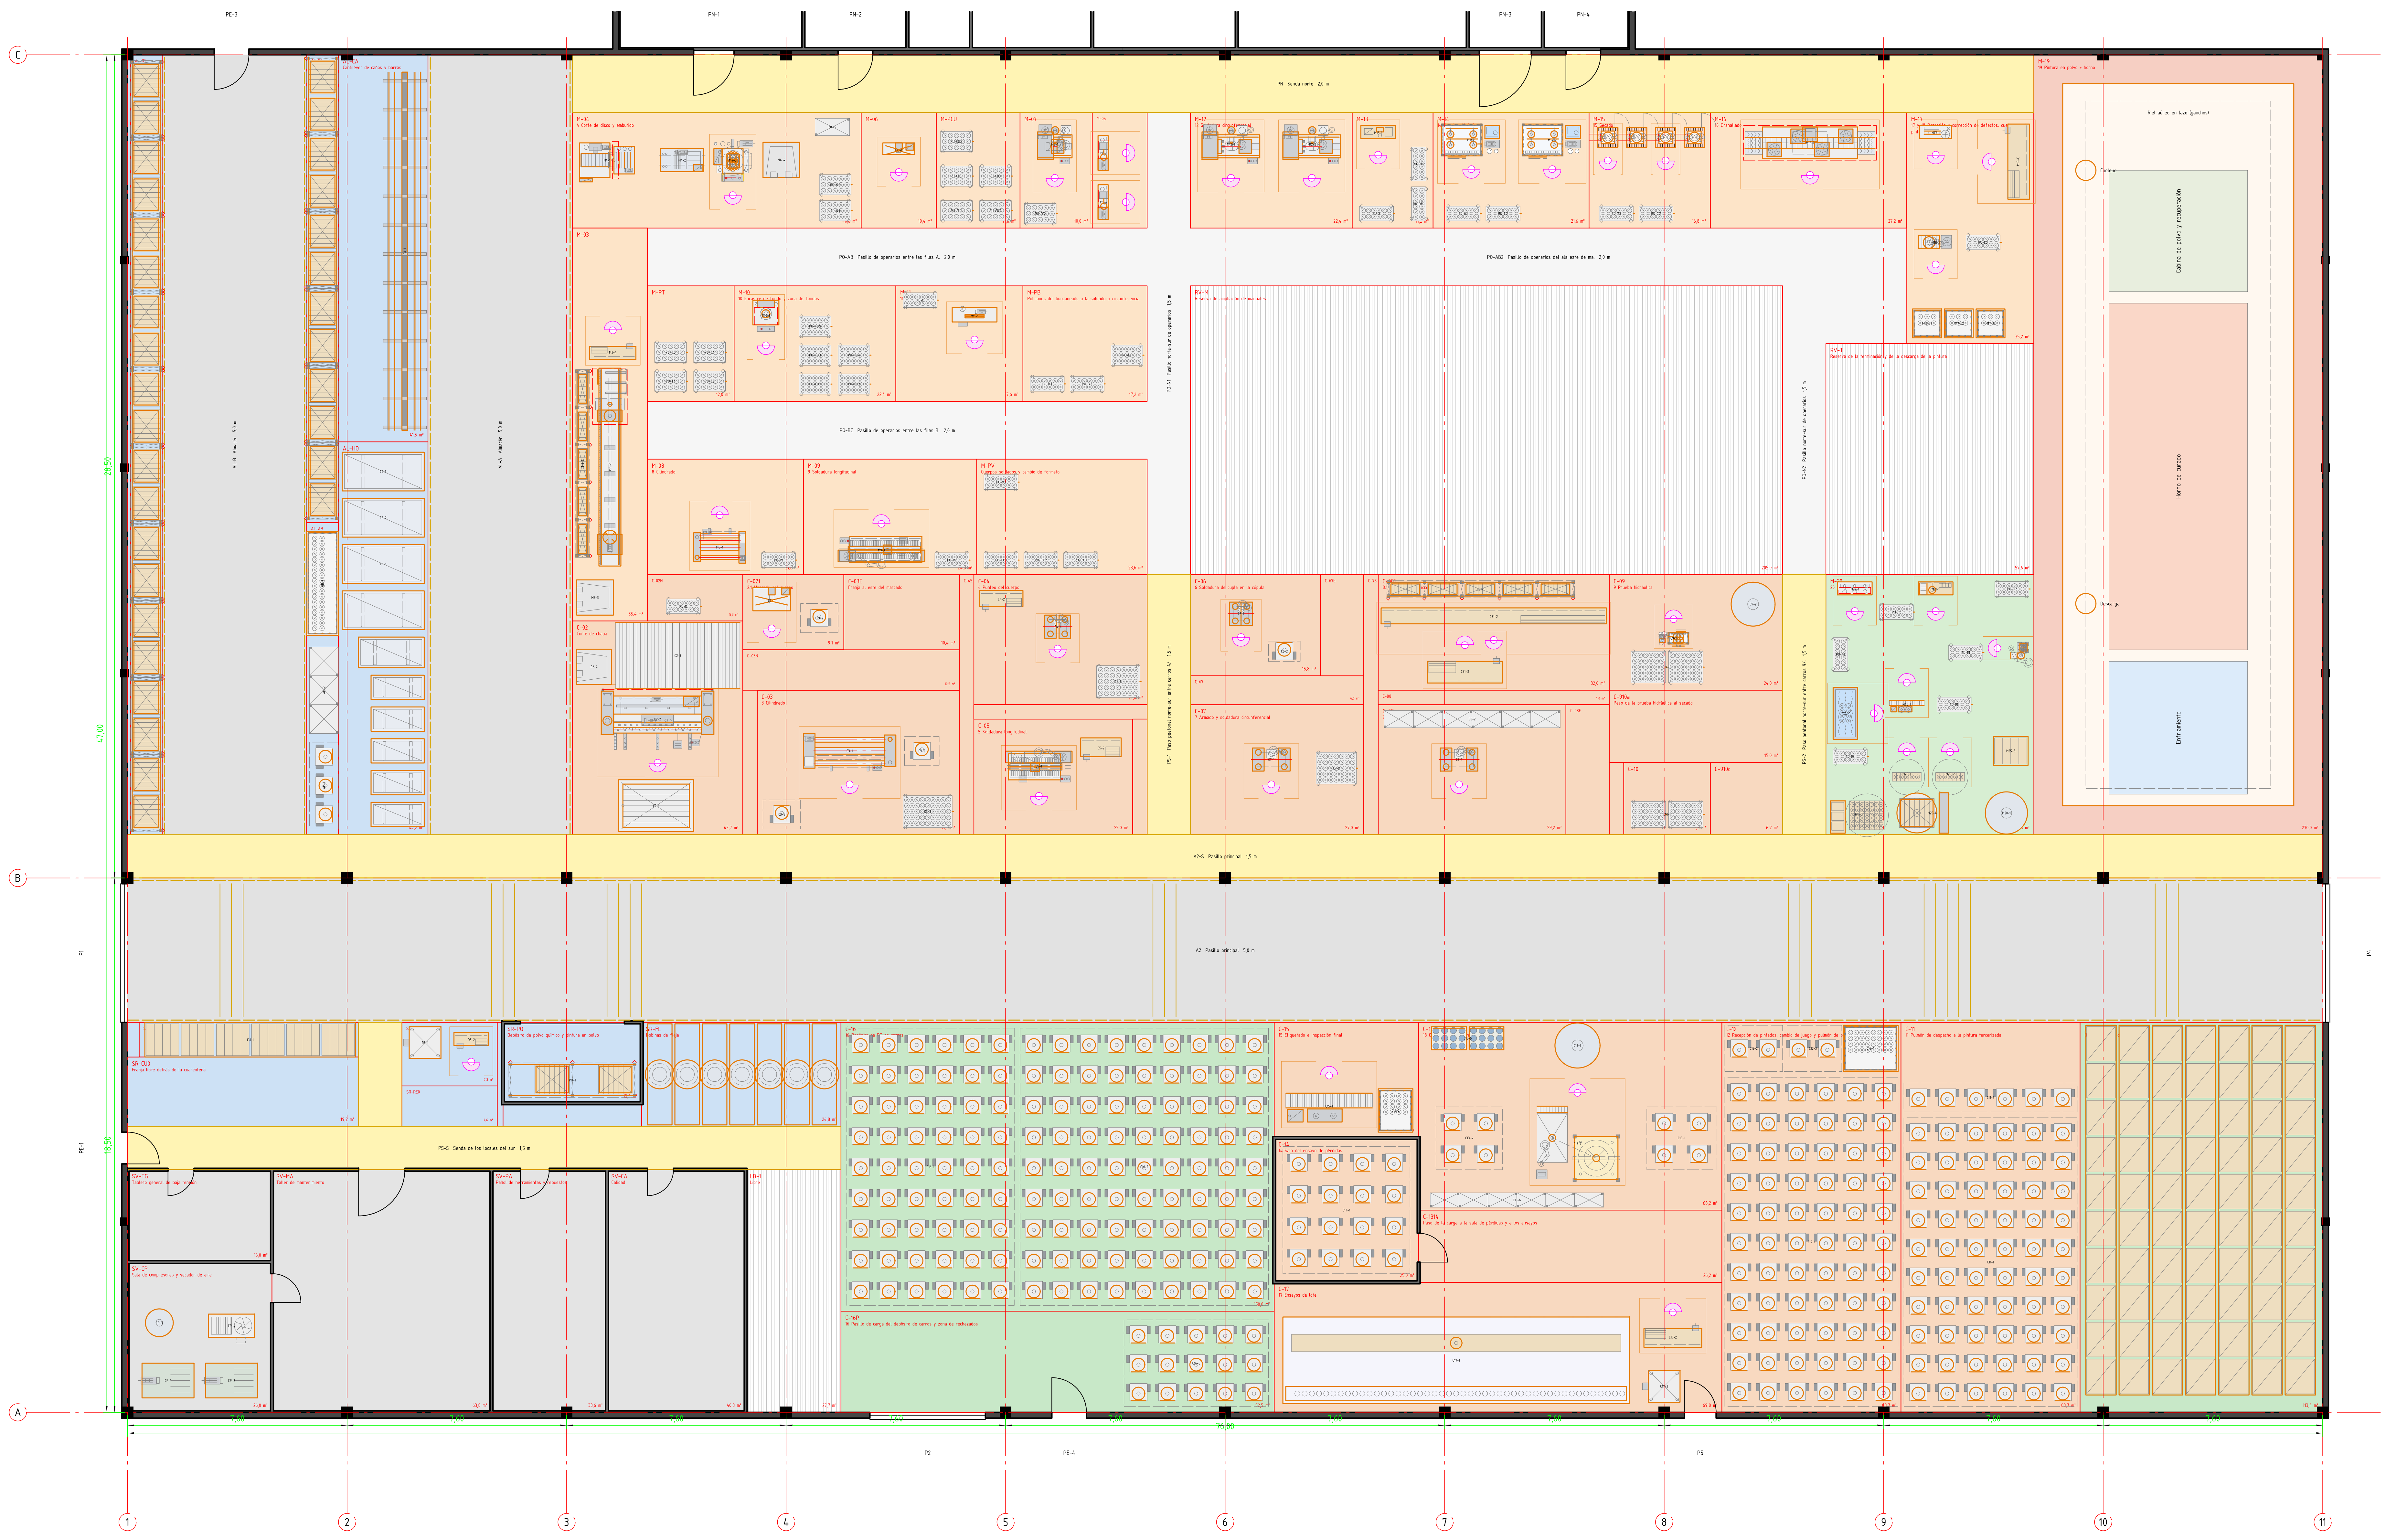
C-05
5 Soldadura longitudinal
22,0 m²
C-07
7 Armado y soldadura circunferencial
27,0 m²
29,2 m²
PS-1 Paso peatonal norte-sur
A2-S Pasillo principal 1,5 m
A2 Pasillo principal 5,0 m
C-15
15 Etiquetado e inspección final

## Equipos principales y su medida en planta

| Cód. | Zona | Equipo | Planta (m) | Fuente de la medida |
|---|---|---|---|---|
| M4-1 | M-04 | Desbobinador con carro portabobinas | 2,00 × 1,50 | Tabla de áreas v10 |
| M4-2 | M-04 | Enderezador y alimentador servo Cena PRE-1 | 1,60 × 1,00 | Tabla de áreas v10 |
| M4-3 | M-04 | Prensa embutidora Sangiacomo T 63R CE | 1,31 × 1,50 | ET |
| M3-2 | M-03 | Láser de tubo Leapion 6012 1,5 kW | 0,80 × 6,85 | Cotización Leapion |
| M5-1 | M-05 | Prensa Pannier MarkFirst MB-21 sobre banco | 0,60 × 1,20 | ET |
| M6-1 | M-06 | Micropercusión Pannier ADP120160D sobre banco | 1,20 × 0,60 | Mesa 1,2 × 0,6 |
| M7-1 | M-07 | Soldadora de cuello Firesafer FS-HFM1 | 1,20 × 1,40 | Catálogo Firesafer FS Cylinder Producti. |
| M8-1 | M-08 | Roladora Firesafer FS-RM01 | 1,80 × 1,30 | Catálogo Firesafer FS Cylinder Producti. |
| M9-1 | M-09 | Soldadora longitudinal Firesafer | 3,00 × 0,90 | ET Getweld ZF-500 |
| M10-1 | M-10 | Prensa hidráulica Del Fabro 30 t | 1,00 × 1,15 | ET |
| M11-1 | M-11 | Bordoneadora motorizada Pilman SWM-400 | 1,65 × 0,70 | Presupuesto Pilman 1310727 |
| M12-1 | M-12 | Soldadora circunferencial Firesafer FS-SWH | 2,00 × 1,40 | Tabla de áreas v10 |
| M13-1 | M-13 | Medidor de espesor Melisam MR017 sobre mesa | 1,20 × 0,60 | Mesa 1,2 × 0,6 |
| M14-1 | M-14 | Banco de prueba hidráulica Firesafer FS-JD12A | 2,05 × 1,10 | Catálogo Firesafer, pág. 11 |
| M15-1 | M-15 | Secadora de cilindros Yukon | 0,70 × 0,68 | ET |
| M16-1 | M-16 | Granalladora de rodillos Airblast G-100 | 4,50 × 1,30 | Cotización Airblast |
| M17-1 | M-17 | Mesa de inspección iluminada | 1,20 × 0,60 | W-MAN 16 |
| M18-1 | M-17 | Mesa de corrección con amoladora y extracción | 1,20 × 0,60 | W-MAN 17 |
| M19-1 | M-19 | Línea de recubrimiento en polvo Firesafer | 8,00 × 25,00 | ET |
| M20-1 | M-20 | Estación de big bag ABC 60 | 1,50 × 1,50 | Tabla de áreas v10 |
| M20-2 | M-20 | Cargadora por vacío Yukon M-000121 | 0,62 × 0,51 | Ficha Yukon |
| M21-1 | M-20 | Mesa de ensamblaje con llave dinamométrica | 1,20 × 0,60 | Mesa 1,2 × 0,6 |
| M22-1 | M-20 | Pinza Yukon M-000150 sobre mesa | 1,20 × 0,60 | Mesa 1,2 × 0,6 |
| M23-1 | M-20 | Tanque de inmersión inoxidable Firesafer FS-SS100 | 1,00 × 1,80 | Catálogo Filling Line, pág. 44 |
| M24-1 | M-20 | Dispensador de etiquetas y Zebra ZD421 sobre mesa | 1,20 × 0,60 | Mesa 1,2 × 0,6 |
| M25-3 | M-20 | Armadora automática de cajas | 2,02 × 1,42 | Sin cotizar; referencia FS-DDP50 |
| M25-4 | M-20 | Envolvedora EDOS PS5 | 2,55 × 1,50 | Plano de cotas EDOS 26880 |
| C2-1 | C-02 | Mesa elevadora de tijera SJG3.0-1.6 | 2,60 × 1,80 | W-CAR 2 |
| C2-2 | C-02 | Guillotina hidráulica CENA 8 × 3200 | 3,90 × 2,10 | W-CAR 2 |
| C21-1 | C-021 | Mesa de marcado con marcadora DTMAQ MPE 150130 | 1,40 × 1,00 | W-CAR 2.1 |
| C3-1 | C-03 | Roladora CNC 4 rodillos W12 8 × 1500 | 3,20 × 1,40 | W-CAR 3 |
| C4-1 | C-04 | Virador sobre base fija | 1,20 × 0,60 | W-CAR 4 |
| C5-1 | C-05 | Soldadora longitudinal ZH-1300 Dragon Welding | 2,30 × 1,14 | W-CAR 5 |
| C6-1 | C-06 | Posicionador de cupla | 1,10 × 0,70 | W-CAR 6 |
| C7-1 | C-07 | Virador 1.000 kg con torcha fija | 1,60 × 0,80 | W-CAR 7 |
| C8-1 | C-08 | Virador | 1,60 × 0,80 | W-CAR 8 |
| C81-2 | C-081 | Caballetes y sensitiva 8,8 × 0,8 | 7,80 × 0,70 | W-CAR 8.1 |
| C9-1 | C-09 | Banco de prueba hidráulica Yukon M-000200 | 1,05 × 0,40 | W-CAR 9 |
| C13-2 | C-13 | Estación B | 3,00 × 2,60 | W-CAR 13 |
| C13-3 | C-13 | Bastidor del big bag con tolva | 1,60 × 1,60 | W-CAR 13 |
| C17-1 | C-17 | Recinto de descarga cerrado | 12,00 × 3,00 | W-CAR 17 |
| RE-1 | SR-RE | Balanza de plataforma 1,20 × 1,20 m, 1.500 kg | 1,20 × 1,20 | W-MAN 1 / W-CAR 1 |
| CA-1 | AL-CA | Cantiléver simple, 5 niveles, brazos de 1,2 m | 1,60 × 12,40 | X-ALM |
| PQ-1 | SR-PQ | Rack pesado de big bags | 4,40 × 1,20 | X-ALM |

## Pulmones (sólo los de W-MAN y W-CAR)

Carro FCHP20505 (1280 × 610 mm, W-MAN 6) o carro de 12 cajones (1200 × 800 mm, W-MAN 2), en violeta. PU-K, PU-CU, PU-FO cúpulas y fondos (W-MAN 3); PU-T tramos de 1 kg (W-MAN 2); PU-D, PU-V1 a V3 y PU-FX cuerpos (W-MAN 6 y 7); PU-CC2 y PU-CC cúpulas con cuello (W-MAN 8); PU-E, PU-B (W-MAN 9 y 10); PU-S y PU-RT (W-MAN 12); PU-6 y PU-7 (W-MAN 13 y 14); PU-CO (W-MAN 16); PU-TP y PU-F1 a F5 (W-MAN 18 a 24).

## Notas

Corte de chapa común (C-02): la mesa elevadora mira al pasillo principal; la zona trasera entrega los desarrollos de manuales hacia el norte (C-02N) y los cuerpos de carros al marcado (2.1, pegado a la rampa).
Corte de tubo norte-sur: el cajón del atado mira al pasillo AL-A, frente al cantiléver (atado con la pluma).
Desbobinador contra AL-A (bobina con el espolón). Contenedores de scrap del corte y del láser contra AL-A.
Granalladora Airblast G-100: los rodillos de entrada y salida están dentro de los 4,5 m (cotización).
Pintura: cuelgue al norte desde la detección y descarga al sur hacia la terminación (riel en lazo).
Carros 11 y 12 sobre el pasillo principal: el camión de la pintura carga y descarga por P4 (W-CAR 11).
Sin medida en ningún presupuesto (criterio, marcado): desbobinador, alimentador Cena PRE-1, soldadora circunferencial FS-SWH, jaulas, estación de big bag; armadora de cajas sin cotizar (referencia FS-DDP50).

| | Fecha | Nombre |
|---|---|---|
| Dibujó | 15/10/26 | Claude Code |
| Revisó | | |
| Aprobó | | |

Escala: 1:100
Método de proyección: ISO E
Unidades: Cotas en m
Formato: A0
Propietario: FLAMA S.A.
Denominación: Puestos y equipos
Layout 2035 v10 – máquinas de X-MAN y X-CAR con su medida
Tipo de documento: Plano de planta
Reemplaza a / Reemplazado por: -
Material: -
Edición: 0
Fecha de emisión: 15/10/2026
Hoja: 2 / 5
Idioma: es
N° de plano: FL_PI10_02