FL_PI10_03 - CIRCULACIÓN, FLUJOS DE MATERIALES Y RECORRIDOS DEL PERSONAL

Carriles del autoelevador, sendas peatonales y pasillos de operarios con su ancho; flujo de MP, de semielaborado y de PT; hilos del personal desde los vestuarios.

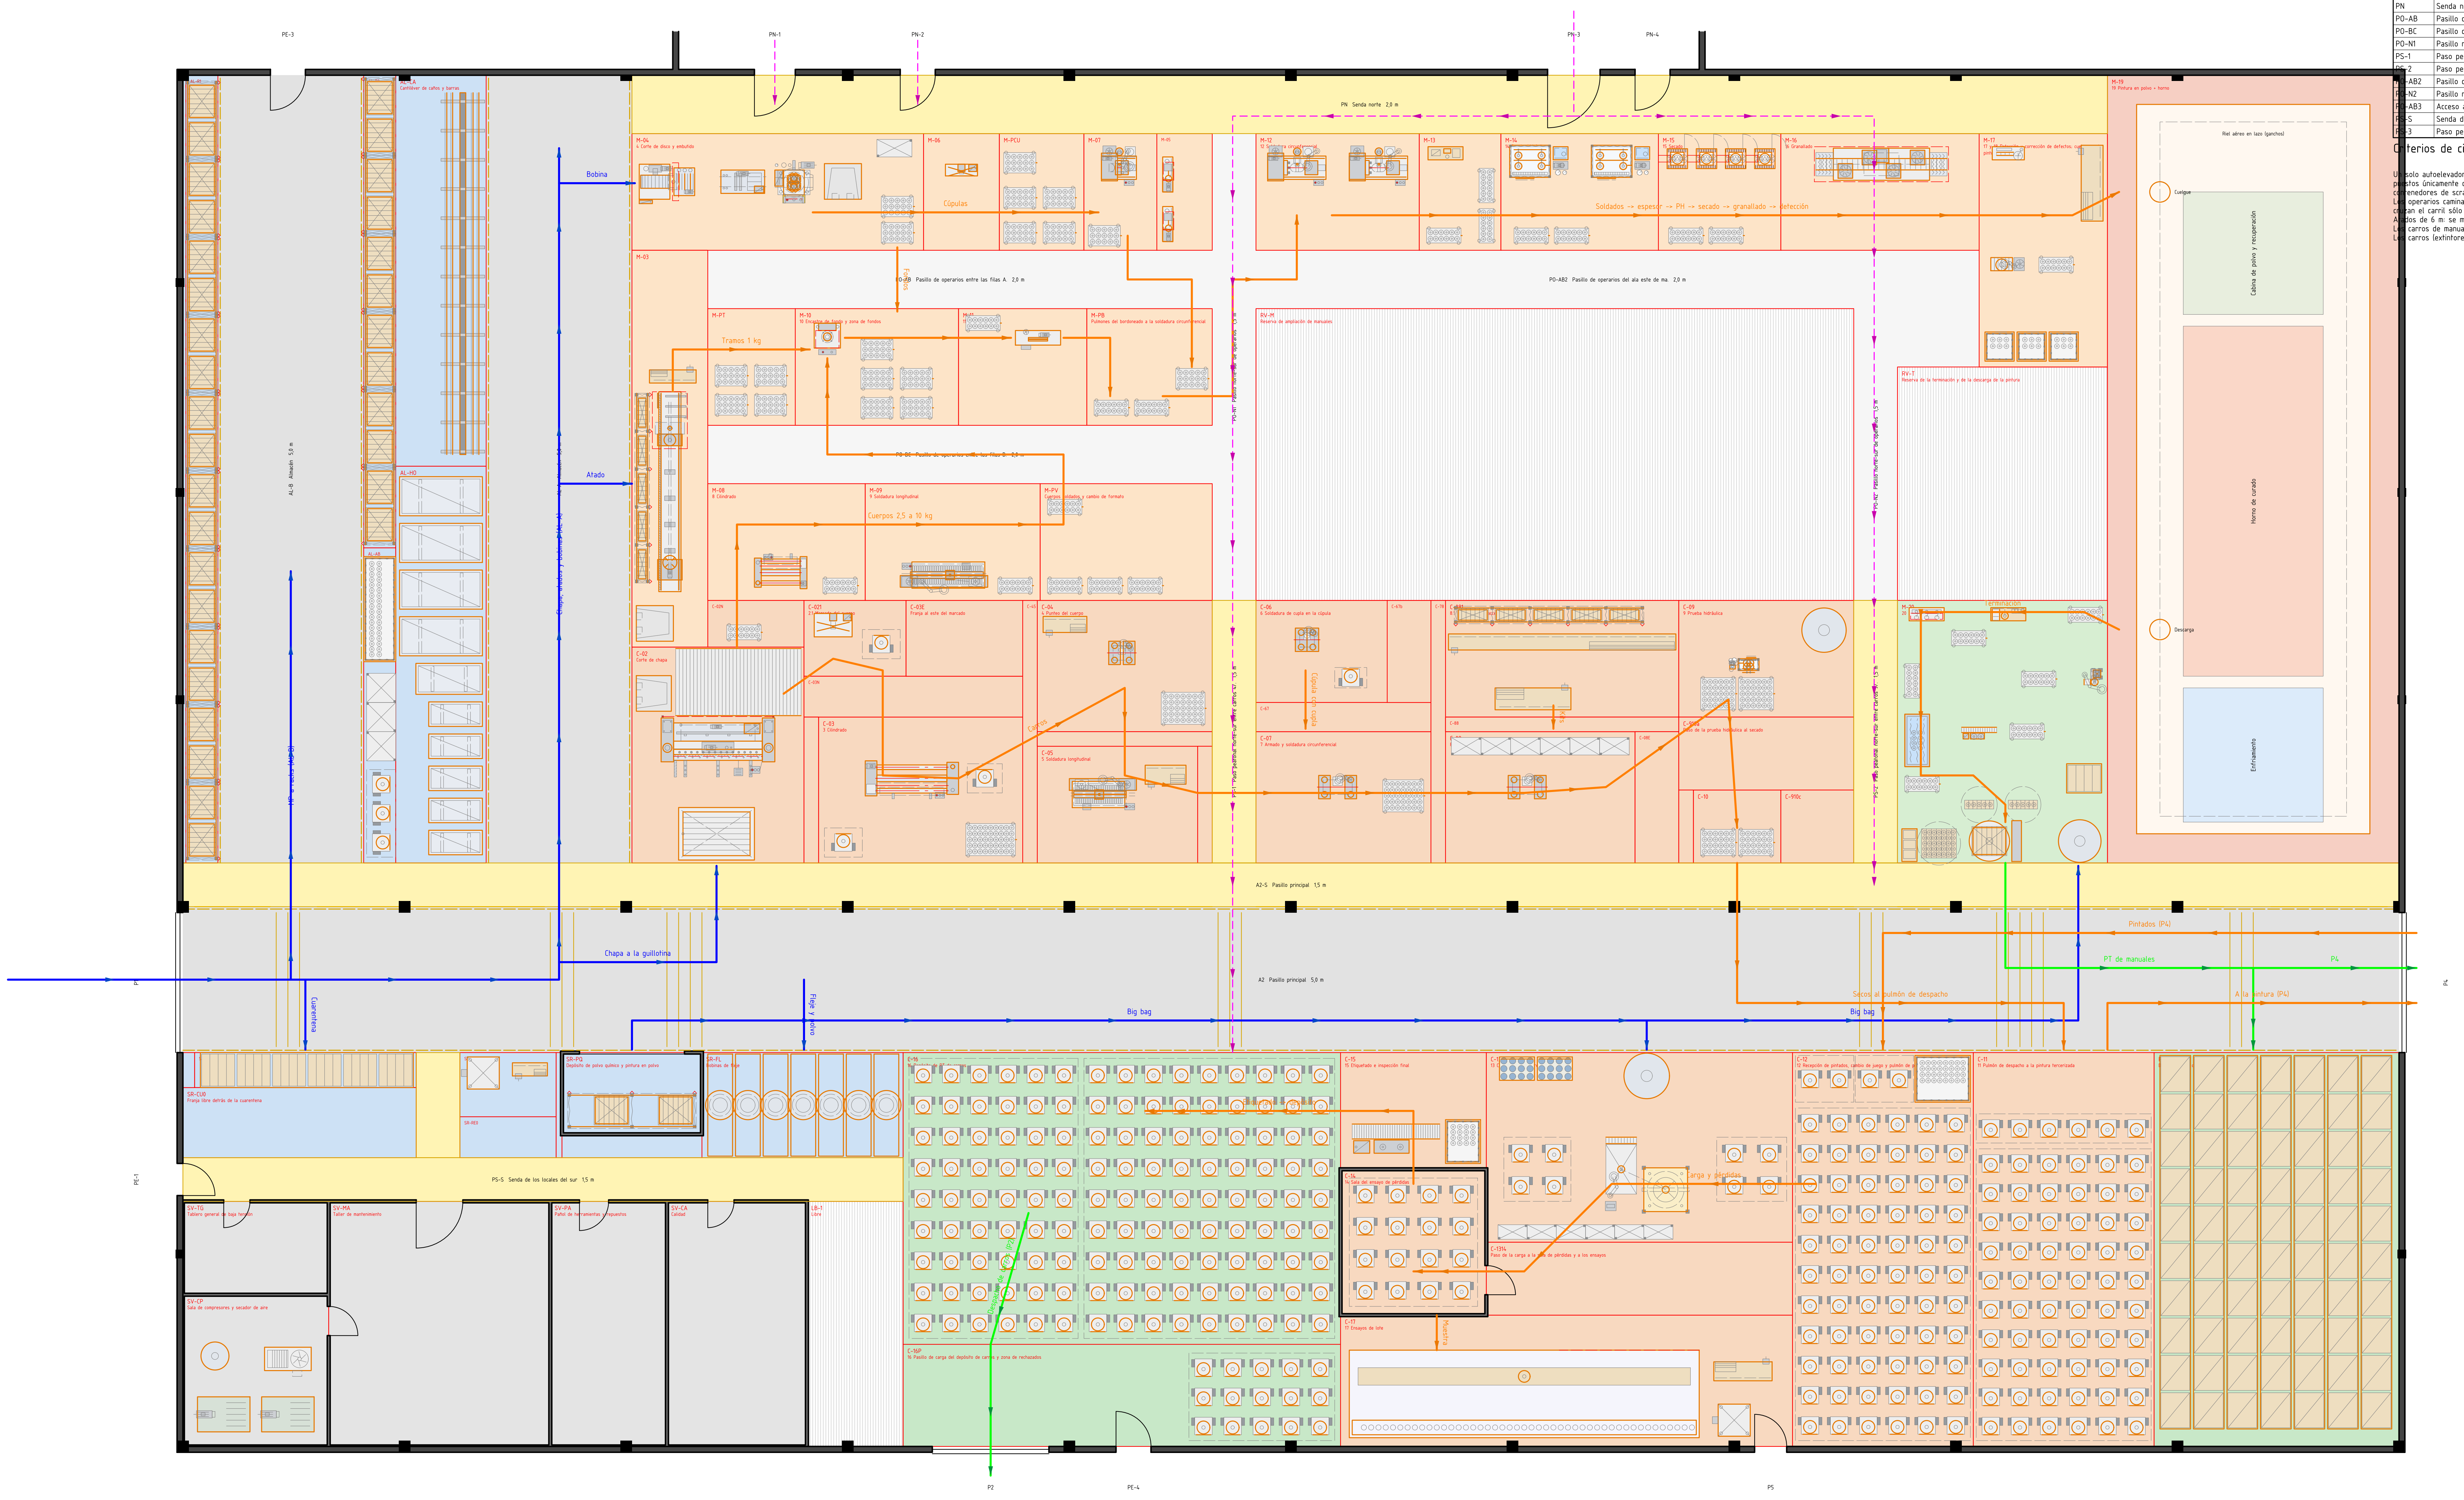
PE-3
PN-1
PN-2
PN-3
PN-4
PN Senda norte 2,0 m
AL-CA Cantiléver de caños y barras
Bobina
M-04 4 Corte de disco y embutido
M-06
M-PCU
M-07
M-05
Cúpulas
M-12
M-13
M-14
M-15 15 Secado
Soldados -> espesor -> PH -> secado -> granallado
Añado
Chapa a la guillotina
Cuarentena
Fleje y polvo
Big bag
A2-S Pasillo principal 1,5 m
A2 Pasillo principal 5,0 m
C-05 5 Soldadura longitudinal
C-10
C-910c
SR-CUO Franja libre detrás de la cuarentena
SR-REO
SR-PQ Depósito de polvo químico y pintura en polvo
SR-FL Bobinas de fleje
C-16
C-15 15 Etiquetado e inspección final
C-12 12 Recepción de pintados, cambio de juego y pulmón de
C-11 11 Pulmón de despacho a la pintura tercerizada
Pintados (P4)
PT de manuales
P4
Secos al pulmón de despacho
A la pintura (P4)
Carga y pérdidas
Etiquetado → depósito
Enfriamiento

Referencias

- ▨ Carril del autoelevador (5,0 m)
- 🟨 Senda peatonal demarcada
- ☐ Pasillo de operarios y carros a mano

Flujos

- → MP: materia prima (azul)
- → SE: semielaborado (naranja)
- → PT: producto terminado (verde)
- - - → Hilos de personal (magenta)

Pasillos (m)

Cód.	Pasillo	Ancho	Largo	Uso
A2	Pasillo principal	5,0	76,0	Autoelevador
A2-S	Pasillo principal	1,5	76,0	Peatonal
AL-A	Almacén	5,0	27,0	Autoelevador
AL-B	Almacén	5,0	27,0	Autoelevador
PN	Senda norte	2,0	50,6	Peatonal
PO-AB	Pasillo de operarios entre las filas A y B de manua.	2,0	17,3	Operarios
PO-BC	Pasillo de operarios entre las filas B y C de manua.	2,0	17,3	Operarios
PO-N1	Pasillo norte-sur de operarios	1,5	16,0	Operarios
PS-1	Paso peatonal norte-sur entre carros 4/5 y 6/7	1,5	9,0	Peatonal
PS-2	Paso peatonal norte-sur entre carros 9/10 y la term.	1,5	9,0	Peatonal
PO-AB2	Pasillo de operarios del ala este de manuales	2,0	24,8	Operarios
PO-N2	Pasillo norte-sur de operarios	1,5	10,0	Operarios
PO-AB3	Acceso a la detección y a la corrección	2,0	2,8	Operarios
PS-S	Senda de los locales del sur	1,5	24,7	Peatonal
PS-3	Paso peatonal de la senda sur al pasillo principal	1,5	3,6	Peatonal

Criterios de circulación

Un solo autoelevador (Heli CPCD50, W-MAN y W-CAR): circula sólo por A2, AL-A y AL-B (5,0 m) y entra a los
puestos únicamente donde la máquina mira al carril: mesa elevadora, cajón del atado, desbobinador,
contenedores de scrap, big bags (terminación y carro 13), envolvedora, calles de PT y carros 11 y 12.
Los operarios caminan por las sendas (amarillas) y por los pasillos de operarios de 1,5 a 2,0 m;
cruzan el carril sólo por los cruces demarcados de la baranda.
Atados de 6 m: se mueven colgados de la pluma (W-MAN 1 y 2), a lo largo del pasillo.
Los carros de manuales (FCHP y de 12 cajones) se empujan a mano entre puestos pegados (W-MAN).
Los carros (extintores rodantes) ruedan sobre su juego provisorio desde el puesto 8 (W-CAR).

	Fecha	Nombre	Propietario	Reemplaza a / Reemplazado por
Dibujó	15/10/26	Claude Code	FLAMA S.A.	-
Revisó			Denominación Circulación y flujos Layout 2035 v10 - pasillos, materiales y personas	Material -
Aprobó				Edición 0
Escala 1:100	Método de proyección ISO E			Fecha de emisión 15/10/2026
				Hoja 3 / 5
				Idioma es
Unidades Cotas en m	Formato A0		Tipo de documento Plano de circulación	N° de plano FL_PI10_03