FL_PI_01 - PLANO GENERAL FORMAL NORMALIZADO: PLANTA ACOTADA 1:100

Nave 88 × 44 m (sin recargas), servicios al personal, oficinas y sala técnica, con cada máquina, puesto, pulmón, mueble y artefacto a escala. Cotas en metros. Ejes 1 a 12 cada 8,00 m y A-B-C.

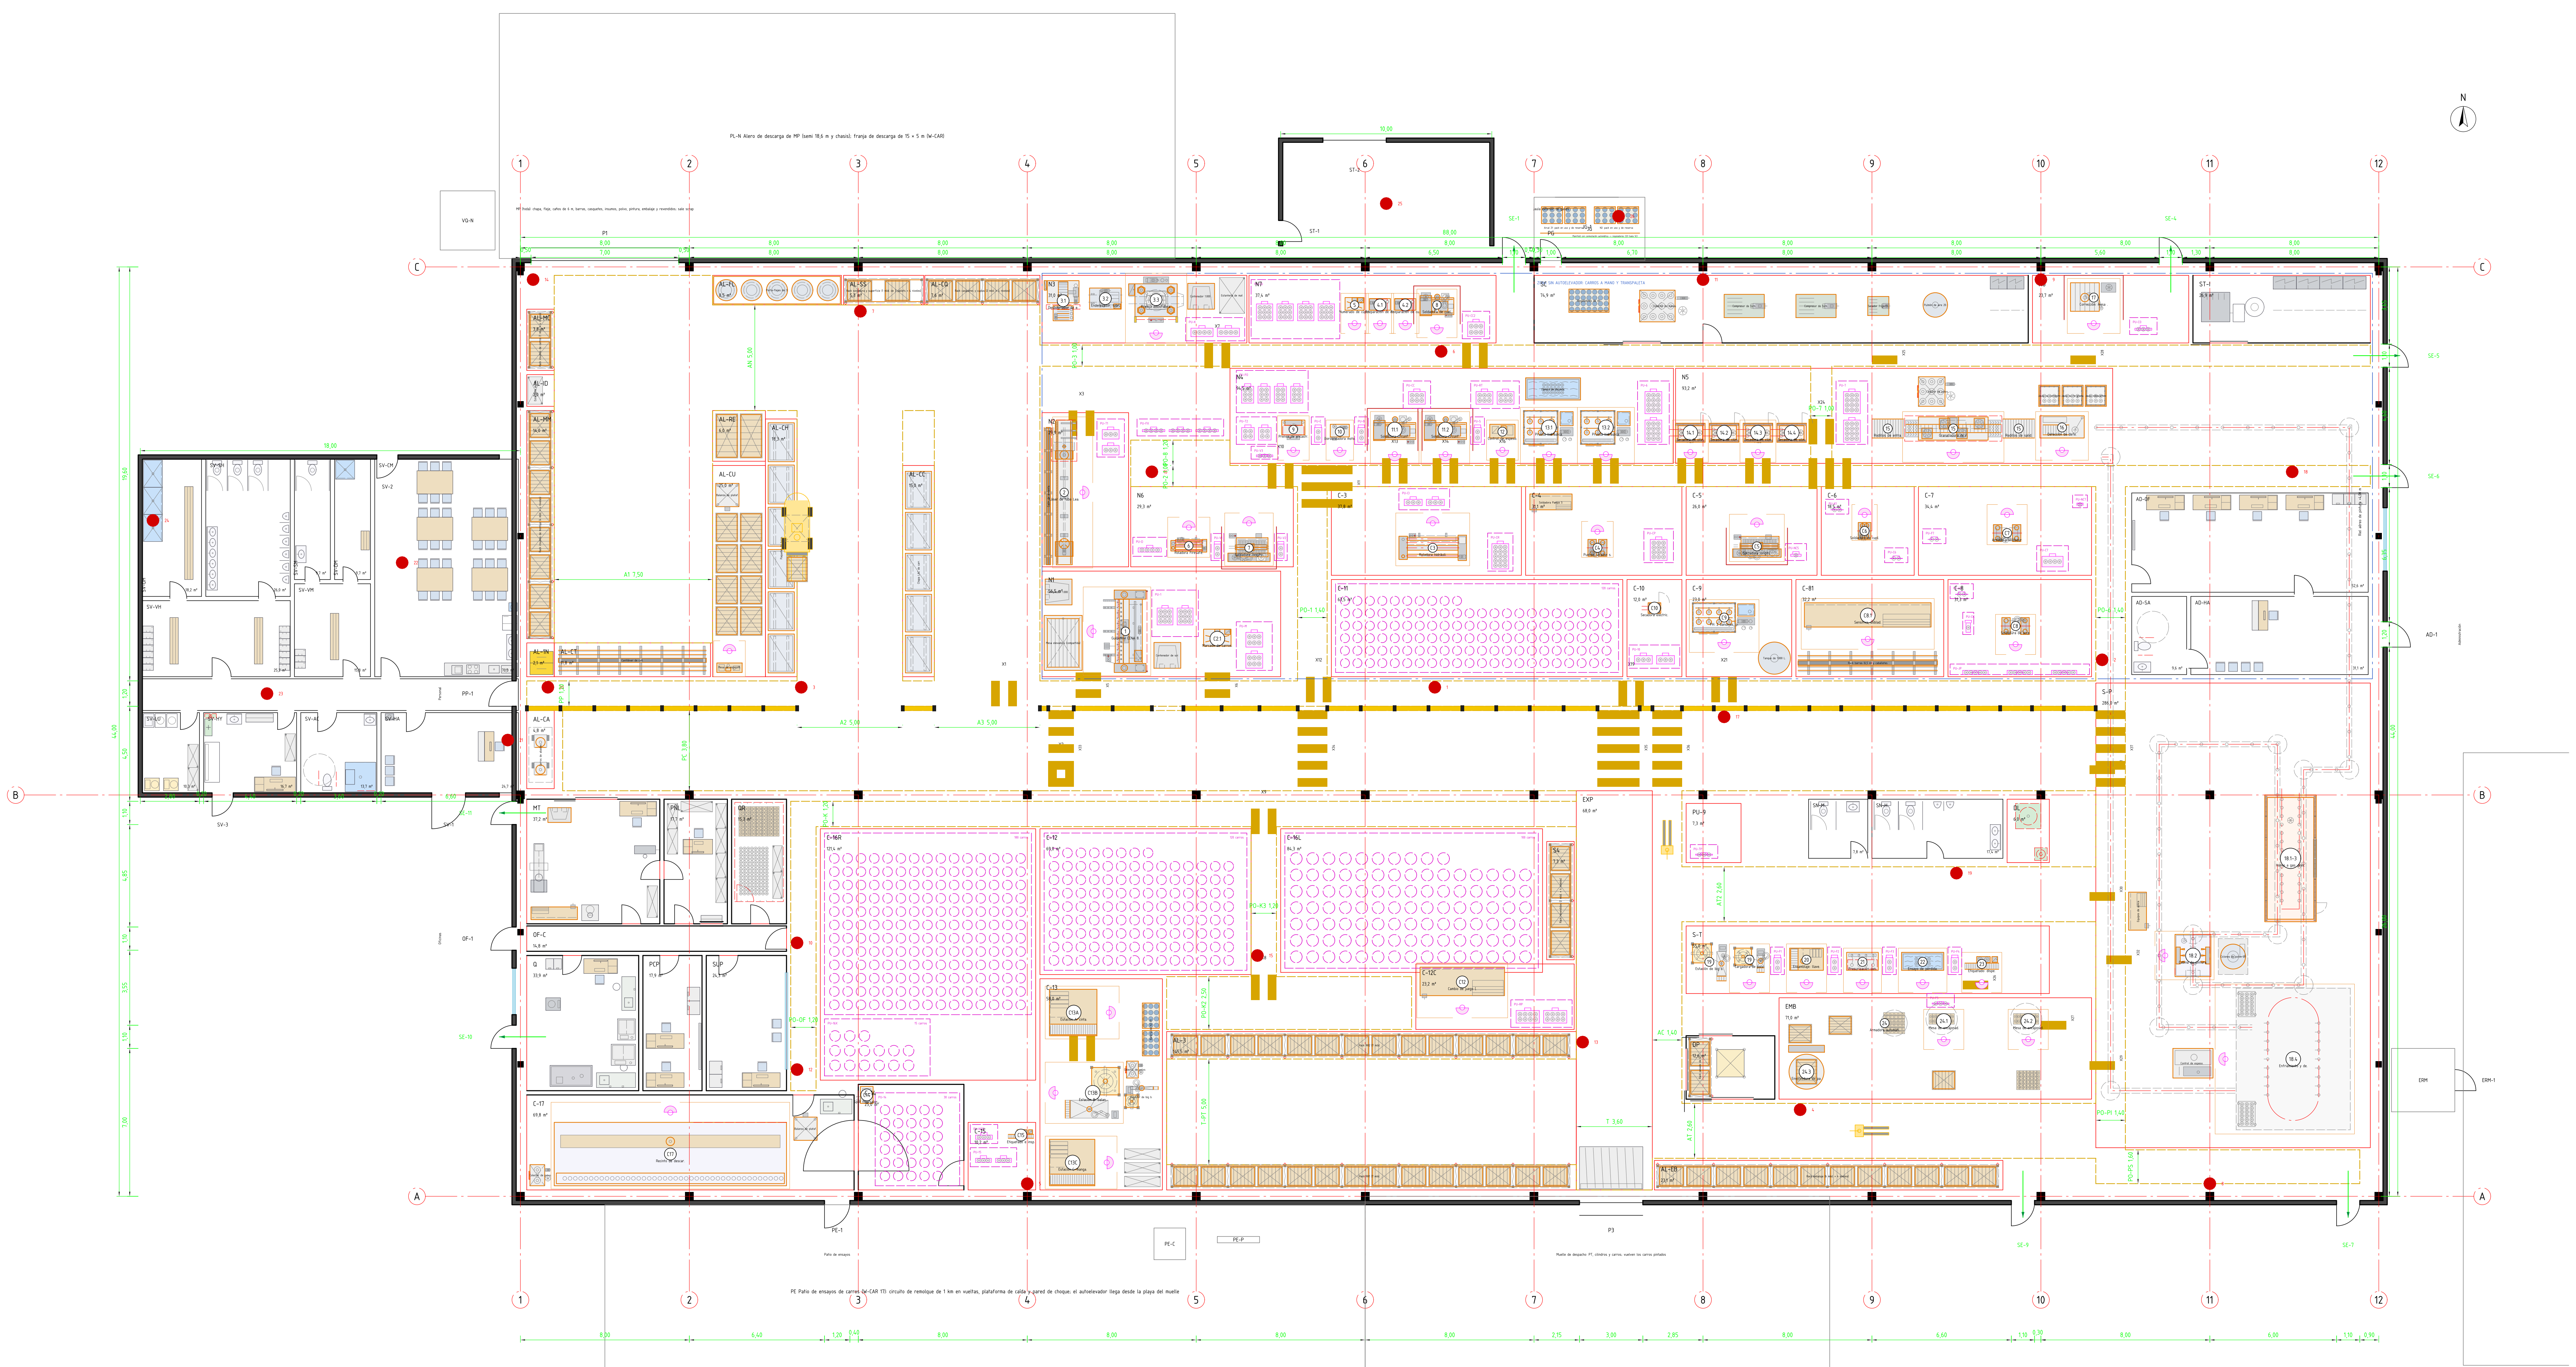
PL-N Alero de descarga de MP (semi 18,6 m y chasis); franja de descarga de 15 × 5 m (W-CAR)
MP (toda): chapa, fleje, caños de 6 m, barras, casquetes, insumos, polvo, pintura, embalaje y revendidos; sale scrap
VQ-N
P1
ST-1
ST-2
SE-1
PG
SC
74,9 m²
SIN AUTOELEVADOR: CARROS A MANO Y TRANSPALETA
AL-FL
AL-SS
AL-CQ
AL-MC
AL-ID
N3
N4
N5
N7
88,00
8,00
10,00
1
2
3
4
5
6
7
8
9
10
11
12
A
B
C

Equipos: medida (cotización o criterio de diseño) y superficie de Guerchet (m²)

Paso	Cód.	Equipo	Medida m	Fuente de la medida	Op.	Ss	St
-	RMM	Rack de insumos de montaje (4 mód. × 4 niv	1,15 × 10,80	X-ALM: 32 posiciones de pallet 1,2 × 1,0	-	12,4	17,1
-	EID	Estantería de identificación (5 niveles)	0,70 × 1,30	X-ALM: estantería de cajas	-	0,9	1,3
-	RMC	Rack de insumos de carros (1 mód. × 4 nive	1,15 × 2,70	X-ALM: 8 posiciones	-	3,1	4,3
-	CAB	Carros de abastecimiento (2)	1,10 × 2,60	W-CAR tabla 5: 3 × 1 m	-	2,9	3,9
-	CT1	Cantiléver de caños y barras (3 niveles)	7,00 × 1,45	X-ALM: caño de 6 m + 0,4 m por extremo; brazos	-	10,1	14,0
-	MI1	Mesa de inspección de recepción (micrómetr	1,20 × 0,60	W-MAN y W-CAR: mesa 1,2 × 0,6	1	0,7	2,0
-	BP1	Balanza de plataforma 1,20 × 1,20 m, 1.500	1,20 × 1,20	W-MAN y W-CAR puesto 1: balanza de plataforma	-	1,4	2,0
-	HJ1	Paquetes de hojas LAF (5 posiciones × 2 al	1,40 × 12,00	X-ALM: 7 lugares de 1,22 × 2,44 a 1,5 × 3,0	-	16,8	23,2
-	HJ2	Chapa LAC de carros (3 posiciones)	1,40 × 9,70	W-CAR: 3 posiciones de 3,0 × 1,5 m	-	13,6	18,7
-	RF1	Porta-flejes de 3 niveles (21 cunas)	6,00 × 1,30	X-ALM 21 rollos; porta-flejes de MP Opción D	-	7,8	10,8
-	RSS	Rack de soldadura y superficie (1 mód. de	3,70 × 1,15	X-ALM: 12 posiciones	-	4,3	5,9
-	RCQ	Rack de casquetes y cuplas (2 mód. × 4 niv	5,35 × 1,15	X-ALM: 11 posiciones	-	6,2	8,5
-	M02	Mesa elevadora de tijera 3 t (compartida)	1,80 × 2,60	W-MAN y W-CAR: 2,6 × 1,8 m	-	4,7	6,5
1	M04	Guillotina CENA 8 × 3200 (compartida)	2,10 × 3,90	W-CAR: ≈ 3,9 × 2,1 m (a confirmar con Cena)	1	8,2	22,6
-	SCG	Contenedor de scrap 1.000 L con volcador	1,47 × 1,42	W-CAR: 1470 × 1420 mm detrás de la guillotina,	-	2,1	2,9
C2.1	MK1	Marcado de carros: mesa 1,4 × 1,0 y marcad	1,40 × 1,00	W-CAR 2.1: lo atiende el operario de corte	-	1,4	1,9
-	CJ1	Cajón de alimentación 0,5 × 0,5 × 6,5 m (a	0,50 × 6,50	W-MAN: el autoelevador deja el atado y se desf	-	3,2	4,5
2	M16	Láser de tubo Leapion 1,5 kW con chiller	0,80 × 6,85	Cotiz. Leapion; W-MAN: recorrido útil 6150 mm	1	5,5	15,1
-	SCL	Contenedor 1.000 L de recortes del láser	1,47 × 1,42	W-MAN: junto a la máquina, lo vacía el autoele	-	2,1	2,9
6	B02	Roladora Firesafer FS-RM01	1,70 × 0,80	W-MAN: trifásica 380 V, 4 kW (huella de catálo	1	1,4	3,8
7	B03	Soldadora longitudinal Firesafer (MAG)	2,00 × 1,40	Cotiz. Firesafer; W-MAN	1	2,8	7,7
3.1	M06	Desbobinador de eje horizontal con carro p	1,80 × 2,00	W-MAN: rollo parado, cargado con el espolón de	-	3,6	5,0
3.2	M07	Enderezador, lubricante y alimentador serv	1,60 × 1,20	Cotiz. Cena PRE-1 (Drive)	-	1,9	2,6
3.3	M08	Prensa embutidora Sangiacomo	2,60 × 2,20	W-MAN: corta el disco y embute en el mismo gol	1	5,7	15,8
-	SCP	Contenedor 1.000 L del esqueleto (sobre ru	1,47 × 1,42	W-MAN: el cortador trocea el esqueleto al cont	-	2,1	2,9
-	EM	Estantería de matrices (8 juegos) y carro	1,20 × 1,70	W-MAN: 8 juegos, al lado de la prensa	-	2,0	2,8
5	M10	Numerado de cúpula: micropercusión Pannier	1,00 × 0,80	W-MAN: marcadora de columna sobre banco	1	0,8	2,2
4.1	M09a	Preparación de cuello: prensa de muesca Pa	1,00 × 0,80	W-MAN: prensa de banco neumática 3.500 kg	1	0,8	2,2
4.2	M09b	Preparación de cuello: prensa de muesca Pa	1,00 × 0,80	W-MAN: prensa de banco neumática 3.500 kg	1	0,8	2,2
8	M11	Soldadura de cuello Firesafer FS-HFM1	1,60 × 1,20	Cotiz. Firesafer FS-HFM1 (plato divisor)	1	1,9	5,3
9	E09	Prensa de encastre Del Fabro 30 t	1,20 × 1,00	W-MAN: prensa hidráulica motorizada, matriz po	1	1,2	3,3
10	B04	Bordoneadora motorizada Pilman SWM-400	1,00 × 0,80	Cotiz. Pilman / Bendmak SWM-400	1	0,8	2,2
11.1	A06	Soldadora circunferencial Firesafer	2,00 × 1,40	W-MAN: cúpula y fondo a la vez, MAG 350 A	1	2,8	7,7
11.2	B06	Soldadora circunferencial Firesafer	2,00 × 1,40	W-MAN: cúpula y fondo a la vez, MAG 350 A	1	2,8	7,7
12	Q01	Control de espesor: mesa y ultrasonido Mel	1,20 × 0,80	W-MAN: mesa al costado de la salida	1	1,0	2,6
13.1	A07	Prueba hidráulica Firesafer FS-JD12A	2,40 × 1,60	Cotiz. Firesafer FS-JD12A (huella de catálogo)	1	3,8	10,6
13.2	B07	Prueba hidráulica Firesafer FS-JD12A	2,40 × 1,60	Cotiz. Firesafer FS-JD12A (huella de catálogo)	1	3,8	10,6
-	DEC	Cámara de decantación y separador de aceit	2,60 × 1,20	W-MAN: compartidos con el ensayo de pérdidas;	-	3,1	4,3
14.1	B14a	Secadora de cilindros (boquilla en el cuel	1,40 × 0,90	W-MAN: secadora Yukon; D gabinete de 4 boquill	1	1,3	3,5
14.2	B14b	Secadora de cilindros (boquilla en el cuel	1,40 × 0,90	W-MAN: secadora Yukon; D gabinete de 4 boquill	-	1,3	1,7
14.3	B14c	Secadora de cilindros (boquilla en el cuel	1,40 × 0,90	W-MAN: secadora Yukon; D gabinete de 4 boquill	1	1,3	3,5
14.4	B14d	Secadora de cilindros (boquilla en el cuel	1,40 × 0,90	W-MAN: secadora Yukon; D gabinete de 4 boquill	-	1,3	1,7
15	RIN	Rodillos de entrada de la granalladora	1,50 × 0,90	W-MAN: los cilindros entran acostados	-	1,3	1,9
15	B08	Granalladora de rodillos AirBlast G-100	4,50 × 1,30	Cotiz. Airblast G-100 4500 × 1300	1	5,8	16,1
-	B13	Colector de polvo de la granalladora	1,80 × 1,40	colector de cartuchos del G-100	-	2,5	3,5
15	ROUT	Rodillos de salida y boquilla de soplado	1,50 × 0,90	W-MAN: soplado del polvo a la salida	-	1,3	1,9
16	B09	Detección de defectos: mesa iluminada	2,20 × 1,20	W-MAN: a continuación de los rodillos de salid	1	2,6	7,3
-	J1	Jaula «a corregir»	1,00 × 1,00	W-MAN: tres jaulas al lado del puesto	-	1,0	1,4
-	J2	Jaula «a re-granallar»	1,00 × 1,00	W-MAN	-	1,0	1,4
-	J3	Jaula «descarte»	1,00 × 1,00	W-MAN	-	1,0	1,4
17	B10	Corrección: mesa y cabina de amolado con e	2,20 × 1,50	W-MAN: amoladora 115 mm, machos y calibres	1	3,3	9,1
18.1-3	P03	Horno a gas: precalentamiento y curado 180	2,44 × 6,00	Cotiz. Electricolor 6 × 2,44 m; W-MAN 15 a 20	-	14,6	20,2
18.2	P04	Cabina de pintura 2 × 1,5 m y reciprocador	1,70 × 2,00	Cotiz. Electricolor	1	3,4	9,4
-	P05	Ciclones de recuperación de polvo (2)	1,40 × 1,70	Cotiz. Electricolor	-	2,4	3,3
-	P02	Equipos de aplicación y tolvas EC40-200D	1,00 × 1,80	Cotiz. Electricolor	-	1,8	2,5
18.4	P08	Enfriamiento y descarga: separa vacíos y t	5,50 × 6,80	Cotiz. Electricolor; W-MAN: el flujo se divide	1	37,4	103,1
-	P09	Control de espesor de película y adherenci	2,00 × 1,40	W-MAN: por muestreo, con registro de temperatu	-	2,8	3,9
-	RKP	Rack pesado de big bags y pallets de pintu	1,10 × 2,80	X-ALM: big bags de 1 t y pallets, 11 posicione	-	3,1	4,2
19	BB1	Estación de big bag (ABC 60) con transport	1,80 × 1,80	W-MAN: bastidor con polipasto y transferencia	-	3,2	4,5
19	T01	Cargadora de polvo por vacío Yukon M-00012	1,60 × 1,20	Cotiz. Yukon M-000121; W-MAN	1	1,9	5,3
20	T03	Ensamblaje: llave dinamométrica y estante	1,60 × 1,20	W-MAN: puesto manual	1	1,9	5,3
21	T05	Presurización con N2: pinza Yukon M-000150	1,50 × 1,00	Cotiz. Yukon M-000150; N2 por cañería del pack	1	1,5	4,1
22	T06	Ensayo de pérdidas: tanque de inmersión y	2,00 × 1,00	W-MAN: 6 matafuegos por tanda, 100 mm de agua	1	2,0	5,5
23	T07	Etiquetado: dispensador, posicionador e im	1,60 × 0,80	W-MAN: etiqueta preimpresa + n° de serie y fec	1	1,3	3,5
24.3	T11	Envolvedora de pallets EDOS PS5	1,80 × 1,80	Cotiz. EDOS PS5 (plato Ø1,65 m + columna)	-	3,2	4,5
24	AC1	Armadora automática de cajas (caja del 1 k	2,40 × 1,20	W-MAN: al inicio de las mesas de encajonado (a	-	2,9	4,0
24.1	T09	Mesa de encajonado: terminados	1,60 × 0,80	W-MAN y X-MAN (embalaje 2): al final de la ter	1	1,3	3,5
24.2	T08	Mesa de encajonado: cilindros vacíos	1,60 × 0,80	W-MAN: al lado de la descarga de pintura	1	1,3	3,5
-	RKE	Rack de embalaje (6 mód. × 4 niveles)	16,20 × 1,10	X-ALM: 48 posiciones de cajas plegadas, film y	-	17,8	24,6
-	RK1	Rack RK1 (7 mód. × 5 niveles)	18,90 × 1,10	X-DT 128 pallets: 7 módulos de 2,7 m × 2 palle	-	20,8	28,7
-	RK2	Rack RK2 (7 mód. × 5 niveles)	18,90 × 1,10	X-DT 128 pallets: 7 módulos × 2 × 5 = 70 (tota	-	20,8	28,7
-	RKR	Rack de revendidos (2 mód. × 4 niveles)	1,10 × 5,40	X-ALM: 17 posiciones	-	5,9	8,2
C3	C01	Roladora hidráulica CNC W12 8 × 1500	3,20 × 1,40	W-CAR: ≈ 3,2 × 1,4 m (a confirmar)	1	4,5	12,4
C4	C02a	Punteo: virador sobre base fija	1,20 × 0,60	W-CAR: 1,2 × 0,6 con 1 m libre en cada boca; X	1	0,7	2,0
-	C02s	Soldadora Pampa 300 y banco con morsa	2,00 × 0,90	W-CAR: soldadora 0,9 × 0,5 y banco 1,5 × 0,7	-	1,8	2,5
C5	C04	Soldadora longitudinal ZH-1300 con mesa	2,30 × 1,14	W-CAR: 2,30 × 1,14 m; fuente MIG-350IX y chill	1	2,6	7,2
C6	C06	Soldadura de cupla: mesa Müller con posici	0,90 × 0,60	W-CAR: ≈ 0,9 × 0,6 m	1	0,5	1,5
C7	C05	Armado y soldadura circ.: virador con tope	1,60 × 0,80	W-CAR: ≈ 1,6 × 0,8 m, 1 m libre en cada punta	1	1,3	3,5
C8	C08	Soldadura de accesorios e inspección de co	1,60 × 0,80	W-CAR: ≈ 1,6 × 0,8 m, 1 m libre en cada punta	1	1,3	3,5
-	C81r	Rack de barras (6,5 m) y caballetes	6,60 × 1,20	W-CAR 8.1: 6,5 × 0,6 + caballetes 6,8 × 0,6	-	7,9	10,9
C8.1	C81	Sensitiva, dobladora, taladro, prensa 20 t	6,00 × 1,30	W-CAR 8.1: ≈ 8,0 × 4,0 m	1	7,8	21,5
C9	C07	PH: 2 bandejas, pantalla y Yukon M-000200	3,00 × 1,40	Cotiz. Yukon M-000200; W-CAR tabla del puesto	1	4,2	11,6
-	C07t	Tanque de 1.000 L con bomba y filtros (cir	1,56 × 1,56	W-CAR: Rotoplas Ø1,56 m en el rincón del fondo	-	2,4	3,4
C10	C10	Secadora eléctrica Melisam MR011 (lanza a	0,60 × 0,50	W-CAR 10: ≈ 0,6 × 0,5 m, resistencia de ≈ 2 kW	-	0,3	0,4
C12	C12J	Cambio de juego (2 lugares): crique carrit	4,00 × 1,50	W-CAR 12: 2 × (2,0 × 1,5 m)	1	6,0	16,5
C13A	T12	Estación A: cinta y control del interior (	2,40 × 2,20	W-CAR 13: 2,4 × 2,2 m del lado del pulmón de p	1	5,3	14,6
C13B	T02	Estación B: balanza de plataforma con ramp	2,60 × 2,60	W-CAR 13: 3,0 × 2,6 m; C Yukon M-000121	1	6,8	18,6
-	BB2	Bastidor de big bag (ABC 90) con tolva de	1,60 × 1,20	W-CAR 13: 1,6 × 1,2 m detrás de la balanza, co	-	1,9	2,6
-	CL13	Colector de polvo 3 HP (aspiración en la b	0,80 × 0,80	W-CAR 13	-	0,6	0,9
-	BN2	Batería de N2 (11 tubos de 50 L) en jaula,	0,90 × 2,60	W-CAR 13: 2,6 × 0,9 m contra la pared, encaden	-	2,3	3,2
C13C	T13	Estación C: manga, traba, precinto y tarje	2,30 × 2,20	W-CAR 13: 2,3 × 2,2 m del lado del etiquetado	1	5,1	14,0
C15	T15	Etiquetado e inspección final: mesa de cal	1,20 × 0,60	W-CAR 15: mesa 1,2 × 0,6 m	-	0,7	1,0
C14	C14	Split frío/calor BGH 3000F y registrador (	0,60 × 0,80	W-CAR 14	-	0,5	0,7
C17	C17R	Recinto de descarga 12 × 3 m, alto 3 m, co	11,00 × 3,00	W-CAR 17: viento < 15 km/h, alcance marcado ca	1	33,0	91,0
-	C17C	Colector de polvo con filtro de mangas (3	1,00 × 1,00	W-CAR 17: ≈ 1,0 × 1,0 m en el fondo del recint	-	1,0	1,4
-	BP2	Balanza de plataforma 1,2 × 1,2 m con ramp	1,20 × 1,20	W-CAR 17: al lado de la puerta del recinto, de	-	1,4	2,0
-	CG1	Reguladores de Arcal 21 y N2 (de la jaula	2,00 × 1,20	W-MAN: pack con manifold y cañería a los puest	-	2,4	3,3
-	CH1	Colector de humos de soldadura (filtro de	2,40 × 1,50	colector de cartuchos 6000 m³/h	-	3,6	5,0
-	CP1	Compresor de tornillo 30 kW	1,90 × 1,10	compresor de tornillo 30 kW (1,9 × 1,1)	-	2,1	2,9
-	CP2	Compresor de tornillo 30 kW (reserva)	1,90 × 1,10	compresor de tornillo 30 kW (1,9 × 1,1)	-	2,1	2,9
-	SEC	Secador frigorífico y filtros	1,00 × 0,90	secador para 5 m³/min	-	0,9	1,2
-	TQ1	Pulmón de aire 2000 L	1,20 × 1,20	tanque vertical Ø 1,2 m	-	1,4	2,0

Guerchet por sector: St = Ss + Sg + Se, k = 0,38

Sector	St Guerchet	Dibujado	Holgura
AL-3	57	146	88
AL-CA	4	5	1
AL-CC	19	15	-4
AL-CH	23	18	-5
AL-CQ	8	8	-1
AL-CT	14	12	-2
AL-CU	4	25	21
AL-EB	25	23	-1
AL-FL	11	9	-2
AL-ID	1	2	1
AL-MC	4	4	-1
AL-MM	17	14	-3
AL-SS	6	5	-1
C-10	0	12	12
C-12C	17	23	7
C-13	54	58	4
C-14	1	25	24
C-15	1	10	9
C-17	94	70	-25
C-3	12	38	25
C-4	4	31	27
C-5	7	26	19
C-6	1	18	17
C-7	4	34	31
C-8	4	31	28
C-81	32	32	-0
C-9	15	23	8
DP	4	13	8
EMB	15	71	56
N1	34	56	23
N2	22	30	7
N3	29	31	2
N4	49	94	45
N5	45	93	48
N6	11	29	18
N7	12	37	26
N8	9	24	15
S-P	142	286	144
S-T	28	55	27
S4	8	7	-1
SC	17	75	58

Sg = Ss × N (lados de operación); Se = k (Ss + Sg), k = h móviles / (2 h fijos) = 1,65 / (2 × 2,18). La holgura incluye los pulmones de los Word (W-MAN, W-CAR), calles y estanterías; Guerchet no los cuenta. En los sectores de carros 11 y 16 el área es casi toda pulmón (120 y 180 carros a 0,5 m² por carro, W-CAR).

Locales y su equipamiento (ningún local vacío)

Local	m²	Equipamiento / función
SV-LU Utilitarios de limpieza	10,3	Pileta de lavado, carros, máquina de piso y artículos de limpieza
SV-HY Higiene y seguridad, medicina laboral,	16,7	Una sola persona: escritorio, camilla, botiquín y lavabo; entrega de EPP por ventani
SV-AC Sanitario accesible con ducha	13,7	Inodoro con 0,80 m libre lateral, lavabo, ducha a nivel con asiento rebatible y barr
SV-HA Hall, recepción y fichado	24,7	Reloj biométrico y tablero de novedades al paso (las visitas de administración entra
SV-VH Vestuario hombres (42 lockers)	25,2	1 locker por empleado: 2 bloques de 7 columnas × 3 filas = 42 (39 en 2035 sin recarg
SV-DH Duchas hombres	18,2	3 duchas sobre la misma pared (art. 49: 40 H en el turno mañana con choferes piden 2
SV-SH Inodoros, mingitorios y lavabos hombre	26,0	3 inodoros en la pared norte, 6 mingitorios en la pared este y 6 lavabos en la pared
SV-VM Vestuario mujeres (9 lockers)	15,8	1 bloque de 3 columnas × 3 filas = 9 lockers (7 en 2035) y banco
SV-SM Inodoro y lavabo mujeres	9,7	Art. 49: 6 M por turno -> 1 inodoro y 1 lavabo
SV-DM Ducha mujeres	9,7	1 ducha, separada del inodoro
SV-CM Comedor (30 plazas) y office	70,0	5 mesas de 6 lejos de la puerta; office con bacha y lavamanos sobre la misma pared;
SN-H Sanitarios hombres (planta)	17,4	2 inodoros y 2 mingitorios (pared norte) y 2 lavabos (pared este)
SN-M Sanitario mujeres (planta)	7,8	1 inodoro y lavabo
AD-OF Administración: compras, ventas y RRHH	52,6	4 puestos (compras 1, ventas 2, RRHH 1) y archivo; puerta a PO-6 para ir a la planta
AD-HA Hall y recepción de visitas	31,1	Entrada por la fachada este (AD-1), lejos de P1 y del alero de MP
AD-SA Sanitario accesible de administración	9,6	Inodoro accesible y lavabo (Ley 24.314); lo usan las visitas y el personal de admini
AL-1N Gasoil del autoelevador	2,1	Armario de inflamables; el Heli CPCD50 diésel (W-MAN) se estaciona al final del pasi
AL-CU Cuarentena de MP (compartida manuales	25,0	W-MAN y W-CAR tabla 5: 10 × 2,5 m, demarcada en amarillo: pallets, mesa de inspecció
AL-RE Retenidos de MP (no conforme)	6,0	W-CAR tabla 5: 4 × 1,5 m demarcados en rojo, 3 pallets; se reclama al proveedor
SC Compresores y colector de humos	74,9	Reguladores de Arcal 21 y N2 que vienen de la jaula exterior (puerta PG), colector d
ST-I Tableros de la línea este y compresor d	26,9	Tablero de N5 y de pintura y compresor sin aceite dedicado a la cabina (pasa del ex
MT Taller de mantenimiento	37,2	Mantenimiento preventivo: bancos, torno, agujereadora, soldadora móvil; entra la tra
PÑL Pañol de mantenimiento y de línea	17,7	Pegado al taller: repuestos críticos, herramental del preventivo, consumibles de sol
QR Cuarentena de producto y muestras retenid	15,3	Jaula con llave: lotes rechazados y un cilindro testigo por lote (IRAM 3517 / 3523)
Q Laboratorio de calidad	33,9	Metrología, ensayo de rotura (1 cilindro por lote, W-MAN), adherencia y espesor de p
PCP Planificación y control de la producción	17,9	2 puestos y tablero de programación
SUP Supervisor de planta	24,3	Oficina propia del encargado de turno, con ventana a la banda de carros
C-17 Ensayos de lote de carros (17)	69,8	W-CAR ≈ 15,5 × 4,5 = 70 m²: recinto de descarga de 12 × 3 m (alto 3 m) con colector
C-14 Sala del ensayo de pérdidas (14)	25,0	W-CAR 5 × 5 m de paneles aislantes con puerta, 21 °C (split BGH 3000F y registrador)
DL Ducha de emergencia y lavaojos	6,0	A menos de 10 s de la carga de polvo, de la presurización y de la descarga de pintur

IMPLANTACIÓN GENERAL - 1:500

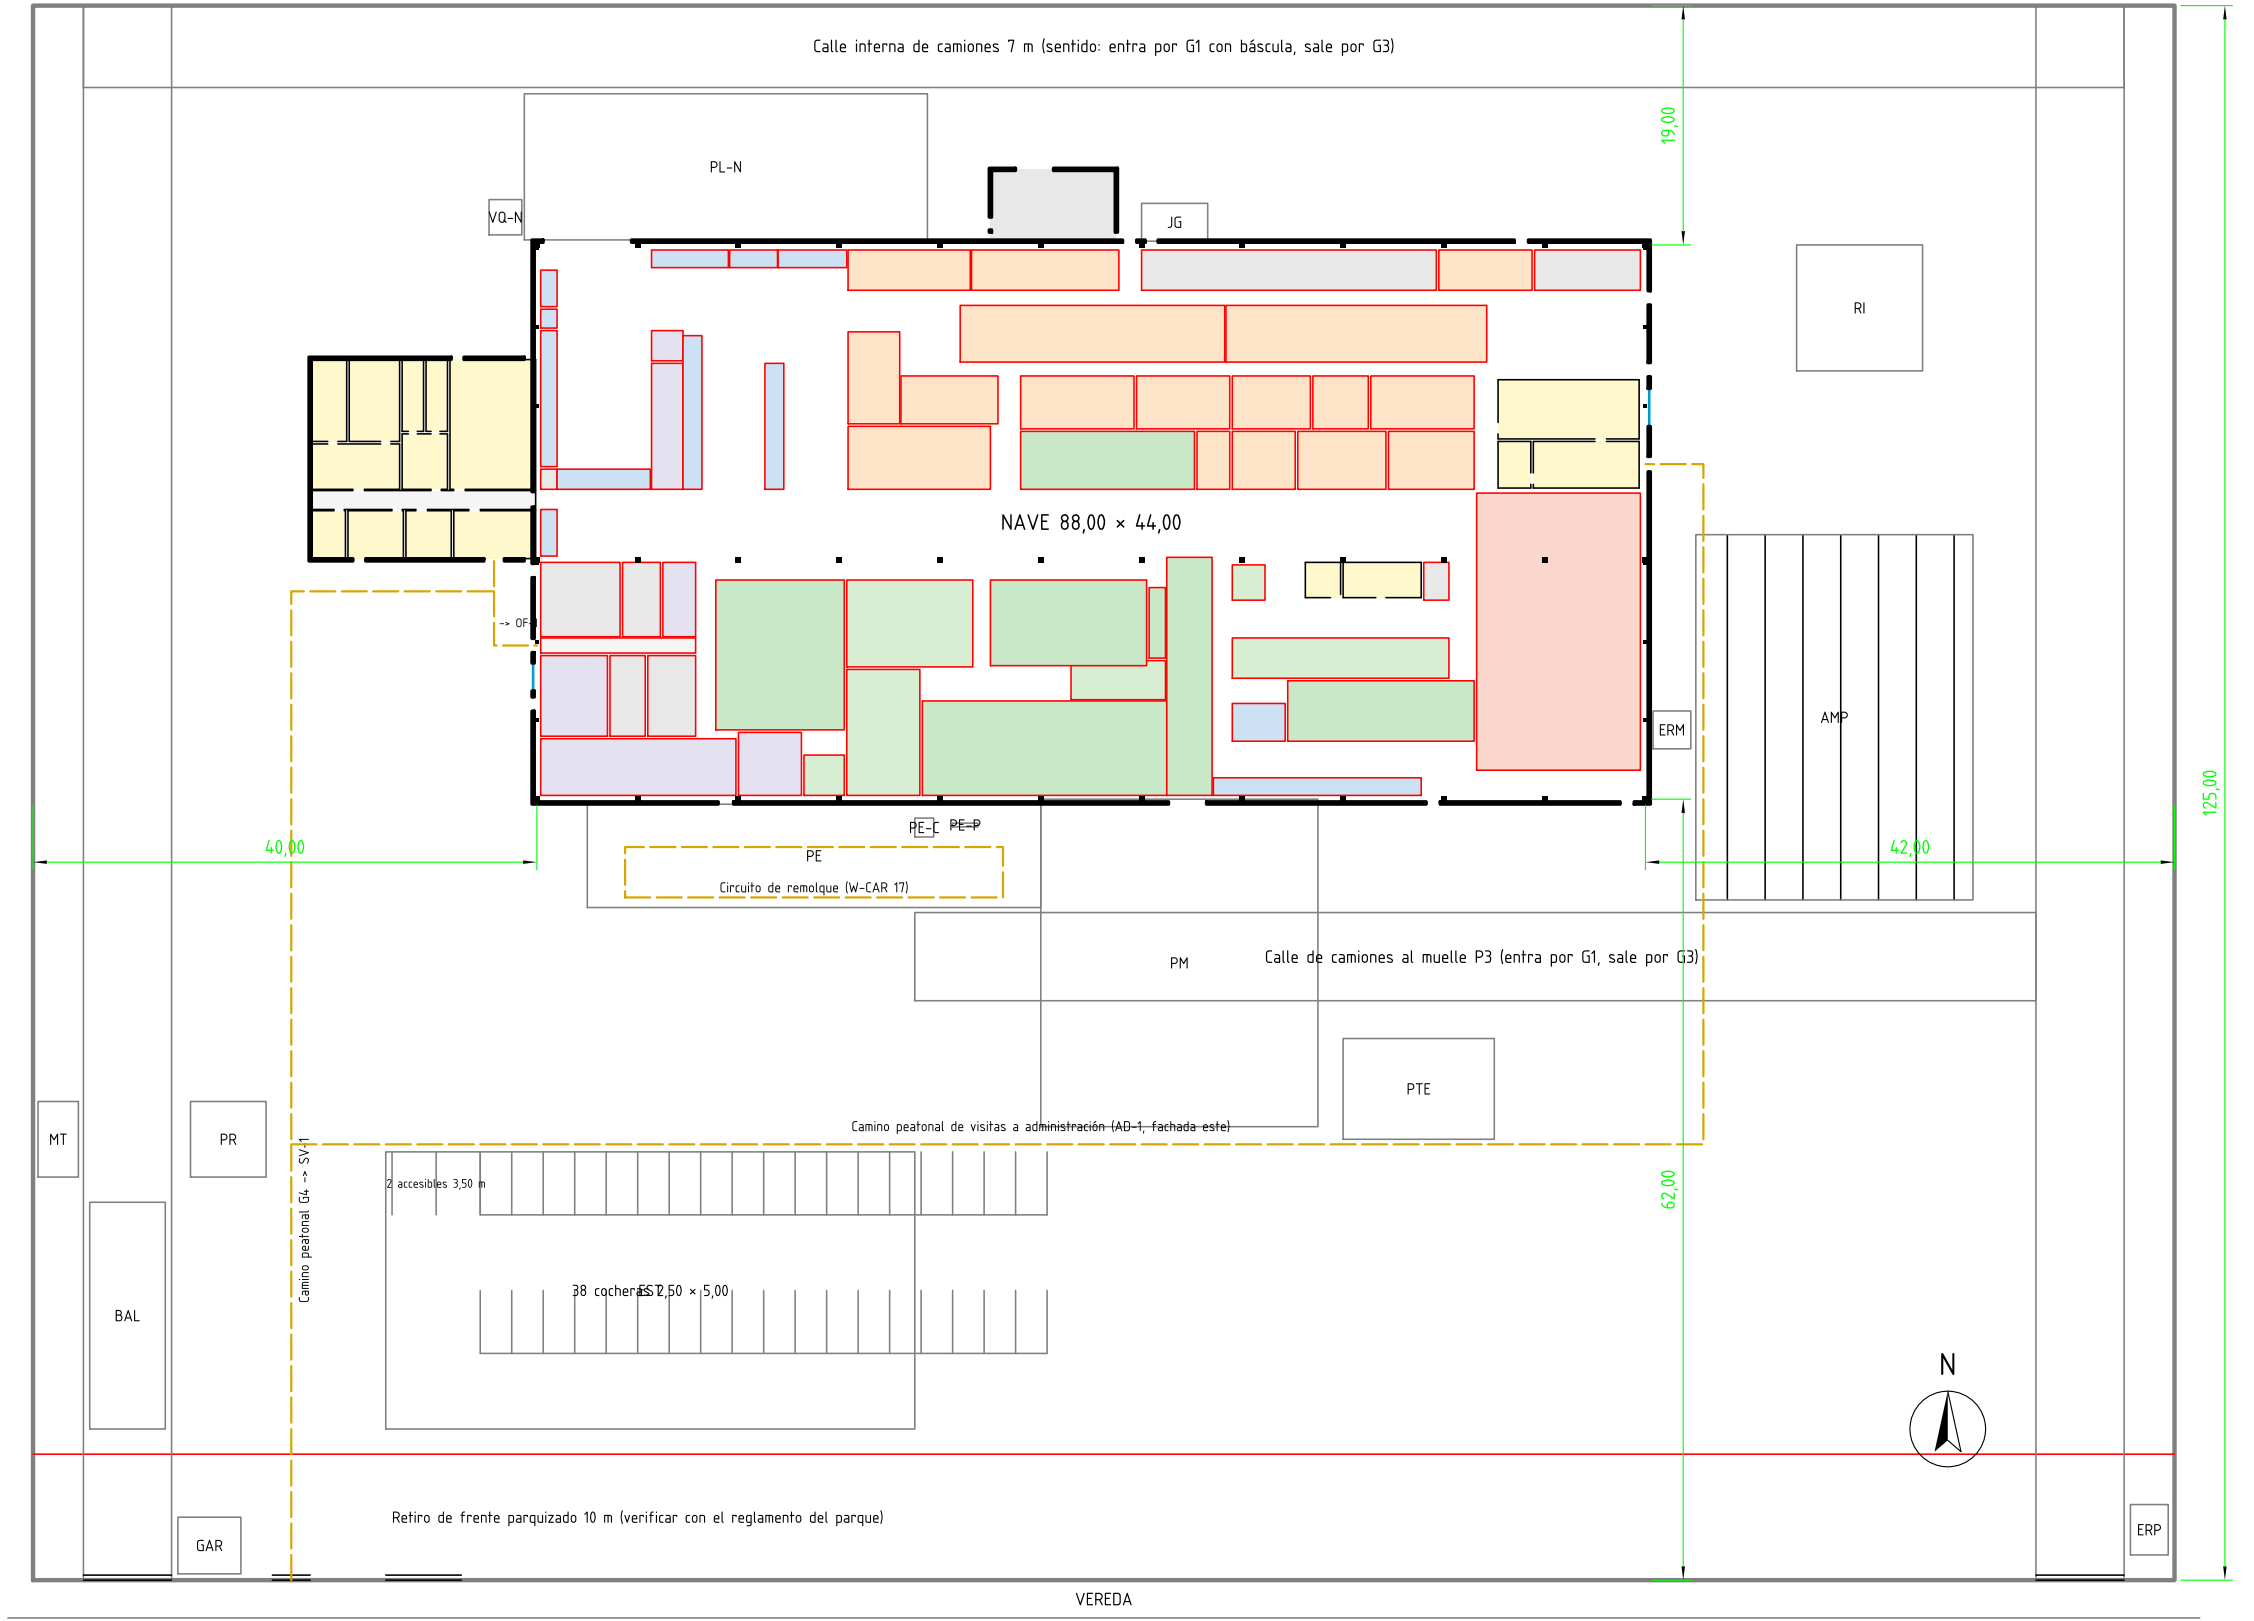
170,00
Calle interna de camiones 7 m (sentido: entra por G1 con báscula, sale por G3)
19,00
PL-N
VQ-N
JG
RI
NAVE 88,00 × 44,00
AMP
ERM
40,00
42,00
PE-C
PE-P
PE
Circuito de remolque (W-CAR 17)
PM
Calle de camiones al muelle P3 (entra por G1, sale por G3)
PTE
Camino peatonal de visitas a administración (AD-1, fachada este)
MT
PR
BAL
Camino peatonal G4 -> SV-1
2 accesibles 3,50 m
38 cocheras 2,50 × 5,00
EST
62,00
125,00
N
Retiro de frente parquizado 10 m (verificar con el reglamento del parque)
GAR
ERP
VEREDA
G1
G4
G2
G3
CALLE (acceso) - Gral. Heredia, Parque Industrial Villa de Luján

CORTE TRANSVERSAL A-A (por eje 4) - 1:200

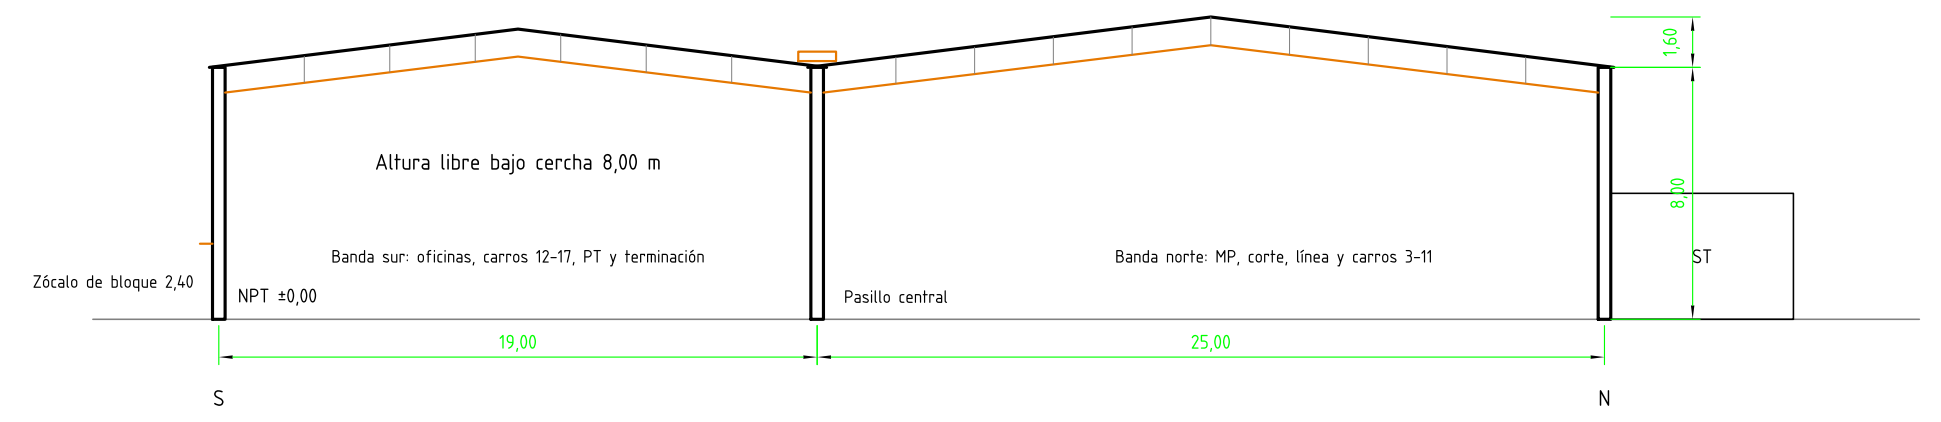
Altura libre bajo cercha 8,00 m
Banda sur: oficinas, carros 12-17, PT y terminación
Banda norte: MP, corte, línea y carros 3-11
Zócalo de bloque 2,40
NPT ±0,00
Pasillo central
ST
1,60
8,00
19,00
25,00
S
N

Cuadro de superficies

Concepto	m²	%
Terreno 170,00 × 125,00	21.250	100,0
Nave industrial 88,00 × 44,00	3.872	18,2
incluye oficinas de planta (SO) y administración (E)	254	
Servicios al personal	288	1,4
Sala técnica norte	58	0,3
Alero de descarga de MP	371	1,7
Superficie cubierta total	4.589	21,6
FOS = cubierta / terreno		0,22

Nave: pórticos metálicos de dos luces (19,40 y 24,60 m) cada 8 m; altura libre 8,00 m; zócalo de bloque 2,40 m y chapa; anexos de mampostería. Pisos de hormigón llaneado con demarcación IRAM 10005; sanitarios con revestimiento hasta 2,10 m (Dec. 351/79 cap. 5).

	Fecha	Nombre
Dibujó	15/10/26	Claude Code
Revisó		
Aprobó		

Escala: 1:100
Método de proyección: ISO E
Unidades: Cotas en m
Formato: 2A0

Propietario: FLAMA S.A.

Denominación:
Plano formal:
planta general acotada
Nave, servicios, oficinas y administración con equipos y mobiliario; implantación y corte

Tipo de documento: Plano de planta

Reemplaza a / Reemplazado por: -
Material: Estructura metálica / mampostería
Edición: 0
Fecha de emisión: 15/10/2026
Hoja: 1 / 1
Idioma: es
N° de plano: FL_PI_01