FL_PI_03 - PERSONAL, EVACUACIÓN Y SEÑALIZACIÓN

Planta industrial FLAMA S.A. - Parque Industrial Villa de Luján, Sarandí (Avellaneda) - dimensionada al año 10 (2035). Escala 1:200. Norte arriba; la calle de acceso está al sur.

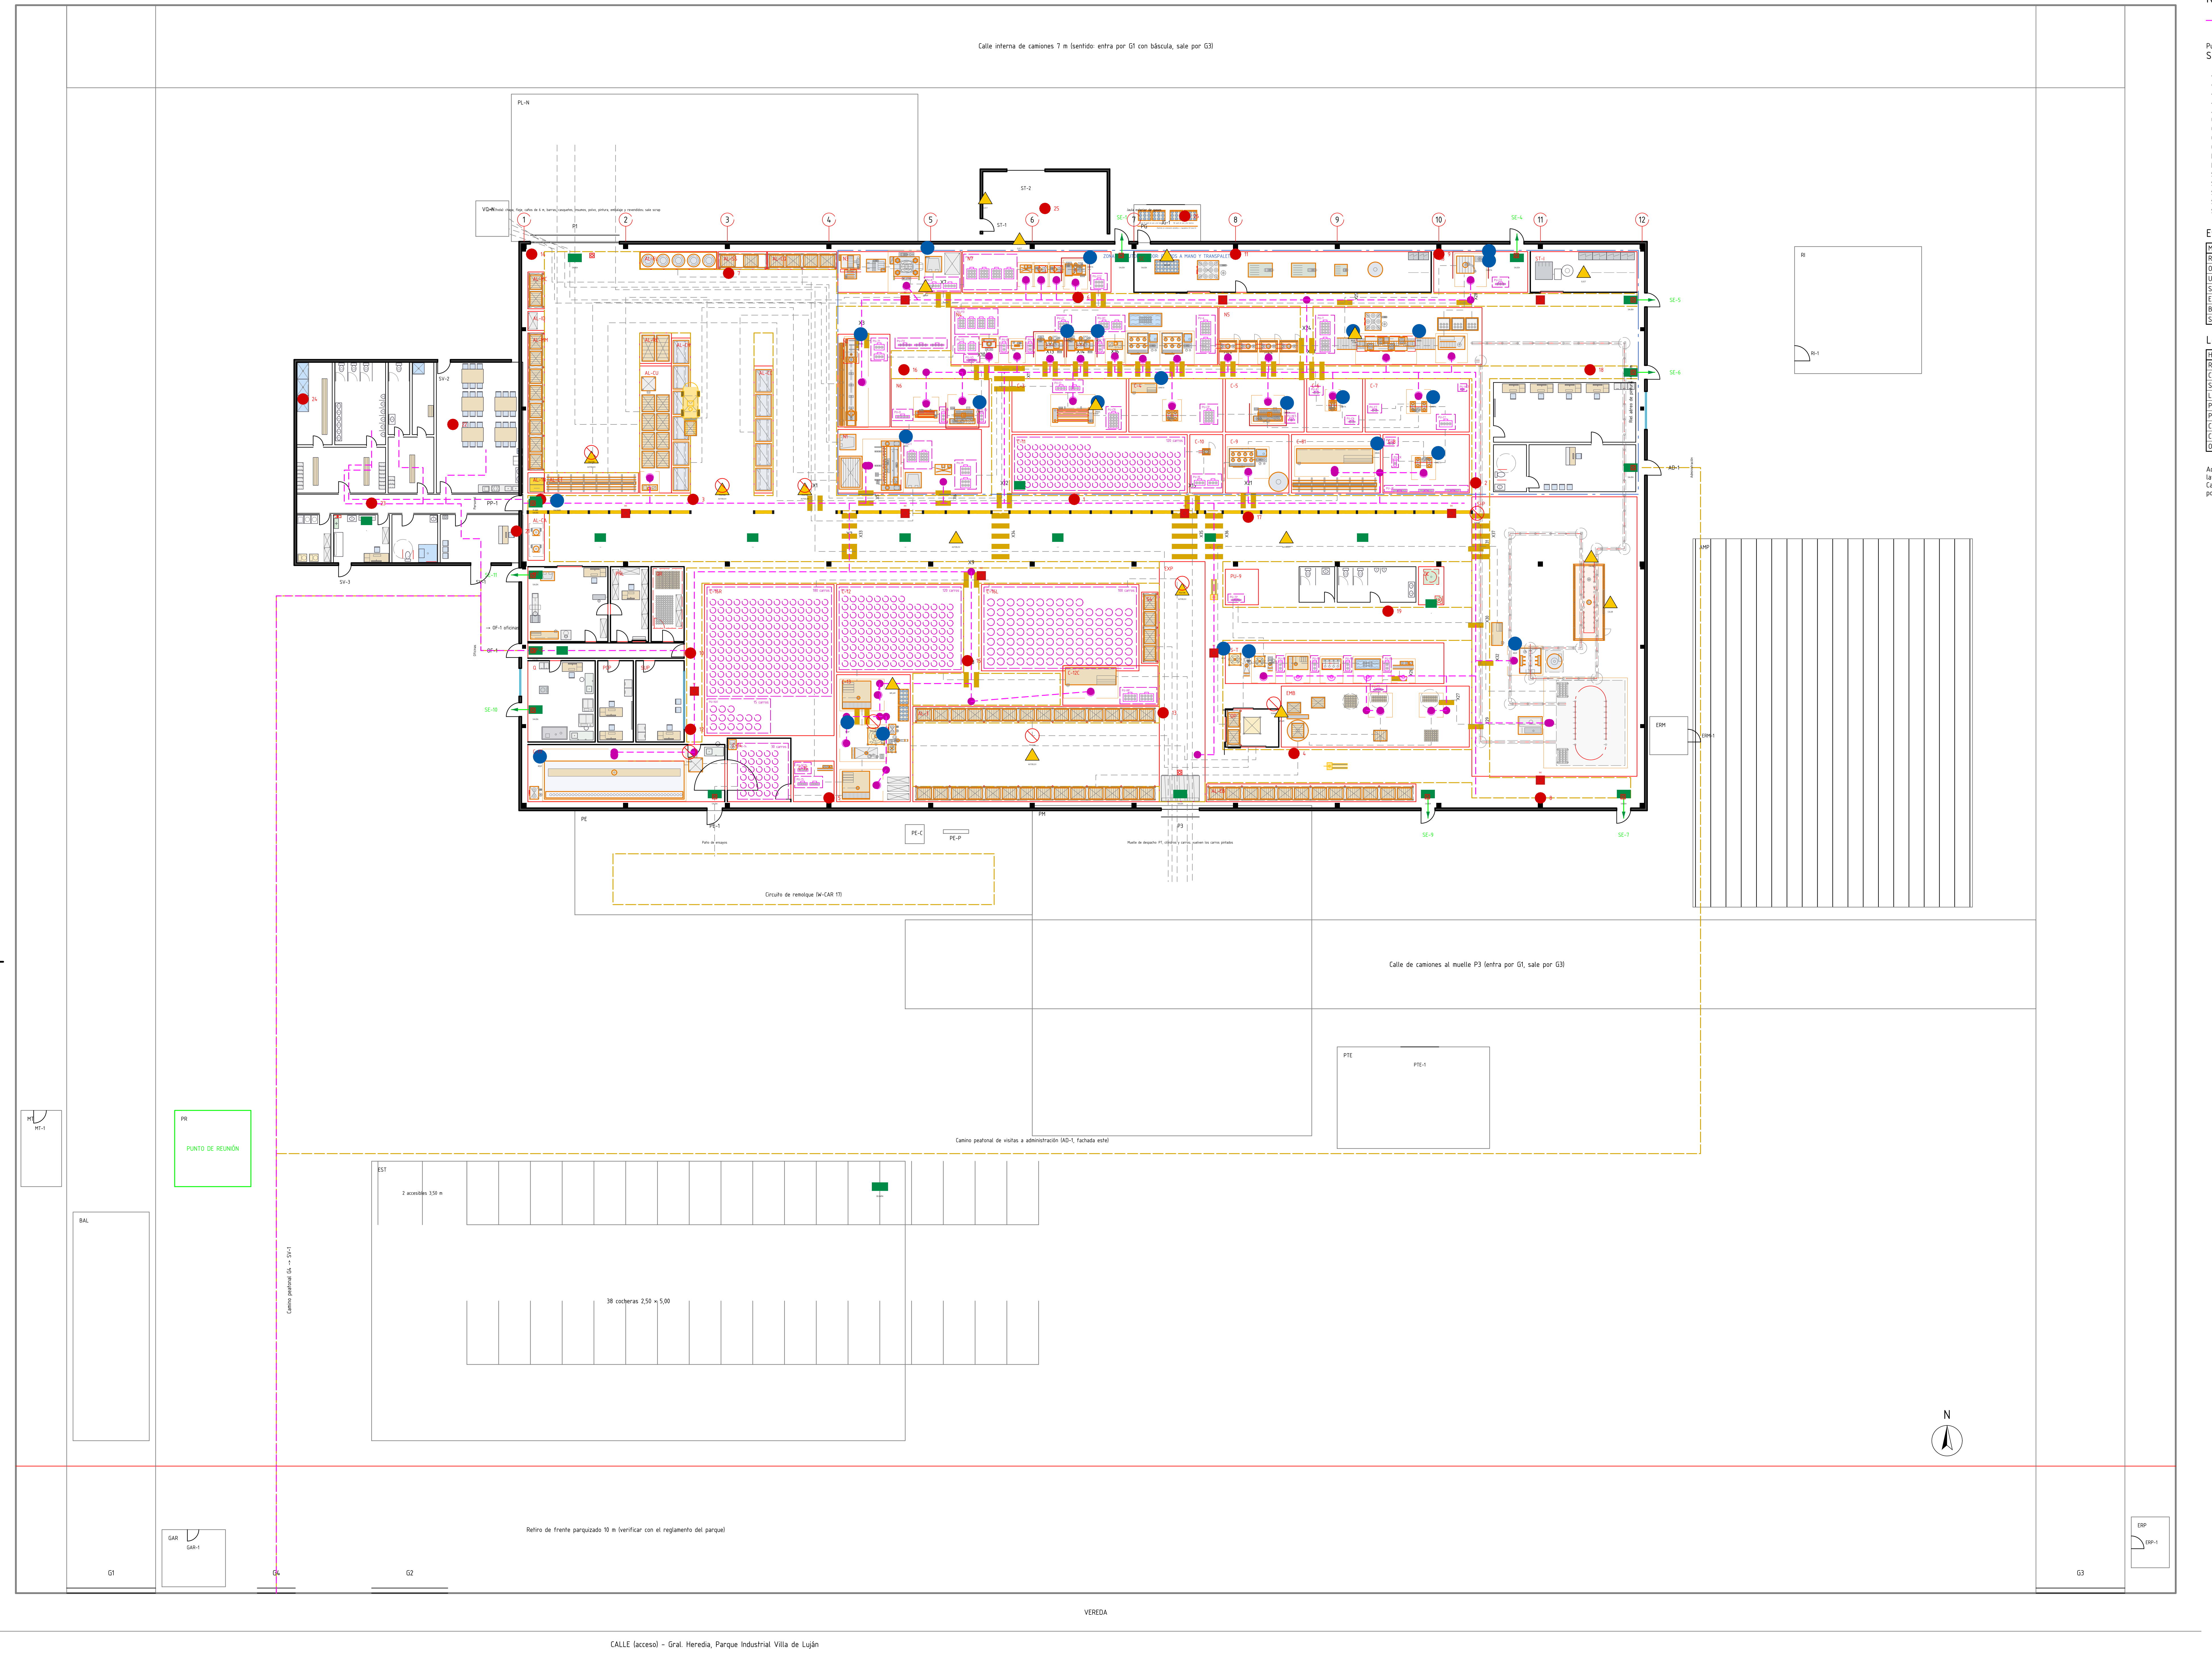
Calle interna de camiones 7 m (sentido: entra por G1 con báscula, sale por G3)
Calle de camiones al muelle P3 (entra por G1, sale por G3)
Camino peatonal de visitas a administración (AD-1, fachada este)
Circuito de remolque (W-CAR 17)
Patio de ensayos
Muelle de despacho: PT, cilindros y carros; vuelven los carros pintados
PE
PE-1
PE-C
PE-P
PM
P3
SE-9
SE-7
ERM
ERM-1
PTE
PTE-1
MT
MT-1
PR
PUNTO DE REUNIÓN
BAL
EST
2 accesibles 3,50 m
38 cocheras 2,50 × 5,00
Camino peatonal G4 -> SV-1
Retiro de frente parquizado 10 m (verificar con el reglamento del parque)
GAR
GAR-1
G1
G4
G2
G3
ERP
ERP-1
N
VEREDA
CALLE (acceso) - Gral. Heredia, Parque Industrial Villa de Luján

Referencias

Hilo de personal (DIR) y puesto de trabajo

X1..: senda peatonal (cebra) donde un hilo cruza un flujo

Punto rojo numerado: extintor ABC 10 kg BIE: boca de incendio equipada ☐: pulsador de alarma

Señales (IRAM 10005-1: formas y colores de seguridad)

Advertencia · ATRAP: Riesgo de atrapamiento / cargas suspendidas
Advertencia · AUTOELEV: Circulación de autoelevadores
Advertencia · CALOR: Superficie caliente (horno)
Advertencia · ELECT: Riesgo eléctrico
Advertencia · INFLAM: Gases a presión
Obligación · CALZADO: Calzado de seguridad y ropa de trabajo (ingreso a planta)
Obligación · CARETA: Careta fotosensible y guantes
Obligación · OÍDOS: Protección auditiva
Obligación · RESP: Respirador P2
Prohibición · FUMAR: Prohibido fumar y llama abierta
Prohibición · PEATON: Prohibido el paso de peatones (calle de autoelevador)
Salvamento y evacuación · +: Primeros auxilios / lavaojos
Salvamento y evacuación · ->: Recorrido de evacuación
Salvamento y evacuación · PLANO: Plano de evacuación (ingreso PP-1)
Salvamento y evacuación · REUNIÓN: Punto de reunión
Salvamento y evacuación · SALIDA: Salida

Evacuación y protección contra incendio

Medios de escape (Dec. 351/79 anexo VII)	Valor
Recorrido máximo real a una salida (grilla 0,5 m, tabiques y equipos)	33,2 m ≤ 40
Ocupación (16 m² por persona en la nave)	242 personas
Unidades de ancho de salida / ancho mínimo	3 / 1,55 m
Salidas de emergencia de 1,10 m con barral antipánico	8
Extintores ABC 10 kg (1 cada 200 m², recorrido ≤ 20 m)	26
Bocas de incendio equipadas / pulsadores de alarma	11 / 14
Sanitarios accesibles (servicios, con ducha, y administración)	2

Longitud de los hilos

Hilo (grupo de puestos)	Desde PP-1 (m)
Recepción, corte de chapa y marcado (N1)	39
Cuerpo, unión y PH (N4, N6)	32
Secado, granallado, detección y corrección (N5, N8)	44
Láser, embutido y celda de cuello (N2, N3, N7)	41
Pintura, terminación y embalaje	40
PT y expedición	21
Carros: puestos 3 a 11 (franja central)	40
Carros: puestos 12 a 17, depósito y calidad (banda sur)	41
Oficinas (MT, PÑL, QR, Q, PCP, SUP)	13

Sanitarios de vestuarios (art. 49): 40 H y 4 M

Artefacto	H req.	H proy.	M req.	M proy.
Inodoros	2	3	1	1
Lavabos	4	6	1	1
Orinales	4	6	0	0
Duchas	2	3	1	1
Armarios (art. 50)	39	42	5	9

Además: sanitarios de planta (banda sur, calle AT2) de hombres (2 inodoros, 2 mingitorios, 2 lavabos) y de mujeres (1 + 1), a < 25 m de pintura, terminación, embalaje y PT. Lockers: 1 por empleado. Cada operario tiene 1,0 m libre detrás de su puesto: ninguna calle ni material ajeno pasa por su espalda (verificado). Mamparas ignífugas en todos los puestos de soldadura.

	Fecha	Nombre
Dibujó	15/10/26	Claude Code
Revisó		
Aprobó		

Escala
1:200

Método de proyección
ISO E

Unidades
Cotas en m

Formato
A0

Propietario
FLAMA S.A.

Denominación
Personal y seguridad
DIR, medios de escape, protección contra incendio, IRAM 10005

Tipo de documento
Plano de seguridad e higiene

Reemplaza a / Reemplazado por
-

Material
-

Edición
0

Fecha de emisión
15/10/2026

Hoja
1 / 1

Idioma
es

N° de plano
FL_PI_03