FL_PI_05 - SERVICIOS AL PERSONAL, OFICINAS Y APOYO A LA LÍNEA

Todo en planta baja (sin entrepiso). Vestuarios y sanitarios (Dec. 351/79 arts. 49-50), accesibilidad (Ley 24.314); oficinas de planta en el ángulo SO (ex recargas) y administración al este, lejos de P1.


DETALLE 1 - SERVICIOS AL PERSONAL - 1:50




DETALLE 2 - OFICINAS DE PLANTA (SO): MANTENIMIENTO, PAÑOL, CALIDAD, SUPERVISOR Y PCP - 1:50




DETALLE 3 - ADMINISTRACIÓN (LADO ESTE) - 1:50

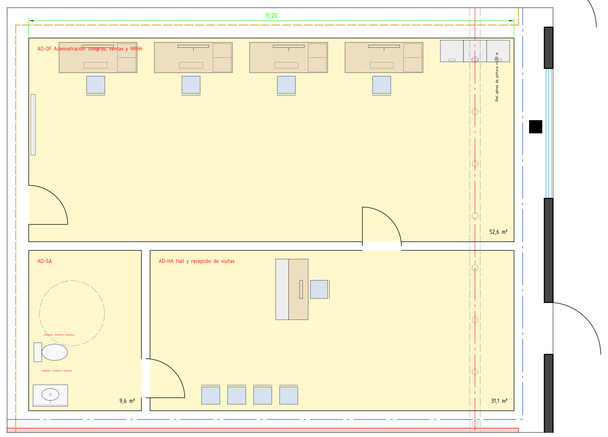

DETALLE 4 - SANITARIOS DE PLANTA (H Y M) - 1:50

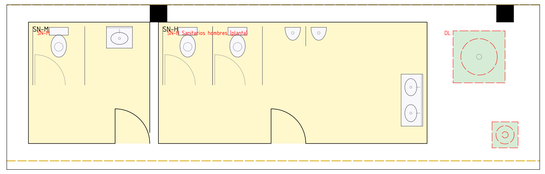

DETALLE 5 - COMPRESORES, COLECTOR Y JAULA EXTERIOR DE GASES - 1:50

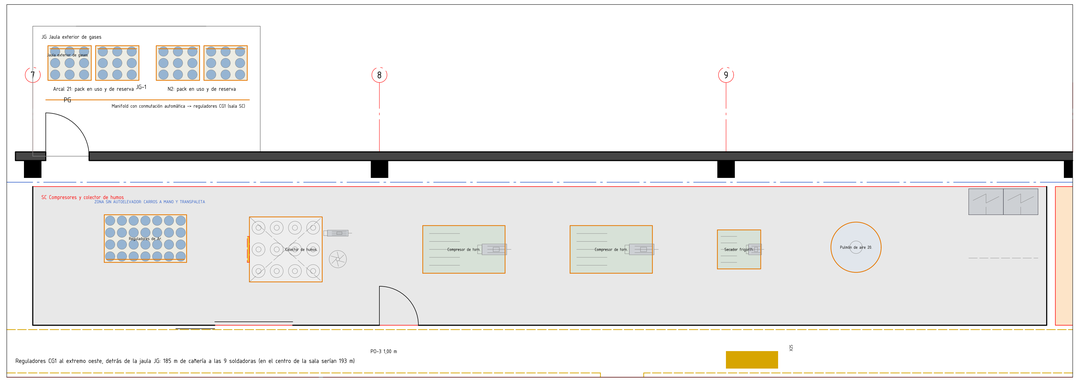

Circuito y criterios

1. Ingreso por SV-1 (camino peatonal desde G4 y la garita); fichado en el hall.
2. Pasillo limpio: al sur limpieza, higiene y seguridad (EPP y primeros auxilios), sanitario accesible y hall; al norte vestuarios y comedor.
3. Vestuario: 1 locker por empleado (bloques de 7 columnas × 3 filas). Duchas en su propio local, separadas de inodoros y mingitorios; todo sólo desde el vestuario.
4. Duchas, inodoros, mingitorios y lavabos: cada grupo alineado sobre una misma pared húmeda.
5. Comedor: abre directo al pasillo limpio (sin pasillo propio) y tiene su salida de emergencia SV-2; el office junto a la puerta y las mesas al fondo.
6. Oficinas de planta en el ángulo SO, donde estaba recargas: entrada OF-1 desde el camino peatonal y pasillo OF-C. Mantenimiento con portón al pasillo central y pañol pegado (ventanilla); calidad y referentes (QUA) juntos; supervisor con ventana a la planta y PCP al lado.
7. Administración (compras, ventas, RRHH) en el lado este, lejos del portón de MP: entrada de visitas AD-1 por la fachada este, hall, office y sanitario accesible propio; no entra nadie de afuera a la planta.
8. Sanitarios de planta sobre la calle AT2, a menos de 25 m de pintura, terminación, embalaje y PT.

Locales de servicios, oficinas, administración y apoyo a la línea

Local	m²	Equipamiento / criterio
SV-LU Utilitarios de limpieza	10,3	Pileta de lavado, carros, máquina de piso y artículos de limpieza
SV-MY Higiene y seguridad, medicina laboral, p	16,5	Una sola persona: escritorio, camilla, botiquín y lavabo; entrega de E
SV-AC Sanitario accesible con ducha	13,7	Inodoro con 0,80 m libre lateral, lavabo, ducha a nivel con asiento re
SV-HA Hall, recepción y fichado	24,7	Reloj biométrico y tablero de novedades al paso; las visitas de admin
SV-VH Vestuario hombres (42 lockers)	25,2	1 locker por empleado: 2 bloques de 7 columnas × 3 filas = 42 (39 en 2
SV-DH Duchas hombres	18,2	3 duchas sobre la misma pared (art. 49 -40 H en el turno mañana con ch
SV-SH Inodoros, mingitorios y lavabos hombres	26,0	3 inodoros en la pared norte, 6 mingitorios en la pared este y 6 lavab
SV-VM Vestuario mujeres (9 lockers)	15,8	1 bloque de 3 columnas × 3 filas = 9 lockers (1 en 2019) y banco
SV-SM Inodoro y lavabo mujeres	9,7	Art. 49 -6 M por turno → 1 inodoro y 1 lavabo
SV-DM Ducha mujeres	9,7	1 ducha, separada del inodoro
SV-CM Comedor (30 plazas) y office	70,0	5 mesas de 6 tapas de la puerta; office con bacha y lavamanos sobre la
SN-H Sanitarios hombres (planta)	17,4	2 inodoros y 2 mingitorios (pared norte) y 2 lavabos (pared este)
SN-M Sanitario mujeres (planta)	7,8	1 inodoro y lavabo
AD-OF Administración: compras, ventas y RRHH	52,6	4 puestos (compras 1, ventas 2, RRHH 1) y archivo; puerta a PO-6 para
AD-HA Hall y recepción de visitas	31,1	Entrada por la fachada este (AD-1); tapa de PI y del diario de MP
AD-SA Sanitario accesible de administración	9,6	Inodoro accesible y lavabo (Ley 24.314): lo usan las visitas y el pers
SC Compresores y colector de humos	74,9	Reguladores de Arcal 21 y N2 que vienen de la jaula exterior (puerta P
MT Taller de mantenimiento	37,2	Mantenimiento preventivo: bancos, torno, agujereadora, soldadora móvil
PAÑ, Pañol de mantenimiento y de línea	17,7	Pegado al taller: repuestos críticos, herramental del preventivo, cons
QM Cuarentena de producto y muestras retenidas	15,3	Jaula con llave: lotes rechazados y un cilindro testigo por lote (IRAM
Q, Laboratorio de calidad	33,9	Metrología, ensayo de rotura (1 cilindro por lote, W-MAN), adherencia
PCP Planificación y control de la producción	17,9	2 puestos y tablero de programación
SUP Supervisor de planta	24,3	Oficina propia del encargado de turno, con ventana a la banda de carro

	Fecha	Nombre	Propietario	Reemplaza a / Reemplazado por
Dibujó	15/10/26	Claude Code	FLAMA S.A.	–
Revisó			Denominación	Materias
Aprobó			Servicios, oficinas y apoyo	Mampostería / estructura metálica
Escala 1:50	Método de proyección ISO E			Edición 0 / Fecha de emisión 15/10/2026
Unidades Cotas en m	Formato A0		Tipo de documento Plano de detalle	Hoja 1 de 1 hojas / Idioma es
			Bloque de servicios, oficinas de planta (SO), administración (E), sanitarios de planta y jaula de compresores	Nº de plano FL_PI_05