
FL_PI10_03 – CIRCULACIÓN, FLUJOS DE MATERIALES Y RECORRIDOS DEL PERSONAL

Carriles del autoelevador, sendas peatonales y pasillos de operarios con su ancho; flujo de MP, de semielaborado y de PT; hilos del personal desde los vestuarios.

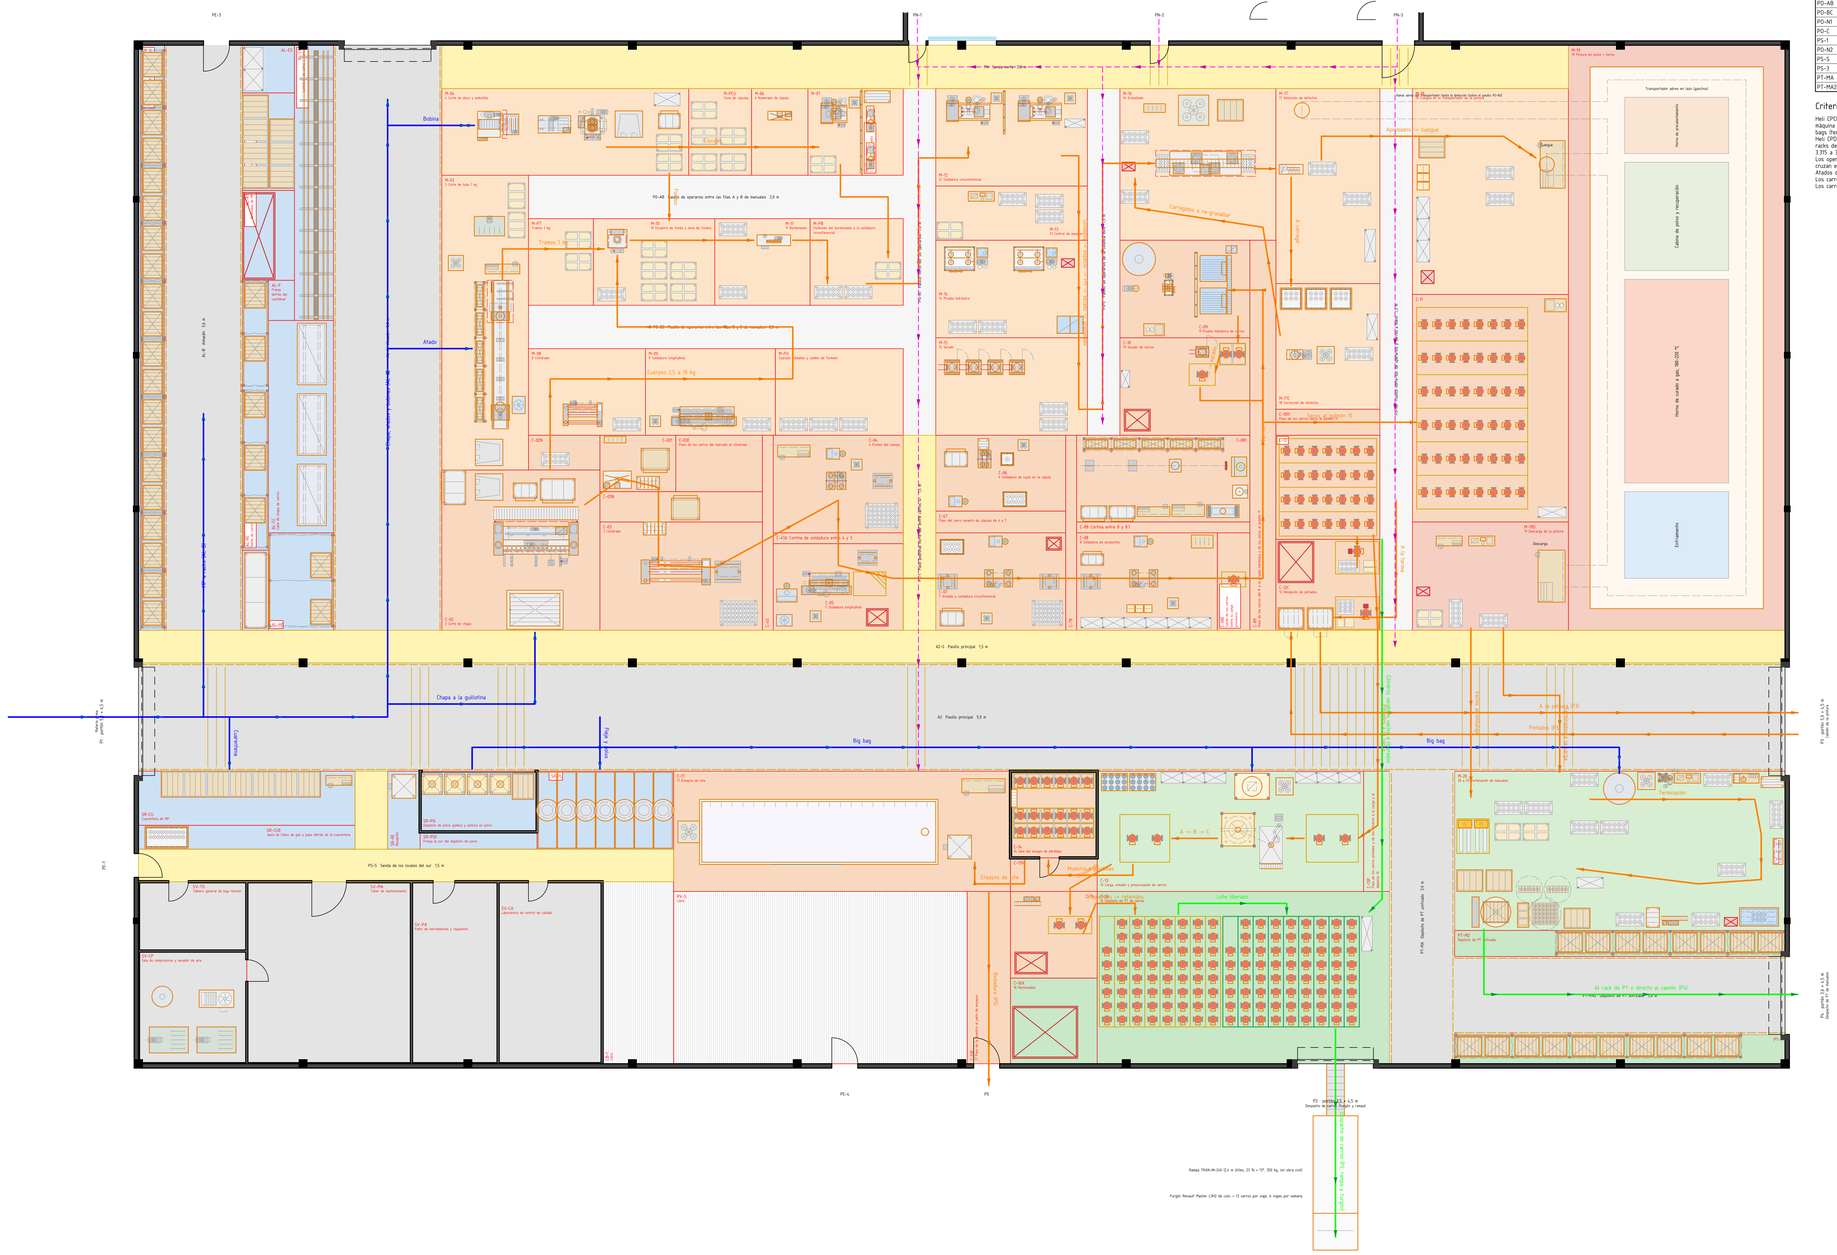

Referencias

- Carril del autoelevador (3,0 a 5,0 m)
- Senda peatonal demarcada
- Pasillo de operarios y carros a mano

Flujos

- MP: materia prima (azul)
- SE: semielaborado (naranja)
- PT: producto terminado (verde)
- Hilos de personal (magenta)

Pasillos (m)

Cód.	Pasillo	Ancho	Largo	Uso
A2	Pasillo principal	3,0	76,0	Autoelevador
A2-S	Pasillo principal	1,5	76,0	Peatonal
AL-A	Almacén	5,0	27,0	Autoelevador
AL-B	Almacén	3,6	27,0	Autoelevador
PN	Senda norte	2,0	52,0	Peatonal
PO-AB	Pasillo de operarios entre las filas A y B de manua.	2,0	17,3	Operarios
PO-BC	Pasillo de operarios entre las filas B y C de manua.	2,0	17,3	Operarios
PO-NH	Pasillo norte-sur de operarios	1,5	16,0	Operarios
PO-C	Pasillo de operarios de la columna este	1,5	16,0	Operarios
PS-1	Paso peatonal norte-sur entre carros 4/5 y 6/7	1,5	9,0	Peatonal
PO-N2	Pasillo norte-sur de operarios y carros a mano	1,5	25,0	Operarios
PS-S	Senda de los locales del sur	1,5	24,7	Peatonal
PS-3	Paso peatonal de la senda sur al pasillo principal	1,5	3,6	Peatonal
PT-MA	Depósito de PT unificado	3,0	13,5	Autoelevador
PT-MA2	Depósito de PT unificado	3,6	15,2	Autoelevador

Criterios de circulación

Heli CPCI50 (W-MAN y W-CAR) circula por A2 y AL-A (5,0 m) y entra a los puestos únicamente donde la máquina mira al carril: mesa elevadora, cajón del atado, desbobinador, contenedores de scrap (a PI1), big bags (terminación y carro 13), las tarimas de los carros 11 y 12 las lleva por el pasillo principal a PI1. Heli CPCI5 eléctrico (agregado por los pasillos angostos que pidió el usuario): racks R1 por AL-B (3,6 m); racks de P1 por PT-MA (5,0 m, un semitolil) y PT-MA2 (3,6 m), envolvedora y camión de P4. Apilado a 90° 3,315 a 3,515 mm según el pallet (ficha Heli CPCI5-20): el CPCI50 necesitaría 4,96 m. Los operarios caminan por las sendas (amarillas) y por los pasillos de operarios de 1,5 a 2,0 m, cruzan el carril sólo por los cruces demarcados de la baranda. Atados de 6 m se mueven colgados de la pluma (W-MAN 1 y 2), a lo largo del pasillo. Los carros de manuales (P-CMP y de 11 cajones) se empujan a mano entre puestos pegados (W-MAN). Los carros lechiformes rodantes ruedan sobre su juego provisorio desde el puesto B (W-CAR).

	Fecha	Nombre
Dibujó	16/10/26	Claude Code
Revisó		
Aprobó		
Escala	Método de proyección	
1:100	ISO E	
Unidades	Formato	
Cotas en m	A0	

Propietario	FLAMA S.A.
Denominación	Circulación y flujos Layout 2035 v10 – pasillos, materiales y personas
Tipo de documento	Plano de circulación
Reemplaza a / Reemplazado por	–
Material	–
Edición	0
Fecha de emisión	16/10/2026
Hoja	3 / 6
Idioma	es
N° de plano	FL_PI10_03