


FL_PI_01 - DIAGRAMA DE RECORRIDO DE HILOS DEL PERSONAL (DIR)

Planta Industrial FLAMA S.A. - Parque Industrial Villa de Luján, Sarandí (Avellaneda) - dimensionada al año 10 (2035). Escala 1:200. Norte arriba; la calle de acceso está al sur.

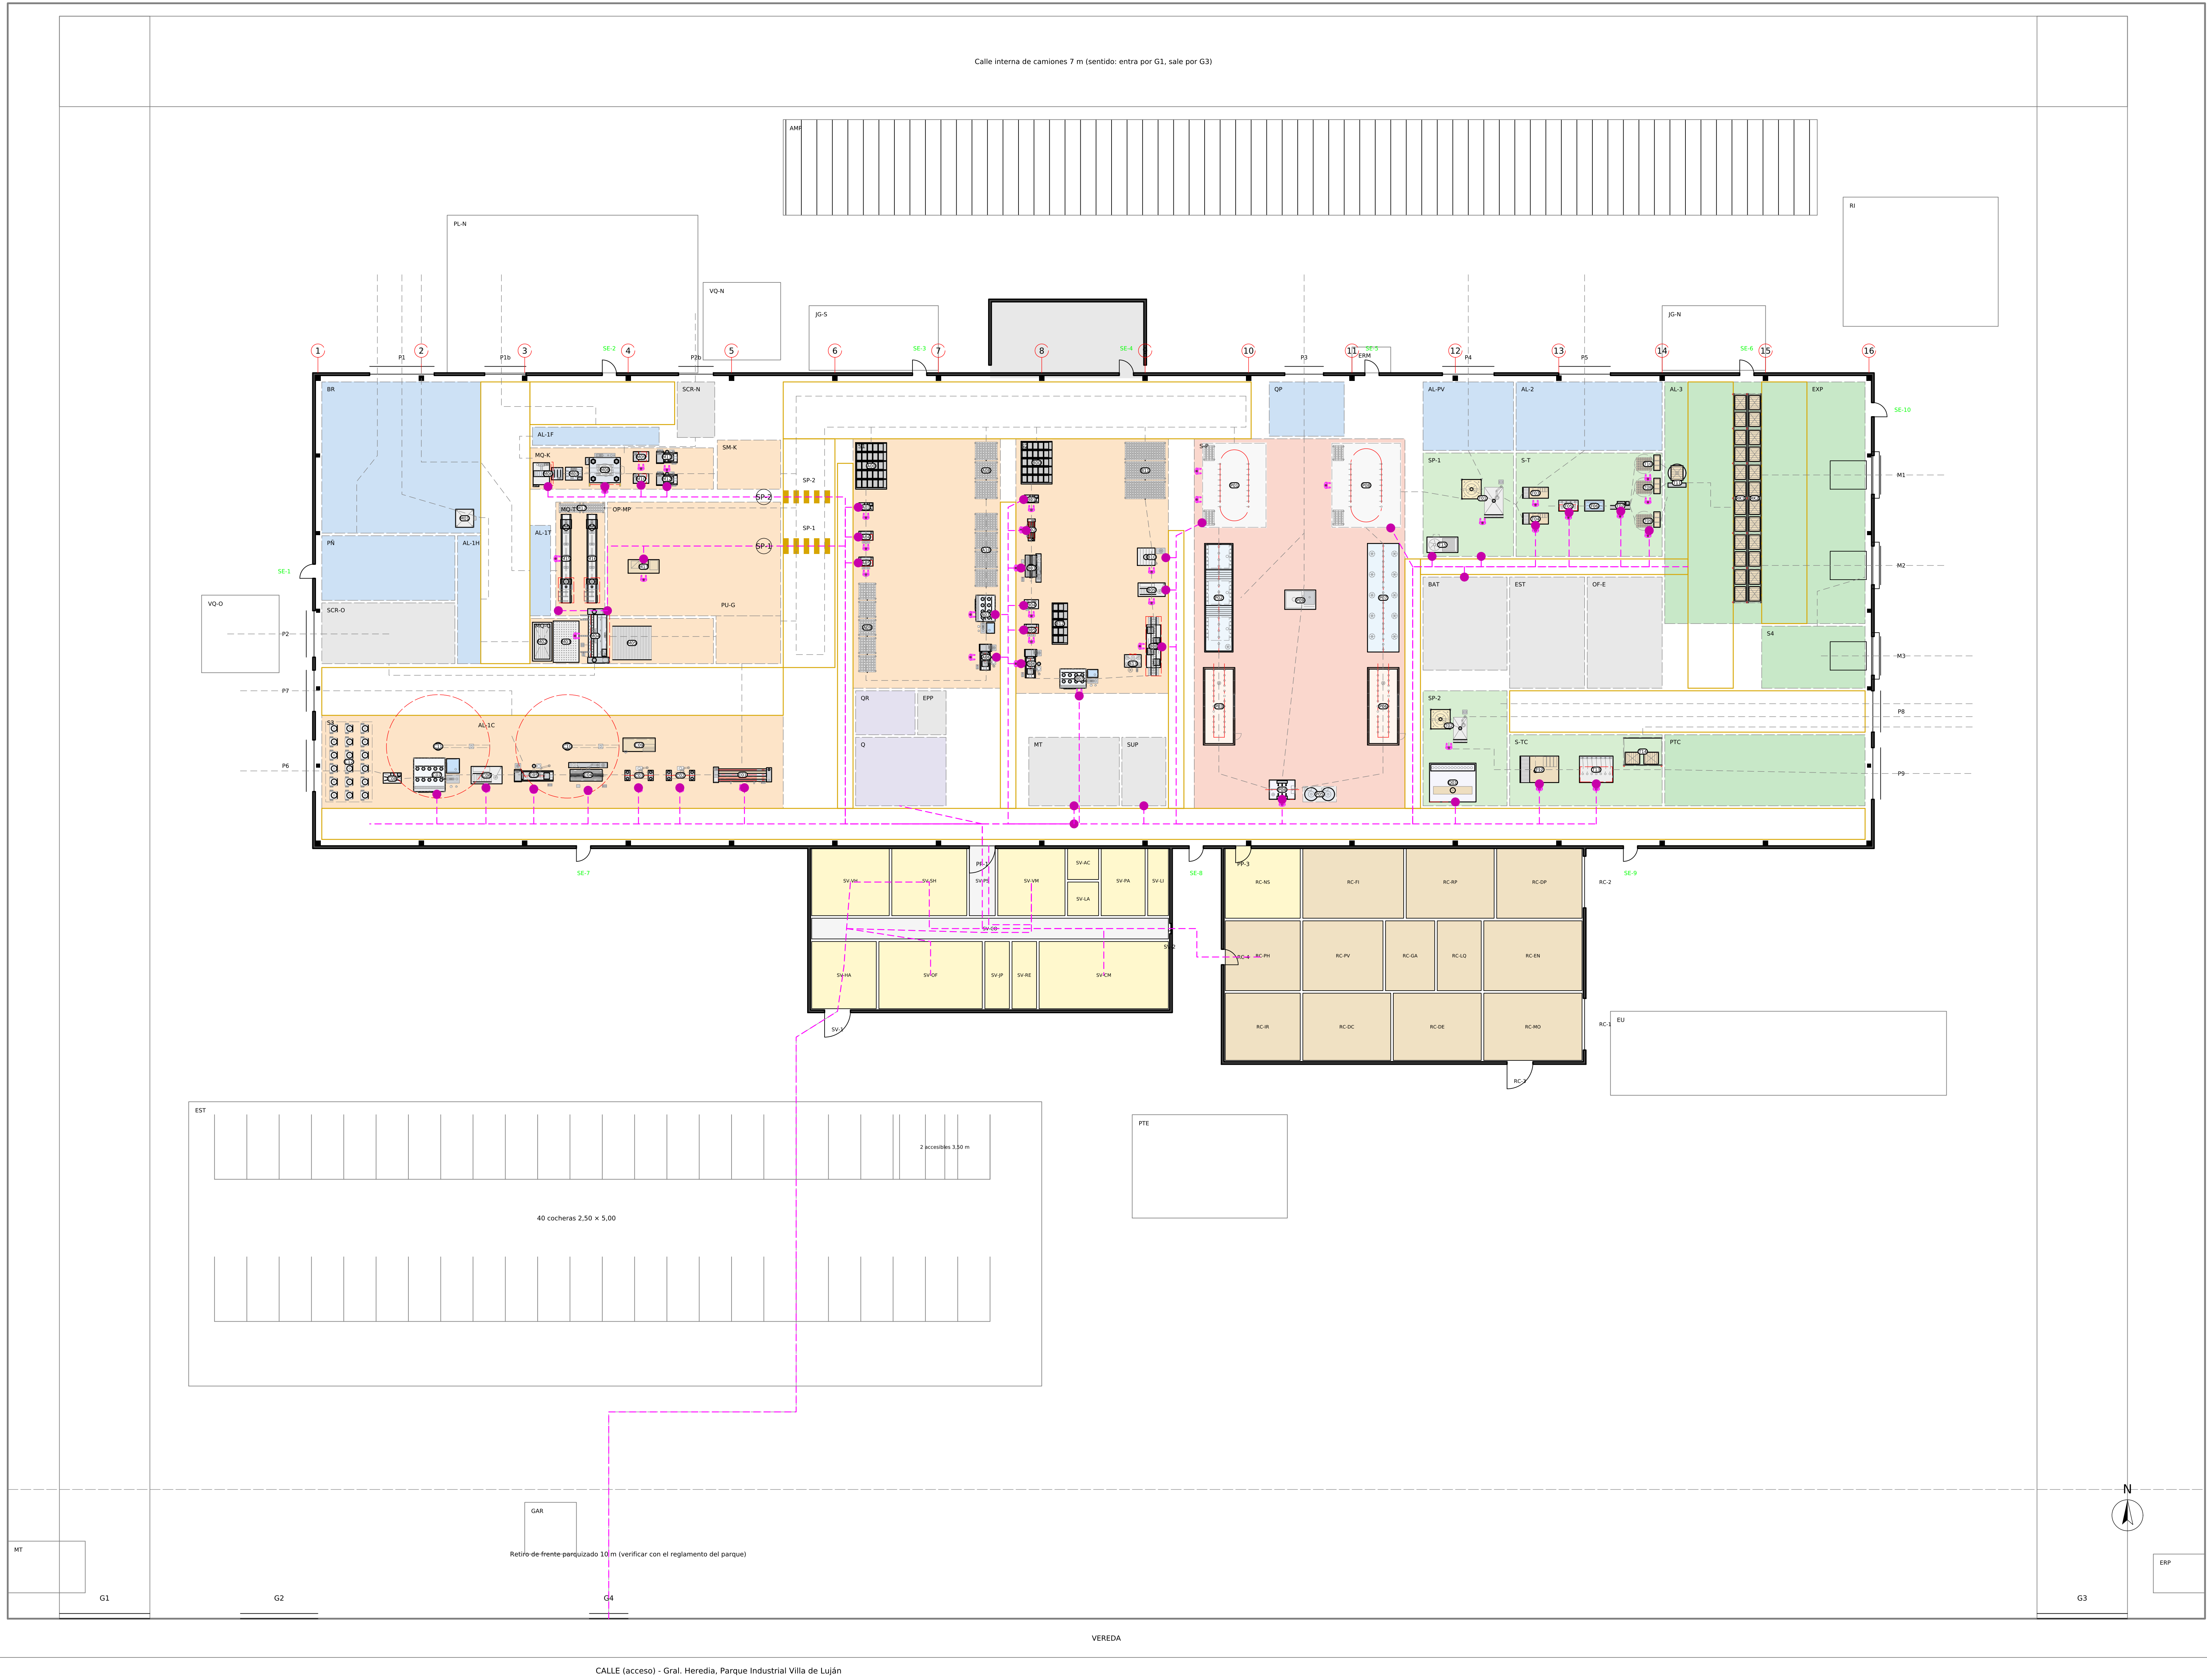

Referencias

- Hilo de personal (magenta, trazos)
- Puesto de trabajo
- Flujos de materiales, de fondo (ver FL_PI_03)
- Senda peatonal señalizada: único cruce de hilo y flujo

Recorrido: estacionamiento -> G4 -> hall y fichado -> vestuario (ropa de calle) -> sanitarios y duchas -> piso a planta PP-1 -> pasillo de personal PP (sur) -> calles de operarios PO -> puesto. Se vuelve por el mismo camino y se pasa por el vestuario (circuito sucio -> limpio). Separación de circulatorios: pasillo de personal PP al sur, contra servicios; pasillo de materiales PM al norte. En las celdas los operarios trabajan del lado de altura de cada horquilla y llegan por las calles PO sin cruzar el recorrido de las piezas. Solo el personal del sector MP cruza el colector del tren logístico, por las sendas SP-1 y SP-2 (demarcación, semáforo y espejo). Cruces de hilos con flujos verificados por cálculo sobre el modelo: 2, ambos en sendas. Recargas: su personal pasa por el pasaje cubierto este (RC-4) y usa el núcleo sanitario este, que también atiende al extremo este de la planta por PP-3. El mostrador tiene puerta propia al estacionamiento: el público no entra a la planta.

Longitud de los hilos (turno mañana)

Hilo (grupo de puestos)	Desde PP-1 (m)	A sanitario (m)
Línea de carros	52	49
Corte y control de recepción	57	52
Presna y cuellos	28	60
Celda 1 kg	36	37
Celda 1 kg y 2.5-10 kg	28	28
PH 2.5-10 kg	15	19
Celda 2.5-10 kg y pintura	38	29
Cabina de pintura	10	6
Descarga de pintura y terminación	61	53
Terminación de carros	17	29
Calidad, mantenimiento y supervisión	20	9
Almacén de PT y expedición	42	56

Puestos con operario en la nave

Sector	Puestos	Operarios
HQ-G Corte de cuerpos (guillotina)	1	1
HQ-T Corte de caño 1 kg	1	1
OP-MP Control de recepción y puestos del sector MP	1	1
HQ-K Cúpulas, fondos y cuellos	3	3
S3 Línea de carros 25-100 kg	7	7
S1 Celda 1 kg	5	5
S2 Celda 2.5-10 kg	10	10
S-P Pintura en polvo 1-10 kg	3	4
SP-1 Sala de carga de polvo 1-10 kg	1	1
S-T Terminación 1-10 kg	7	7
SP-2 Sala de carga de polvo de carros	1	1
S-TC Terminación de carros	2	2
Total de puestos (la DT, con coef. hombre-máquina, da 38 operarios)	43	

Sanitarios (Dec. 351/79 art. 49): 55 H y 6 M en el turno más numeroso

Armario	H req.	M proy.	M req.	M proy.
Inodoros	3	5	1	3
Lavabos	6	8	1	3
Orinales	6	8	0	0
Duchas	3	4	1	2
Armarios (art. 50)	56	62	7	14
Sanitario accesible	-	2	-	unisex

Turno mañana: 53 personas + 8 choferes que inician y terminan en planta; 10 % mujeres (DT 2035). Dos núcleos para repartir la planta en forma equitativa: principal (servicios, junto a PP-1) y este (sala de recargas, PP-3, sala uno con H, M y sanitario accesible (Ley 24.314, Dec. 914/97). Vestuario de mujeres al 20 % de la dotación para no condicionar la incorporación de personal femenino. Lactario (Ley 26.873) y primeros auxilios en servicios. Espacio de cuidado (Dec. 144/2022); no obligatorio con menos de 100 personas (dotación 71).

	Fecha	Nombre	Propietario	Reemplaza a / Reemplazado por
Dibujó	02/10/26	Claude Code	FLAMA S.A.	-
Revisó			Denominación	Material
Aprobó				
Escala	Método de proyección			Edición
1:200	ISO E			0
Unidades	Recorrido del personal - año 10			Fecha de emisión
Cotas en m	Formato			1 / 1
	A0			es
	Tipo de documento			Nº de plano
	Diagrama de recorrido			FL_PI_01