


FL\_PI\_02 - FLUJO DE OPERACIONES Y PROCESOS POR SECCIÓN

Planta Industrial FLAMA S.A. - Parque Industrial Villa de Luján, Sarandí (Avellaneda) - dimensionada al año 10 (2035). Escala 1:200. Norte arriba; la calle de acceso está al sur.

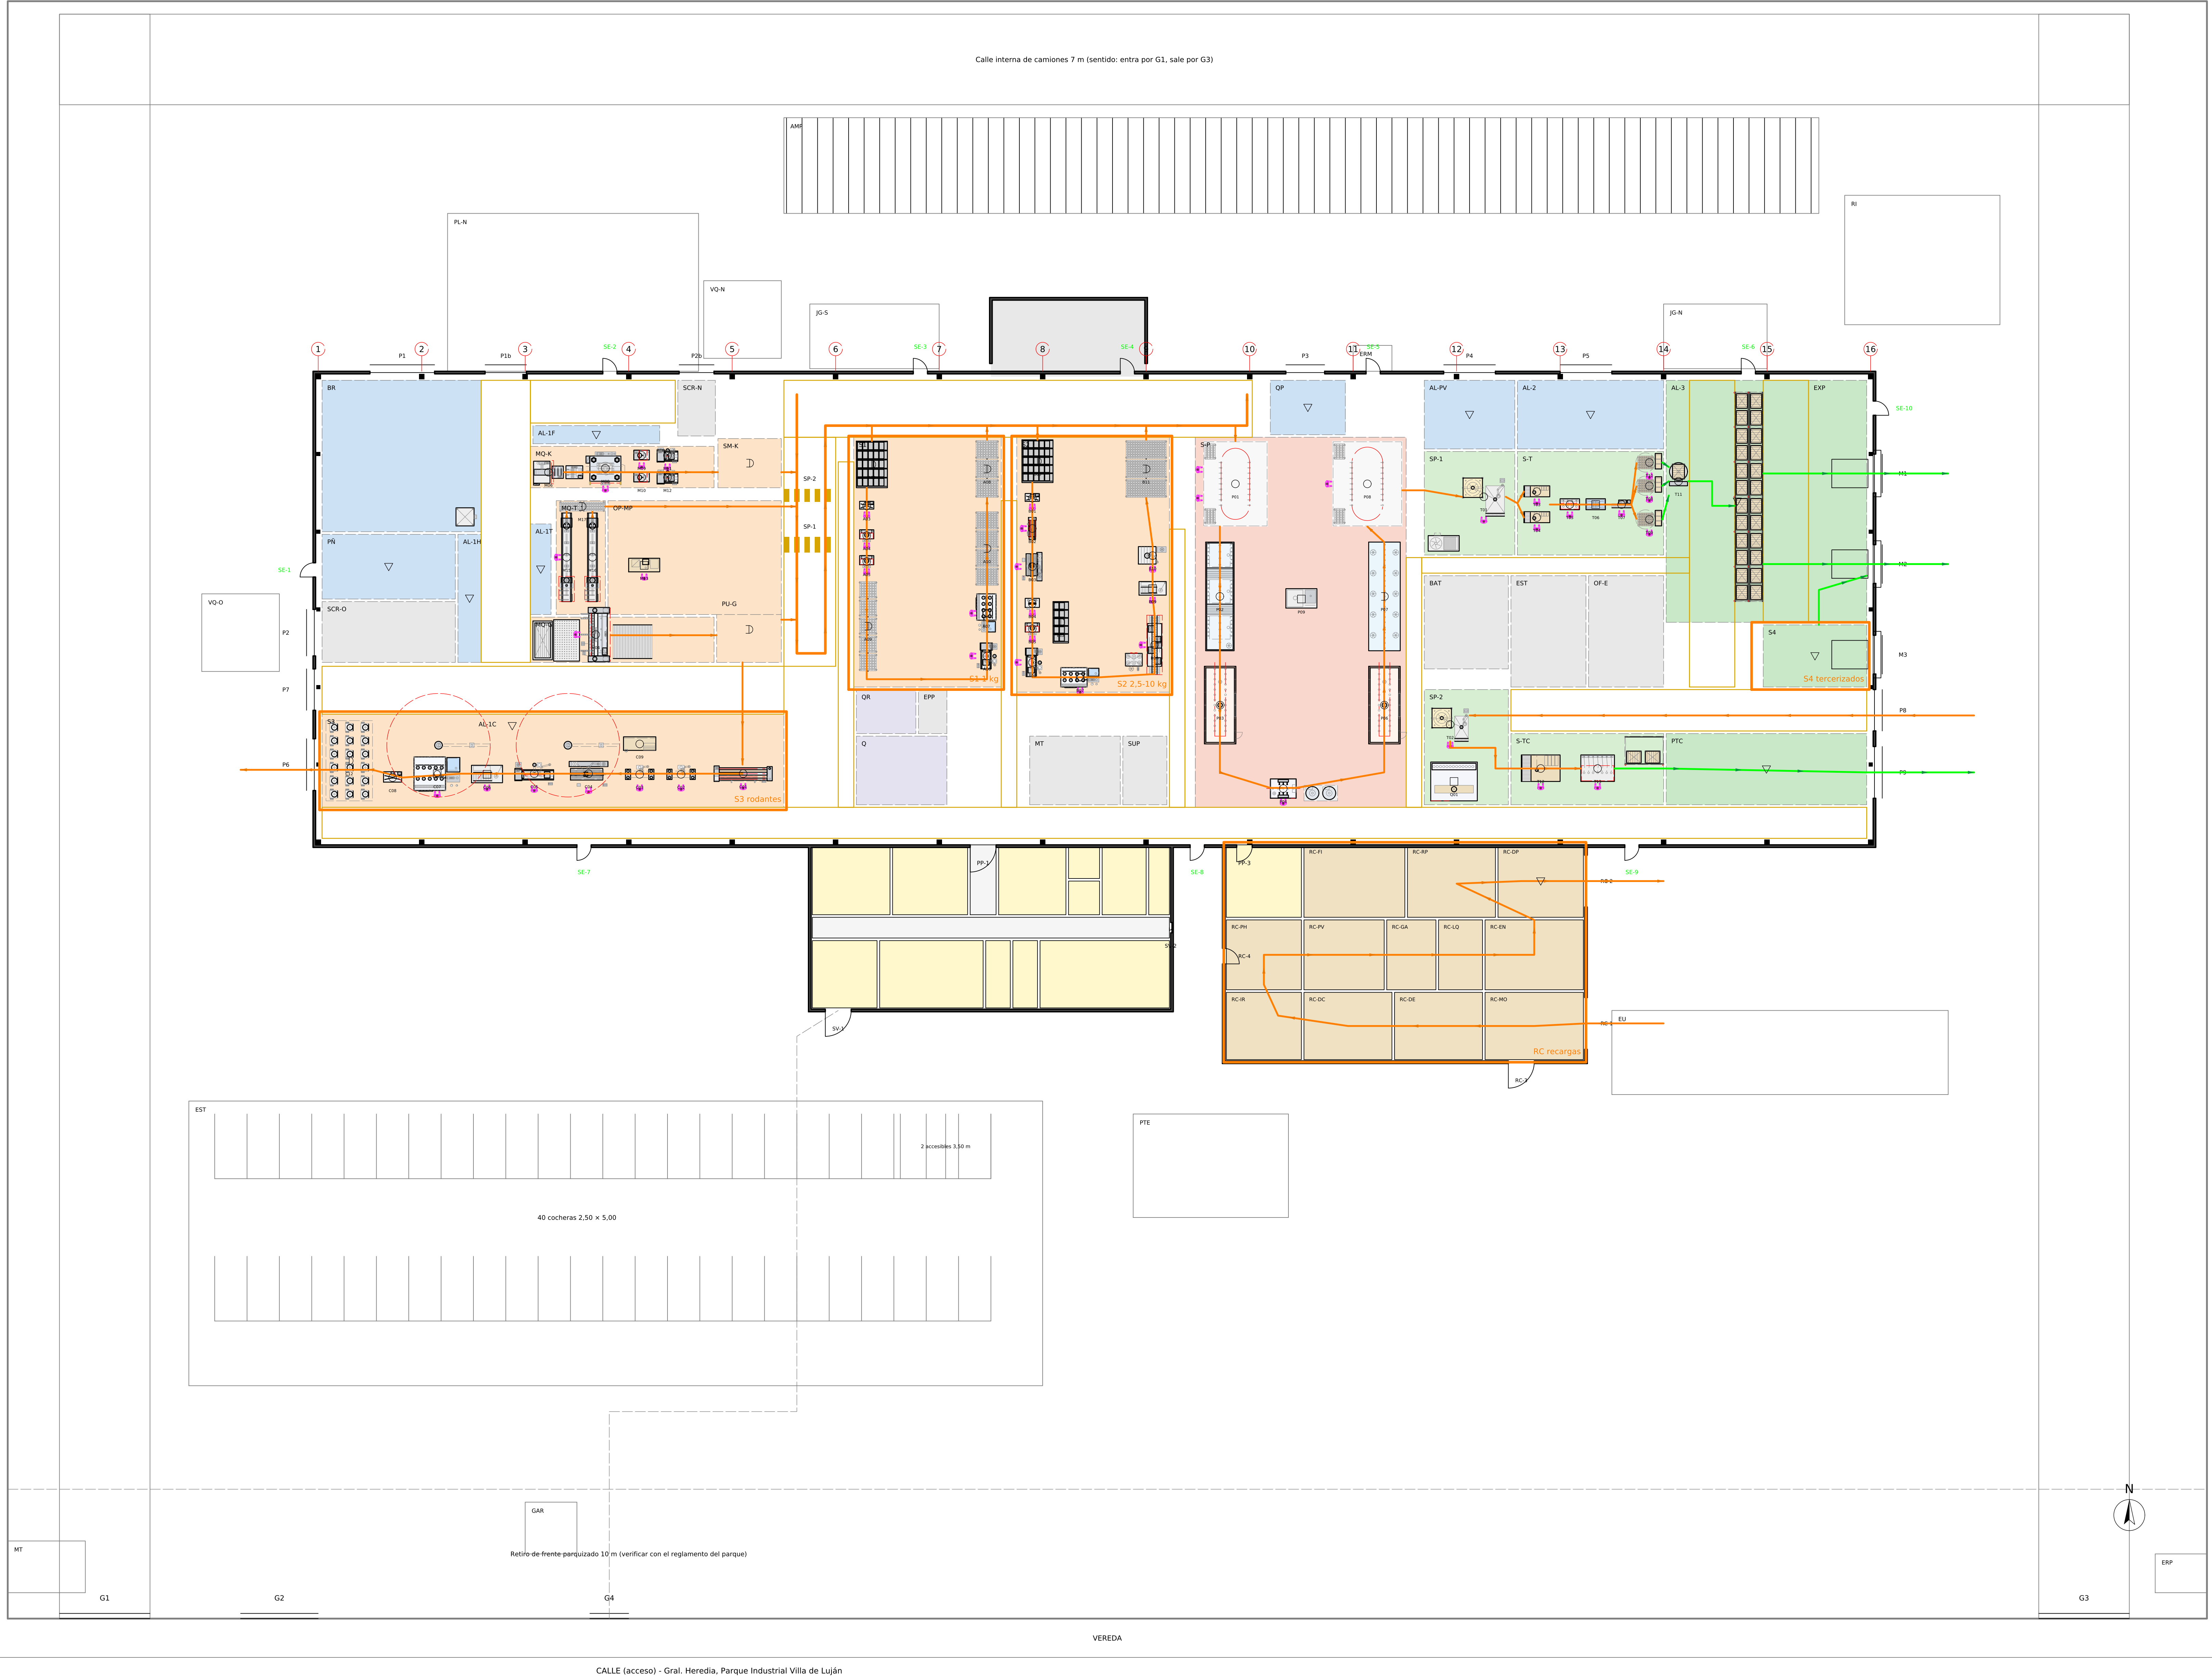

Símbolos (ASME)

- Operación
- Inspección / control
- Operación e inspección combinadas
- Transporte (tren logístico, autoelevador, carro)
- Demora: pulmón o supermercado
- Almacenamiento

Flujos

- SE: semielaborado (naranja)
- Tren logístico de un sentido (SE)
- PT: producto terminado (verde)

| S1 - Matafuegos ABC 1 kg (fabricados) |         | Subconjunto cúpulas y fondos 1-10 kg |         | S2 - Matafuegos ABC 2,5 / 5 / 10 kg |         |
|---------------------------------------|---------|--------------------------------------|---------|-------------------------------------|---------|
| Paso                                  | Dónde   | Paso                                 | Dónde   | Paso                                | Dónde   |
| ✓ Corte en cartón                     | AL-1F   | ✓ Hoja LAF                           | AL-3F   | ✓ Hoja LAF                          | AL-3H   |
| ○ Corte de caño láser                 | M15,M16 | ○ Desdoblado y enderezado            | M06     | ○ Corte de cuerpo                   | M04     |
| ⌈ Pulmón                              | M17     | ○ Corte y embudo                     | M08     | ⌈ Pulmón                            | PU-G    |
| ➡ Tren logístico                      | PM      | ○ Preparación de cuello              | M09,M10 | ➡ Tren logístico                    | PM      |
| ⌈ Kanban                              | A00     | ⌈ Soldadura de cuello                | M11,M12 | ⌈ Supermercado                      | B00     |
| ○ Numerado                            | A03     | ⌈ Supermercado                       | SA-K    | ○ Numerado                          | B01     |
| ○ Encastre de fondo                   | A04     | ➡ Tren logístico a A04/A05 y B05     | PM      | ○ Cilindrado                        | B02     |
| ○ Encastre de cúpula con cuello       | A05     |                                      |         | ○ Soldadura longitudinal            | B03     |
| ⌈ Pulmón                              | A09     |                                      |         | ○ Bordonado                         | B04     |
| ○ Soldadura circumferencial           | A06     |                                      |         | ○ Encastre de fondo y cúpula        | B05     |
| ⌈ Prueba hidráulica 100 %             | A07     |                                      |         | ○ Soldadura circumferencial         | B06     |
| ⌈ Pulmón a pintura                    | A08     |                                      |         | ⌈ Prueba hidráulica 100 %           | B07     |
| ➡ Tren logístico                      | PM      |                                      |         | ○ Granallado                        | B08     |
| ○ Pintado                             | P02     |                                      |         | ○ Detección de defectos             | B09     |
| ○ Secado                              | P03     |                                      |         | ○ Corrección                        | B10     |
| ○ Pintura en polvo                    | P04     |                                      |         | ⌈ Pulmón a pintura                  | B11     |
| ○ Pulverizado                         | P06     |                                      |         | ➡ Tren logístico                    | PM      |
| ⌈ Espesor y adherencia                | P09     |                                      |         | ○ Pintura (igual que S1)            | P02-P06 |
| ○ Encamilla                           | T03,T04 |                                      |         | ○ Terminación (igual que S1)        | T01-T11 |
| ○ Presurización con N <sub>2</sub>    | T05     |                                      |         | ⌈ Almacen de PT                     | AL-3    |
| ○ Hermeticidad                        | T06     |                                      |         | ⌈ Expedición                        | M1,M2   |
| ○ Etiquetado                          | T07     |                                      |         |                                     |         |
| ○ Embalaje y palletizado              | T08,T09 |                                      |         |                                     |         |
| ○ Envolvido                           | T11     |                                      |         |                                     |         |
| ⌈ Almacen de PT                       | AL-3    |                                      |         |                                     |         |
| ⌈ Expedición                          | M1,M2   |                                      |         |                                     |         |

| S3 - Matafuegos ABC rodantes 25 / 50 / 70 ... |         | S4 - Tercerizados revendidos (CO <sub>2</sub> , agua, A... |       | RC - Recargas (servicio)              |            |
|-----------------------------------------------|---------|------------------------------------------------------------|-------|---------------------------------------|------------|
| Paso                                          | Dónde   | Paso                                                       | Dónde | Paso                                  | Dónde      |
| ✓ Hojes LAC                                   | AL-1H   | ○ Recepción                                                | H3    | ○ Recepción                           | RC-1       |
| ○ Corte de cuerpo                             | M04     | ⌈ Control de recepción y sello IRAM                        | S4    | ⌈ Clasificación en 4 calas            | RC-1       |
| ⌈ Pulmón                                      | PU-G    | ⌈ Stock                                                    | S4    | ○ Desarme                             | RC-DE      |
| ○ Cilindrado 4 rodillos                       | C01     | ⌈ Expedición con el pedido                                 | M2    | ○ Descarga y ensayo de funcionamiento | RC-DC      |
| ○ Punteo, refuerzo y estructura               | C02,C03 |                                                            |       | ⌈ PH lavado y secado                  | RC-PH      |
| ○ Soldadura longitudinal                      | C04     |                                                            |       | ○ Recarga por familia                 | RC-PVGA/LQ |
| ○ Soldadura circ. (casquetes AL-1C)           | C05     |                                                            |       | ○ Ensamblado y presurización          | RC-EN      |
| ○ Inspección de costuras                      | C06     |                                                            |       | ○ Peso y hermeticidad                 | RC-EN      |
| ⌈ Prueba hidráulica 4,0 MPa                   | C07     |                                                            |       | ○ Retoque y etiquetado                | RC-EP      |
| ○ Marcado                                     | C08     |                                                            |       | ⌈ Para entregar                       | RC-EP      |
| ○ Espera de retiro                            | C12     |                                                            |       | ⌈ Despacho                            | RC-2       |
| ⌈ Pintura terciada (P6 -> P8)                 | -       |                                                            |       |                                       |            |
| ○ Carga de polvo                              | T02     |                                                            |       |                                       |            |
| ○ Armado de ruedas y manguera                 | T12     |                                                            |       |                                       |            |
| ○ Presurización y etiquetado                  | T13     |                                                            |       |                                       |            |
| ⌈ Carros terminados                           | PTC     |                                                            |       |                                       |            |
| ⌈ Expedición                                  | P9      |                                                            |       |                                       |            |

| Fecha                                         | Nombre               | Propietario          | Reemplaza a / Reemplazado por |
|-----------------------------------------------|----------------------|----------------------|-------------------------------|
| 02/10/26                                      | Claude Code          | FLAMA S.A.           | -                             |
| Revisó                                        | Aprobó               | Denominación         | Material                      |
|                                               |                      | Flujo de operaciones | -                             |
| Escala                                        | Método de proyección | Flujo de operaciones |                               |
| 1:200                                         | ISO E                |                      |                               |
| Unidades                                      | Formato              | Diagrama de proceso  |                               |
| Cotas en m                                    | A0                   |                      |                               |
| Secuencia de operaciones por sección - año 10 |                      | Edición              |                               |
|                                               |                      | 0                    |                               |
|                                               |                      | Fecha de emisión     |                               |
|                                               |                      | 02/10/2026           |                               |
|                                               |                      | Hoja                 |                               |
|                                               |                      | 1 / 1                |                               |
|                                               |                      | es                   |                               |
|                                               |                      | Nº de plano          |                               |
|                                               |                      | FL_PI_02             |                               |