


Planta industrial FLAMA S.A. - Parque Industrial Villa de Luján, Sarandí (Avellaneda) - dimensionada al año 10 (2035). Escala 1:200. Norte arriba; la calle de acceso está al sur.

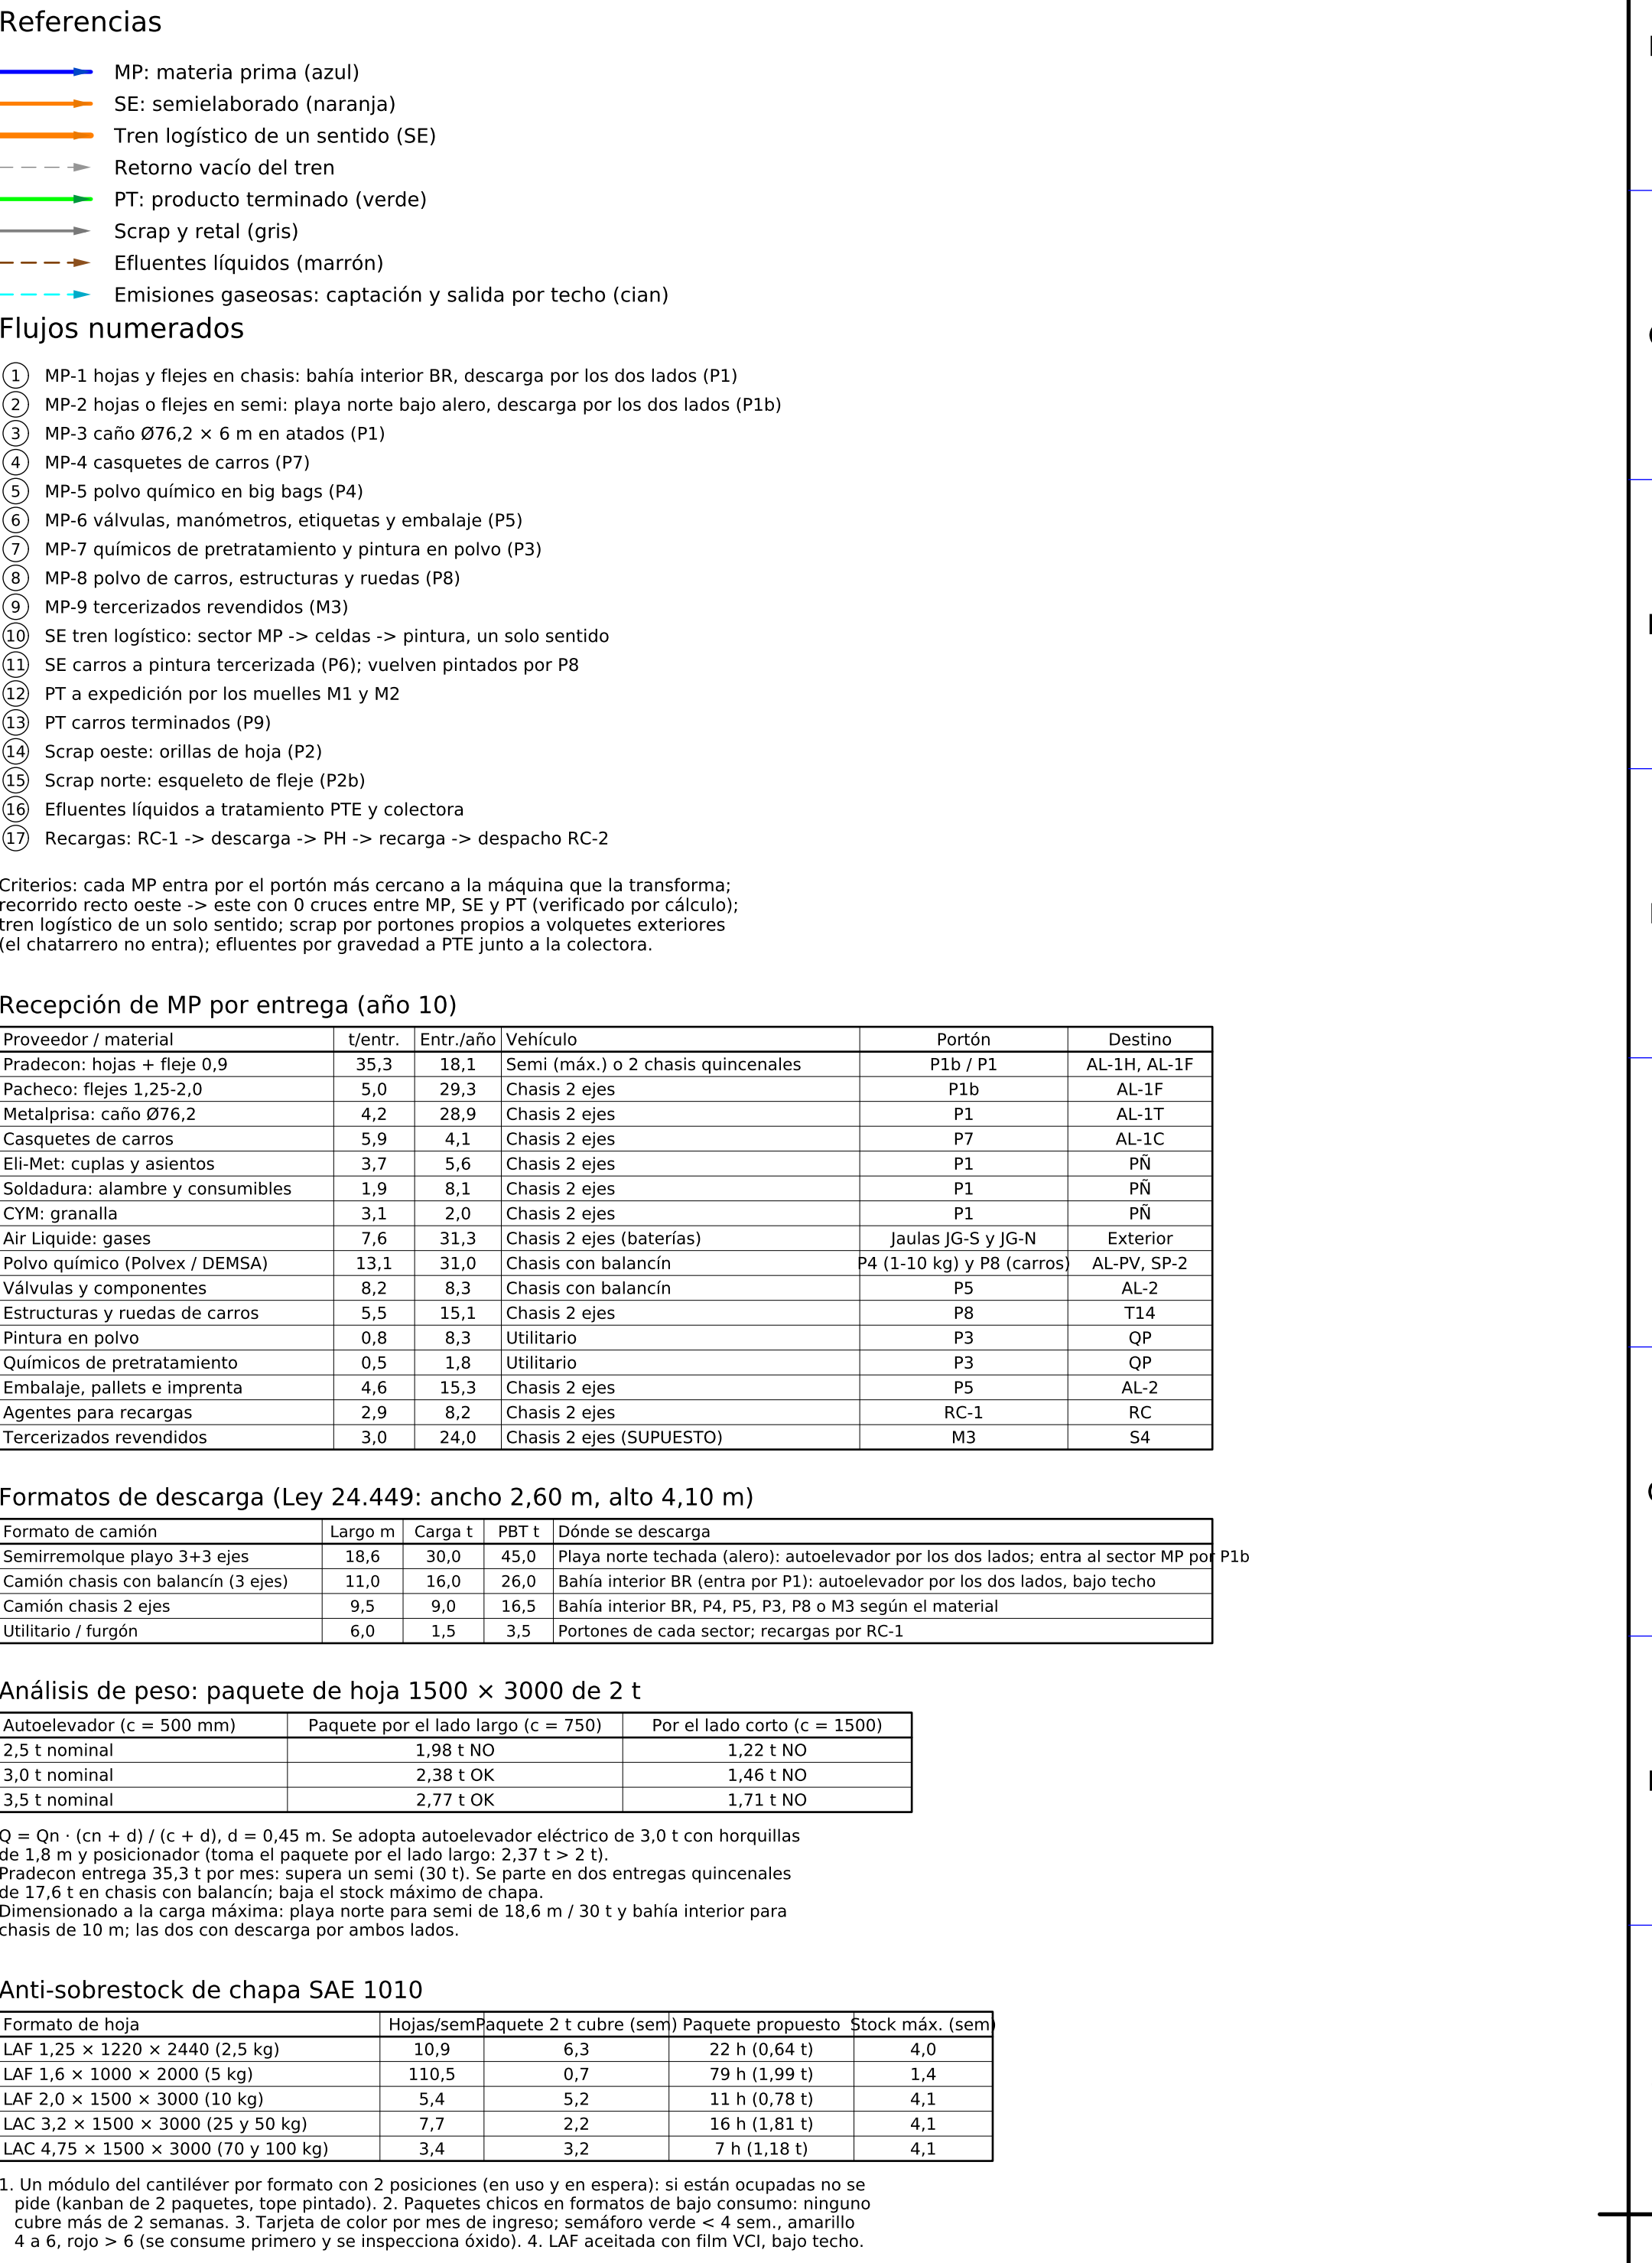


	Fecha	Nombre	Propietario	Reemplaza a / Reemplazado por
Dibujó	02/10/2016	Claude Code	FLAMA S.A.	Material

Aprobó		Escala		Método de proyección		Edición		Fecha de emisión	
1:200				ISO E		0		02/10/2026	
Unidades		Formato		Flujo de materiales		Hoja		Idioma	
				MP, SE, PT, scrap y efluentes - año 10		1 / 2		es	

19 20 21 22 23 24

FL_PI_03 - REDES: ELECTRICIDAD, AIRE, GASES Y EFLUENTES

Planta Industrial FLAMA S.A. - Parque Industrial Villa de Luján, Sarandí (Avellaneda) - dimensionada al año 10 (2035). Escala 1:200. Norte arriba; la calle de acceso está al sur.

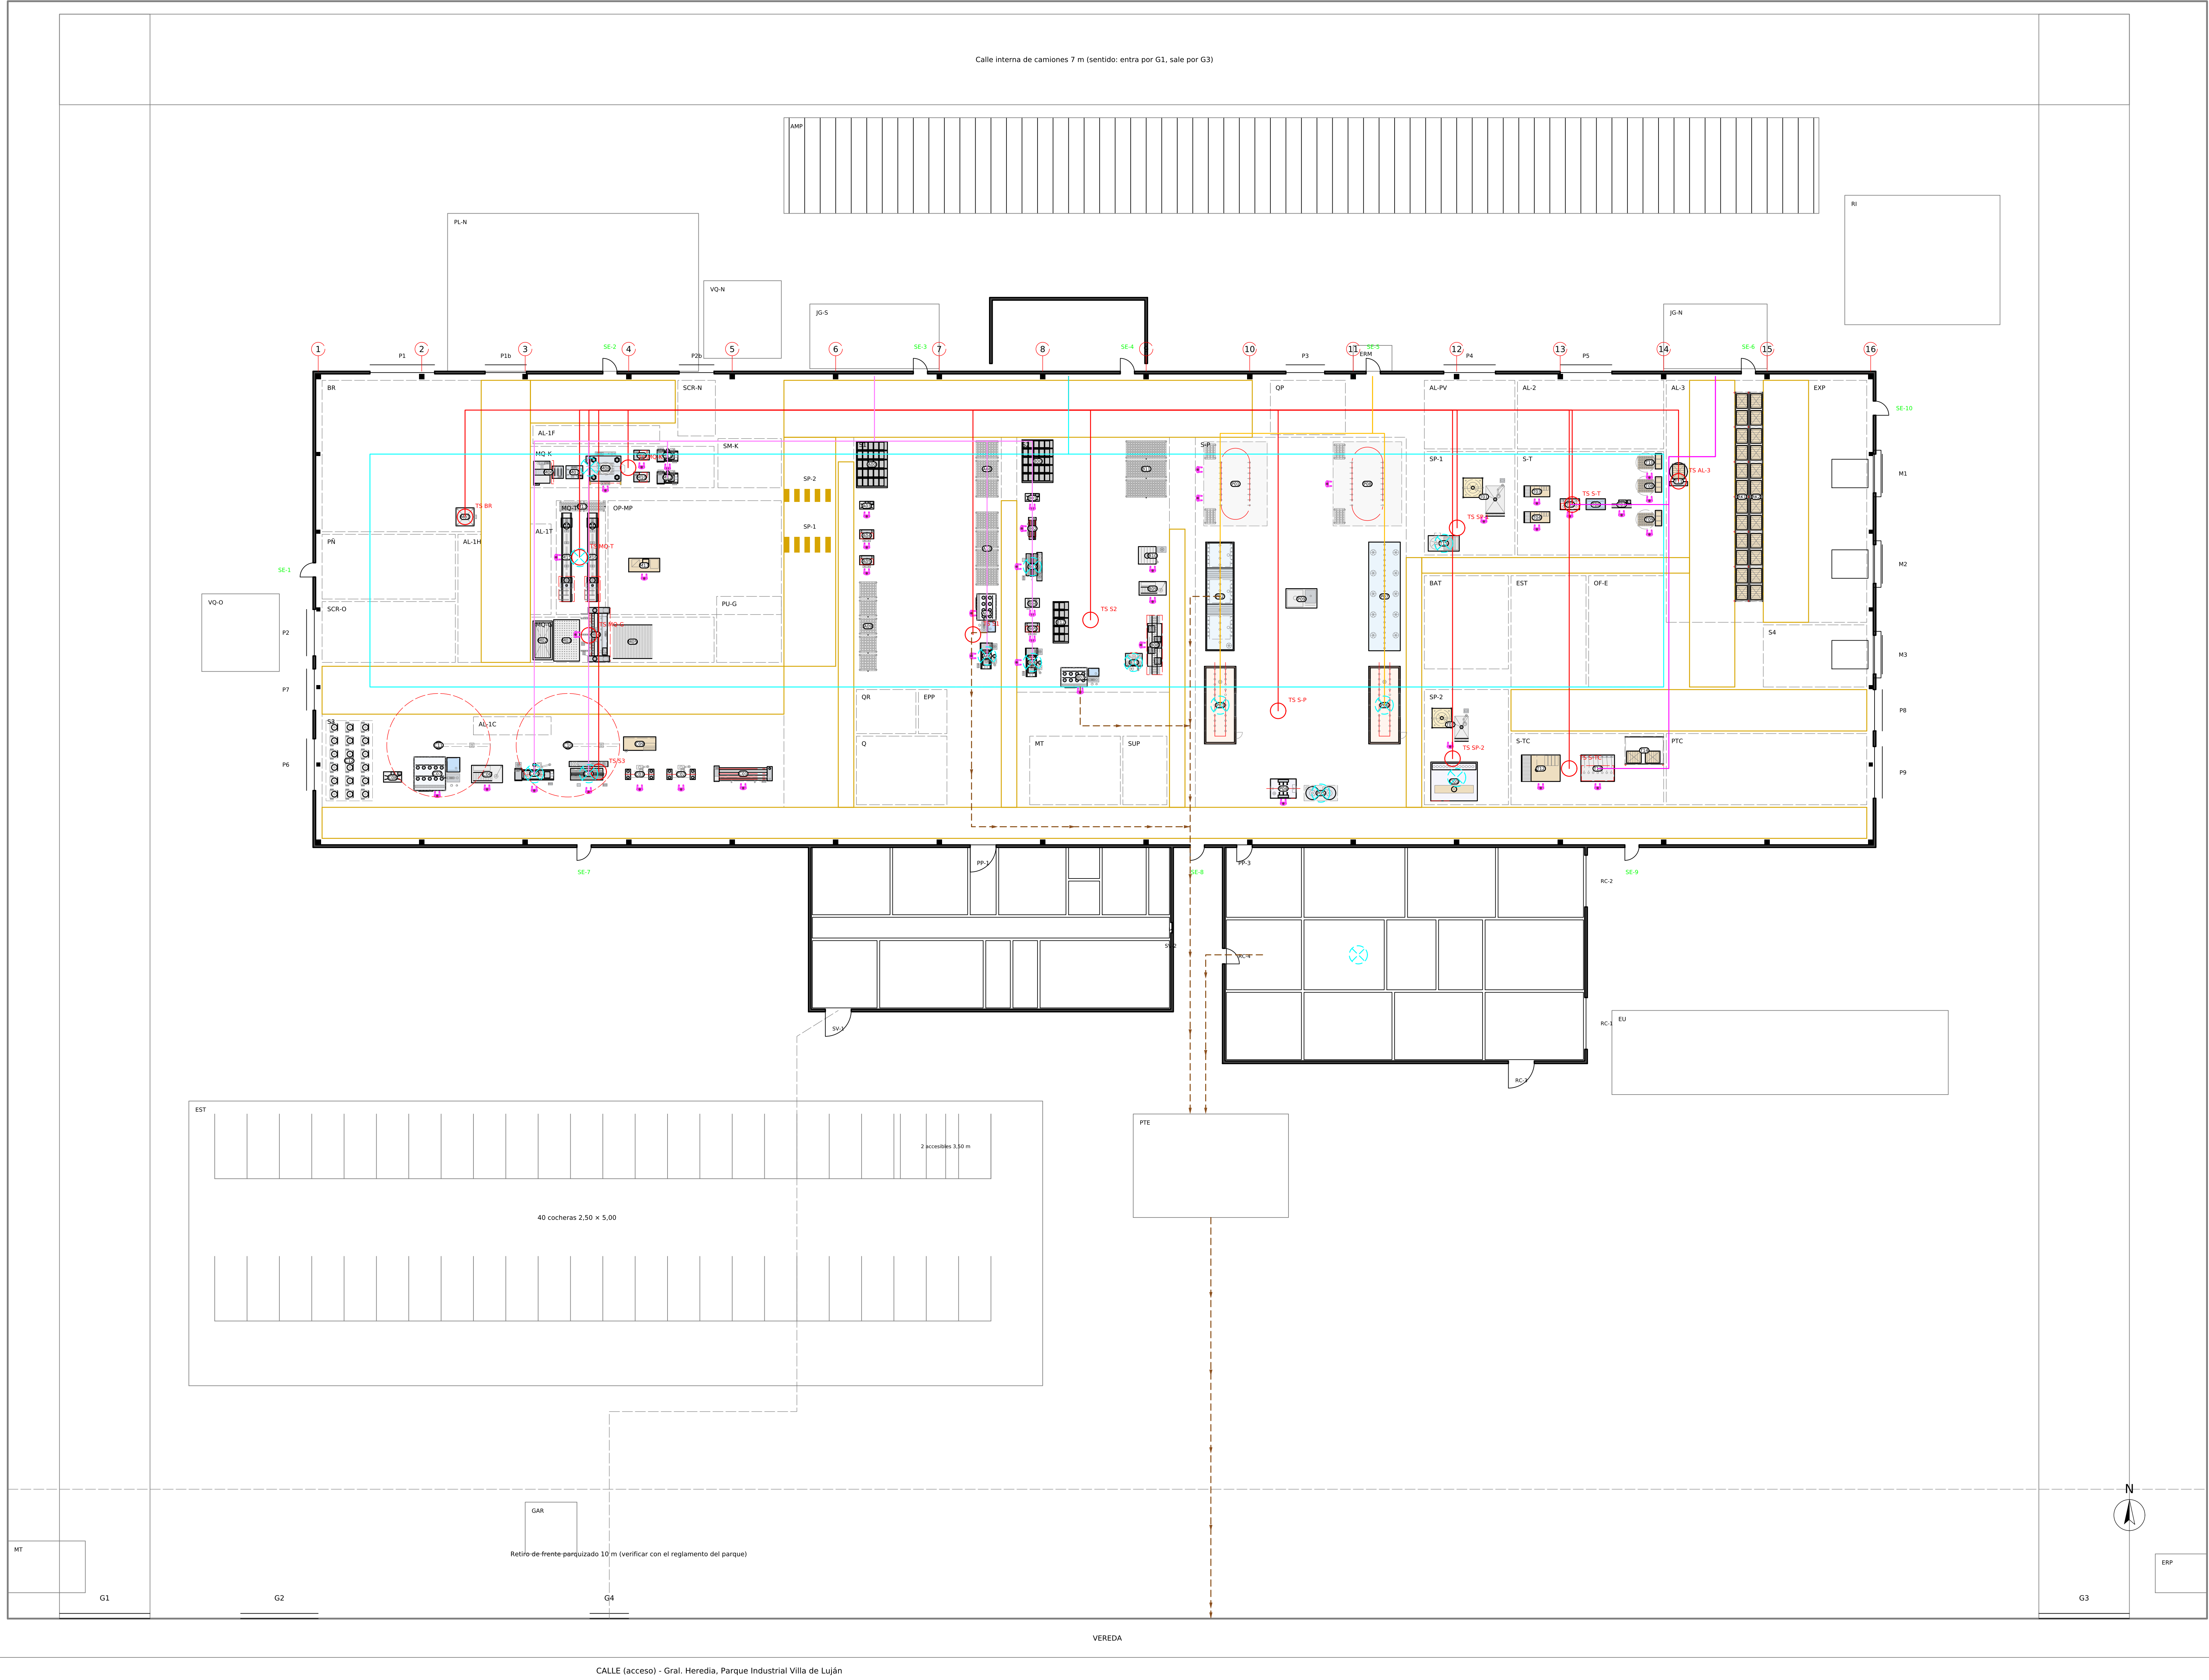

Referencias

- Alimentador eléctrico TGBT -> tablero seccional (TS)
- Aire comprimido: anillo con bajadas FRL cada 8 m
- Gas de soldadura Ar/CO₂ (ARCAL 21) desde la jaula JG-S
- Nitrógeno para presurización desde la jaula JG-N
- Gas natural a los hornos desde la regulación ERM
- Efluentes líquidos a PTE (enterrado, por gravedad)
- Captación localizada y salida por techo

Criterio 4 (minimizar tendidos): la sala técnica ST (transformador, TGBT y compresores) está en el centro de cargas, sobre la fachada norte; las jaulas de gases, junto a sus consumos; la PTE, al sur junto a la colectora. Los procesos con efluente líquido (PH, pretratamiento y lavado de recargas) quedan en una franja central de 20 m de ancho para acortar la cañería enterrada. Recargas tiene tableros propios, manifold de N₂ y cámara de decantación. Potencia instalada de equipos: 311 kW, con simultaneidad 0,6 -> transformador de 215 xVA (verificar con el relevamiento de cargas definitivo).

Alimentadores (recorrido ortogonal)

Tablero seccional	kW	Largo desde TGBT m
BR	0,1	37,5
MQ-G	17,2	57,1
MQ-T	20,0	51,8
MQ-K	45,0	41,1
S3	69,5	66,9
S1	21,5	27,3
S2	66,1	20,5
S-P	33,0	42,0
SP-1	9,0	41,7
S-T	2,5	48,8
AL-3	1,5	55,3
SP-2	5,0	59,2
S-TC	1,0	69,0
Total	311,4	638,3

Agua de PH y pretratamiento a PTE

Punto	Largo m
A07	36,1
B07	43,9
P02	40,7
Total	140,6

Gas natural a hornos

Punto	Largo m
P03	37,2
P06	26,3
Total	63,5

Nitrógeno

Punto	Largo m
T05	21,1
T13	39,4
Total	60,6

Gas de soldadura

Punto	Largo m
M11	22,1
M12	23,8
C04	52,8
C05	57,0
A06	30,3
B03	26,9
B06	34,3
Total	247,2

Anillo de aire comprimido: 292 m.

Compresor a tornillo, tanque pulmón y secador frigorífico en ST.
N₂: manifold con conmutación automática, regulador y detector de fugas.

Fecha	Nombre	Propietario	Reemplaza a / Reemplazado por
02/10/2026	Claude Code	FLAMA S.A.	-
Revisó		Denominación	Material
Aprobó			
Escala	Método de proyección	Redes e instalaciones	
1:200	ISO E	Tendidos mínimos desde la sala técnica	
Cotas en m	Formato	Tipo de documento	
A0	A0	Plano de instalaciones	
Edición			Nº de plano
0			FL_PI_03
Fecha de emisión			
02/10/2026			
Hoja			
2 / 2			
Formato			
ISO E			