# FL_PI_03 – PERSONAL, EVACUACIÓN Y SEÑALIZACIÓN

Planta industrial FLAMA S.A. – Parque Industrial Villa de Luján, Sarandí (Avellaneda) – dimensionada al año 10 (2035). Escala 1:200. Norte arriba; la calle de acceso está al sur.

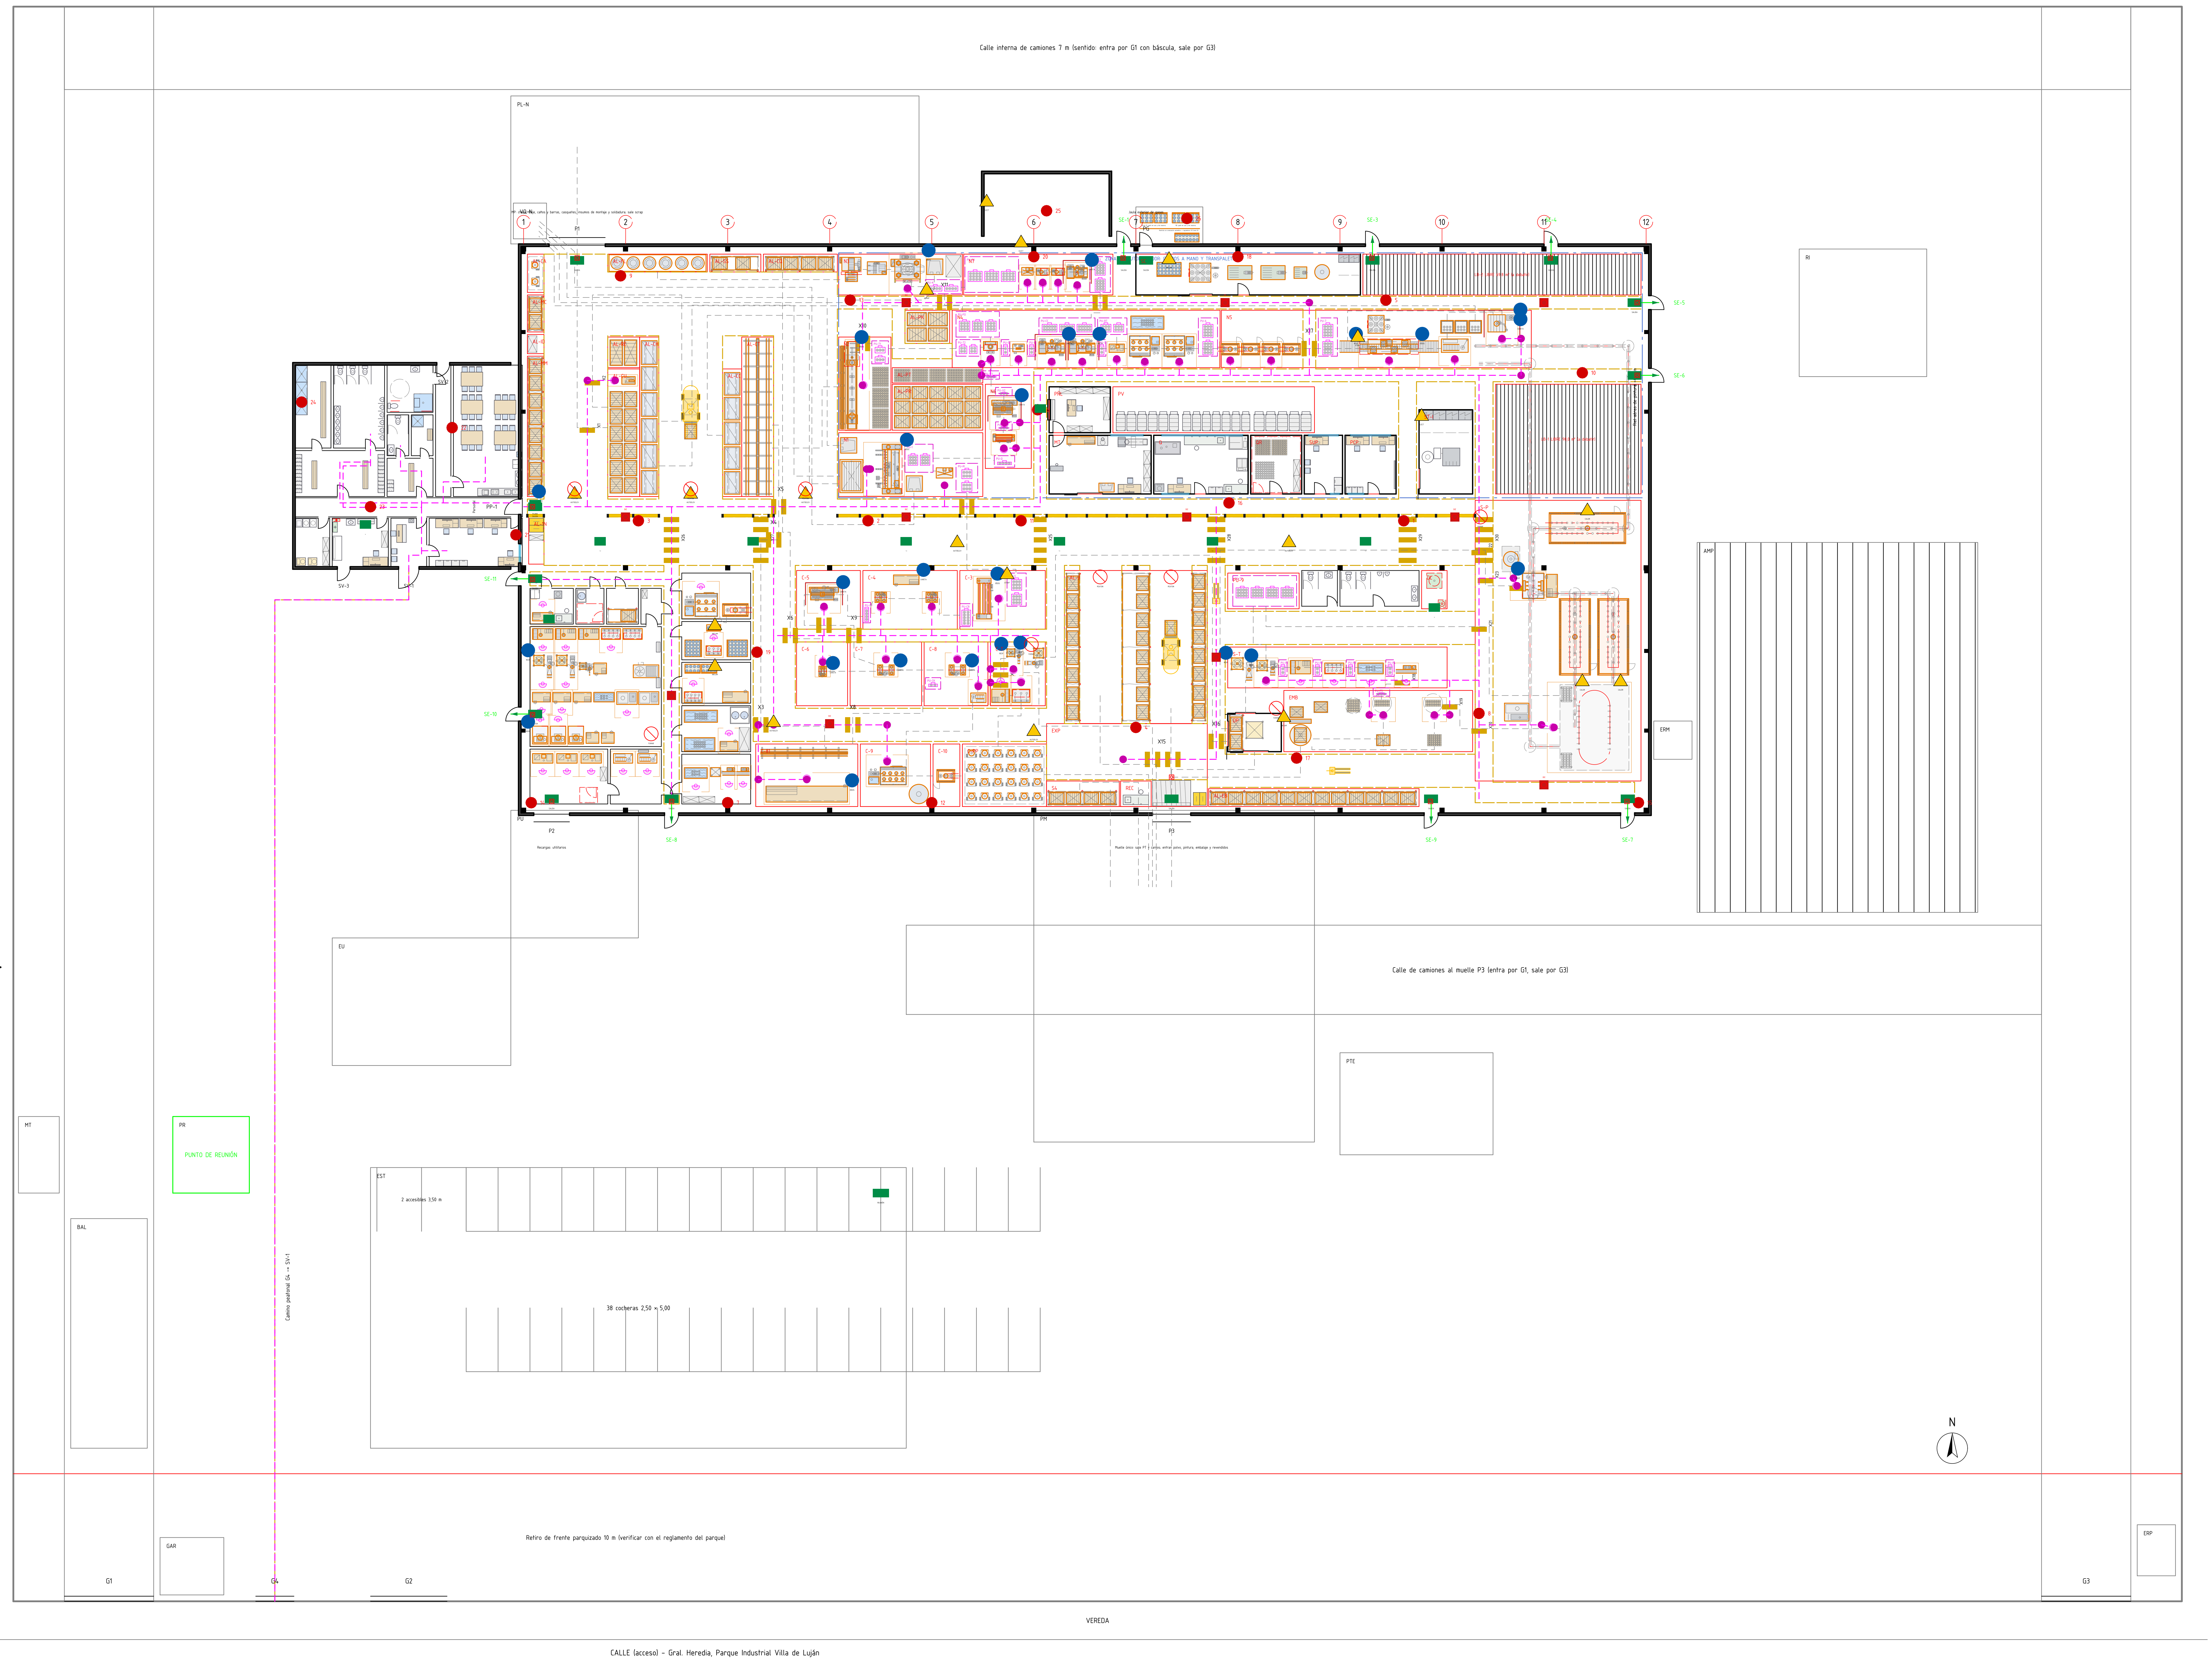
Calle interna de camiones 7 m (sentido: entra por G1 con báscula, sale por G3)
PL-N
1
2
3
4
5
6
7
8
9
10
11
12
P1
PG
SE-1
SE-3
SE-4
SE-5
AMP
P2
P3
EU
Calle de camiones al muelle P3 (entra por G1, sale por G3)
PTE
MT
PR
PUNTO DE REUNIÓN
BAL
EST
2 accesibles 3,50 m
38 cocheras 2,50 × 5,00
Camino peatonal G4 → SV-1
GAR
G1
G4
G2
G3
ERP
N
Retiro de frente parquizado 10 m (verificar con el reglamento del parque)
VEREDA
CALLE (acceso) – Gral. Heredia, Parque Industrial Villa de Luján

## Referencias

Hilo de personal (DIR) y puesto de trabajo

X1..: senda peatonal (cebra) donde un hilo cruza un flujo

Punto rojo numerado: extintor ABC 10 kg    BIE: boca de incendio equipada    ☐: pulsador de alarma

## Señales (IRAM 10005-1: formas y colores de seguridad)

- Advertencia · ATRAP: Riesgo de atrapamiento / cargas suspendidas
- Advertencia · AUTOELEV: Circulación de autoelevadores
- Advertencia · CALOR: Superficie caliente (hornos)
- Advertencia · ELECT: Riesgo eléctrico
- Advertencia · INFLAM: Gases a presión
- Obligación · CALZADO: Calzado de seguridad y ropa de trabajo (ingreso a planta)
- Obligación · CARETA: Careta fotosensible y guantes
- Obligación · OÍDOS: Protección auditiva
- Obligación · RESP: Respirador P2
- Prohibición · FUMAR: Prohibido fumar y llama abierta
- Prohibición · PEATON: Prohibido el paso de peatones (calle de autoelevador)
- Salvamento y evacuación · +: Primeros auxilios / lavaojos
- Salvamento y evacuación · ->: Recorrido de evacuación
- Salvamento y evacuación · PLANO: Plano de evacuación (ingreso PP-1)
- Salvamento y evacuación · REUNIÓN: Punto de reunión
- Salvamento y evacuación · SALIDA: Salida

## Evacuación y protección contra incendio

| Medios de escape (Dec. 351/79 anexo VII) | Valor |
|---|---|
| Recorrido máximo real a una salida (grilla 0,5 m, tabiques y equipos) | 36,9 m ≤ 40 |
| Ocupación (16 m² por persona en la nave) | 242 personas |
| Unidades de ancho de salida / ancho mínimo | 3 / 1,55 m |
| Salidas de emergencia de 1,10 m con barral antipánico | 10 |
| Extintores ABC 10 kg (1 cada 200 m², recorrido ≤ 20 m) | 26 |
| Bocas de incendio equipadas / pulsadores de alarma | 11 / 14 |
| Sanitario accesible con ducha (bloque de servicios) | 1 |

## Longitud de los hilos

| Hilo (grupo de puestos) | Desde PP-1 (m) |
|---|---|
| Recepción, corte de chapa y marcado (N1) | 46 |
| Cuerpo, unión y PH (N4, N6) | 33 |
| Secado, granallado y detección (N5) | 37 |
| Láser, embutido y celda de cuello (N2, N3, N7) | 41 |
| Pintura, terminación y embalaje | 40 |
| PT y expedición | 27 |
| Línea de carros (S3) | 40 |
| Recargas (RC) | 34 |

## Sanitarios de vestuarios (art. 49): 55 H y 6 M

| Artefacto | H req. | H proy. | M req. | M proy. |
|---|---|---|---|---|
| Inodoros | 3 | 3 | 1 | 1 |
| Lavabos | 6 | 6 | 1 | 1 |
| Orinales | 6 | 6 | 0 | 0 |
| Duchas | 3 | 3 | 1 | 1 |
| Armarios (art. 50) | 56 | 60 | 7 | 9 |

Además: sanitarios de planta (banda sur, calle AT2) de hombres (2 inodoros, 2 mingitorios, 2 lavabos) y de mujeres (1 + 1), a < 25 m de pintura, terminación, embalaje y PT. Lockers: 1 por empleado. Cada operario tiene 1,0 m libre detrás de su puesto: ninguna calle ni material ajeno pasa por su espalda (verificado). Mamparas ignífugas en todos los puestos de soldadura.

| | Fecha | Nombre |
|---|---|---|
| Dibujó | 14/10/26 | Claude Code |
| Revisó | | |
| Aprobó | | |

Escala
1:200

Método de proyección
ISO E

Unidades
Cotas en m

Formato
A0

Propietario
FLAMA S.A.

Denominación
Personal y seguridad
DIR, medios de escape, protección contra incendio, IRAM 10005

Tipo de documento
Plano de seguridad e higiene

Reemplaza a / Reemplazado por
–

Material
–

Edición
0

Fecha de emisión
14/10/2026

Hoja
1 / 1

Idioma
es

N° de plano
FL_PI_03