

FL_PI_05 - SERVICIOS AL PERSONAL, OFICINAS Y APOYO A LA LÍNEA

Todo en planta baja (sin entrepiso). Circuito del personal, vestuarios con 1 locker por empleado y sanitarios (Dec. 351/79 arts. 49-50), accesibilidad (Ley 24.314), supervisor y PCP sobre la línea.


DETALLE 1 - SERVICIOS Y ADMINISTRACIÓN - 1:50

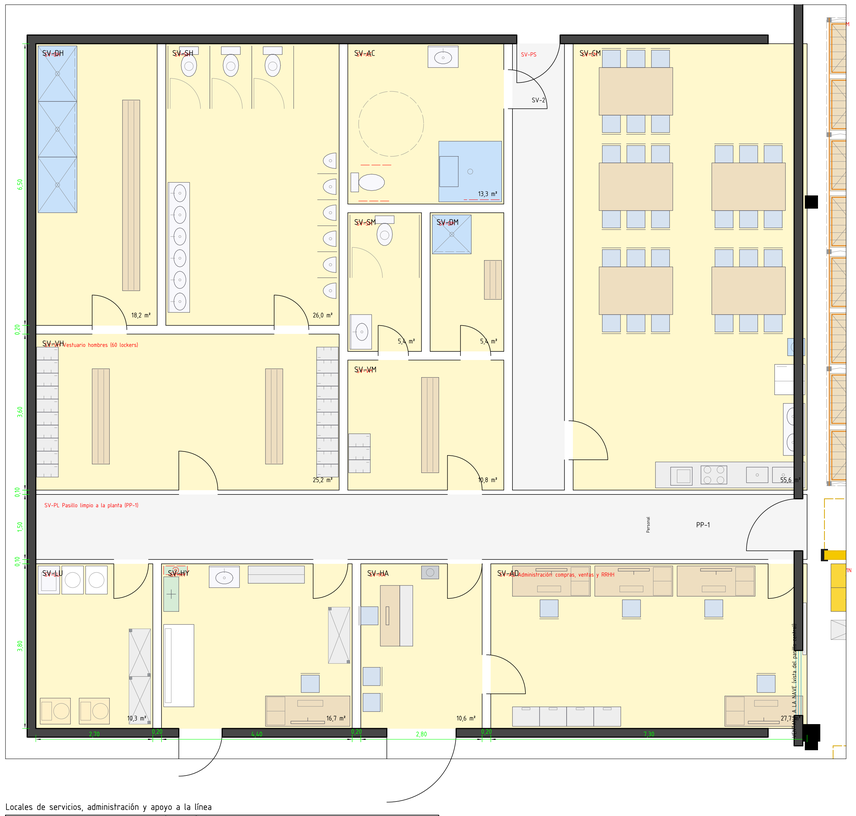


DETALLE 2 - FILA CENTRAL: MANTENIMIENTO, PAÑOL, CALIDAD, SUPERVISOR Y PCP - 1:50

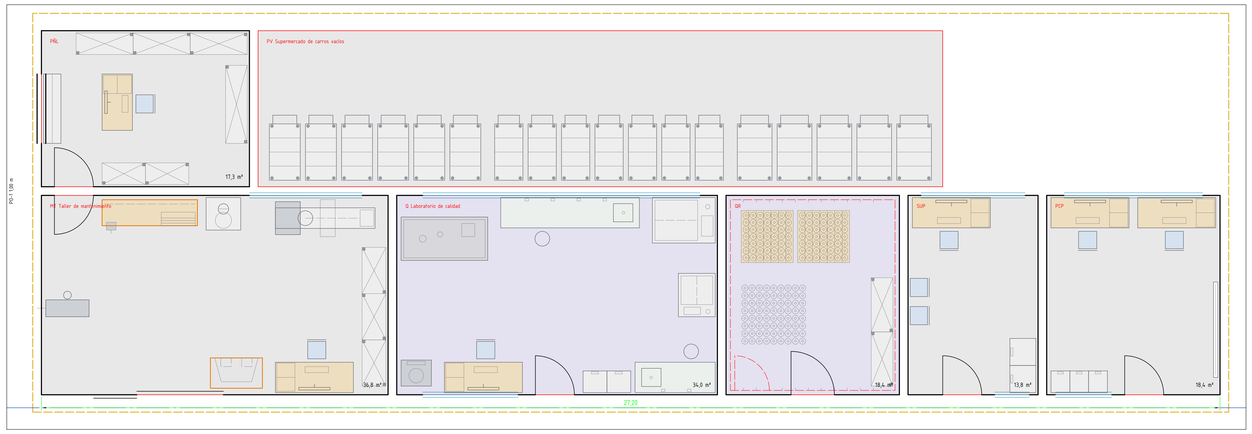

DETALLE 3 - SANITARIOS DE PLANTA (H Y M) - 1:50

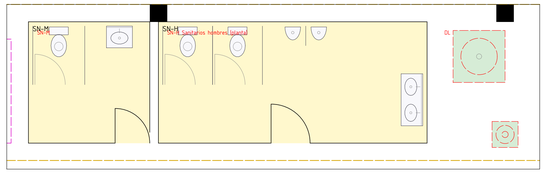

DETALLE 4 - COMPRESORES, COLECTOR Y JAULA EXTERIOR DE GASES - 1:50

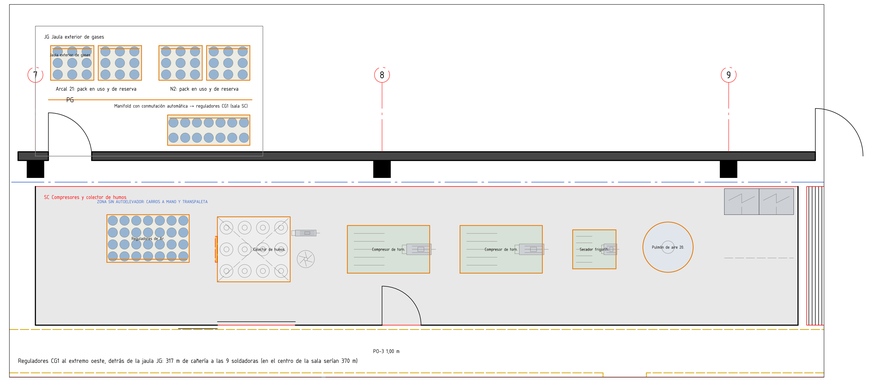

Locales de servicios, administración y apoyo a la línea

Local	m²	Equipamiento / criterio
SV-LU Utilitarios de limpieza	10,3	Pileta de lavado, carros, máquina de piso y artículos de limpieza
SV-HY Higiene y seguridad, medicina laboral, p	16,3	Una sola persona: escritorio, camilla, botiquín y lavabo; entrega de E
SV-HA Hall, recepción y fichado	10,6	Reloj biométrico y tablero de novedades al paso, ahenda a visitas y p
SV-AD Administración, compras, ventas y RRHH	27,3	4 puestos (compras 1, ventas 2, RRHH 1) y archivo; ventana a la nave a
SV-VH Vestuario hombres (60 lockers)	25,2	1 locker por empleado: 2 bloques de 10 columnas × 3 filas = 60 (56 en
SV-DH Duchas hombres	18,2	3 duchas sobre la misma pared (art. 49-55 H en el turno mañana con ch
SV-SH Inodoros, mingitorios y lavabos hombres	26,0	3 inodoros en la pared norte, 6 mingitorios en la pared este y 6 lavab
SV-VM Vestuario mujeres (9 lockers)	10,8	1 bloque de 3 columnas × 3 filas = 9 lockers (1 en 2070) y banco
SV-SM Inodoro y lavabo mujeres	5,4	Art. 49. 6 M por turno → 1 inodoro y 1 lavabo
SV-DM Ducha mujeres	5,4	1 ducha, separada del inodoro
SV-AC Sanitario accesible con ducha	13,3	Inodoro con 0,80 m libre lateral, lavabo, ducha a nivel con asiento re
SV-CM Comedor (30 plazas) y office	55,6	5 mesas de 6 lejos de la puerta; office con bacha y lavamanos sobre la
SN-H Sanitarios hombres (planta)	17,4	2 inodoros y 2 mingitorios (pared norte) y 2 lavabos (pared este)
SN-M Sanitario mujeres (planta)	7,8	1 inodoro y lavabo
MT Taller de mantenimiento	36,8	Mantenimiento preventivo: bancos, torno, agujereadora, soldadora móvil
PAÑ Pañol de mantenimiento y de línea	17,3	Pegado al taller: repuestos críticos, herramental del preventivo, cons
Q Laboratorio de calidad	34,9	Metrología, ensayo de rotura (1 cilindro por lote, W-HVAC), adherencia
QR Cuarentena de producto y muestras retenidas	18,4	Jaula con llave: lotes rechazados y un cilindro testigo por lote (BRAM
SUP Supervisor de planta	13,8	Oficina propia del encargado de turno, con ventana a la línea y al pas
PCP Planificación y control de la producción	18,4	Separada del supervisor: 2 puestos y tablero de programación con venta
SC Compresores y colector de humos	56,3	Reguladores de Arcal 25 y N2 que vienen de la jaula exterior (puerta P

Circuito y criterios

1. Ingreso por SV-1 (camino peatonal desde G4 y la garita); fichado en el hall.
2. Pasillo limpio: al sur limpieza, higiene y seguridad (con EPP y primeros auxilios), hall y administración; al norte vestuarios, sanitario accesible y comedor.
3. Vestuario: 1 locker por empleado (bloques de 10 columnas × 3 filas). Duchas en su propio local, separadas de inodoros y mingitorios; todo sólo desde el vestuario.
4. Duchas, inodoros, mingitorios y lavabos: cada grupo alineado sobre una misma pared húmeda.
5. Sanitario accesible con ducha a nivel donde estaba limpieza: se entra por el pasillo PS, que termina en la salida de emergencia SV-2.
6. Comedor: el office (bacha y lavamanos sobre la misma pared) junto a la puerta; las mesas al fondo.
7. Administración (compras, ventas, RRHH) contra la nave: ventana a lo largo del pasillo central y PP-1 a 6 m.
8. Supervisor en oficina propia y PCP separado; los dos con ventana a la línea; mantenimiento con su pañol pegado; calidad y cuarentena (con muestras y archivo) juntas.

	Fecha	Nombre	Propietario	Reemplaza a / Reemplazado por
Dibujó	14/10/26	Claude Code	FLAMA S.A.	-
Revisó			Denominación	Materiales: Mampostería / estructura metálica
Aprobó			Servicios, oficinas y apoyo	Edición: 0 — Fecha de emisión: 14/10/2026
Escala: 1:50	Método de proyección: ISO E		Bloque de servicios y administración, fila central (mantenimiento, calidad, supervisor, PCP), sanitarios de planta y sala de compresores	Hoja: 1 de 1 — Idioma: es
Unidades: Cotas en m	Formato: A0		Tipo de documento: Plano de detalle	N° de plano: FL_PI_05