


FL_PI_03 - PERSONAL, EVACUACIÓN Y SEÑALIZACIÓN

Planta Industrial FLAMA S.A. - Parque Industrial Villa de Luján, Sarandí (Avellaneda) - dimensionada al año 10 (2035). Escala 1:200. Norte arriba; la calle de acceso está al sur.

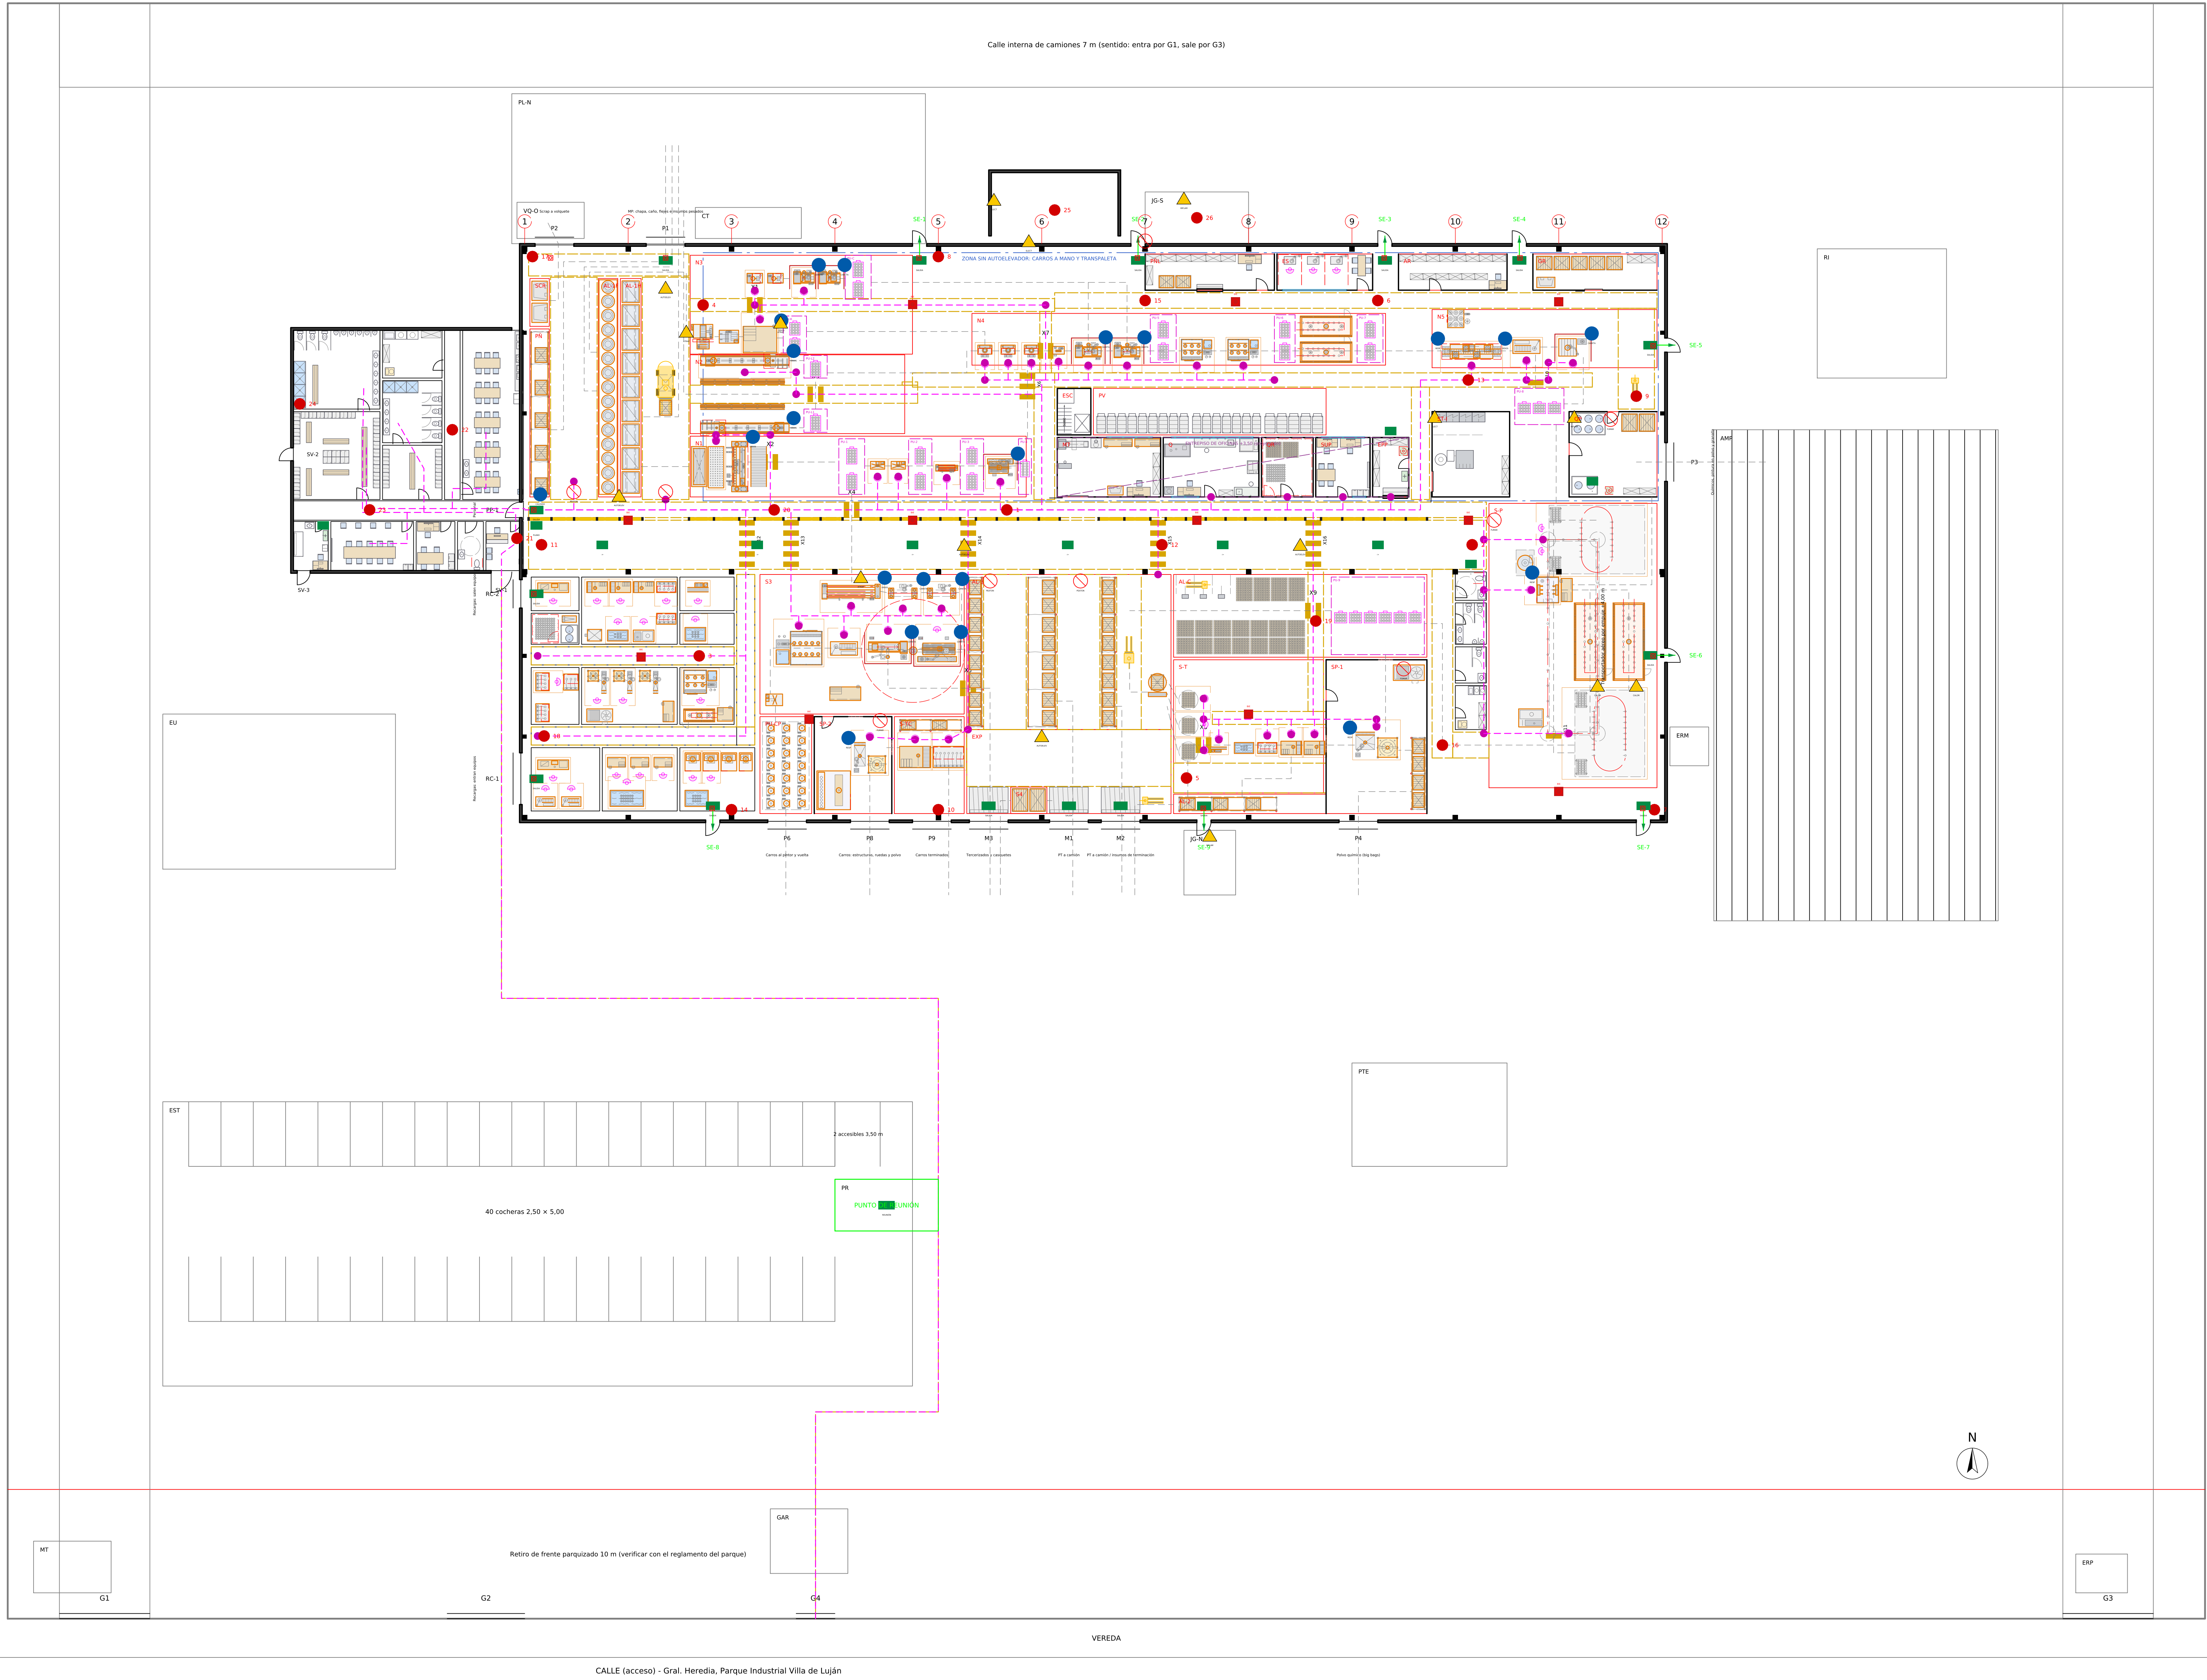

Referencias

- Hilo de personal (DIR) y puesto de trabajo
- X1... senda peatonal (cebra) donde un hilo cruza un flujo
- Punto rojo numerado: extintor ABC 10 kg BIE: boca de incendio equipada ☐ pulsador de alarma
- Señales (IRAM 10005-1: formas y colores de seguridad)
- Advertencia - ATRAP: Riesgo de atrapamiento / cargas suspendidas
- Advertencia - AUTOSILEV: Circulación de autoelevadores
- Advertencia - CALOR: Superficie caliente (hornos)
- Advertencia - ELECT: Riesgo eléctrico
- Advertencia - INFLAM: Inflamables / gases a presión
- Obligación - CALZADO: Calzado de seguridad y ropa de trabajo (ingreso a planta)
- Obligación - CARETA: Careta fotosensible y guantes
- Obligación - OIDOS: Protección auditiva
- Obligación - RESPI: Respirador P2
- Prohibición - FUMAR: Prohibido fumar y flama abierta
- Prohibición - PEATON: Prohibido el paso de peatones (calle de autoelevador)
- Salvamento y evacuación - +: Primeros auxilios / lavajeros
- Salvamento y evacuación - ->: Recorrido de evacuación
- Salvamento y evacuación - PLANO: Plano de evacuación (ingreso PP-1)
- Salvamento y evacuación - REUNION: Punto de reunión
- Salvamento y evacuación - SALIDA: Salida

Evacuación y protección contra incendio

Medios de escape (Dec. 351/78 anexo VIII)	Valor
Recorrido máximo real a una salida (grilla 0,5 m, tabiques y equipos)	31,9 m ≤ 40
Ocupación (16 n° por persona en la nave)	242 personas
Unidades de ancho de salida / ancho mínimo	3 / 1,55 m
Salidas de emergencia de 1,10 m con barril antipánico	9
Extintores ABC 10 kg (1 cada 200 m², recorrido a 20 m)	26
Bocas de incendio equipadas / pulsadores de alarma	11 / 14
Sanitarios accesibles (servicios, planta y entrepisos)	3

Longitud de los hilos

Hilo (grupo de puestos)	Desde PP-1 (m)
Almacén de MP y corte (N1)	44
Líderes, ciudadas, unión y PH (N2-N4)	35
Granallado, defectos y pintura (N5, S-P)	52
Terminación, calidad y expedición	48
Línea de carros (S3)	58
Recargas (RC)	34

Sanitarios de vestuarios (art. 49): 55 H y 6 M

Artículo	H req.	H proy.	M req.	M proy.
Artículo	3	3	1	4
Inodoros	6	6	1	4
Lavabos	6	6	0	0
Orinales	3	4	1	3
Armarios (art. 50)	56	60	7	20

Además: núcleo sanitario de planta (este) con 2 inodoros, 2 mingitorios, 2 lavabos H, 1 inodoro M, sanitario accesible y sala de limpieza, a < 25 m de pintura, terminación y PT. Cada operario tiene 1,0 m libre detrás de su puesto: integra calle M materia ajena para por su espalda (verificado). Mamparas ignífugas en todos los puestos de soldadura.

Fecha	Nombre	Propietario	Reemplaza a / Reemplazado por
03/10/2026	Claude Code	FLAMA S.A.	-
Revisó	Aprobó	Denominación	Material
		Personal y seguridad	-
Escala	Método de proyección	Edición	Fecha de emisión
1:200	ISO E	0	03/10/2026
Unidades	Formato	Tipos de documento	Tipos de documento
Cotas en m	A0	Plano de seguridad e higiene	FL_PI_03