


FL_PI_03 - PERSONAL, EVACUACIÓN Y SEÑALIZACIÓN

Planta Industrial FLAMA S.A. - Parque Industrial Villa de Luján, Sarandí (Avellaneda) - dimensionada al año 10 (2035). Escala 1:200. Norte arriba; la calle de acceso está al sur.

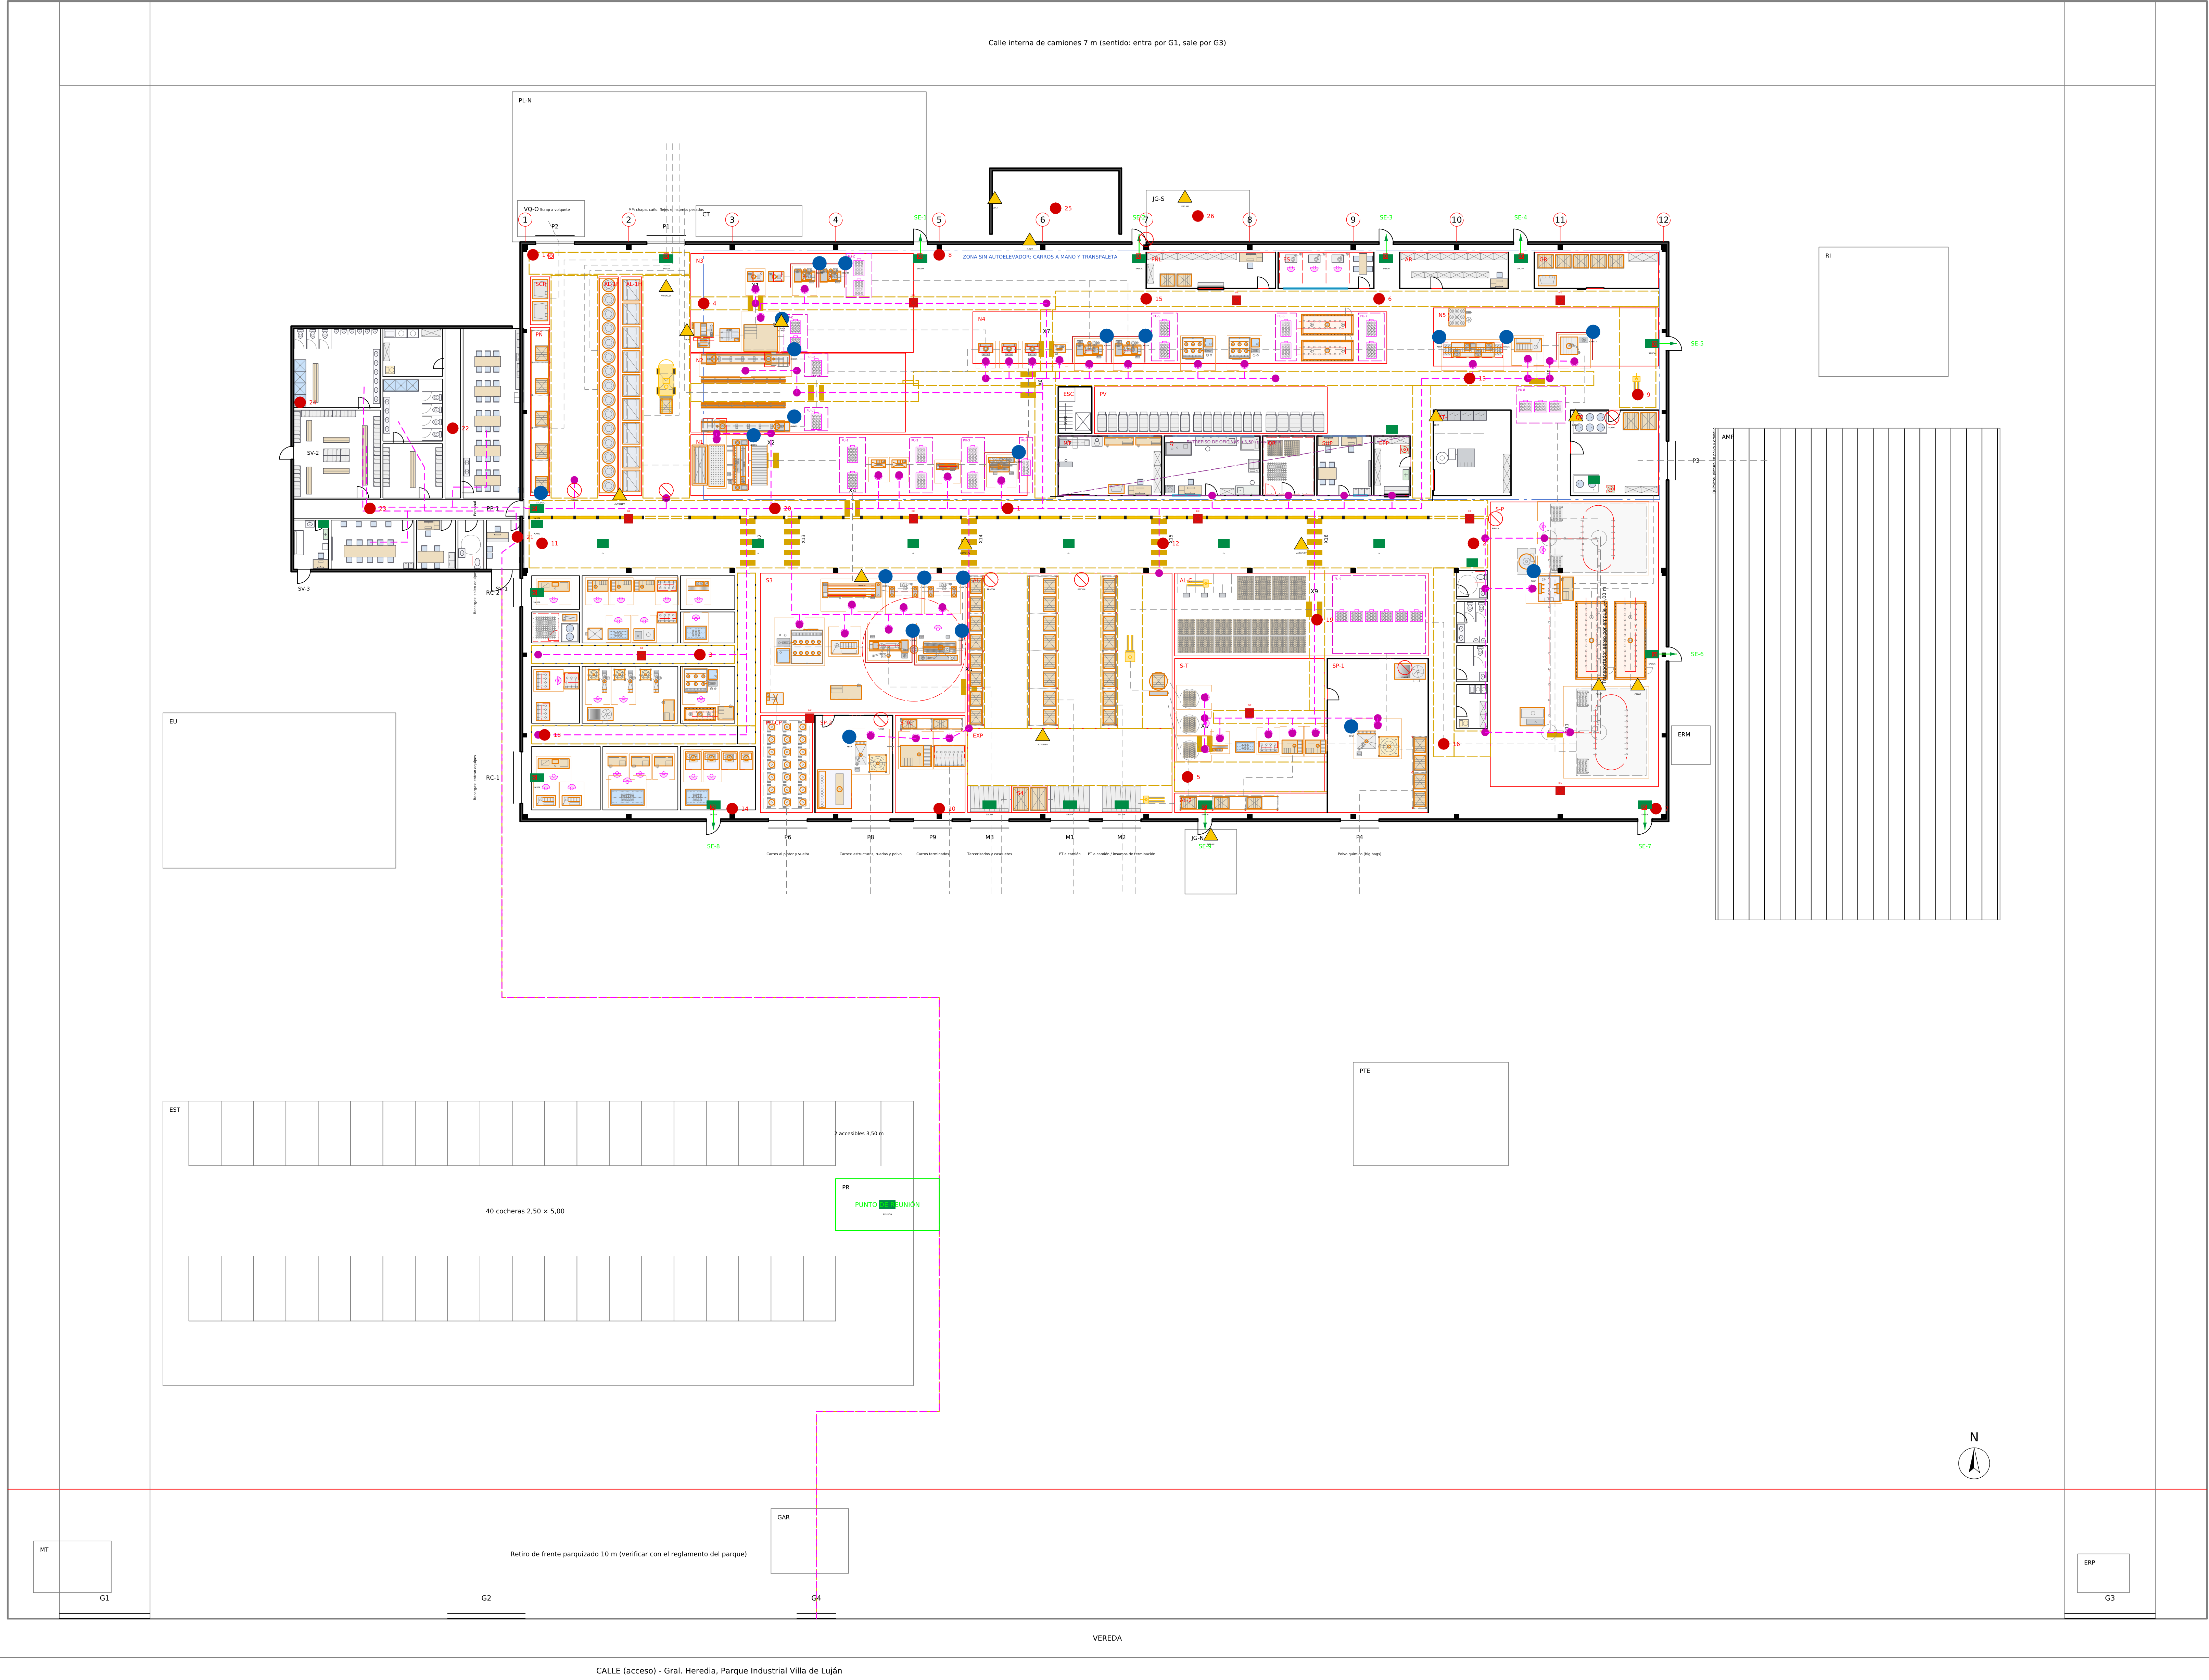

Referencias

Hilo de personal (DIR) y puesto de trabajo
X1... senda peatonal (cebra) donde un hilo cruza un flujo
Punto rojo numerado: extintor ABC 10 kg BIE: boca de incendio equipada ☐ pulsador de alarma
Señales (IRAM 10005-1: formas y colores de seguridad)

Advertencia - ATRAP: Riesgo de atrapamiento / cargas suspendidas
Advertencia - AUTOSILEV: Circulación de autoelevadores
Advertencia - CALOR: Superficie caliente (hornos)
Advertencia - ESECT: Riesgo eléctrico
Advertencia - INFLAM: Inflamables / gases a presión
Obligación - CALZADO: Calzado de seguridad y ropa de trabajo (ingreso a planta)
Obligación - CARETA: Careta fotosensible y guantes
Obligación - ODDOS: Protección auditiva
Obligación - RESQ: Respirador P2
Prohibición - FUMAR: Prohibido fumar y flama abierta
Prohibición - PEATON: Prohibido el paso de peatones (calle de autoelevador)
Salvamento y evacuación - +: Primeros auxilios / lavabos
Salvamento y evacuación - ->: Recorrido de evacuación
Salvamento y evacuación - PLANO: Plano de evacuación (ingreso PP-1)
Salvamento y evacuación - REUNION: Punto de reunión
Salvamento y evacuación - SALIDA: Salidas

Evacuación y protección contra incendio	
Recorrido de escape (DSC - 331/78 anexo VII)	Valor
Recorrido máximo real a una salida (grilla 0,5 m, tabiques y equipos)	31,9 m ≤ 40
Ocupación (16 m² por persona en la nave)	242 personas
Unidades de ancho de salida / ancho mínimo	3 / 1,55 m
Salidas de emergencia de 1,10 m con barril antipánico	9
Extintores ABC 10 kg (1 cada 200 m², recuento ≤ 20 m)	26
Bocas de incendio equipadas / pulsadores de alarma	13 / 14
Sanitarios accesibles (servicios, planta y entrepisos)	3

Longitud de los hilos

Hilo (grupo de puestos)	Desde PP-1 (m)
Almacén de RP y corte (N1)	44
Laborios, cuartos, unión y PH (N2-N4)	35
Granallado, defectos y pintura (N5, S-P)	52
Terminación, calidad y expedición	48
Línea de carnos (S3)	58
Recargas (RC)	34

Sanitarios de vestuarios (art. 49): 55 H y 6 M

Artefacto	H req.	H proy.	M req.	M proy.
Inodoros	3	3	1	4
Lavabos	6	6	1	4
Orinales	6	6	0	0
Duchas	3	4	1	3
Armarios (art. 50)	56	60	7	20

Además: núcleo sanitario de planta (este) con 2 inodoros, 2 mingitorios, 2 lavabos H, 1 inodoro M, sanitario accesible y sala de limpieza, a < 25 m de pintura, terminación y PT. Cada operario tiene 1,0 m libre detrás de su puesto: integra calle M materia ajena pasa por su espalda (verificado). Mamparas ignífugas en todos los puestos de soldadura.

Fecha		Nombre		Propietario		Reemplaza a / Reemplazado por	
Dibujó 02/10/26		Claude Code		FLAMA S.A.			
Revisó				Denominación		Material	
Aprobó							
Escala		Método de proyección		Personal y seguridad		Edición	
1:200		ISO E				0	
Unidades		Formato		medios de acceso, protección contra incendio, IRAM 11005		Fecha de emisión	
				N° de plano		02/10/2026	
Cotas en m		A0		Tipo de documento		Hoja	
				Plano de seguridad e higiene		1 / 1	
						es	
						FL_PI_03	