

FL PI_05 - SERVICIOS AL PERSONAL, OFICINAS Y PCP


Circuito del personal, vestuarios y sanitarios (Dec. 351/79 arts. 49-50), oficinas con vista y acceso directo a producción, accesibilidad (Ley 24.314).

DETALLE 1 - BLOQUE DE SERVICIOS (PLANTA BAJA) - 1:50




Locales de servicios, oficinas y núcleo sanitario	
Local	m² Equipamiento / criterio
SV-RA Inmensa auxiliar y accesorio	10.3 Camilla, botiquín, lavabo y heladero. salida directa al exterior para
SV-DE Sala de capacitación (12 personas)	24.3 Inducción, teoría de la escuela de soldadura y simulación; comedor d
SV-JP Higiene y seguridad y medicina laboral	11.4 Servicio de IyS (Dec. 1339/96). Ingreso, exámenes periódicos, EPP
SV-AC Sanitario accesible y de visitas	7.6 Circuito libre Ø 1.50 m, barras, inodoro con 0.80 m libre lateral (art. 5)
SV-MA Hall, recepción y fichado	11.0 Reloj biométrico y tablero de novedades al paso
SV-SH Vestuario hombres (60 armarios dobles)	40.9 Armario doble ropa de calle / de trabajo (Dec. 351/79 art. 50) / neg. 5
SV-SH Sanitarios y duchas hombres	40.9 3 inodoros, 6 mingitorios, 6 lavabos, 4 duchas (art. 49, turno mañana
SV-SM Vestuario mujeres (120 armarios dobles)	19.3 Ropa, 10 en 2035
SV-SM Sanitarios y duchas mujeres	22.1 4 inodoros, 4 lavabos, 3 duchas
SV-U Limpieza, reposta y lavadero	17.0 Lavado de ropa de trabajo; carro y artículos de limpieza
SV-MA Comedor (30 plazas) y office	61.6 3 mesas de 6, 2 tandas de 30 min por turno (21 personas en la tanda ma
SN-AC Sanitario accesible (planta)	5.3 Circuito Ø 1.50 m, barras; abre a la calle este, a 4 m del pasillo cent
SN-H Sanitario hombres (planta)	7.7 2 inodoros, 2 mingitorios, 2 lavabos sobre la misma pared húmeda
SN-M Sanitario mujeres (planta)	6.7 1 inodoro y lavabo
SN-U Sala de limpieza (planta)	6.2 Pileta de lavado, carro y artículos de limpieza; barridora
PA-OF Administración, ventas, compras y calida	25.9 Servicios y Oficinas 2035; 6 puestos en el turno mañana
PA-PCP Planificación y control de la producció	12.5 Tablero de programación a la vista de la línea
PA-J Jefatura de planta	11.2
PA-RE Sala de reuniones (8)	15.0
PA-AC Sanitario accesible	6.1
PA-AR Archivo y office	5.8

DETALLE 2 - ENTREPISO DE OFICINAS +3,50 SOBRE LA FILA CENTRAL - 1:50

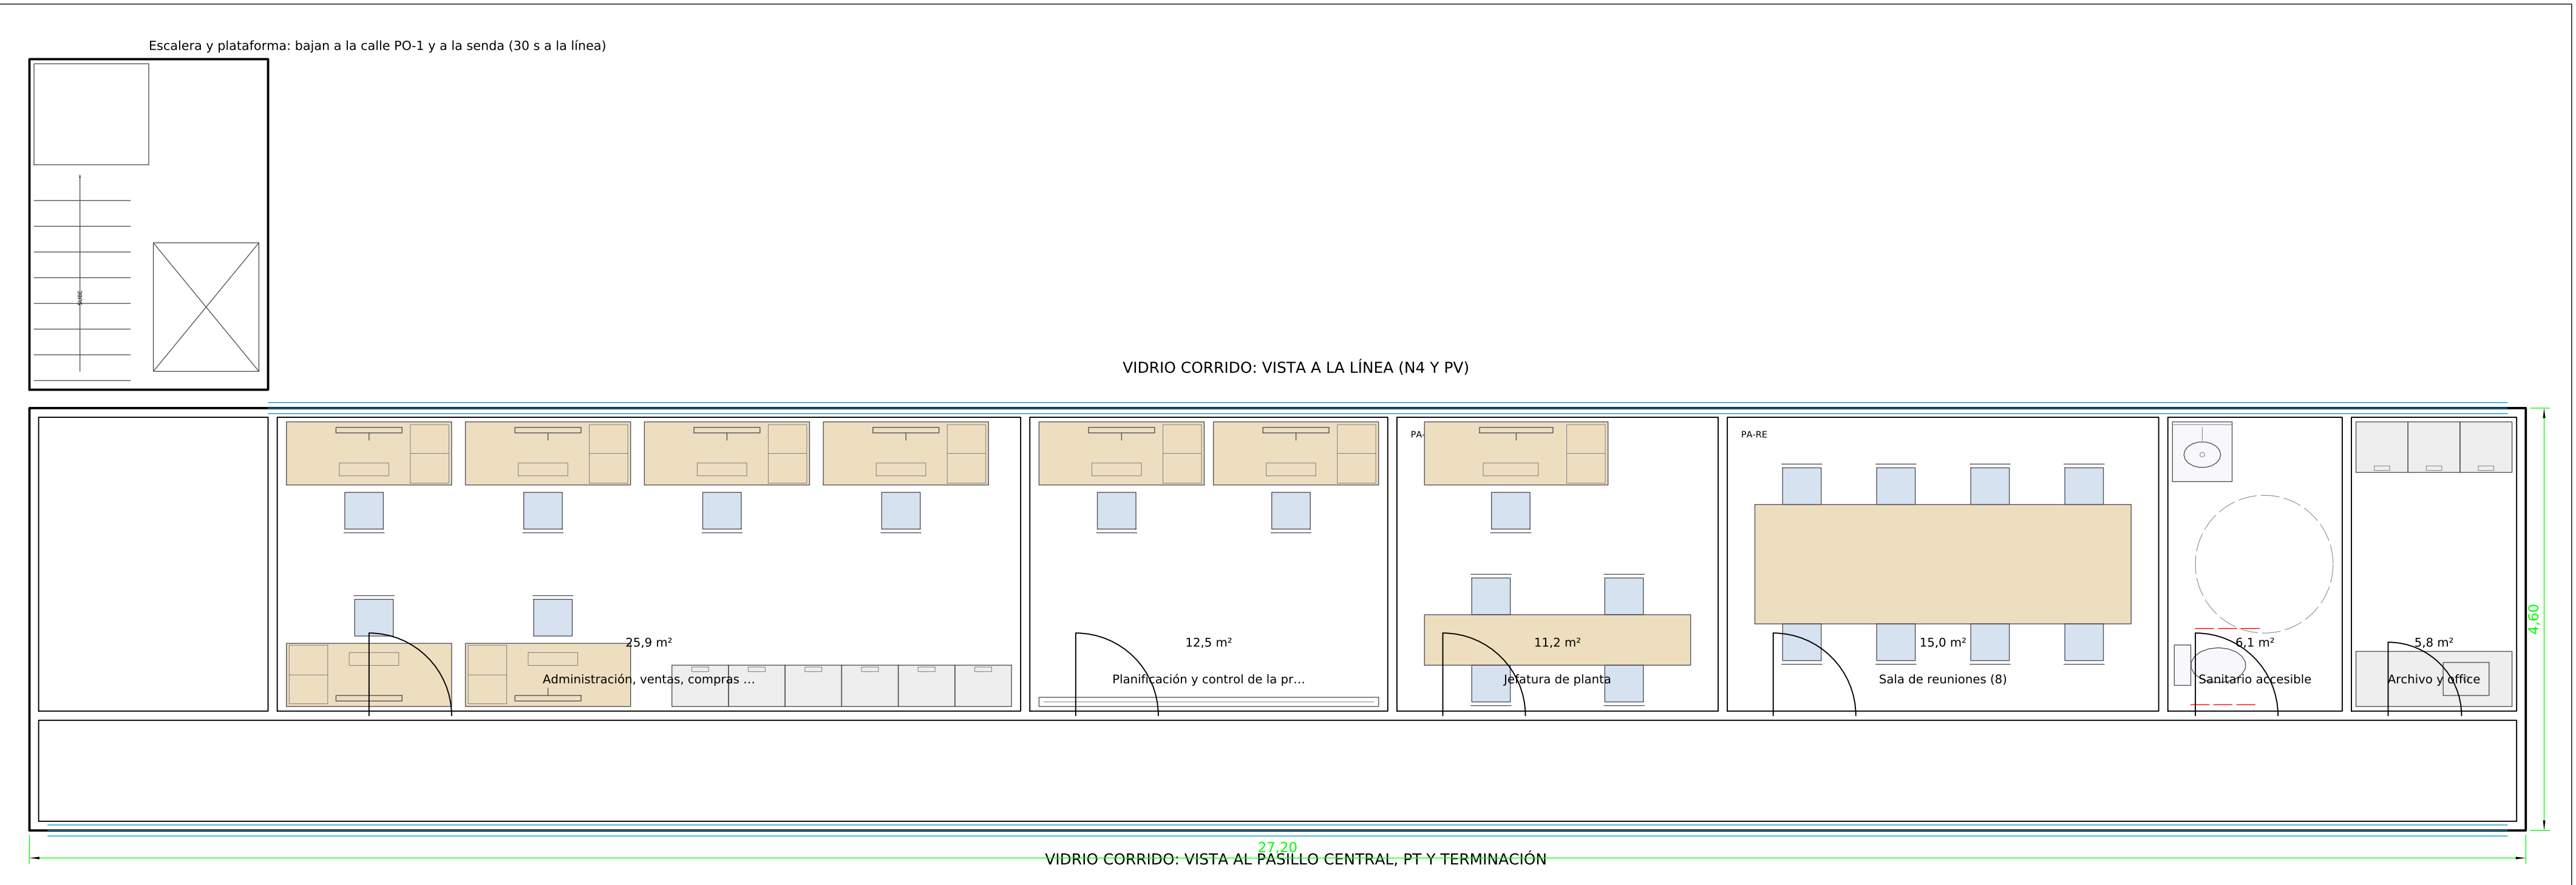


DETALLE 3 - NÚCLEO SANITARIO DE PLANTA - 1:50

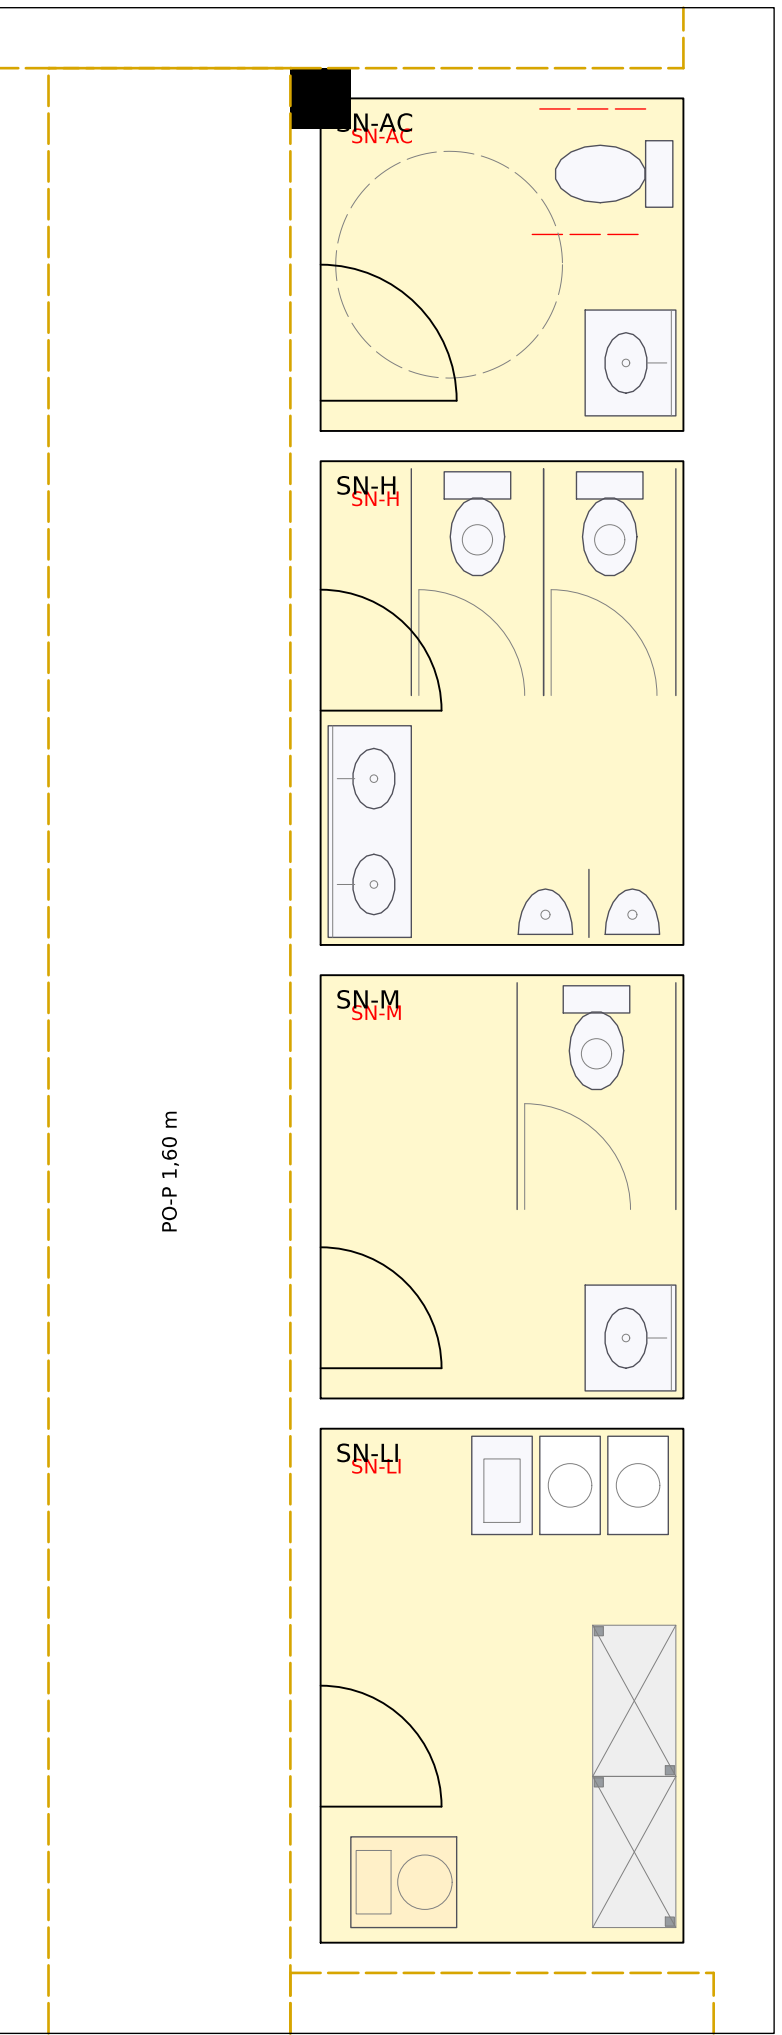

Circuito y criterios

- Ingreso por SV-1 desde el estacionamiento; fichado en el hall (reloj biométrico).
- Pasillo limpio: a la izquierda vestuarios, a la derecha oficinas de servicio y capacitación.
- Vestuario: armario doble (ropa de calle / de trabajo). Duchas y sanitarios sólo desde el vestuario.
- Inodoros, mingitorios y lavabos sobre la misma pared húmeda (montante único de agua y cloaca).
- PP-1: entrada a la senda peatonal separada del autotransporte por la defensa.
- Comedor a 6 m de PP-1 con lavamanos en la entrada (refrigerio de 30 min en 2 tandas).
- Administración, PCP y jefatura en el entrepiso: ven toda la línea y bajan a ella en 30 s.
- Supervisión de turno en planta baja (fila central) con ventana a la línea.

CORTE B-B POR EL ENTREPISO (x = 55 m) - 1:100

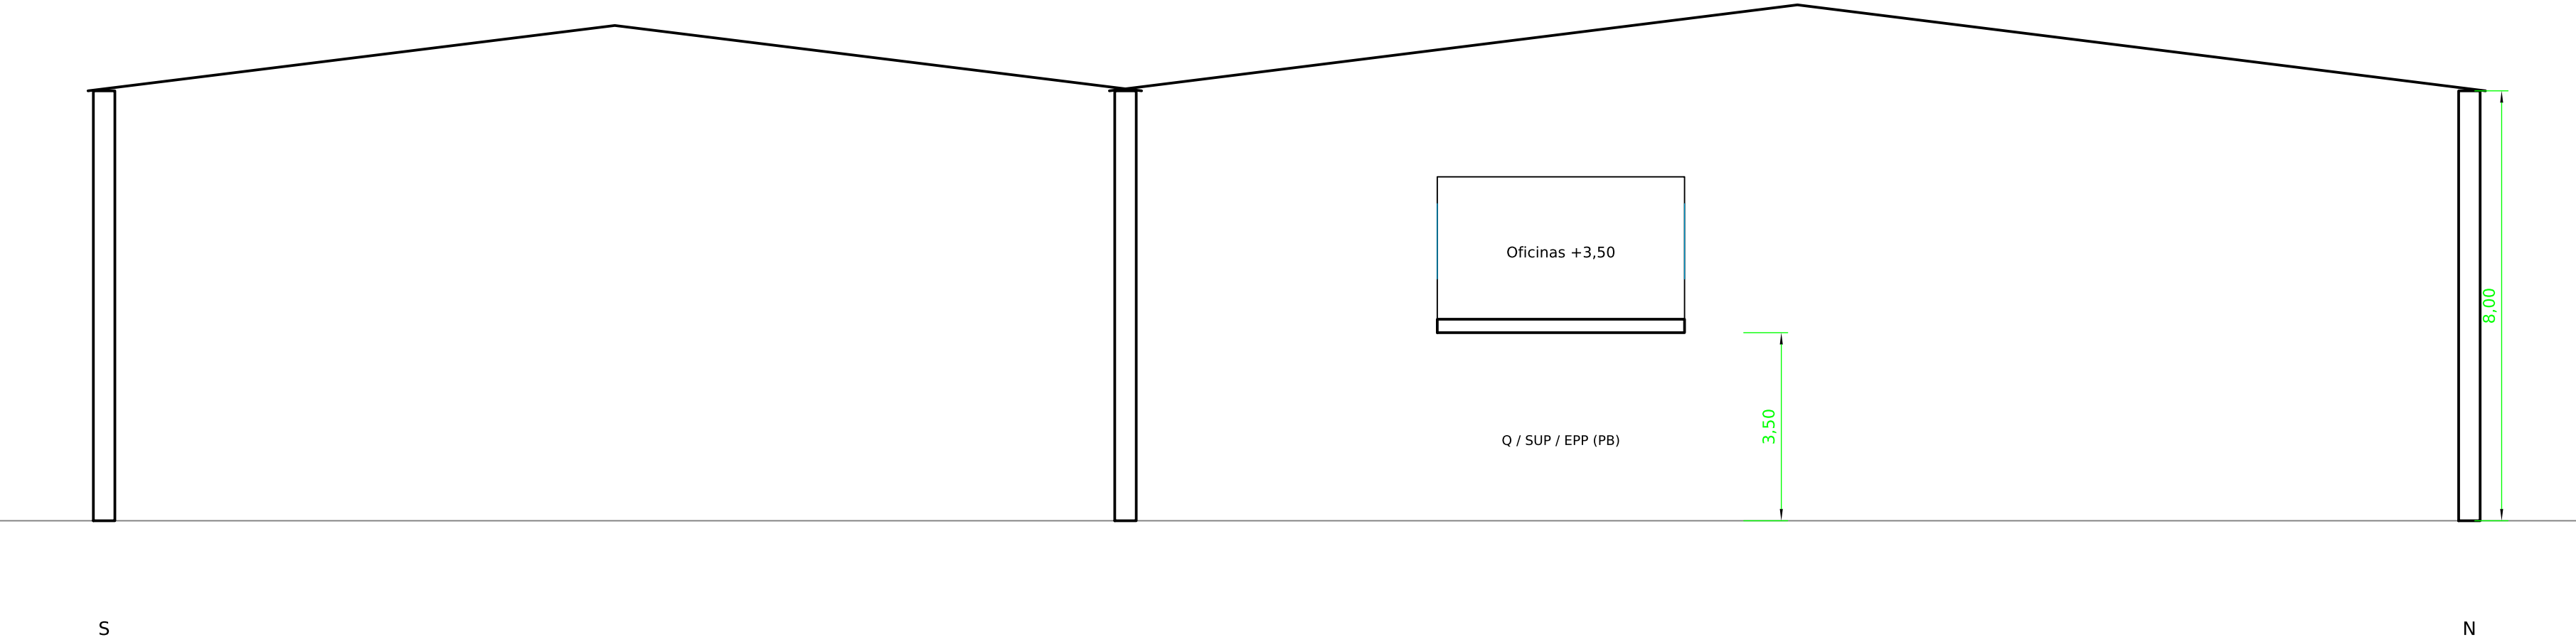

Fecha	Nombre	Propietario	Reemplaza a / Reemplazado por	
02/10/2026	Claude Code	FLAMA S.A.	Material	-
Revisó	Aprobó	Denominación	Denominación	
		Servicios, oficinas y PCP	Mampostería / estructura metálica	
Escala	Método de proyección	Edición		Fecha de emisión
1:50	ISO E	0		02/10/2026
Unidades	Formato	Tipo de documento		Nº de plano
Cotas en m	A0	Plano de detalle		FL_PI_05