FL_PI10_03 - CIRCULACIÓN, FLUJOS DE MATERIALES Y RECORRIDOS DEL PERSONAL

Carriles del autoelevador, sendas peatonales y pasillos de operarios con su ancho; flujo de MP, de semielaborado y de PT; hilos del personal desde los vestuarios.

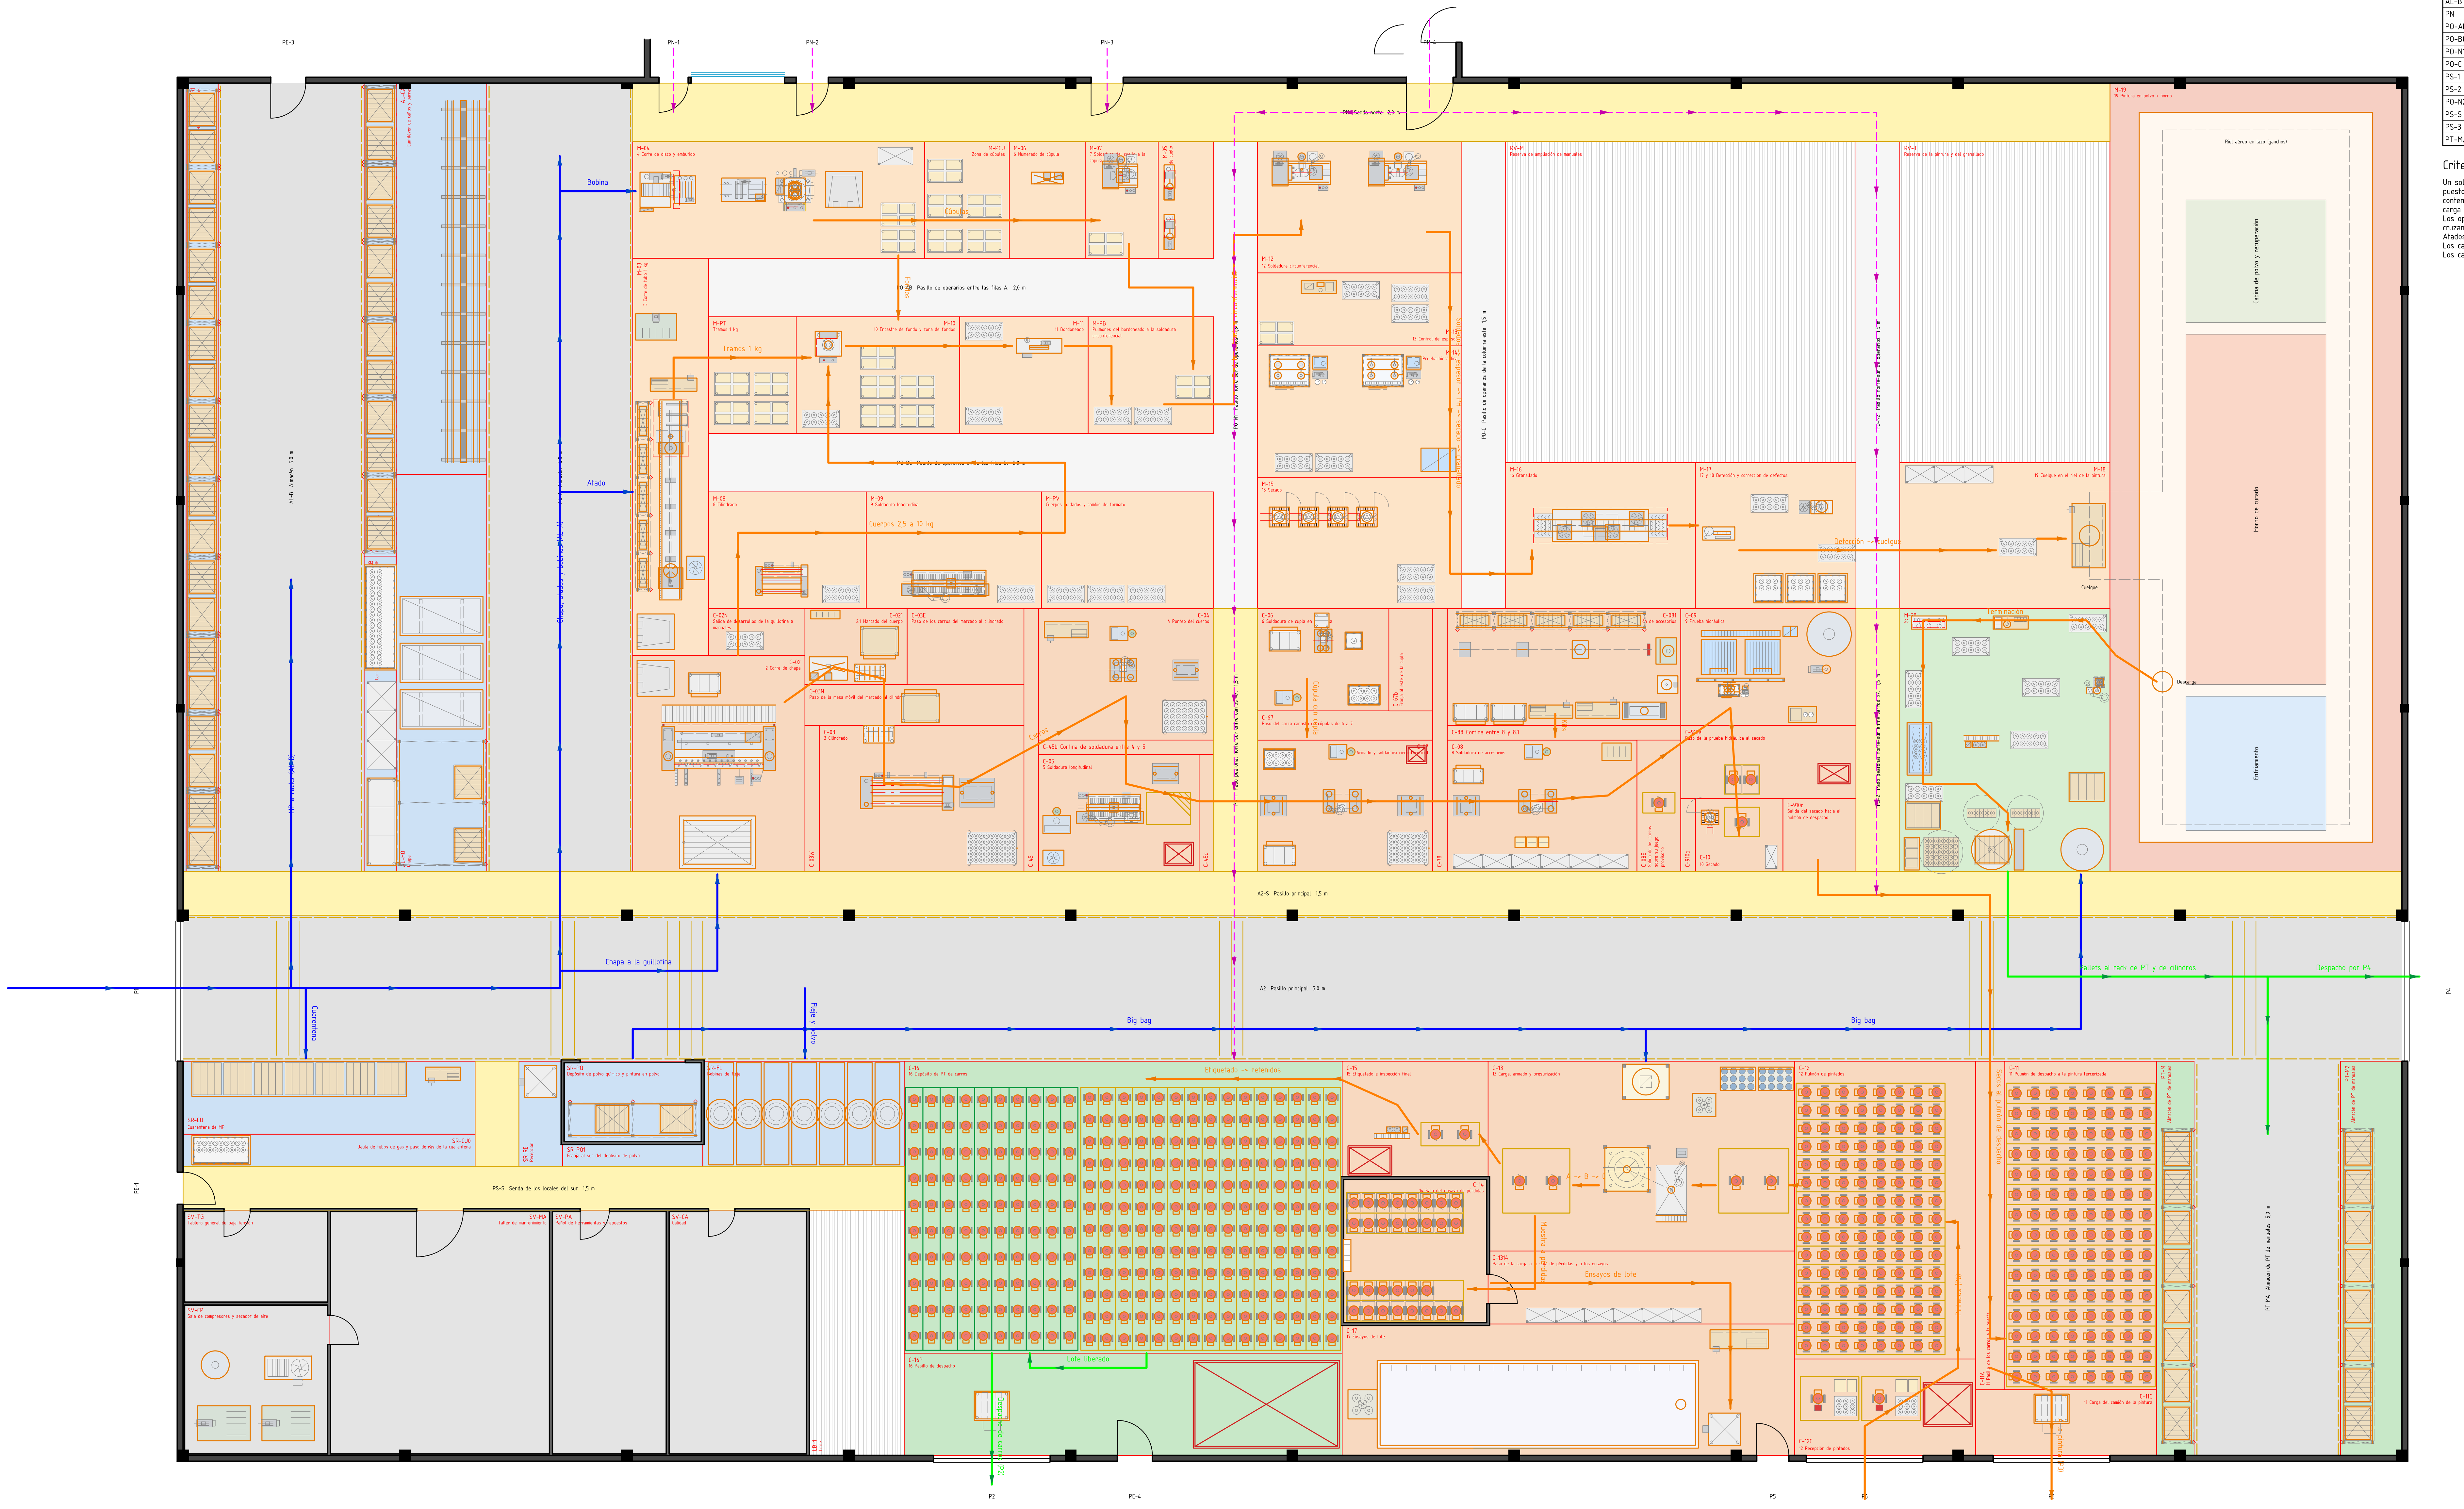
Bobina
Añado
Chapa a la guillotina
Cuarentena
Fleje y polvo
Big bag
Big bag
Pallets al rack de PT y de cilindros
Despacho por P4
A2-S Pasillo principal 1,5 m
A2 Pasillo principal 5,0 m
PS-S Senda de los locales del sur 1,5 m
Etiquetado → retenidos
Enfriamiento
Horno de curado
Cabina de polvo y recuperación
PN-1
PN-2
PN-3
PE-1
P2
PE-4
P5

Referencias

🟥	Carril del autoelevador (5,0 m)
🟨	Senda peatonal demarcada
☐	Pasillo de operarios y carros a mano

Flujos

→	MP: materia prima (azul)
→	SE: semielaborado (naranja)
→	PT: producto terminado (verde)
- - →	Hilos de personal (magenta)

Pasillos (m)

Cód.	Pasillo	Ancho	Largo	Uso
A2	Pasillo principal	5,0	76,0	Autoelevador
A2-S	Pasillo principal	1,5	76,0	Peatonal
AL-A	Almacén	5,0	27,0	Autoelevador
AL-B	Almacén	5,0	27,0	Autoelevador
PN	Senda norte	2,0	50,6	Peatonal
PO-AB	Pasillo de operarios entre las filas A y B de manua.	2,0	17,3	Operarios
PO-BC	Pasillo de operarios entre las filas B y C de manua.	2,0	17,3	Operarios
PO-N1	Pasillo norte-sur de operarios	1,5	16,0	Operarios
PO-C	Pasillo de operarios de la columna este	1,5	16,0	Operarios
PS-1	Paso peatonal norte-sur entre carros 4/5 y 6/7	1,5	9,0	Peatonal
PS-2	Paso peatonal norte-sur entre carros 9/10 y la term.	1,5	9,0	Peatonal
PO-N2	Pasillo norte-sur de operarios	1,5	16,0	Operarios
PS-S	Senda de los locales del sur	1,5	24,7	Peatonal
PS-3	Paso peatonal de la senda sur al pasillo principal	1,5	3,6	Peatonal
PT-MA	Almacén de PT de manuales	5,0	13,5	Autoelevador

Criterios de circulación

Un solo autoelevador (Heli CPCD50, W-MAN y W-CAR): circula sólo por A2, AL-A y AL-B (5,0 m) y entra a los puestos únicamente donde la máquina mira al carril: mesa elevadora, cajón del atado, desbobinador, contenedores de scrap, big bags (terminación y carro 13), envolvedora y calles de PT; las tarimas de carga de los carros (P2, P3 y P6) las toma desde la playa sur.
Los operarios caminan por las sendas (amarillas) y por los pasillos de operarios de 1,5 a 2,0 m; cruzan el carril sólo por los cruces demarcados de la baranda.
Atados de 6 m: se mueven colgados de la pluma (W-MAN 1 y 2), a lo largo del pasillo.
Los carros de manuales (FCHP y de 12 cajones) se empujan a mano entre puestos pegados (W-MAN).
Los carros (extintores rodantes) ruedan sobre su juego provisorio desde el puesto 8 (W-CAR).

	Fecha	Nombre
Dibujó	15/10/26	Claude Code
Revisó		
Aprobó		

Escala: 1:100
Método de proyección: ISO E
Unidades: Cotas en m
Formato: A0

Propietario: FLAMA S.A.

Denominación: Circulación y flujos
Layout 2035 v10 - pasillos, materiales y personas

Tipo de documento: Plano de circulación

Reemplaza a / Reemplazado por: -
Material: -
Edición: 0
Fecha de emisión: 15/10/2026
Hoja: 3 / 5
Idioma: es
N° de plano: FL_PI10_03