


FL_PI_02 - FLUJO DE OPERACIONES Y PROCESOS POR SECCIÓN

Planta Industrial FLAMA S.A. - Parque Industrial Villa de Luján, Sarandí (Avellaneda) - dimensionada al año 10 (2035). Escala 1:200. Norte arriba; la calle de acceso está al sur.

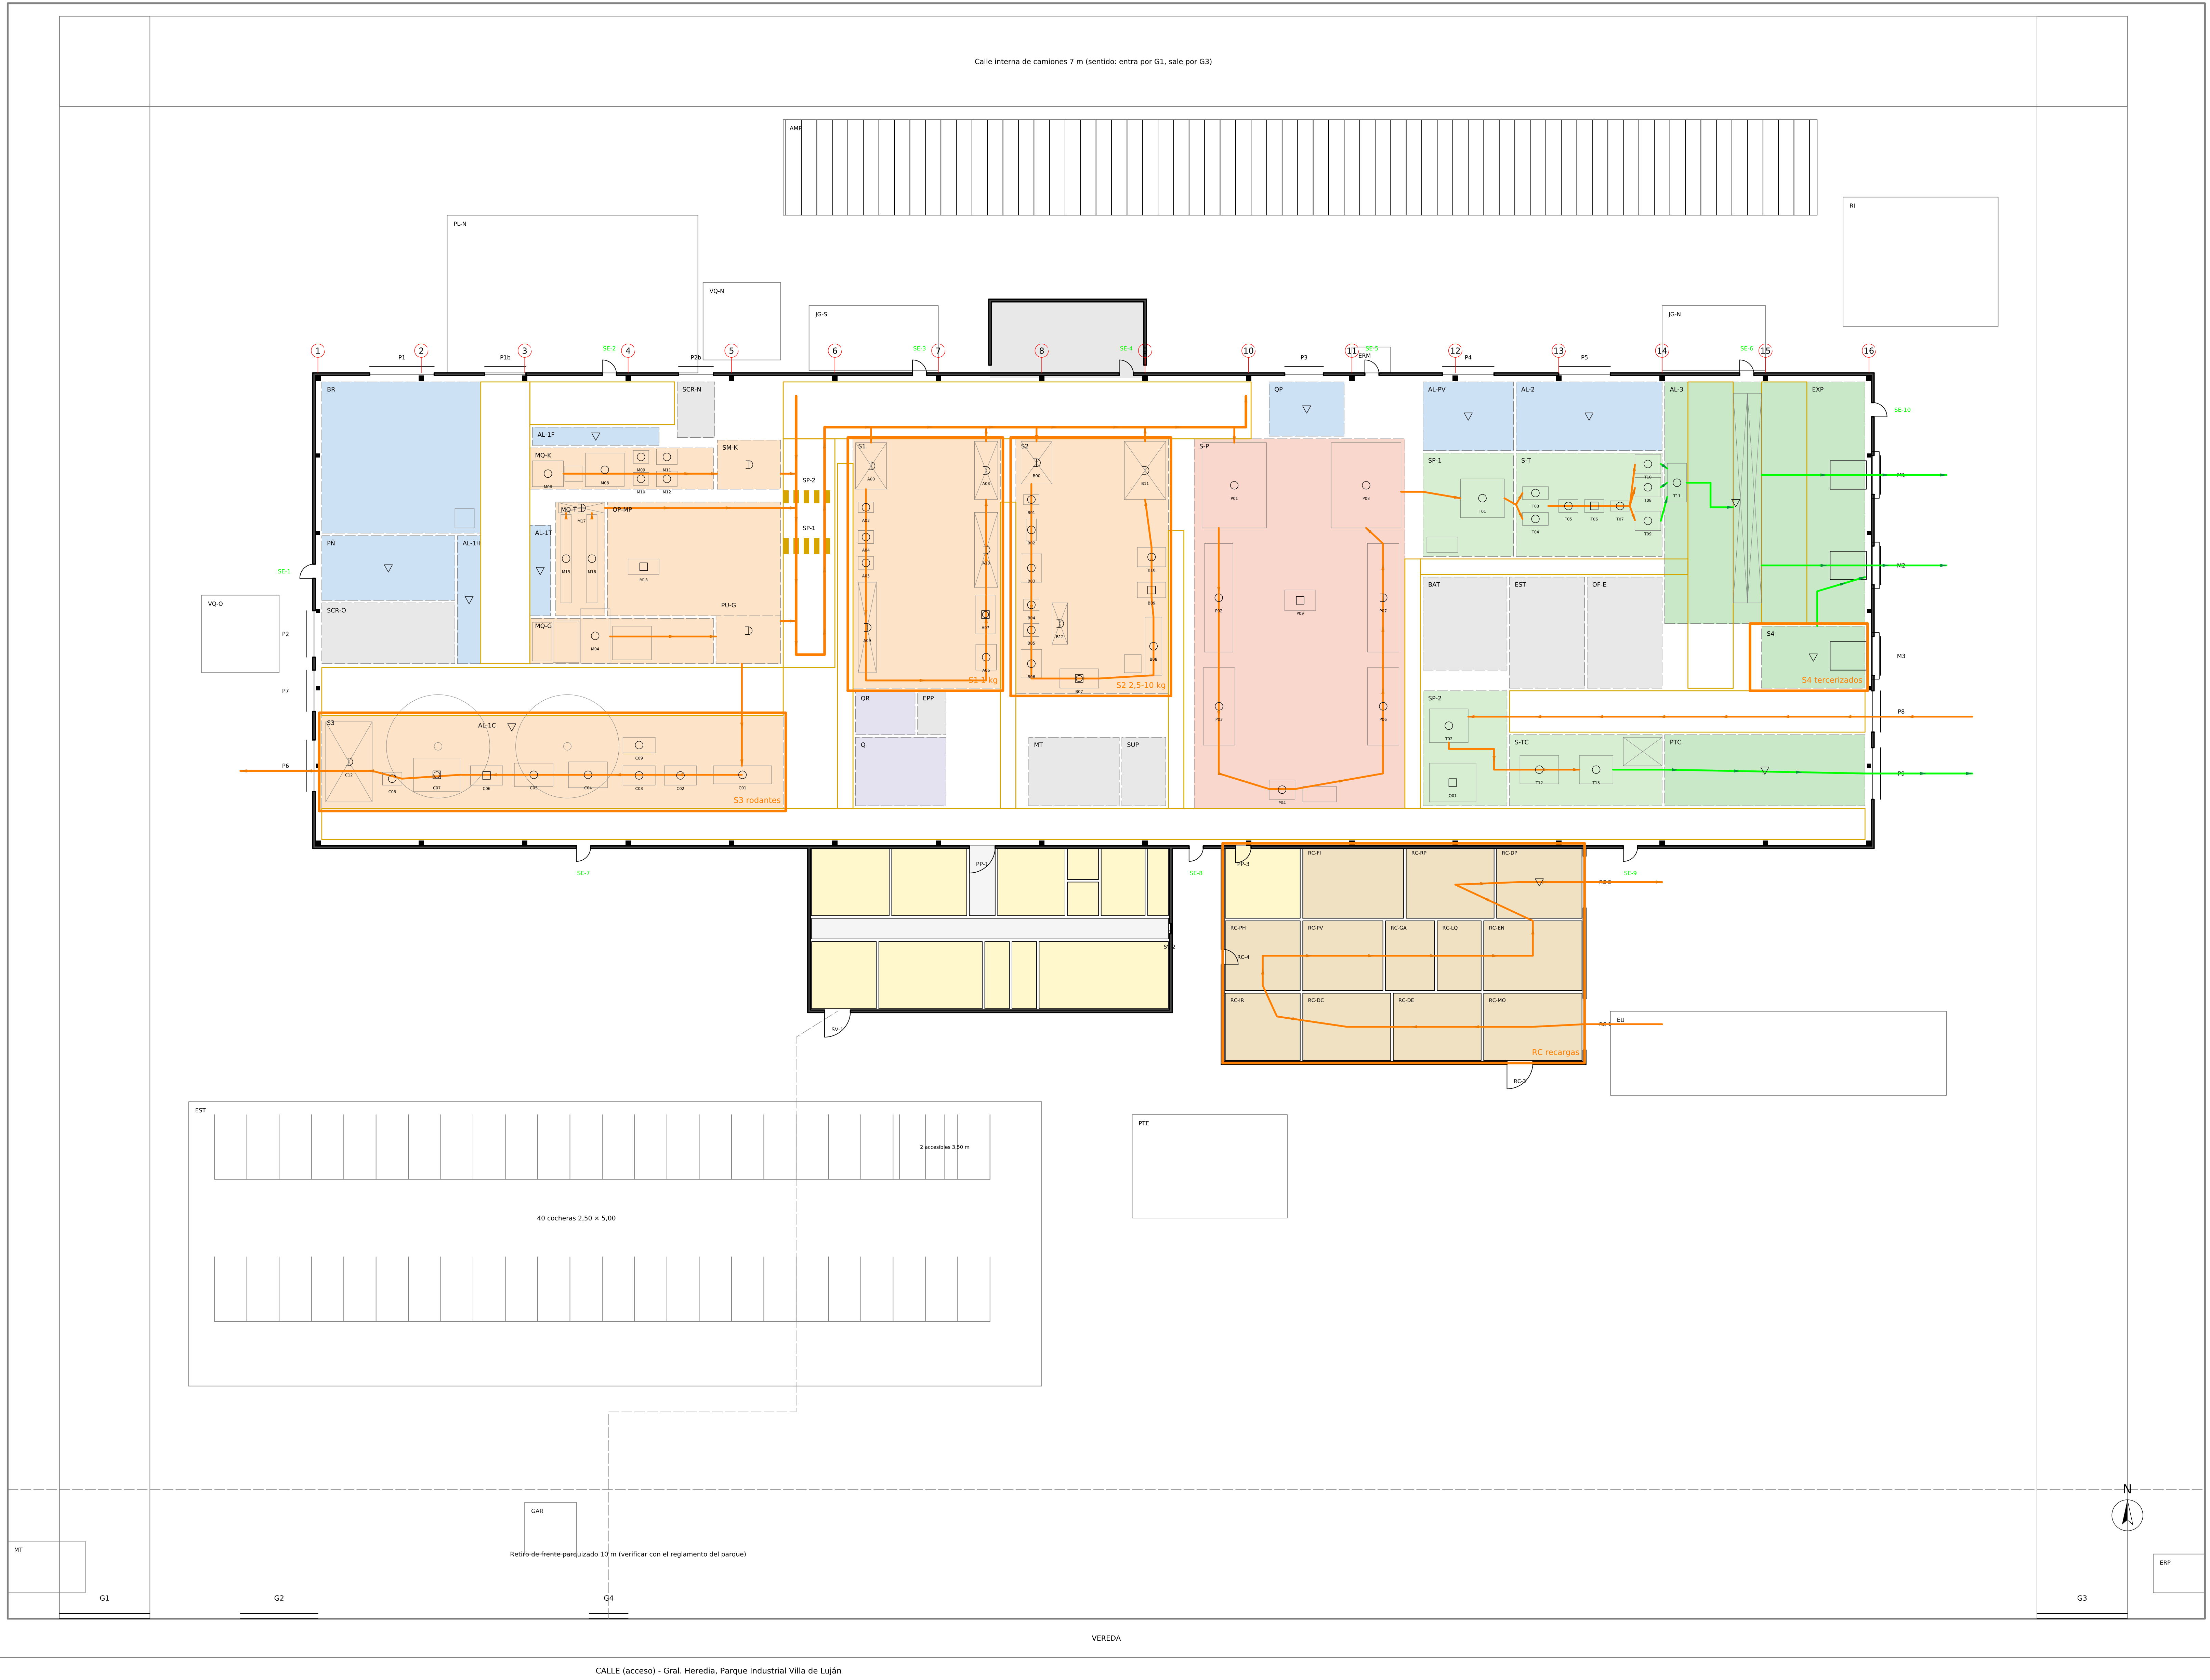

Símbolos (ASME)

- Operación
- Inspección / control
- Operación e inspección combinadas
- Transporte (tren logístico, autoelevador, carro)
- Demora: pulmón o supermercado
- Almacenamiento

Flujos

- SE: semielaborado (naranja)
- Tren logístico de un sentido (SE)
- PT: producto terminado (verde)

S1 - Matafuegos ABC 1 kg (fabricados)		Subconjunto cúpulas y fondos 1-10 kg		S2 - Matafuegos ABC 2,5 / 5 / 10 kg	
Paso	Dónde	Paso	Dónde	Paso	Dónde
✓ Corte en cartón	AL-1F	✓ Hoja LAF	AL-3H	✓ Hoja LAF	AL-3H
○ Corte de caño láser	M15,M16	○ Desdoblado y enderezado	M06	○ Corte de cuerpo	M04
⌈ Pulmón	M17	○ Corte y embudo	M08	⌈ Pulmón	PU-G
⌈ Tren logístico	PM	○ Preparación de cuello	M09,M10	⌈ Tren logístico	PM
⌈ Kanban	A00	○ Soldadura de cuello	M11,M12	⌈ Supermercado	B00
○ Numerado	A03	⌈ Supermercado	SM-K	○ Numerado	B01
○ Encastre de fondo	A04	⌈ Tren logístico a A04/A05 y B05	PM	○ Cilindrado	B02
○ Encastre de cúpula con cuello	A05			○ Soldadura longitudinal	B03
⌈ Pulmón	A09	○ Bordonado	B04	○ Bordonado	B04
○ Soldadura circumferencial	A06	○ Encastre de fondo y cúpula	B05	○ Encastre de fondo y cúpula	B05
⌈ Prueba hidráulica 100 %	A07	○ Soldadura circumferencial	B06	○ Soldadura circumferencial	B06
⌈ Pulmón a pintura	A08	○ Prueba hidráulica 100 %	B07	○ Prueba hidráulica 100 %	B07
⌈ Tren logístico	PM	○ Granallado	B08	○ Granallado	B08
○ Pintado	P02	○ Detección de defectos	B09	○ Detección de defectos	B09
○ Secado	P03	○ Corrección	B10	○ Corrección	B10
○ Pintura en polvo	P04	⌈ Pulmón a pintura	B11	⌈ Pulmón a pintura	B11
○ Pulverizado	P06	⌈ Tren logístico	PM	⌈ Tren logístico	PM
⌈ Espesor y adherencia	P09	○ Pintura (igual que S1)	P02-P06	○ Pintura (igual que S1)	P02-P06
○ Encamillado	T03	○ Terminación (igual que S1)	T01-T11	○ Terminación (igual que S1)	T01-T11
○ Presurización con N ₂	T05	⌈ Almacen de PT	AL-3	⌈ Almacen de PT	AL-3
○ Hermeticidad	T06	○ Expedición	M1,M2	○ Expedición	M1,M2
○ Etiquetado	T07				
○ Embalaje y palletizado	T08,T09				
○ Envolvido	T11				
⌈ Almacen de PT	AL-3				
○ Expedición	M1,M2				

S3 - Matafuegos ABC rodantes 25 / 50 / 70 ...		S4 - Tercerizados revendidos (CO ₂ , agua, A...		RC - Recargas (servicio)	
Paso	Dónde	Paso	Dónde	Paso	Dónde
✓ Hojes LAC	AL-1H	○ Recepción	H3	○ Recepción	RC-1
○ Corte de cuerpo	M04	⌈ Control de recepción y sello IRAM	S4	⌈ Clasificación en 4 celas	RC-1
⌈ Pulmón	PU-G	○ Stock	S4	○ Desarme	RC-DE
○ Cilindrado 4 rodillos	C01	⌈ Expedición con el pedido	M2	○ Descarga y ensayo de funcionamiento	RC-DC
○ Punteo, refuerzo y estructura	C02,C03			⌈ PH lavado y secado	RC-PH
○ Soldadura longitudinal	C04			○ Recarga por familia	RC-PVGA/Q
○ Soldadura circ. Casquetes AL-1C	C05			○ Ensamblado y presurización	RC-EN
○ Inspección de costuras	C06			○ Peso y hermeticidad	RC-EN
○ Prueba hidráulica 4,0 MPa	C07			○ Retoque y etiquetado	RC-EP
○ Marcado	C08			⌈ Para entregar	RC-EP
○ Espera de retiro	C12			⌈ Despacho	RC-2
⌈ Pintura terciada (P6 -> P8)	-				
○ Carga de polvo	T02				
○ Armado de ruedas y manguera	T12				
○ Presurización y etiquetado	T13				
⌈ Carros terminados	PTC				
○ Expedición	P9				

Fecha	Nombre	Propietario	Reemplaza a / Reemplazado por
30/09/26	Claude Code	FLAMA S.A.	-
Revisó	Aprobó	Denominación	Material
		Flujo de operaciones	-
Escala	Método de proyección	Flujo de operaciones	
1:200	ISO E		
Unidades	Formato	Diagrama de proceso	
Cotas en m	A0		
Secuencia de operaciones por sección - año 10		Edición	
		0	
		30/09/2026	
		Hoja	
		1 / 1	
		es	
		Nº de plano	
		FL_PI_02	