
FL_PI10_01 – PLANTA GENERAL E IMPLANTACIÓN, ZONAS Y SUPERFICIES

Calle al norte: administración y servicios al personal al norte de la nave (croquis del usuario). Cada m² de la nave tiene código y nombre (verificado).

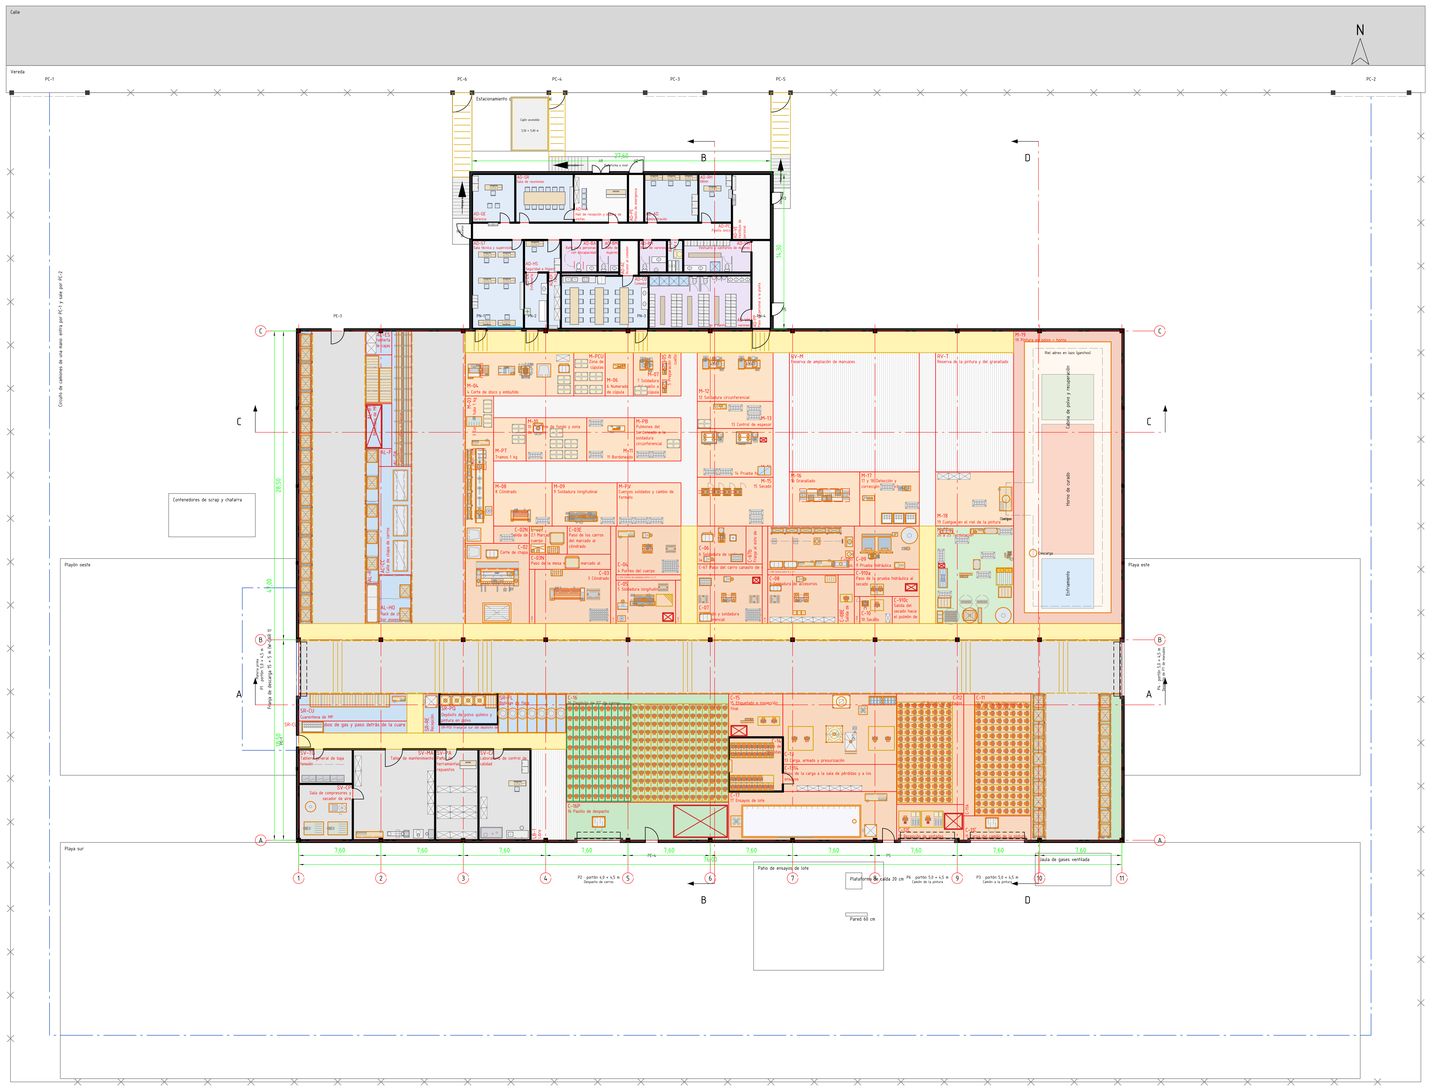

Zonas de la nave y del anexo (m² del plano y m² que pide la fuente)

Código	Zona	m²	Fuente
AL-RI	Rack selectivo RI, 4 niveles	29,7	–
AL-V	Franja del muro oeste	2,7	–
AL-AB	Estacionamiento de los carros de abastecimiento	4,4	–
AL-RC	Racks de carros	14,9	14,7
AL-RT	Rehenidos de MP	10,0	6,0
AL-PV	Pilas de pallets vacíos	10,8	–
AL-ES	Estantería de cajas	5,3	–
AL-HO	Rack de chapas por espesor	13,5	–
AL-CC	Calle de chapa de carros	30,0	20,0
AL-F	Franja detrás del cantilever	2,0	–
AL-CA	Cantilever de caños y barras	22,5	–
SR-CU	Cuarentena de MP	25,0	25,0
SR-CU0	Jaula de fubos de gas y paso detrás de la cuarentena	11,0	–
SR-RE	Recepción	5,4	–
SR-PQ	Depósito de polvo químico y pintura en polvo	15,1	–
SR-PQ1	Franja al sur del depósito de polvo	4,3	–
SR-FL	Bobinas de flejes	22,7	22,0
M-04	4 Corte de disco y embutido	40,0	26,0
M-PCU	Zona de cúpulas	11,6	–
M-06	6 Numerado de cúpula	10,4	2,3
M-07	7 Soldadura del cuello a la cúpula	10,0	5,3
M-05	5 Preparación de cuello	7,6	4,5
M-03	3 Corte de tubo 1 kg	35,4	25,5
M-PT	Tramos 1 kg	12,0	–
M-10	10 Encastre de fondo y zona de fondos	22,4	3,6
M-11	11 Bordoneado	17,6	3,6
M-PB	Pulmones del bordoneado a la soldadura circunferencial	17,2	–
M-08	8 Cilindrado	21,6	7,3
M-09	9 Soldadura longitudinal	24,0	8,4
M-PV	Cuerpos soldados y cambio de formato	23,6	–
M-12	12 Soldadura circunferencial	31,5	17,5
M-13	13 Control de espesor	17,5	2,3
M-14	14 Prueba hidráulica	31,5	14,1
M-15	15 Secado	31,5	6,0
M-16	16 Granallado	32,5	27,4
M-17	17 y 18 Detección y corrección de defectos	27,5	9,2
M-18	19 Cuelgue en el riel de la pintura	36,0	–
M-19	19 Pintura en polvo + horno	270,0	270,0
M-20	20 a 25 Terminación	64,8	47,0
C-02	2 Corte de chapa	43,7	44,0
C-02N	Salida de desarrollos de la guillotina a manuales	5,3	–
C-021	21 Marcado del cuerpo	9,1	9,0
C-03	3 Cilindrado	35,0	35,0
C-03N	Paso de la mesa móvil del marcado al cilindrado	10,5	–
C-03W	Franja entre el corte y el cilindrado	2,5	–
C-03E	Paso de los carros del marcado al cilindrado	10,4	–
C-05	5 Soldadura longitudinal	22,0	22,0
C-04	4 Punteo del cuerpo	27,0	27,0
C-45	Cortina de soldadura entre 3 y 4/5	4,5	–
C-45b	Cortina de soldadura entre 4 y 5	3,0	–
C-45c	Franja al este de la soldadura longitudinal	2,0	–
C-07	7 Armado y soldadura circunferencial	27,0	27,0
C-06	6 Soldadura de cupla en la cúpula	15,8	16,0
C-67	Paso del carro canasto de cúpulas 6 a 7	6,0	–
C-67b	Franja al este de la cupla	5,2	–

Código	Zona	m²	Fuente
C-08	8 Soldadura de accesorios	29,2	29,0
C-081	8.1 Fabricación de accesorios	32,0	32,0
C-T8	Cortina de soldadura entre 7 y 8	4,5	–
C-88	Cortina entre 8 y 8.1	4,0	–
C-08E	Salida de los carros sobre su juego provisorio	6,8	–
C-10	10 Secado	7,5	7,5
C-09	9 Prueba hidráulica	24,0	22,0
C-910a	Paso de la prueba hidráulica al secado	15,0	–
C-910b	Franja junto al secado	1,2	–
C-910c	Salida del secado hacia el pulmón de despacho	6,2	–
C-17	17 Ensayos de lote	69,8	70,0
C-14	14 Sala del ensayo de pérdidas	25,0	25,0
C-15	15 Etiquetado e inspección final	20,0	9,0
C-13	13 Carga, armado y presurización	68,2	60,0
C-13¼	Paso de la carga a la sala de pérdidas y a los ensayos	26,2	–
C-12	12 Pulmón de pintados	63,2	–
C-12C	12 Recepción de pintados	20,5	–
C-11A	11 Pasillo de los carros a la puerta	11,2	–
C-11	11 Pulmón de despacho a la pintura tercerizada	58,5	57,0
C-11C	11 Carga del camión a la pintura	13,9	–
C-16	16 Depósito de PT de carros	150,0	150,0
C-16P	16 Pasillo de despacho	52,5	50,0
PT-M	Almacén de PT de manuales	17,5	–
PT-M2	Almacén de PT de manuales	28,4	–
SV-CP	Sala de compresores y secador de aire	26,0	–
SV-TG	Tablero general de baja tensión	16,0	–
SV-MA	Taller de mantenimiento	63,8	–
SV-PA	Pañol de herramientas y repuestos	33,6	–
SV-CA	Laboratorio de control de calidad	40,3	–
LB-1	Libre	27,7	–
RV-M	Reserva de ampliación de manuales	132,0	–
RV-T	Reserva de la pintura y del granallado	79,2	–
AD-GE	Gerencia	18,0	–
AD-SR	Sala de reuniones	24,3	–
AD-HA	Hall de recepción y espera de visitas	22,5	–
AD-PE	Pasillo de emergencia	6,8	–
AD-AD	Administración	22,5	–
AD-RH	RRHH	14,0	–
AD-VE	Vestíbulo de personal	22,0	–
AD-PC	Pasillo único	38,4	–
AD-ST	Sala técnica y supervisión	39,4	–
AD-HS	Seguridad e Higiene	10,2	–
AD-EN	Enfermería	11,4	–
AD-EP	Pañol de EPP	6,2	–
AD-BA	Baño para personas con discapacidad	10,2	–
AD-BM	Baño de mujeres	6,0	–
AD-AC	Acceso al comedor	5,9	–
AD-BH	Baño de varones	7,8	–
AD-LI	Limpieza y termofanque	4,5	–
AD-VM	Vestuario y sanitarios de mujeres	18,9	–
AD-CO	Comedor	39,7	–
AD-VH	Vestuario y sanitarios de varones	46,5	–
AD-PP	Paso de personal a la planta	14,8	–
AD-PL1	Plenum sanitario	1,6	–
AD-PL2	Plenum sanitario	3,1	–

Portones de la nave y del predio

Portón	Uso	Ancho (m)
P1	Materia prima: del playón oeste al pasillo principal	5,0
P2	Despacho de carros (depósito 16, liberados)	4,0
P3	Carga del camión a la pintura tercerizada (puesto 11)	5,0
P6	Descarga de los carros pintados (puesto 12)	5,0
P4	Playa este: despacho de PT de manuales (al final del pasillo)	5,0
PC-1	Entrada de camiones, 7,0 m (criterio: semirremolque)	7,0
PC-2	Salida de camiones, 7,0 m (circuito de una mano)	7,0
PC-3	Estacionamiento, 5,5 m	5,5
PC-4	Peatonal: visitas, gerencia y oficinas	1,5
PC-5	Peatonal: operarios (ingreso lateral este)	1,8
PC-6	Peatonal: supervisión, PCP, calidad y HyS (oeste)	1,8

Superficies por destino

Destino	m²	% de la nave
Almacén de MP y recepción	229,3	6,4
Manuales 1 a 10 kg	461,4	12,9
Pintura	270,0	7,6
Terminación de manuales	64,8	1,8
Carros 25 a 100 kg	736,1	20,6
Depósitos de producto terminado	248,4	7,0
Servicios técnicos (mantenimiento, calidad, aire, energía)	179,8	5,0
Libre / reserva	238,9	6,7
Pasillos y sendas	1.143,4	32,0
TOTAL NAVE (76,0 × 47,0 m)	3.572,0	100,0
Anexo de administración y servicios (27,6 × 14,3 m)	394,7	–

Referencias

- Almacén de MP y recepción
- Manuales 1 a 10 kg
- Pintura
- Terminación de manuales
- Carros 25 a 100 kg
- Depósitos de producto terminado
- Servicios técnicos (mantenimiento, calidad, aire, energía)
- Oficinas
- Vestuarios y sanitarios
- Libre / reserva
- Carril del autoelevador (5,0 m)
- Senda peatonal demarcada
- Pasillo de operarios y carros a mano

Criterios

Nave de 76,0 × 47,0 m, 10 vanos de 7,6 m, pórticos de 18,5 × 28,5 m con la fila de columnas en el borde norte del carril del autoelevador (ninguna columna dentro de un carril).
Pasillo principal: carril de 5,0 m (Hilti CFC150, W-CAR) + senda de 1,5 m con baranda y cruces.
Almacén con dos pasillos de 5,0 m (AL-A junto a las máquinas de corte, AL-B entre racks).
Portones de la nave (croquis de circuitos de carros): P1 MP 5,0 m (oeste, con la franja de descarga de 15 × 5 m y la cuarentena pegada); P4 PT de manuales 5,0 m (este); P2 despacho de carros 4,0 m; P3 camión a la pintura 5,0 m y P6 regreso de los pintados 5,0 m (sur); P5 patio de ensayos; PE de emergencia.
Predio con cerco: PC-1 entrada y PC-2 salida de camiones (circuito de una mano); PC-3 estacionamiento y PC-4 a PC-6 accesos peatonales del croquis de oficinas. Cortes A–A y B–B en P1_PI10_06.
Carros en planta según el lexrd de carros: 100 en el pulmón de despacho, 100 pintados, 39 en la sala de pérdidas, 180 rehenidos y 100 liberados. PT de manuales en racks (M-MAN): 100 posiciones de pallet (70 de PT y 17 reversibles de V-ALM). Almacén de MP por secciones de V-ALM (FL_PI10_04).
Reservas (RV) y LB1: lugar para la máquina siguiente de los puestos de manuales al 92-97 % en 2035 (M-MAN) y el espacio libre del croquis. El largo de la nave lo fijan la fila de carros más la terminación y la pintura (norte) y los puestos 11 a 17 de carros más el PT (sur).

	Fecha	Nombre
Dibujó	15/10/26	Claude Code
Revisó		
Aprobó		

Escala	1:200
Método de proyección	ISO E
Unidades	Cotas en m
Formato	A0
Propietario	FLAMA S.A.
Denominación	Planta general e implantación
	Layout 2035 v10 – zonas codificadas y áreas
Tipo de documento	Plano de planta
Reemplaza a / Reemplazado por	–
Material	–
Edición	0
Fecha de emisión	15/10/2026
Hoja	1 / 6
Idioma	es
N° de plano	FL_PI10_01