

FL_PI10_04 – ALMACÉN DE MATERIA PRIMA, RECEPCIÓN Y LOCALES DEL ÁNGULO SUDOESTE

Secciones de X-ALM v5 con su color; espacios de W-CAR 1 al pie de la letra (cuarentena, retenidos, calle de chapa, racks de carros, franja de descarga).

Portón P1 y franja de descarga, recepción, cuarentena, polvo, fleje y locales del ángulo SO (x −6 a 26; y 0 a 19)

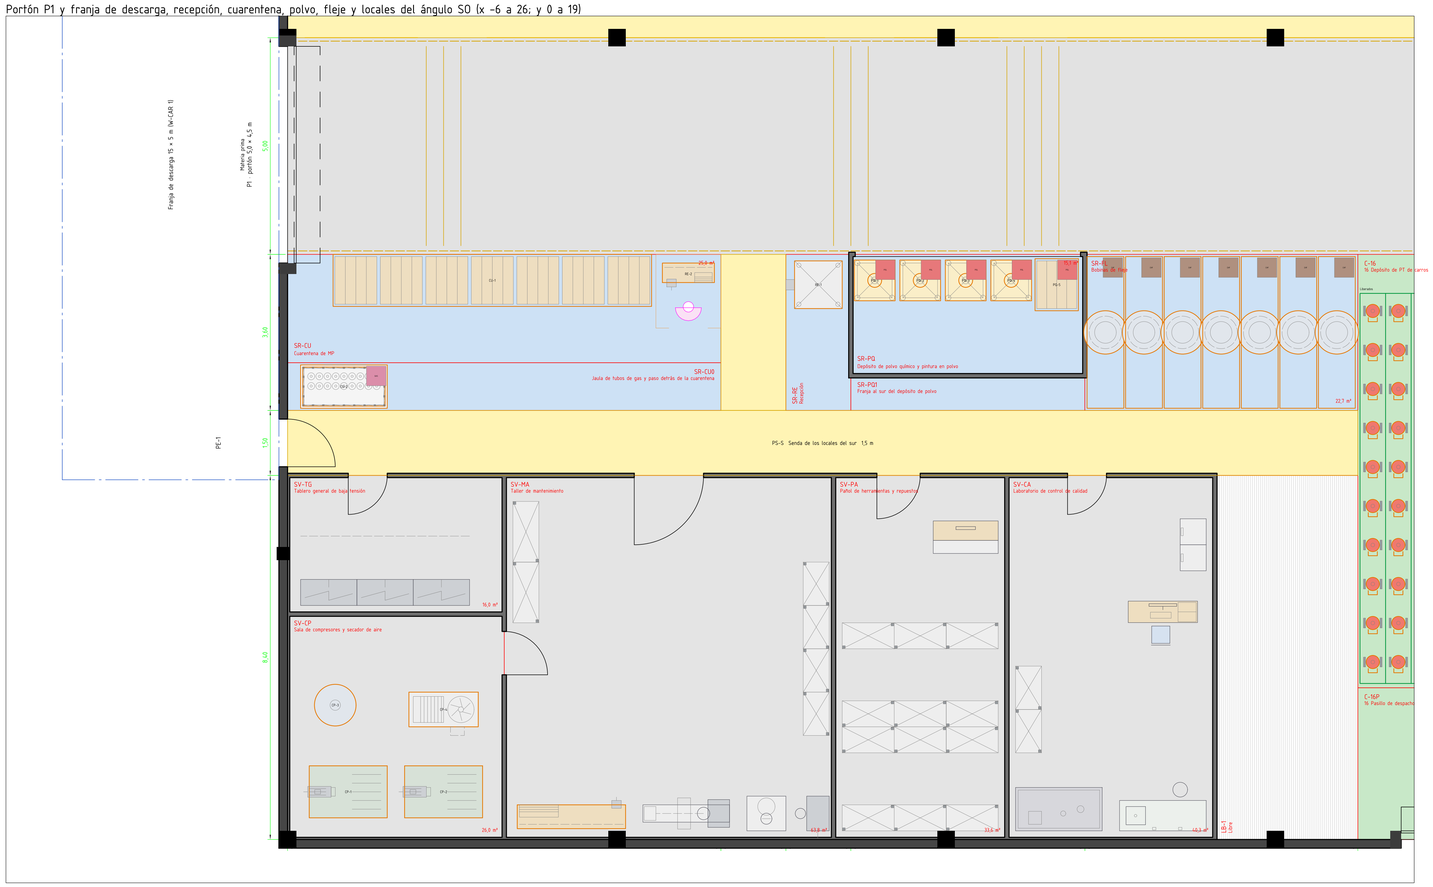

Almacén de MP (x 0 a 15,4; y 20 a 47)

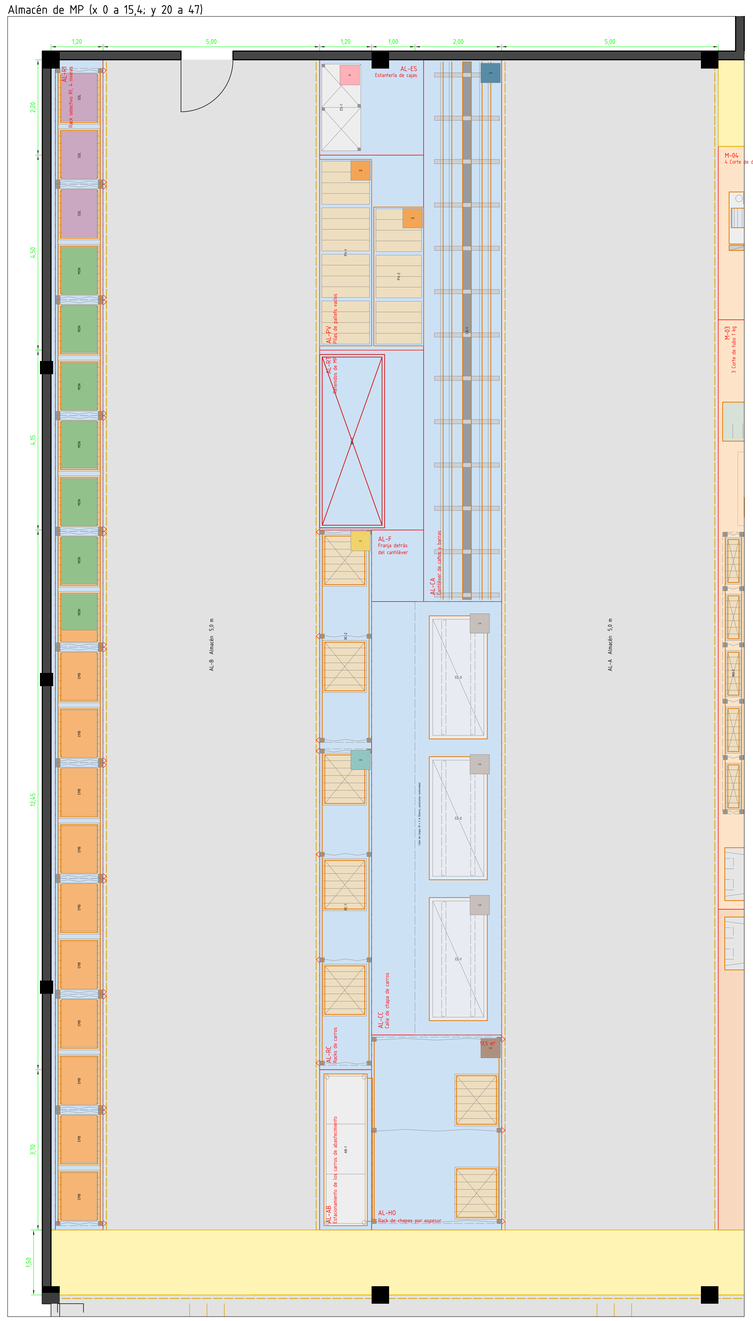

Almacenamiento (cantidades de la fuente)

Sección	Cómo se guarda	Cantidad	Fuente
Rack R1	80 posiciones: 10 módulos de 2,67 m × 4 niveles × 2 pallets, por secciones	80 pos.	X-ALM
Racks de carros	casquetes y cuplas 7,3 × 1,2 m (12 pos.) e insumos 4,9 × 1,2 m (8 pos.), 2 niveles	20 pos.	W-CAR 1
Hojas de manuales	rack por espesor, 4 niveles, 3 bocas (1,25, 1,6 y 2,0 mm)	12 paq.	W-MAN 1
Calle de chapa de carros	10 × 2 m, 3 posiciones de 3,0 × 1,5 m, 2 paquetes de alto	20 m²	W-CAR 1
Cantilever	frente de 12,4 m, 5 niveles, brazos de 1,2 m	11 pos.	X-ALM
Bobinas de fleje	21 posiciones en 7 calles de 3 (pallet en piso, 1 nivel)	21 pos.	X-ALM P05-P11
Polvo químico y pintura	big bags en el piso de a 2 (4 pilas) y 1 pila de 2 pallets, local cerrado	10 u	W-CAR 1 / X-ALM
Pallets vacíos	7 pilas en piso (sección embalaje)	7 pilas	X-ALM
Identificación e insumos chicos	estantería de cajas de 5 niveles, identificación bajo llave	15 lug.	X-ALM
Cuarentena	10 × 2,5 m: 7 pallets, mesa de inspección y 1,3 m de circulación, pegada a P1	25 m²	W-CAR 1
Retenidos de MP	4 × 1,5 m demarcado en rojo, 3 pallets	6 m²	W-CAR 1
Jaula de tubos de gas	N2 y Ar/CO2, llenos separados de vacíos, ventilada	2 m²	W-CAR 1
Recepción	balanza 1,20 × 1,20 m y mesa de inspección 1,2 × 0,6 m	6,8 m²	W-MAN 1 / W-CAR 1
Carros de abastecimiento	3 carros FCEP1P520 (2 de carros y 1 de manuales)	3,5 m²	W-CAR 1 / W-MAN 1
Franja de descarga (playón)	15 × 5 m frente a P1, línea discontinua, compartida con manuales	75 m²	W-CAR 1
Jaula de gases (exterior)	packs de Arcal 21 y de N2 con manifold, al sur.	21 m²	W-MAN 1
Revendidos	van al rack de PT (sección «almacén de producto terminado» de X-ALM)	17 pos.	X-ALM

Secciones del almacén (X-ALM v5; colores del croquis del usuario)

- PT — Almacén de producto terminado (revendidos) (17 pos.): Rack de PT de matafuegos terminados (PTM-1): la sección es de producto terminado
- EMB — Embalaje (50 pos.): R1: cajas de cartón, 41 pos.; pilas de pallets vacíos en piso, 7; estantería (etiquetas de caja), 2
- MON — Insumos de montaje (manuales) (31 pos.): R1: 27 pos.; estantería (asientos M22), 4
- SOL — Insumos de soldadura y superficie (12 pos.): R1: alambre y granalla
- CAS — Rack de casquetes y cuplas (carros) (11 pos.): Rack propio de W-CAR: 12 posiciones
- ICA — Rack de insumos de montaje (carros) (7 pos.): Rack propio de W-CAR: 8 posiciones
- POL — Depósito de polvo químico (8 pos.): Local cerrado: 4 pilas de 2 big bags y 1 pila de 2 pallets de pintura (sin los polvos de recargas)
- CHP — Chapa y fleje (manuales) (28 pos.): Rack de chapas por espesor y 21 bobinas en sus calles
- CCH — Calle de chapa (carros) (3 pos.): Calle de 10 × 2 m con 3 posiciones (W-CAR)
- CAN — Cantilever de caños y barras (11 pos.): Cantilever de 12,4 m
- CE — Identificación (9 pos.): Estantería de cajas bajo llave
- GAS — Jaula de gases (12 pos.): Jaula exterior (packs) y jaula de tubos de la cuarentena

Pasillos de 5,0 m para el Heli CPCD50 (W-CAR 1). Los racks de carros, los retenidos, las pilas de pallets y la estantería miran a AL-B; el rack de chapas, la calle de chapa y el cantilever miran a AL-A (W-CAR 1: «la calle de chapa y los racks quedan del otro lado del pasillo»). El procesado de X-ALM no va al almacén: W-MAN lo guarda en los carros de 12 cajones al lado de cada puesto. Los insumos de recargas no van.

	Fecha	Nombre
Dibujó	15/10/26	Claude Code
Revisó		
Aprobó		

Escala: 1:50 — Método de proyección: ISO E — Unidades: Cotas en m — Formato: A0

Propietario: FLAMA S.A.

Denominación: Almacén de MP y recepción

Layout 2035 v10 – X-ALM v5 con el autoelevador de W-CAR

Tipo de documento: Plano de detalle

Reemplaza a / Reemplazado por: –

Material: –

Edición: 0 — Fecha de emisión: 15/10/2026

Hoja: 4 / 6 — Idioma: es

Nº de plano: FL_PI10_04