

FL_PI10_06 – CORTES DE LA NAVE A-A, B-B, C-C Y D-D

Alturas con fuente (ET, cotizaciones, W-CAR, hoja de especificaciones); lo que no tiene alto en ninguna fuente va marcado «s/d». Ubicación de los cortes en la planta de la derecha y en FL_PI10_01.


CORTE A-A (longitudinal por y = 12,5 m, mirando al norte)

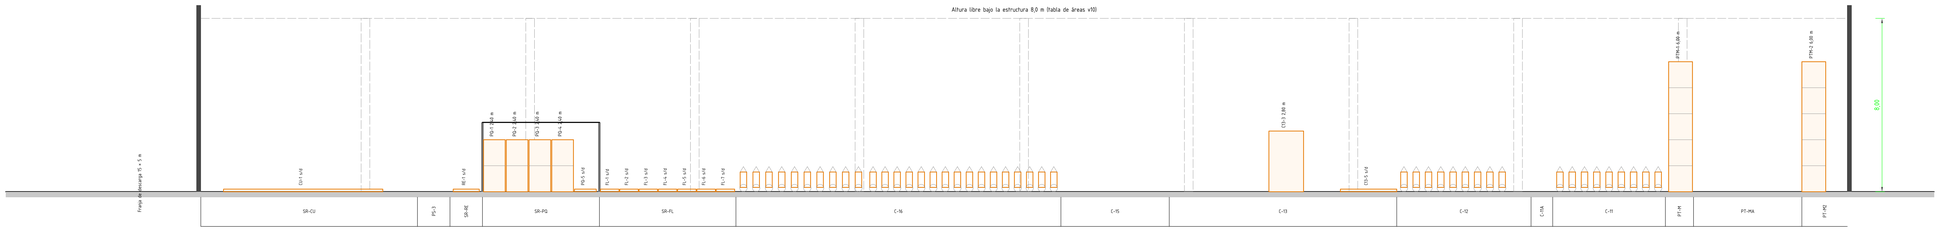


Ubicación de los cortes (1:500)

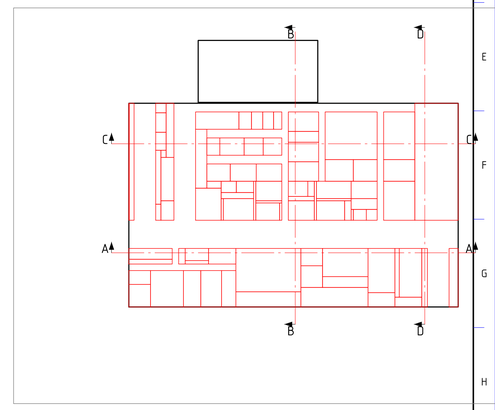


CORTE C-C (longitudinal por y = 37,65 m, mirando al norte)

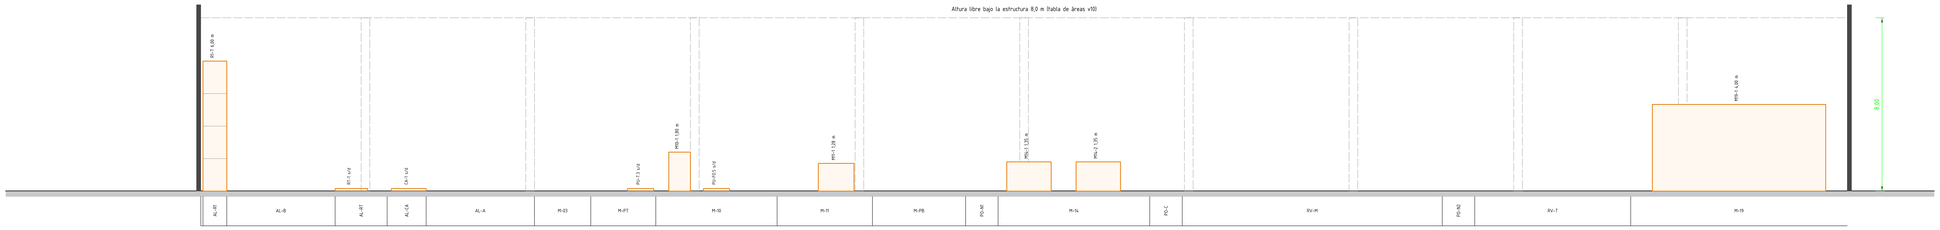

CORTE B-B (transversal por x = 38,4 m, mirando al oeste; el norte a la derecha)

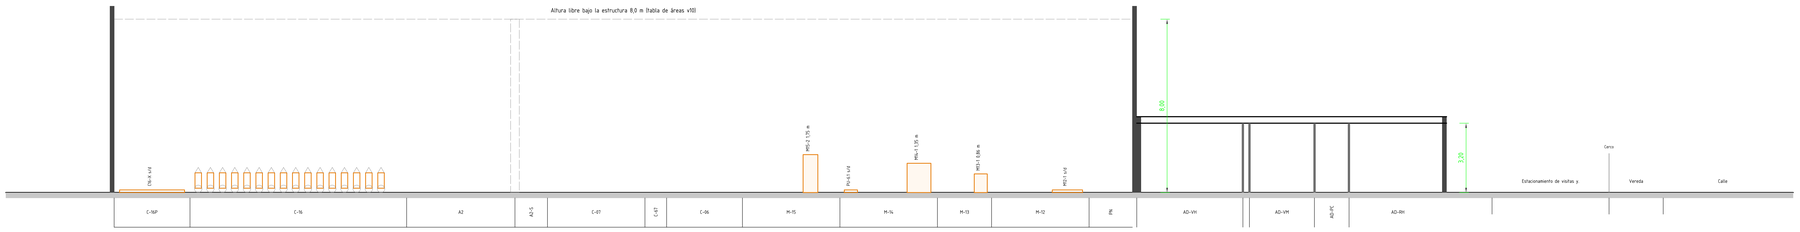

CORTE D-D (transversal por x = 68,3 m, mirando al oeste; el norte a la derecha)

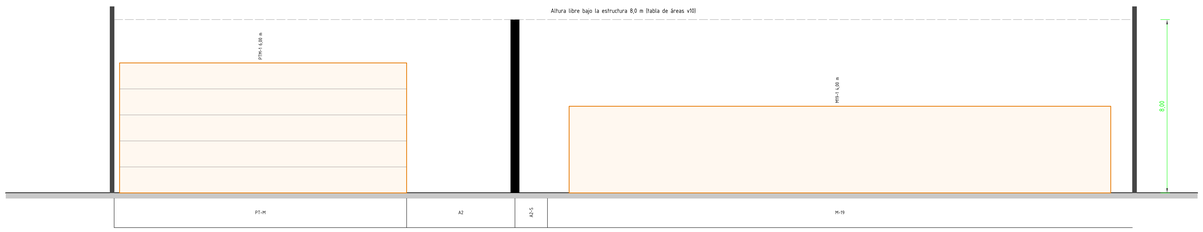

Alturas dibujadas y su fuente

Elemento	Alto (m)	Fuente
Anexo	3,20	Locales de servicio de 3,20 m (tabla de áreas v10; Dec. 351/79 cap. 5: 3 m como mínimo)
Big bags	2,40	W-CAR 1: big bag de 1,2 m de alto, apilado de a 2
C13-3	2,80	W-CAR 13: bastidor de 2,8 m
Carros	1,16	Hoja de especificaciones «Polvos carros»: carro de 50 kg, 1160 mm (25 kg 1085; 100 kg 1360)
M10-1	1,80	ET Del Fabro: 1800 mm
M11-1	1,28	Presupuesto Pilman SWM-400: 1280 mm
M19-1	4,00	ET línea Firesafer: 25 × 8 × 4 m
Mesas y bancos	0,86	W-CAR 1: mesa de 86 cm
Nave	8,00	Altura libre de la nave: 8,0 m (tabla de áreas v10; Dec. 351/79 cap. 5)
Prueba hidráulica	1,35	Catálogo Firesafer FS-JD12A: 1350 mm
Rack RT	6,00	Criterio: la carga de arriba llega a la elevación máxima del Heli CPCD50; 6 m (W-CAR 1)
Racks de PT	6,00	Criterio: 5 niveles hasta la elevación máxima del Heli CPCD50; 6 m (W-CAR 1)
SR-PG	3,20	Locales de servicio de 3,20 m (tabla de áreas v10; Dec. 351/79 cap. 5: 3 m como mínimo)
Secadoras	1,75	ET secadora Yukon: 1750 mm

Portones: 4,5 m de alto (criterio: caja de camión de hasta 4,1 m, Ley 24.449 art. 53); P1 y P4 de 5,0 m de ancho, P2 de 4,0 m, P3 y P6 de 5,0 m (croquis de circuitos de carros del usuario).
Los equipos sin alto en ninguna fuente (guillotina, roladora W12, viradores, soldadoras, bobinas, carros de planta, pallets en piso) se marcan «s/d» se complefan con el plano del fabricante.

	Fecha	Nombre
Dibujó	15/10/26	Claude Code
Revisó		
Aprobó		

Escala 1:100 — Método de proyección ISO E

Unidades: Cotas en m — Formato: A0

Propietario: FLAMA S.A.

Denominación: Cortes de la nave

layout 2035 v10 – cortes A-A a D-D con las alturas de las fuentes

Tipo de documento: Plano de cortes

Reemplaza a / Reemplazado por: –

Material: –

Edición: 0 — Fecha de emisión: 15/10/2026

Hoja: 6 / 6 — Idioma: es

N° de plano: FL_PI10_06