FL_PI10_01 - PLANTA GENERAL E IMPLANTACIÓN, ZONAS Y SUPERFICIES

Calle al norte: administración y servicios al personal al norte de la nave (croquis del usuario). Cada m² de la nave tiene código y nombre (verificado).

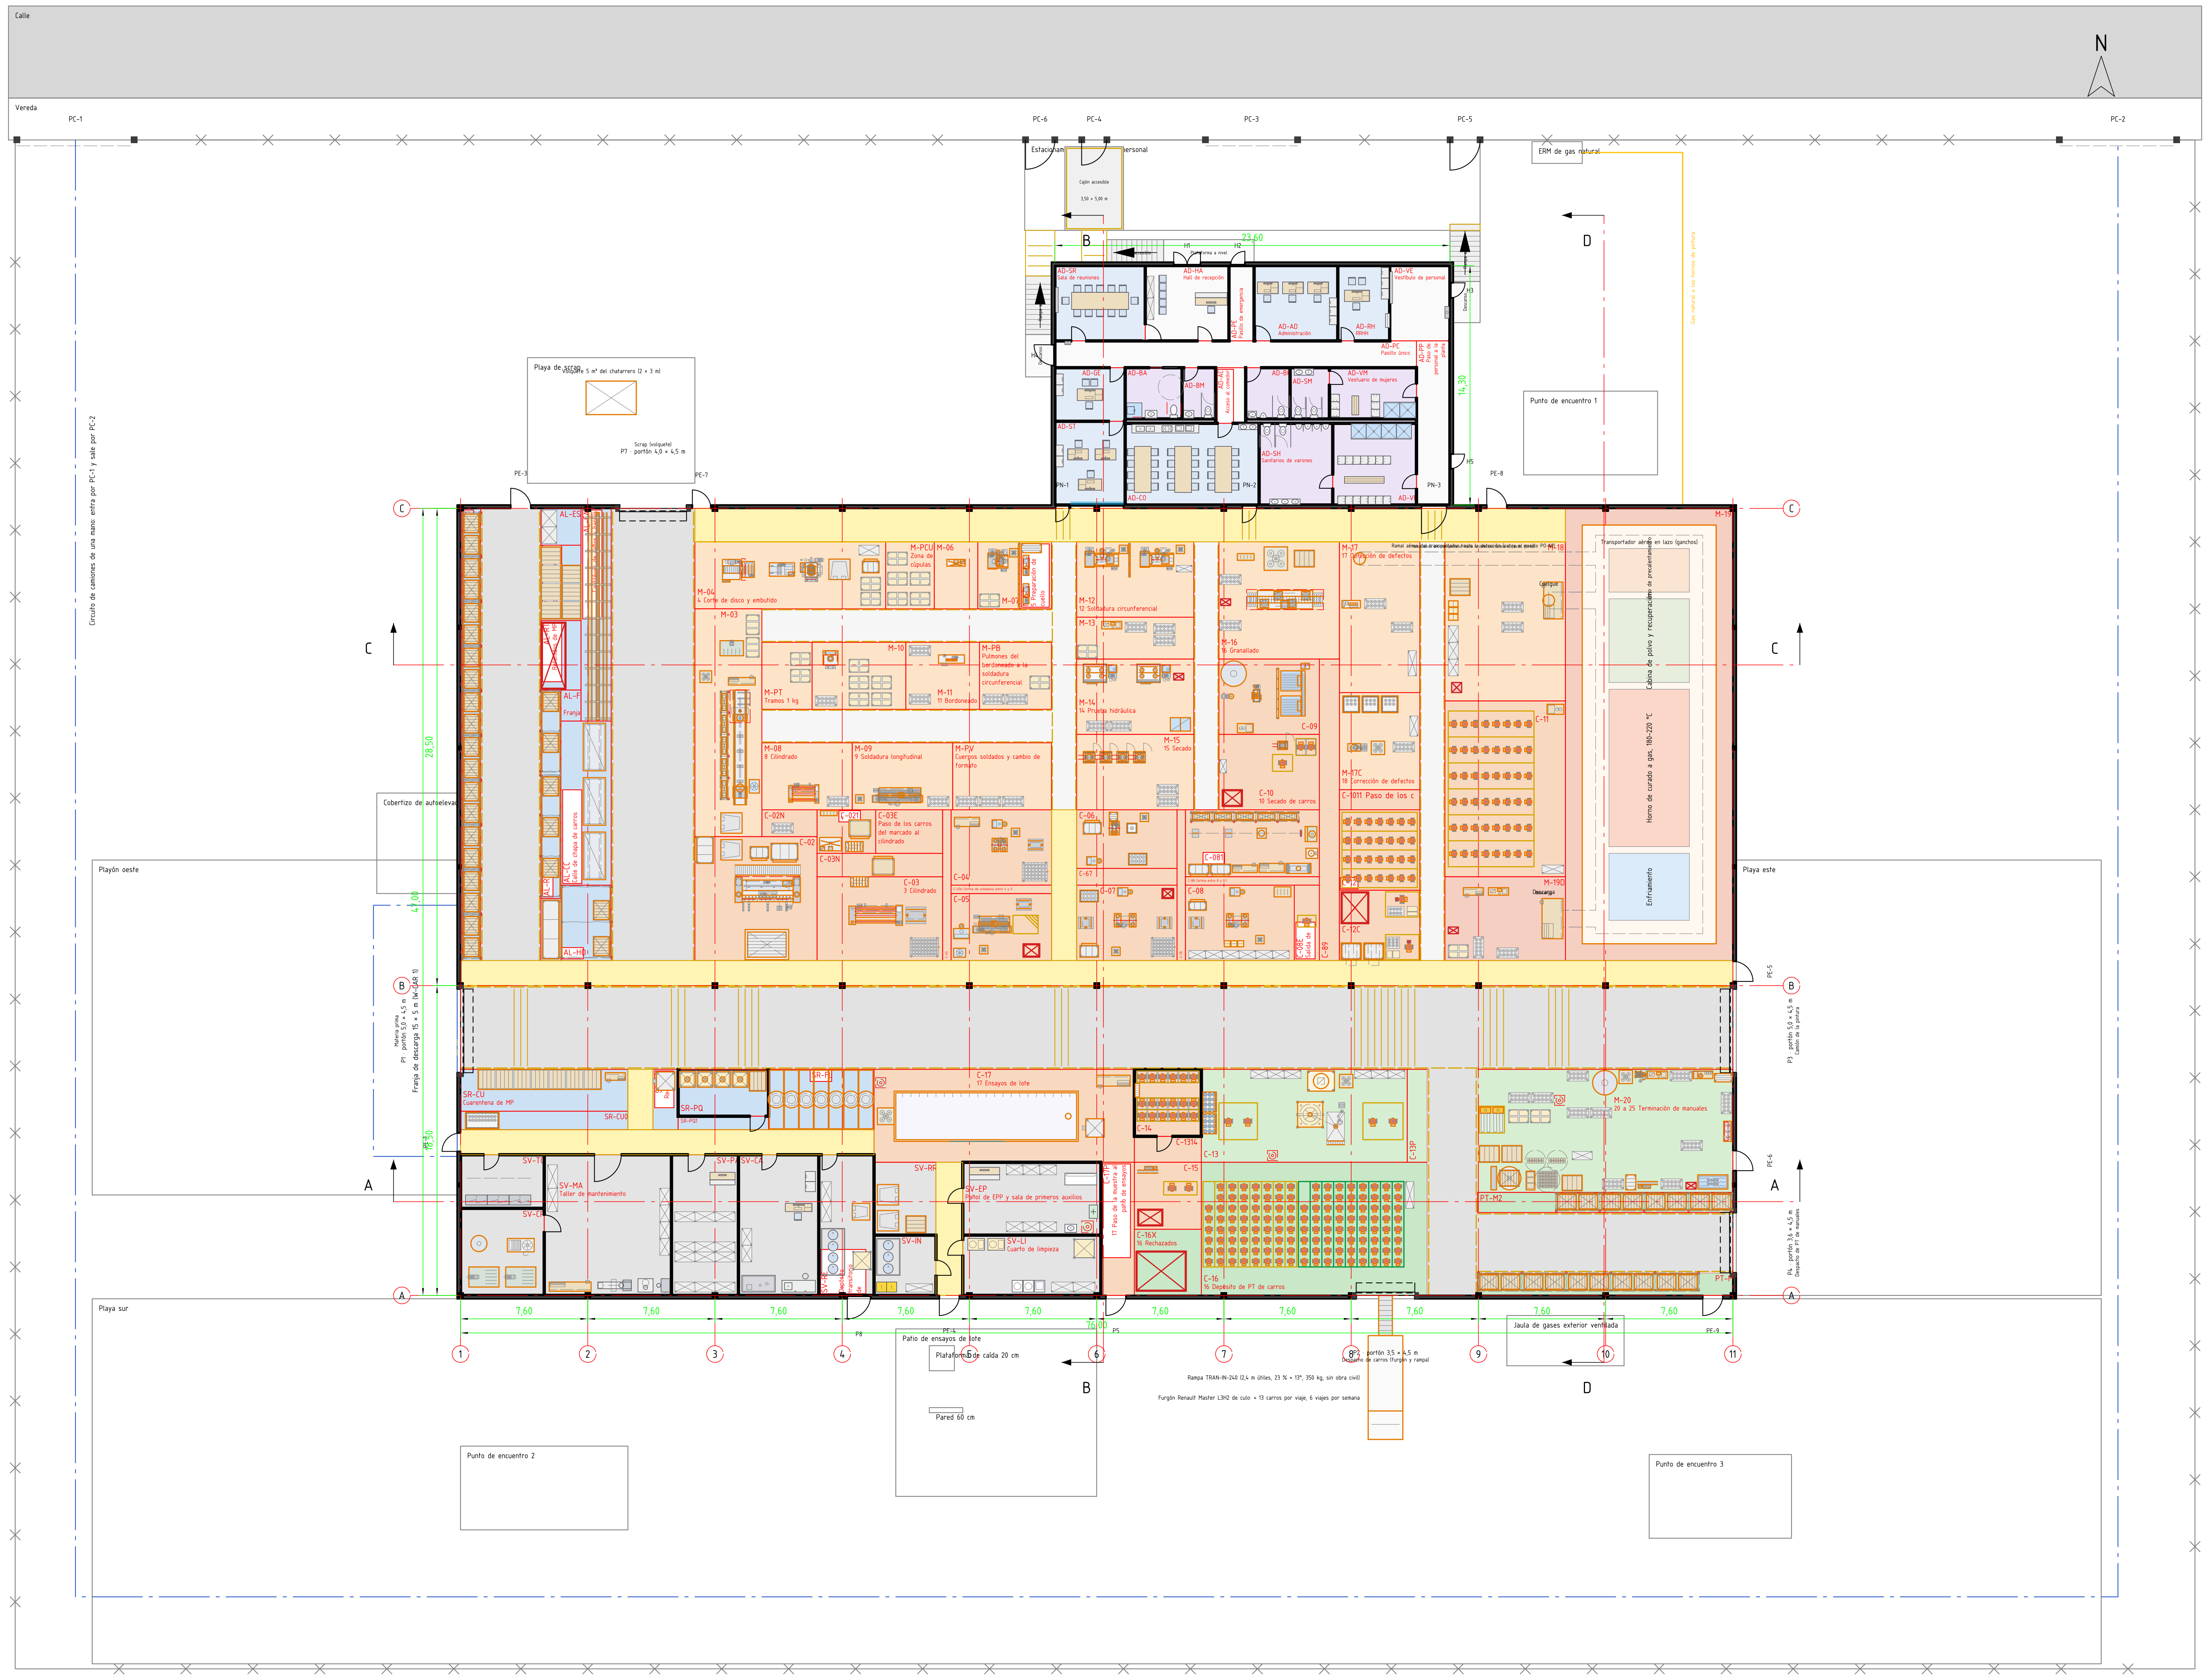

Zonas de la nave y del anexo (m² del plano y m² que pide la fuente)

Código	Zona	m²	Fuente
AL-R1	Rack selectivo R1, 4 niveles	29,7	-
AL-W	Franja del muro oeste	2,7	-
AL-AB	Estacionamiento de los carros de abastecimiento	4,4	-
AL-RC	Racks de carros	14,9	14,7
AL-RT	Retenidos de MP	10,0	6,0
AL-PV	Pilas de pallets vacíos	10,8	-
AL-ES	Estantería de cajas	5,3	-
AL-HO	Rack de chapas por espesor	13,5	-
AL-CC	Calle de chapa de carros	29,4	20,0
AL-F	Franja detrás del cantiléver	2,2	-
AL-CA	Cantiléver de caños y barras	22,9	-
SR-CU	Cuarentena de MP	25,0	25,0
SR-CU0	Jaula de tubos de gas y paso detrás de la cuarentena	11,0	-
SR-RE	Recepción	5,4	-
SR-PQ	Depósito de polvo químico y pintura en polvo	15,1	-
SR-PQ1	Franja al sur del depósito de polvo	4,3	-
SR-FL	Bobinas de fleje	22,7	22,0
M-04	4 Corte de disco y embutido	45,6	26,0
M-PCU	Zona de cúpulas	11,6	-
M-06	6 Numerado de cúpula	10,4	2,3
M-07	7 Soldadura del cuello a la cúpula	10,0	5,3
M-05	5 Preparación de cuello	7,6	4,5
M-03	3 Corte de tubo 1 kg	54,4	25,5
M-PT	Tramos 1 kg	12,0	-
M-10	10 Encastre de fondo y zona de fondos	22,4	3,6
M-11	11 Bordoneado	17,6	3,6
M-PB	Pulmones del bordoneado a la soldadura circunferencial	17,2	-
M-08	8 Cilindrado	21,6	7,3
M-09	9 Soldadura longitudinal	24,0	8,4
M-PV	Cuerpos soldados y cambio de formato	23,6	-
M-12	12 Soldadura circunferencial	31,5	17,5
M-13	13 Control de espesor	17,5	2,3
M-14	14 Prueba hidráulica	31,5	14,1
M-15	15 Secado	31,5	6,0
M-16	16 Granallado	50,4	27,4
M-17	17 Detección de defectos	43,2	9,2
M-17C	18 Corrección de defectos	27,8	-
M-18	19 Cuelgue en el transportador de la pintura	68,4	-
M-19	19 Pintura en polvo + horno	270,0	270,0
M-19D	19 Descarga de la pintura	36,0	-
C-13	13 Carga, armado y presurización de carros	68,3	60,0
C-13P	Paso de los carros pintados y de los cilindros a la carga y al depósito 16	6,7	-
M-20	20 a 25 Terminación de manuales	112,1	47,0
C-02	2 Corte de chapa	54,0	44,0
C-02N	Salida de desarrollos de la guillotina a manuales	5,3	-
C-021	2.1 Marcado del cuerpo	9,1	9,0
C-03	3 Cilindrado	37,5	35,0
C-03N	Paso de la mesa móvil del marcado al cilindrado	10,5	-
C-03E	Paso de los carros del marcado al cilindrado	10,4	-
C-05	5 Soldadura longitudinal	24,0	22,0
C-04	4 Punteo del cuerpo	27,0	27,0
C-45	Cortina de soldadura entre 3 y 4/5	4,5	-
C-45b	Cortina de soldadura entre 4 y 5	3,0	-
C-07	7 Armado y soldadura circunferencial	27,0	27,0

Código	Zona	m²	Fuente
C-06	6 Soldadura de cupla en la cúpula	21,0	16,0
C-67	Paso del carro canasto de cúpulas de 6 a 7	6,0	-
C-08	8 Soldadura de accesorios	29,2	29,0
C-081	8.1 Fabricación de accesorios	32,0	32,0
C-78	Cortina de soldadura entre 7 y 8	4,5	-
C-88	Cortina entre 8 y 8.1	4,0	-
C-08E	Salida de los carros sobre su juego provisorio	6,8	-
C-09	9 Prueba hidráulica de carros	27,0	22,0
C-10	10 Secado de carros	27,0	7,5
C-89	Paso de los carros del 8 a la prueba hidráulica y de los secos al pulmón 11	21,6	-
C-12C	12 Recepción de pintados	20,2	-
C-12	12 Pulmón de pintados	23,0	14,0
C-1011	Paso de los carros secos al pulmón 11	5,8	-
C-11	11 Pulmón de despacho a la pintura tercerizada	75,6	24,0
C-17	17 Ensayos de lote	86,3	70,0
C-1314	Paso de la carga a la sala de pérdidas, a los ensayos y al etiquetado	6,2	-
C-14	14 Sala del ensayo de pérdidas	16,0	15,0
C-17P	17 Paso de la muestra al patio de ensayos	15,9	-
C-15	15 Etiquetado e inspección final	16,0	9,0
C-16X	16 Rechazados	15,8	6,0
C-16	16 Depósito de PT de carros	107,3	66,0
PT-M	Depósito de PT unificado	20,6	-
PT-M2	Depósito de PT unificado	18,3	-
SV-CP	Sala de compresores y secador de aire	26,0	-
SV-TG	Tablero general de baja tensión	16,0	-
SV-MA	Taller de mantenimiento	63,8	-
SV-PA	Pañol de herramientas y repuestos	33,6	-
SV-CA	Laboratorio de control de calidad	40,3	-
SV-RE	Depósito transitorio de residuos especiales	27,7	-
SV-IN	Depósito de aceites e inflamables	13,3	-
SV-RR	Residuos reciclables y asimilables	16,1	-
SV-LI	Cuarto de limpieza	29,7	-
SV-EP	Pañol de EPP y sala de primeros auxilios	35,9	-
AD-SR	Sala de reuniones	24,3	-
AD-HA	Hall de recepción	22,5	-
AD-PE	Pasillo de emergencia	6,8	-
AD-AD	Administración	22,5	-
AD-RH	RRHH	14,0	-
AD-VE	Vestíbulo de personal	16,2	-
AD-PC	Pasillo único	34,6	-
AD-PP	Paso de personal a la planta	19,6	-
AD-GE	Gerencia	13,4	-
AD-ST	Sala técnica / supervisión	21,0	-
AD-BA	Baño para personas con discapacidad	10,4	-
AD-BM	Baño de mujeres	6,1	-
AD-AC	Acceso al comedor	6,0	-
AD-BH	Baño de varones	8,1	-
AD-SM	Sanitarios de mujeres	7,2	-
AD-VM	Vestuario de mujeres	15,9	-
AD-PL1	Plenum sanitario	1,4	-
AD-PL2	Plenum sanitario	2,7	-
AD-CO	Comedor	39,0	-
AD-SH	Sanitarios de varones	21,5	-
AD-VH	Vestuario de varones	24,4	-

Portones de la nave y del predio

Portón	Uso	Ancho (m)
P1	Materia prima: del playón oeste al pasillo principal	5,0
P2	Despacho de carros: furgón Renault Master L3H2 y rampa TRAN-IN-240	3,5
P3	Camión de la pintura: carros secos (11) y pintados (12)	5,0
P4	Despacho de PT de manuales (pasillo de los racks de 3,6 m)	3,6
P7	Scrap: del pasillo AL-A a la playa con volquete	4,0
PC-1	Entrada de camiones, 7,0 m (criterio: semirremolque)	7,0
PC-2	Salida de camiones, 7,0 m (circuito de una mano)	7,0
PC-3	Estacionamiento, 5,5 m	5,5
PC-4	Peatonal: visitas, gerencia y oficinas	1,5
PC-5	Peatonal: operarios (ingreso lateral este)	1,8
PC-6	Peatonal: supervisión (ingreso oeste)	1,8

Superficies por destino

Destino	m²	% de la nave
Almacén de MP y recepción	229,3	6,4
Manuales 1 a 10 kg	579,8	16,2
Pintura	306,0	8,6
Terminación de manuales	187,0	5,2
Carros 25 a 100 kg	656,4	18,4
Depósitos de producto terminado	162,0	4,5
Servicios técnicos (mantenimiento, calidad, aire, energía)	302,5	8,5
Libre / reserva	0,0	0,0
Pasillos y sendas	1.149,0	32,2
TOTAL NAVE (76,0 × 47,0 m)	3.572,0	100,0
Anexo de administración y servicios (23,6 × 14,3 m)	337,5	-

Referencias

🟦	Almacén de MP y recepción
🟧	Manuales 1 a 10 kg
🟥	Pintura
🟩	Terminación de manuales
🟧	Carros 25 a 100 kg
🟩	Depósitos de producto terminado
⬜	Servicios técnicos (mantenimiento, calidad, aire, energía)
🟦	Oficinas
🟪	Vestuarios y sanitarios
▨	Libre / reserva
⬜	Carril del autoelevador (3,0 a 5,0 m)
🟨	Senda peatonal demarcada
⬜	Pasillo de operarios y carros a mano

Criterios

Nave de 76,0 × 47,0 m, 10 vanos de 7,6 m; pórticos de 18,5 + 28,5 m con la fila de columnas en el borde norte del carril del autoelevador (ninguna columna dentro de un carril).
Pasillo principal: carril de 5,0 m (Heli CPCD50, W-CAR) + senda de 1,5 m con baranda y cruces.
Almacén: AL-A de 5,0 m (CPCD50: chapa, atados y bobinas) y AL-B de 3,6 m entre racks (pedido del usuario); los racks R1 y de PT los atiende un Heli CPD15 eléctrico (apilado a 90° en 3,3 a 3,5 m, ficha Heli).
Portones de la nave: P1 MP 5,0 m (oeste, con la franja de descarga de 15 × 5 m y la cuarentena), P3 camión de la pintura 5,0 m y P4 PT de manuales 3,6 m (este), P2 despacho de carros 3,5 m con rampa y furgón (sur), P7 scrap 4,0 m (norte del almacén, playa con volquete); P5 patio de ensayos; PE emergencia.
Predio con cerco: PC-1 entrada y PC-2 salida de camiones (circuito de una mano), PC-3 estacionamiento y PC-4 a PC-6 accesos peatonales del plano de oficinas. Cortes A-A a D-D en FL_PI10_06.
Carros: pico de 48 por semana a la pintura con 2 envíos (dato del usuario) -> lotes de media semana: 48 en el pulmón de despacho, 28 pintados, 18 en la sala de pérdidas, 62 retenidos, 70 liberados y 12 rechazados. PT unificado de manuales y carros contra el muro sur, debajo de la terminación compartida (carga y presurización de manuales y carros), que queda debajo de la pintura, cruzando el pasillo; racks de manuales de 90 posiciones (70 de PT y 17 revendidos de X-ALM).
Prueba hidráulica de carros al lado de la de manuales y secado de carros al lado del de manuales (y pegado a su prueba, W-CAR 10); granallado, detección, corrección y cuelgue arriba; descarga de la pintura frente al embalaje. Lo que quedaba libre en el ángulo SO se usa para residuos especiales (con puerta P8 al exterior), aceites e inflamables, reciclables, limpieza y el pañol de EPP con primeros auxilios (FL_PI10_07).

	Fecha	Nombre
Dibujó	16/10/26	Claude Code
Revisó		
Aprobó		

Escala
1:200

Método de proyección
ISO E

Unidades
Cotas en m

Formato
A0

Propietario
FLAMA S.A.

Denominación
Planta general e implantación
Layout 2035 v10 - zonas codificadas y áreas

Tipo de documento
Plano de planta

Reemplaza a / Reemplazado por
-

Material
-

Edición
0

Fecha de emisión
16/10/2026

Hoja
1 / 7

Idioma
es

N° de plano
FL_PI10_01