FL_PI10_03 - CIRCULACIÓN, FLUJOS DE MATERIALES Y RECORRIDOS DEL PERSONAL

Carriles del autoelevador, sendas peatonales y pasillos de operarios con su ancho; flujo de MP, de semielaborado y de PT; hilos del personal desde los vestuarios.

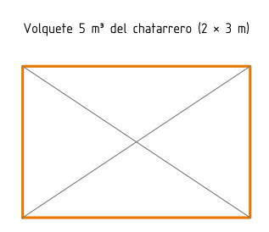

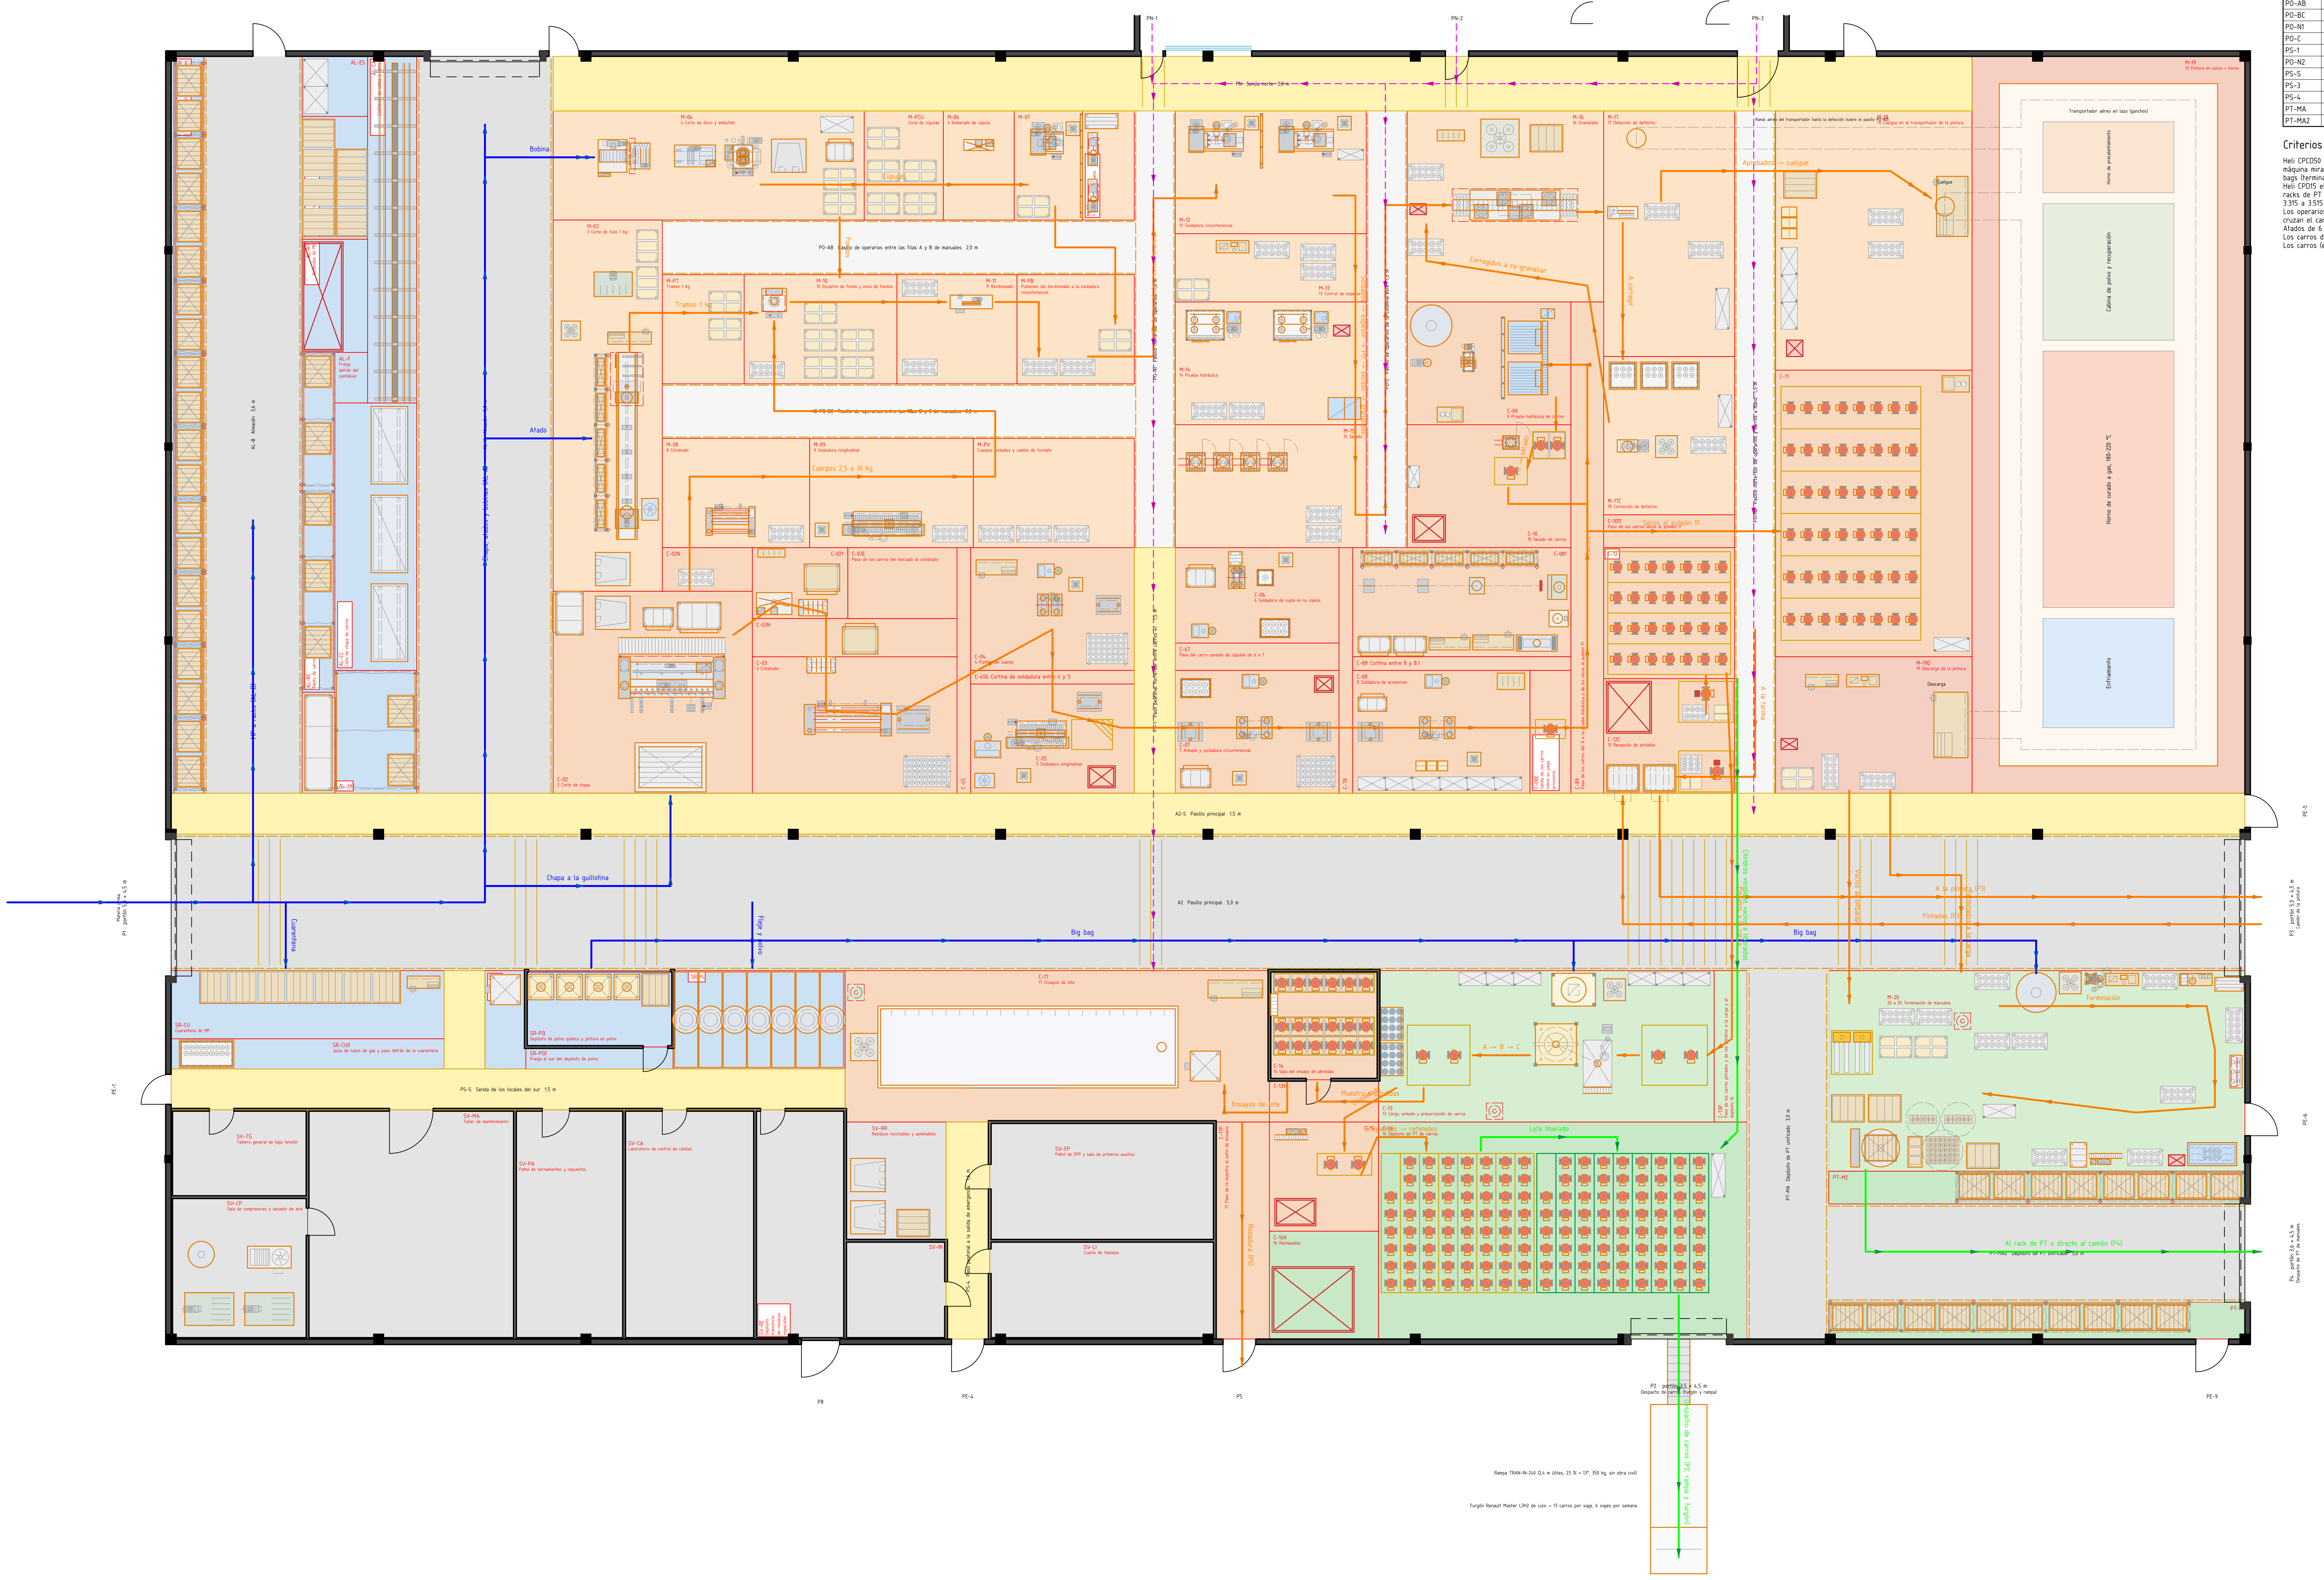
Bobina
Atado
Materia prima
P1 · portón 5,0 × 4,5 m
Cuarentena
Chapa a la guillotina
Fleje y polvo
Big bag
A2-S Pasillo principal 1,5 m
A2 Pasillo principal 5,0 m
C-02
2 Corte de chapa
C-05
5 Soldadura longitudinal
C-07
7 Armado y soldadura circunferencial
C-08
8 Soldadura de accesorios
C-12C
12 Recepción de pintados
C-14
14 Sala del ensayo de pérdidas
C-17
17 Ensayos de lote
SR-CU
Cuarentena de MP
SR-CU0
Jaula de tubos de gas y paso detrás de la cuarentena
SR-PQ
Depósito de polvo químico y pintura en polvo
SR-PQ1
Franja al sur del depósito de polvo
A la pintura (P3)
Pintados (P3)
Vacíos al embalaje
Terminados a la carga
Cilindros vendidos vacíos a liberados
A la tarima
Descarga
M-20
20 a 25 Terminación de manuales
Terminación
A -> B -> C
P3 · portón 5,0 × 4,5 m
Camión de la pintura
PE-5
P2 · portón 3,5 × 4,5 m
Despacho de carros (furgón y rampa)
Despacho de carros (P2, rampa y furgón)
Rampa TRAN-IN-240 (2,4 m útiles, 23 % ≈ 13°, 350 kg, sin obra civil)
Furgón Renault Master L3H2 de culo: ≈ 13 carros por viaje, 6 viajes por semana

Referencias

- ▨ Carril del autoelevador (3,0 a 5,0 m)
- 🟨 Senda peatonal demarcada
- ☐ Pasillo de operarios y carros a mano

Flujos

- → MP: materia prima (azul)
- → SE: semielaborado (naranja)
- → PT: producto terminado (verde)
- - - → Hilos de personal (magenta)

Pasillos (m)

Cód.	Pasillo	Ancho	Largo	Uso
A2	Pasillo principal	5,0	76,0	Autoelevador
A2-S	Pasillo principal	1,5	76,0	Peatonal
AL-A	Almacén	5,0	27,0	Autoelevador
AL-B	Almacén	3,6	27,0	Autoelevador
PN	Senda norte	2,0	52,0	Peatonal
PO-AB	Pasillo de operarios entre las filas A y B de manua.	2,0	17,3	Operarios
PO-BC	Pasillo de operarios entre las filas B y C de manua.	2,0	17,3	Operarios
PO-N1	Pasillo norte-sur de operarios	1,5	16,0	Operarios
PO-C	Pasillo de operarios de la columna este	1,5	16,0	Operarios
PS-1	Paso peatonal norte-sur entre carros 4/5 y 6/7	1,5	9,0	Peatonal
PO-N2	Pasillo norte-sur de operarios y carros a mano	1,5	25,0	Operarios
PS-S	Senda de los locales del sur	1,5	24,7	Peatonal
PS-3	Paso peatonal de la senda sur al pasillo principal	1,5	3,6	Peatonal
PS-4	Paso peatonal a la salida de emergencia PE-4	1,6	8,0	Peatonal
PT-MA	Depósito de PT unificado	3,0	13,5	Autoelevador
PT-MA2	Depósito de PT unificado	3,6	15,2	Autoelevador

Criterios de circulación

Heli CPCD50 (W-MAN y W-CAR): circula por A2 y AL-A (5,0 m) y entra a los puestos únicamente donde la máquina mira al carril: mesa elevadora, cajón del atado, desbobinador, contenedores de scrap (a P7), big bags (terminación y carro 13); las tarimas de los carros 11 y 12 las lleva por el pasillo principal a P3.
Heli CPD15 eléctrico (agregado por los pasillos angostos que pidió el usuario): racks R1 por AL-B (3,6 m), racks de PT por PT-MA (3,0 m, un sentido) y PT-MA2 (3,6 m), envolvedora y camión de P4. Apilado a 90°: 3.315 a 3.515 mm según el pallet (ficha Heli CPD15-20); el CPCD50 necesitaría 4,96 m.
Los operarios caminan por las sendas (amarillas) y por los pasillos de operarios de 1,5 a 2,0 m; cruzan el carril sólo por los cruces demarcados de la baranda.
Atados de 6 m: se mueven colgados de la pluma (W-MAN 1 y 2), a lo largo del pasillo.
Los carros de manuales (FCHP y de 12 cajones) se empujan a mano entre puestos pegados (W-MAN).
Los carros (extintores rodantes) ruedan sobre su juego provisorio desde el puesto 8 (W-CAR).

	Fecha	Nombre
Dibujó	16/10/26	Claude Code
Revisó		
Aprobó		

Escala: 1:100
Método de proyección: ISO E
Unidades: Cotas en m
Formato: A0
Propietario: FLAMA S.A.
Denominación: Circulación y flujos
Layout 2035 v10 – pasillos, materiales y personas
Tipo de documento: Plano de circulación
Reemplaza a / Reemplazado por: -
Material: -
Edición: 0
Fecha de emisión: 16/10/2026
Hoja: 3 / 7
Idioma: es
N° de plano: FL_PI10_03