

# FL_PI10_04 - ALMACÉN DE MATERIA PRIMA, RECEPCIÓN Y LOCALES DEL ÁNGULO SUDOESTE

Secciones de X-ALM v5 con su color; espacios de W-CAR 1 al pie de la letra (cuarentena, retenidos, calle de chapa, racks de carros, franja de descarga).

## Almacén de MP (x 0 a 14,0; y 20 a 47)

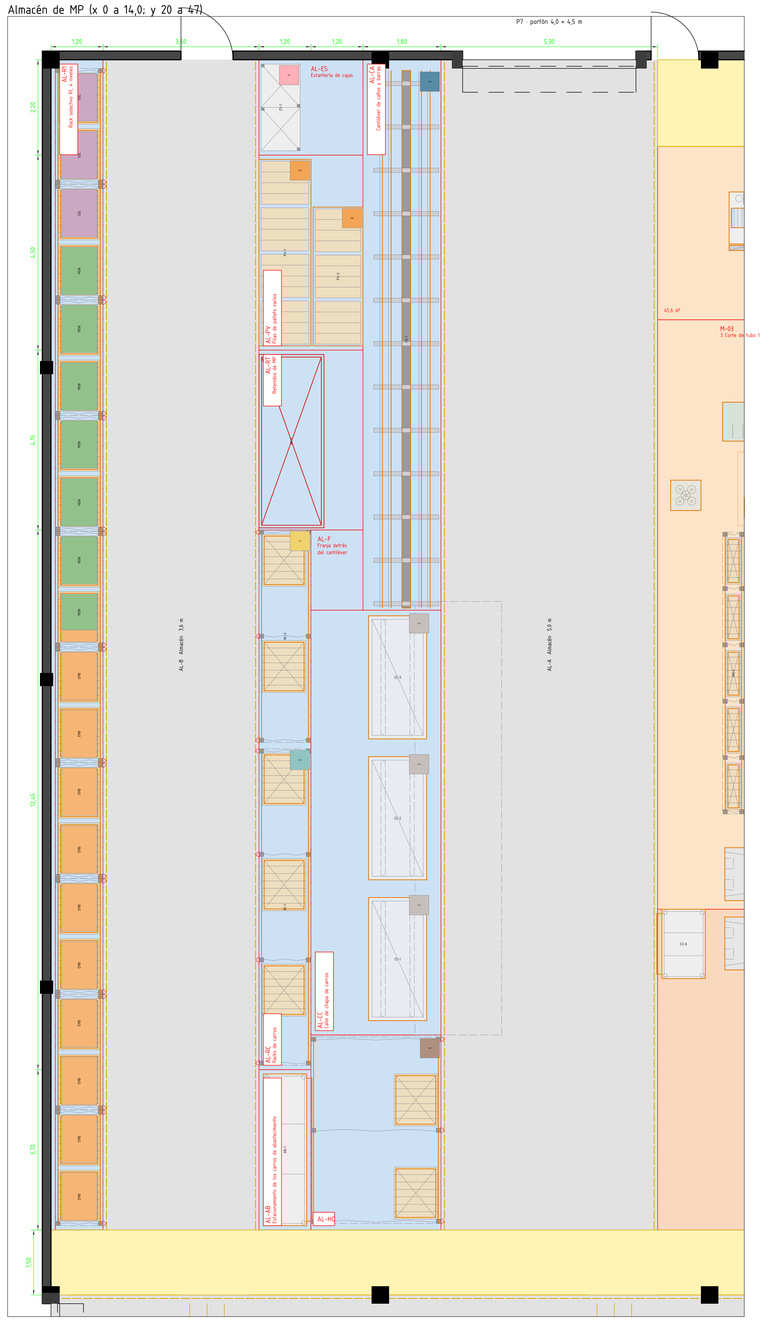


## Portón P1 y franja de descarga, recepción, cuarentena, polvo, fleje y locales del ángulo SO (x -6 a 26; y 0 a 19)

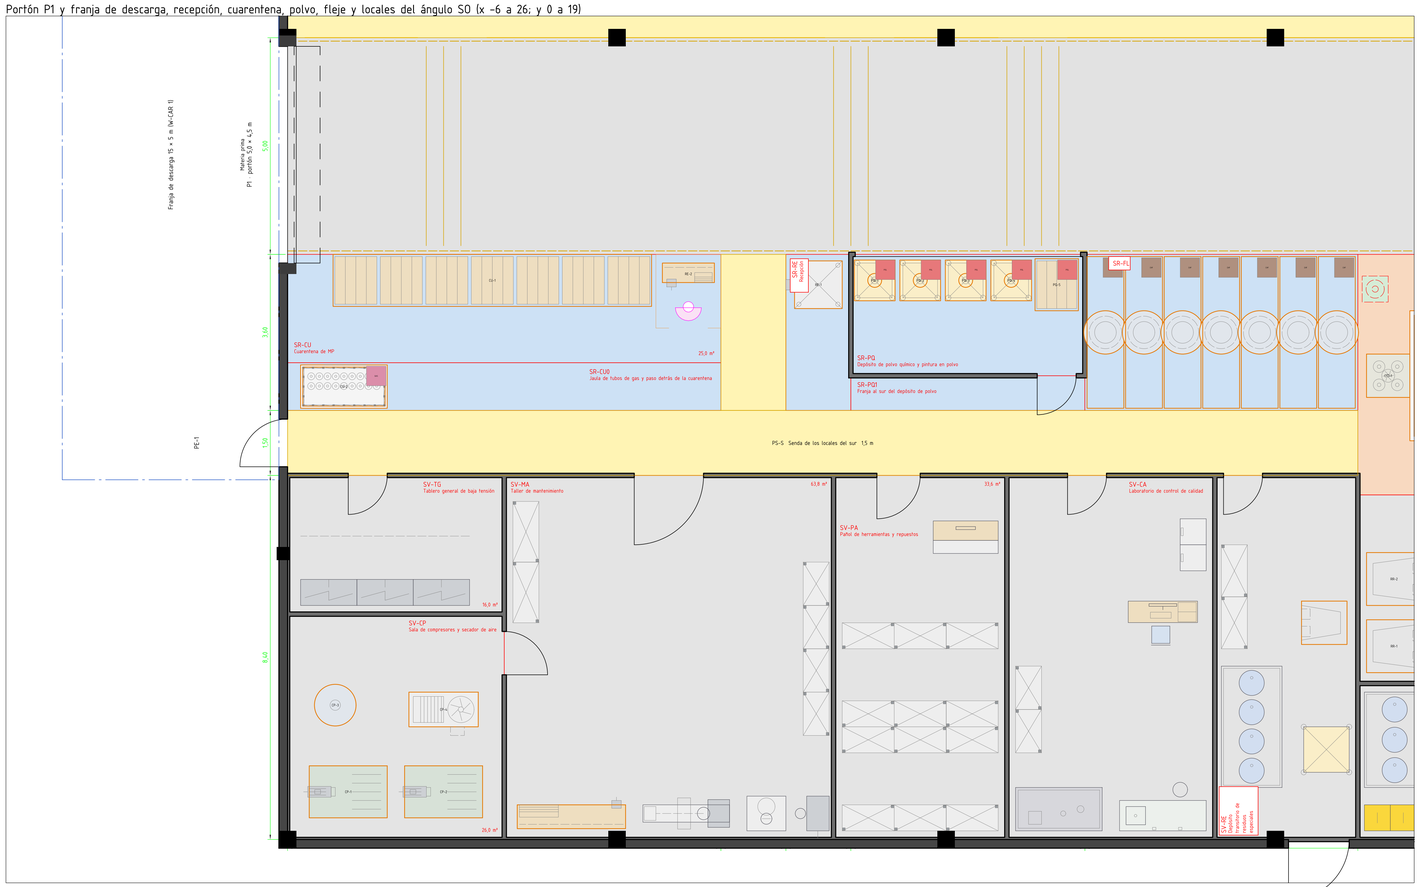


## Almacenamiento (cantidades de la fuente)

| Sección | Cómo se guarda | Cantidad | Fuente |
|---|---|---|---|
| Rack RI | 80 posiciones: 10 módulos de 2,67 m × 4 niveles × 2 pallets, por secciones | 80 pos. | X-ALM |
| Racks de carros | casquetes y cuplas 7,3 × 1,2 m (12 pos.) e insumos 4,9 × 1,2 m (8 pos.), 2 niveles | 20 pos. | W-CAR 1 |
| Hojas de manuales | rack por espesor, 4 niveles, 3 bocas (1,25, 1,6 y 2,0 mm) | 12 paq. | W-MAN 1 |
| Calle de chapa de carros | 10 × 2 m, 3 posiciones de 3,0 × 1,5 m, 2 paquetes de alto | 20 m² | W-CAR 1 |
| Cantilever | frente de 12,4 m, 5 niveles, brazos de 1,2 m | 11 pos. | X-ALM |
| Bobinas de fleje | 21 posiciones en 7 calles de 3 (pallet en piso, 1 nivel) | 21 pos. | X-ALM P05-P11 |
| Polvo químico y pintura | big bags en el piso de a 2 (4 pilas) y 1 pila de 2 pallets, local cerrado | 10 u | W-CAR 1 / X-ALM |
| Pallets vacíos | 7 pilas en piso (sección embalaje) | 7 pilas | X-ALM |
| Identificación e insumos chicos | estantería de cajas de 5 niveles, identificación bajo llave | 15 lug. | X-ALM |
| Cuarentena | 10 × 2,5 m: 7 pallets, mesa de inspección y 1,3 m de circulación, pegada a P1 | 25 m² | W-CAR 1 |
| Retenidos de MP | 4 × 1,5 m demarcado en rojo, 3 pallets | 6 m² | W-CAR 1 |
| Jaula de tubos de gas | N2 y Ar/CO2, llenos separados de vacíos, ventilada | 2 m² | W-CAR 1 |
| Recepción | balanza 1,20 × 1,20 m y mesa de inspección 1,2 × 0,6 m | 6,8 m² | W-MAN 1 / W-CAR 1 |
| Carros de abastecimiento | 3 carros FCEPI1520 (2 de carros y 1 de manuales) | 3,5 m² | W-CAR 1 / W-MAN 1 |
| Franja de descarga (playón) | 15 × 5 m frente a P1, línea discontinua, compartida con manuales | 75 m² | W-CAR 1 |
| Jaula de gases (exterior) | packs de Arcal 21 y de N2 con manifold, al sur. | 21 m² | W-MAN 1 |
| Revendidos | van al rack de PT (sección «almacén de producto terminado» de X-ALM) | 17 pos. | X-ALM |

## Secciones del almacén (X-ALM v5; colores del croquis del usuario)

- PT — Almacén de producto terminado (revendidos) (17 pos.): Rack de PT de matafuegos terminados (PTM-1): la sección es de producto terminado
- EMB — Embalaje (50 pos.): R1: cajas de cartón, 41 pos.; pilas de pallets vacíos en piso, 7; estantería (etiquetas de caja), 2
- MON — Insumos de montaje (manuales) (31 pos.): R1: 27 pos.; estantería (asientos M22), 4
- SOL — Insumos de soldadura y superficie (12 pos.): R1: alambre y granalla
- CAS — Rack de casquetes y cuplas (carros) (11 pos.): Rack propio de W-CAR: 12 posiciones
- ICA — Rack de insumos de montaje (carros) (7 pos.): Rack propio de W-CAR: 8 posiciones
- POL — Depósito de polvo químico (8 pos.): Local cerrado: 4 pilas de 2 big bags y 1 pila de 2 pallets de pintura (sin los polvos de recargas)
- CHP — Chapa y fleje (manuales) (28 pos.): Rack de chapas por espesor y 21 bobinas en sus calles
- CCH — Calle de chapa (carros) (3 pos.): Calle de 10 × 2 m con 3 posiciones (W-CAR)
- CAN — Cantilever de caños y barras (11 pos.): Cantilever de 12,4 m
- CE — Identificación (9 pos.): Estantería de cajas bajo llave
- GAS — Jaula de gases (12 pos.): Jaula exterior (packs) y jaula de tubos de la cuarentena

AL-A de 5,0 m para el Heli CPCD50 (W-CAR 1) y AL-B de 3,6 m para el Heli CPD15 (pedido del usuario; ficha Heli: 3,3 a 3,5 m para apilar a 90°). Los racks de carros, los retenidos, las pilas de pallets y la estantería miran a AL-B; el rack de chapas, la calle de chapa y el cantilever miran a AL-A (W-CAR 1: «la calle de chapa y los racks quedan del otro lado del pasillo»). El procesado de X-ALM no va al almacén W-MAN lo guarda en los carros de 12 cajones al lado de cada puesto. Los insumos de recargas no van.

| | Fecha | Nombre |
|---|---|---|
| Dibujó | 16/10/26 | Claude Code |
| Revisó | | |
| Aprobó | | |

Escala 1:50 · Método de proyección ISO E · Unidades Cotas en m · Formato A0

Propietario: FLAMA S.A.

Denominación: Almacén de MP y recepción

Layout 2035 v10 - X-ALM v5 con el autoelevador de W-CAR

Tipo de documento: Plano de detalle

Reemplaza a / Reemplazado por: –

Material: –

Edición 0 · Fecha de emisión 16/10/2026

Hoja 4 / 7 · Idioma es

Nº de plano FL_PI10_04