

FL_PI10_06 – CORTES DE LA NAVE A-A, B-B, C-C Y D-D

Alturas con fuente (ET, cotizaciones, W-CAR, hoja de especificaciones); lo que no tiene alto en ninguna fuente va marcado «s/d». Ubicación de los cortes en la planta de la derecha y en FL_PI10_01.


CORTE A-A (longitudinal por y = 5,6 m, mirando al norte)

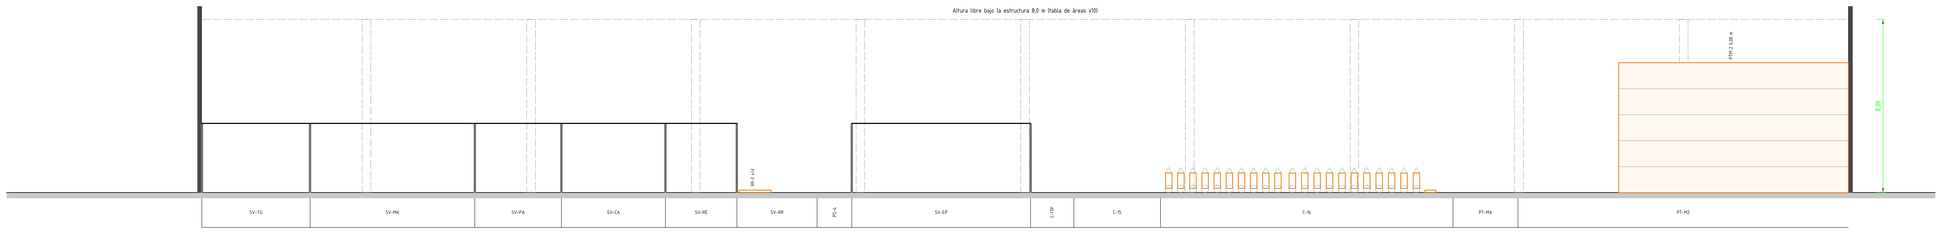


CORTE C-C (longitudinal por y = 37,65 m, mirando al norte)

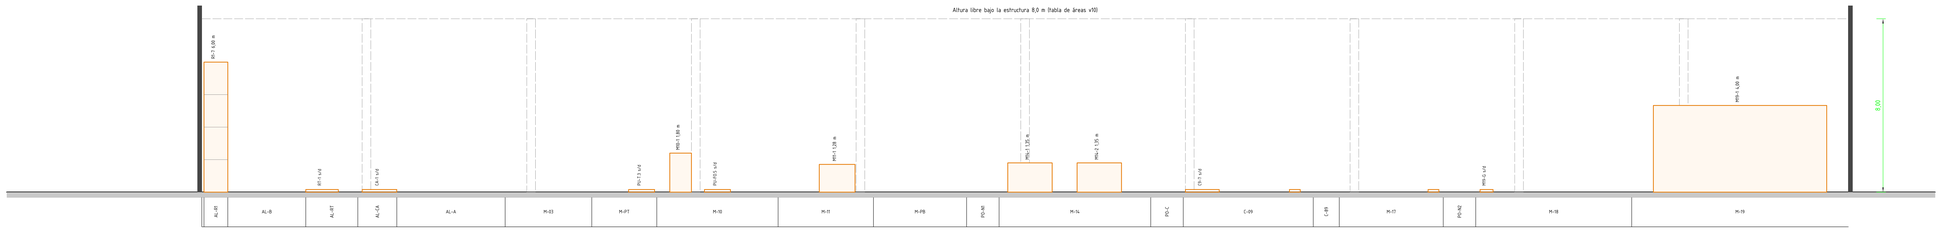

Ubicación de los cortes (1:500)

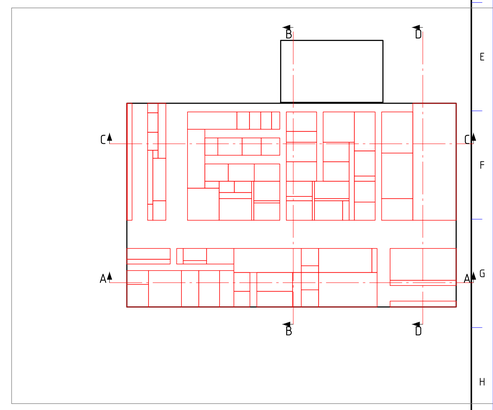

CORTE B-B (transversal por x = 38,4 m, mirando al oeste; el norte a la derecha)

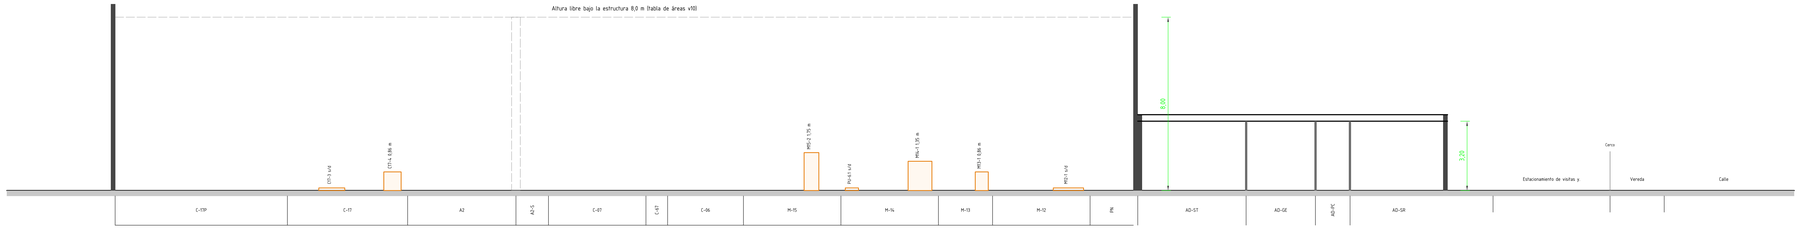

CORTE D-D (transversal por x = 68,3 m, mirando al oeste; el norte a la derecha)



Alturas dibujadas y su fuente

Elemento	Alto (m)	Fuente
Anexo	3,20	Locales de servicio de 3,20 m (tabla de áreas v10; Dec. 351/79 cap. 5: 3 m como mínimo)
Carros	1,16	Hoja de especificaciones «Polvos carros»: carro de 50 kg, 1160 mm (25 kg 1085; 100 kg 1360)
M10-1	1,80	ET Del Fabro: 1800 mm
M11-1	1,28	Presupuesto Pilman SWM-400: 1280 mm
M19-1	4,00	ET línea Firesafer: 25 × 8 × 4 m
Mesas y bancos	0,86	W-CAR 1: mesa de trabajo metálica de unos 86 cm de alto
Nave	8,00	Altura libre de la nave: 8,0 m (tabla de áreas v10; Dec. 351/79 cap. 5)
Prueba hidráulica	1,35	Catálogo Firesafer PS-ID12A: 1350 mm
Rack R1	6,00	Criterio: la carga de arriba llega a la elevación máxima del Heli CPCD50, 6 m (W-CAR 1)
Racks de PT	6,00	Criterio: 5 niveles hasta la elevación máxima del Heli CPCD50, 6 m (W-CAR 1)
SV-CA	3,20	Locales de servicio de 3,20 m (tabla de áreas v10; Dec. 351/79 cap. 5: 3 m como mínimo)
SV-EP	3,20	Locales de servicio de 3,20 m (tabla de áreas v10; Dec. 351/79 cap. 5: 3 m como mínimo)
SV-MA	3,20	Locales de servicio de 3,20 m (tabla de áreas v10; Dec. 351/79 cap. 5: 3 m como mínimo)
SV-PA	3,20	Locales de servicio de 3,20 m (tabla de áreas v10; Dec. 351/79 cap. 5: 3 m como mínimo)
SV-RE	3,20	Locales de servicio de 3,20 m (tabla de áreas v10; Dec. 351/79 cap. 5: 3 m como mínimo)
SV-TG	3,20	Locales de servicio de 3,20 m (tabla de áreas v10; Dec. 351/79 cap. 5: 3 m como mínimo)
Secadoras	1,75	ET secadora Yukon: 1750 mm

Portones: 4,5 m de alto (criterio: caja de camión de hasta 4,1 m, Ley 24.449 art. 53); P1 y P3 de 5,0 m de ancho, P4 de 3,6 m (pasillo de los racks), P7 de 4,0 m y P2 de 3,5 m (plano de carros, rev 6). Los equipos sin alto en ninguna fuente (guillotina, roladora W12, vradores, soldadoras, bobinas, carros de planta, pallets en piso) se marcan «s/d» se completan con el plano del fabricante.

	Fecha	Nombre
Dibujó	16/10/26	Claude Code
Revisó		
Aprobó		

Escala 1:100 · Método de proyección ISO E · Unidades Cotas en m · Formato A0

Propietario: FLAMA S.A.

Denominación: Cortes de la nave

Tipo de documento: Plano de cortes

Reemplaza a / Reemplazado por: –

Material: –

Edición 0 · Fecha de emisión 16/10/2026

Hoja 6 / 7 · Idioma es

Nº de plano FL_PI10_06

layout 2035 v10 – cortes A-A a D-D con las alturas de las fuentes