


FL_PI_01 - DIAGRAMA DE RECORRIDO DE HILOS DEL PERSONAL (DIR)

Planta Industrial FLAMA S.A. - Parque Industrial Villa de Luján, Sarandí (Avellaneda) - dimensionada al año 10 (2035). Escala 1:200. Norte arriba; la calle de acceso está al sur.

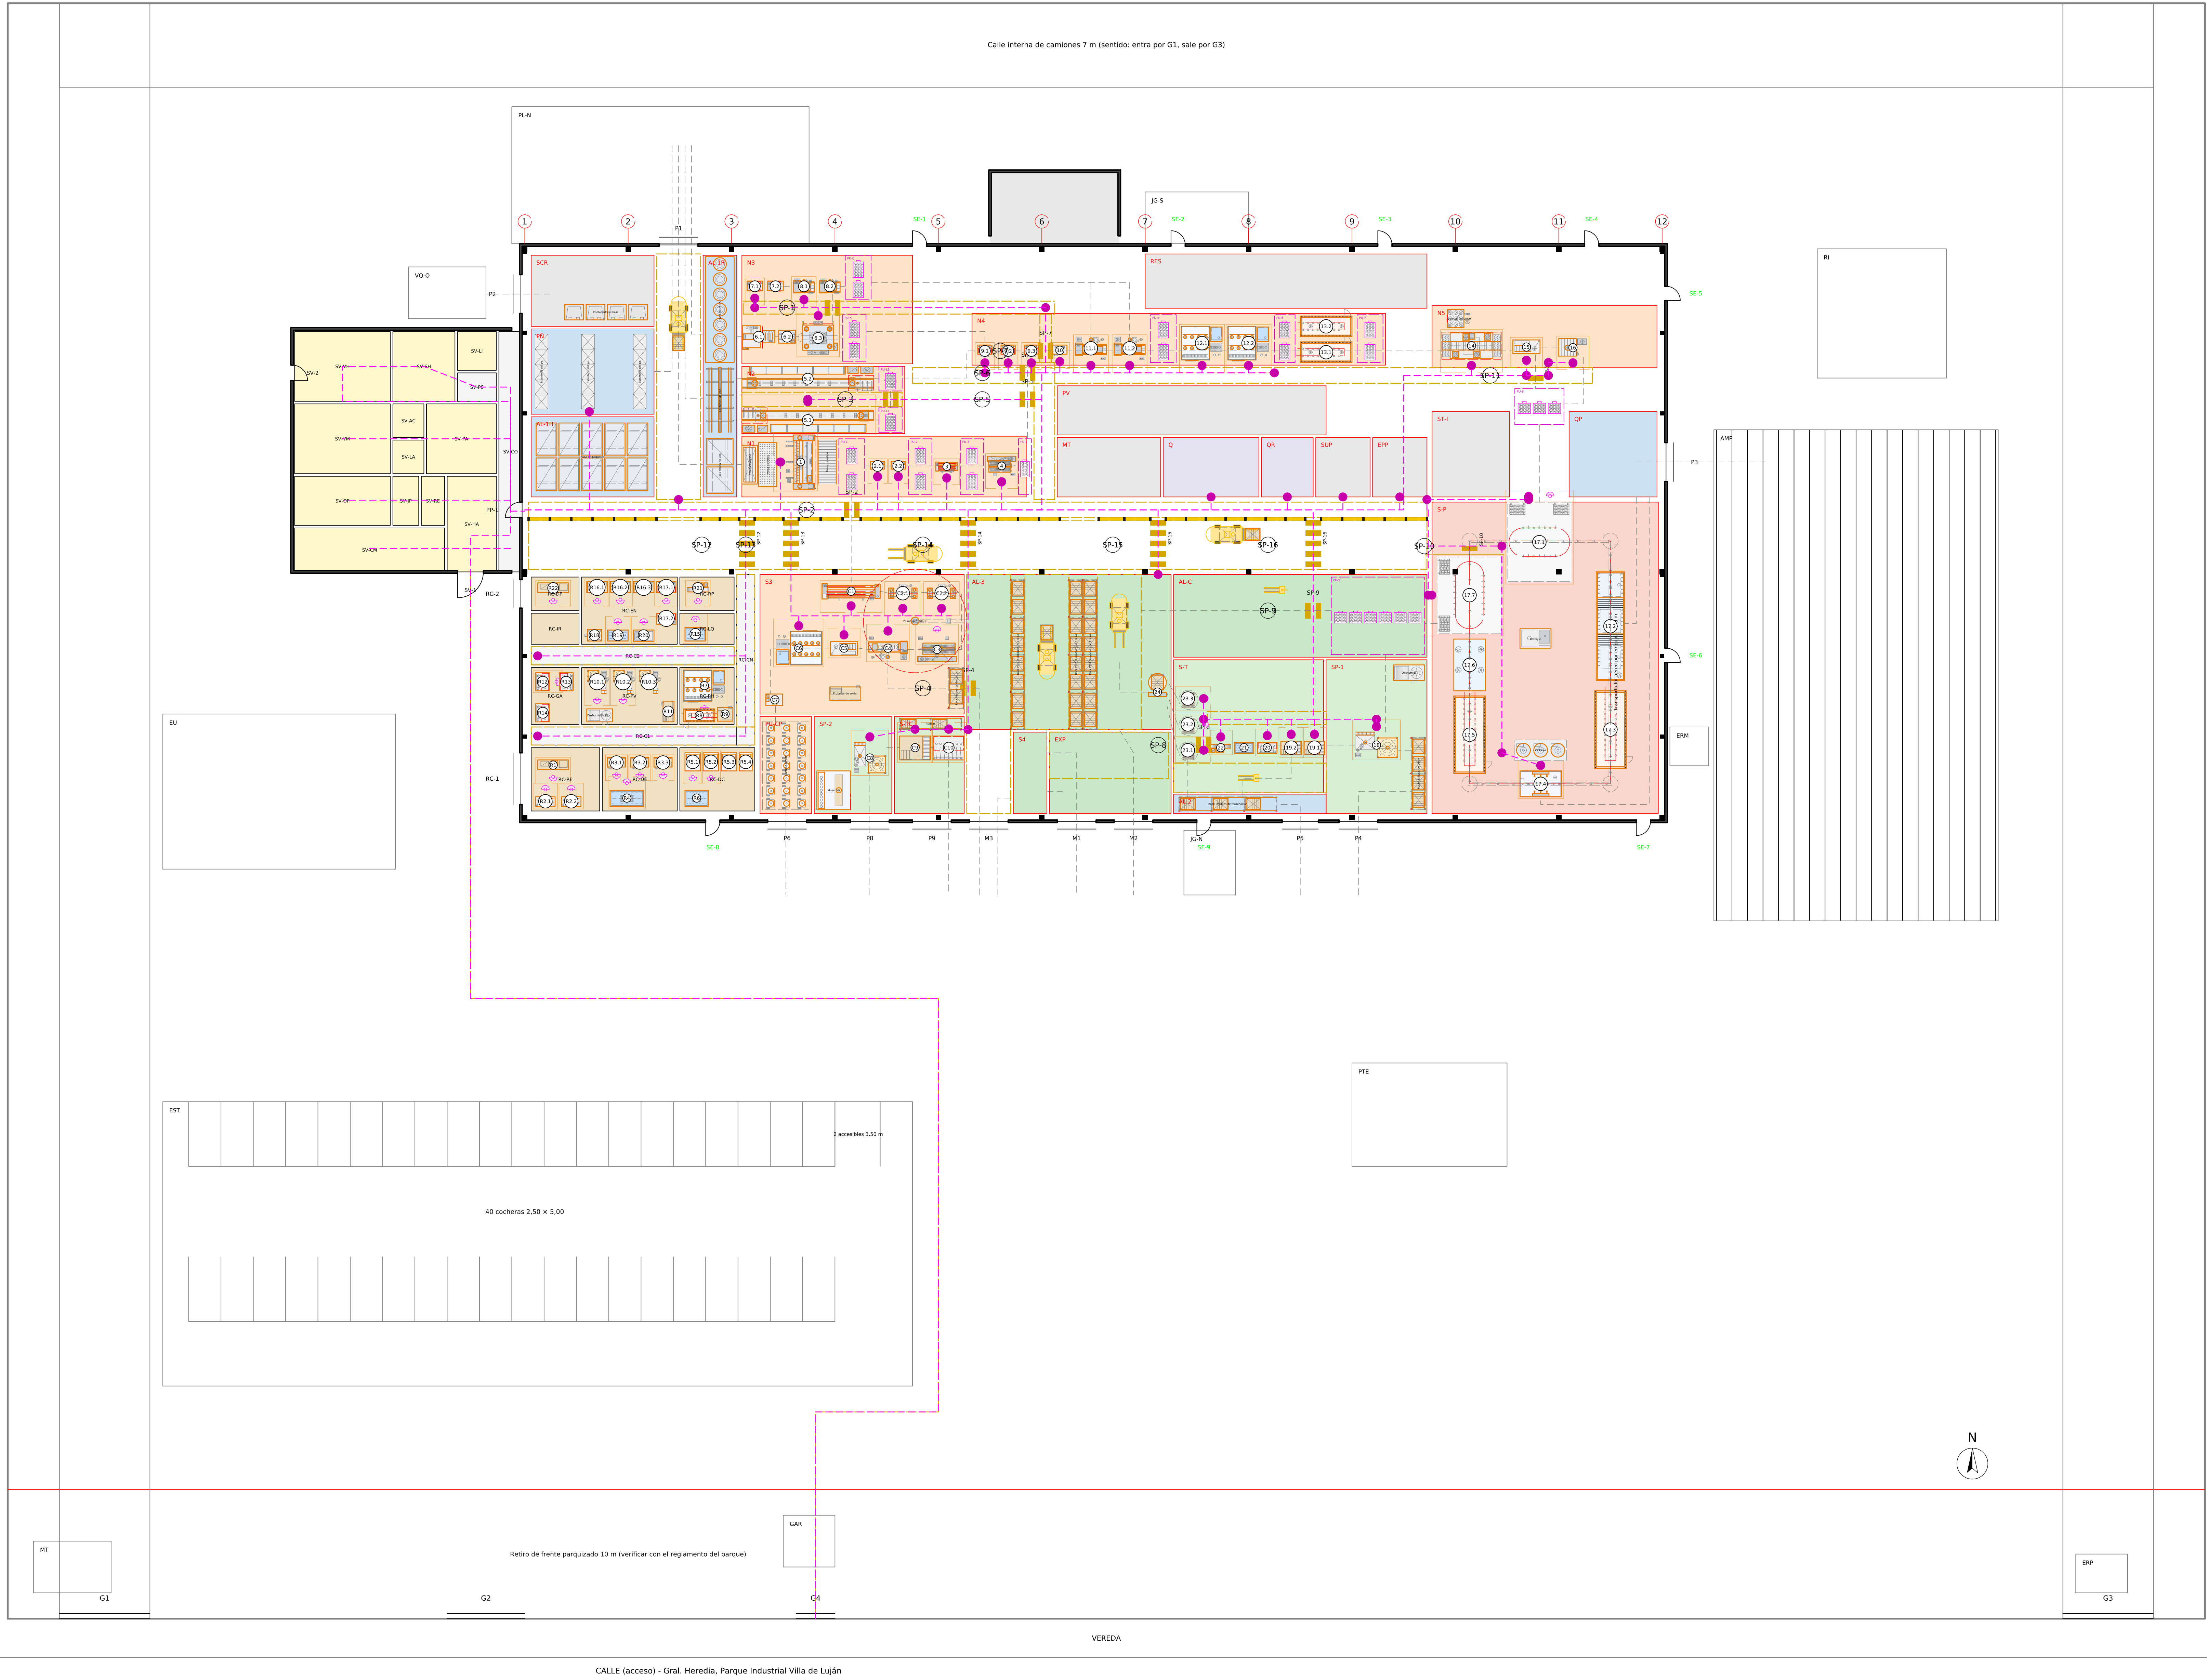

Referencias

Hilo de personal (magenta, trazos)
 Puesto de trabajo
 Flujos de materiales, de fondo (ver FL_PI_03)
 Senda peatonal señalizada: único cruce de hilo y flujo

Recorrido: estacionamiento -> G4 -> hall y fichado -> vestuario (loga de calle) -> sanitarios y duchas -> paso a planta PP-1 -> pabellón central de personal PC (cpe B) -> puesto.
 Se vuelve por el mismo camino y se pasa por el vestuario (circuito sucio -> limpio).
 El PC corre entre las dos bandas de la U: los operarios de la banda norte trabajan del lado sur de sus máquinas y los de la banda sur del lado norte, de modo que llegan al puesto sin cruzar el recorrido de las piezas. La línea de carros es una horquilla con su calle de operarios adentro.
 Donde un hilo corta un flujo (cuernos de carros, cúpulas, láseres, lazo de pintura) hay una senda peatonal SP demarcada (cebra amarilla IRAM 1.0005, espejo y prioridad peatonal).
 Cruces de hilos con flujos verificados por cálculo sobre el modelo: todos en 16 sendas.
 Recargas ocupan el ángulo SO de la nave: su personal entra por el PC y usa los sanitarios del bloque de servicios. El mostrador tiene portón propio (RC-1); el público no entra a la planta.

Longitud de los hilos (turno mañana)

Hilo (grupo de puestos)	Desde PP-1 (m)	A sanitario (m)
Almacén de N1 y corte (N1)	46	46
Láseres, cúpulas, unión y PH (N2-N4)	35	58
Granallado, defectos y pintura (N5, S-P)	56	86
Terminación, calidad y expedición	48	85
Línea de carros (S3)	58	49
Recargas (RC)	34	42

Puestos con operario en la nave

Sector	Puestos	Operarios
N2 Corte y cuerpo 2.5-10 kg	1	1
N3 Cúpulas, fondos y cuellos	3	3
N4 Unión y prueba hidráulica	8	8
N5 Granallado y defectos	3	3
S-P Pintura en polvo (lazo)	3	4
SP-1 Sala de carga de polvo	1	1
S-T Terminación 1-10 kg	7	7
S3 Línea de carros 25-100 kg	7	7
SP-2 Sala de carga de polvo de carros	1	1
S-TC Terminación de carros	2	2
RC-NE	3	3
RC-DE	4	4
RC-DC	2	2
RC-PH	1	1
RC-PV	2	2
RC-GA	1	1
RC-LQ	1	1
RC-EN	5	5
RC-AP	1	1
RC-DP	1	1
Total de puestos (la DT, con coef. hombre-máquina, da 30 operarios)	63	

Sanitarios (Dec. 351/79 art. 49): 55 H y 6 M en el turno más numeroso

Artefacto	H req.	H proy.	M req.	M proy.
Inodoros	3	5	1	3
Lavabos	6	8	1	3
Orinales	6	8	0	0
Duchas	3	4	1	2
Armarios (lat. 50)	56	62	7	14
Sanitario accesible	-	2	-	unisex

Turno mañana: 53 personas + 8 choferes que inician y terminan en plátano: 10 % mujeres (DT 2035).
 Núcleo sanitario en servicios, junto a PP-1, con H y M y sanitario accesible (Ley 24.334, Dec. 914/97); el PC lleva a todos los puestos sin cruzar flujos fuera de las sendas.
 Vestuario de mujeres al 20 % de la dotación para no condicionar la incorporación de personal femenino.
 Lactario (Ley 26.873) y primeros auxilios en servicios.
 Espacio de cuidado (Dec. 144/2022): no obligatorio con menos de 100 personas (dotación 7.1).

Fecha	Nombre	Propietario	Reemplaza a / Reemplazado por
02/10/26	Claude Code	FLAMA S.A.	-
Revisó		Denominación	Material
Aprobó		DIR hilos de personal	-
Escala	Método de proyección		Edición
1:200	ISO E		0
Unidades	Formato	Recorrido del personal - año 10	Fecha de emisión
Cotas en m	A0	Diagrama de recorrido	1 / 1
			es
			Nº de plano
			FL_PI_01