


FL\_PI\_04 - PLANO FORMAL NORMALIZADO - HOJA 1: IMPLANTACIÓN GENERAL

Parque Industrial Villa de Luján, Gral. Heredia 3220, Sarandí (Avellaneda). Escala 1:200. Cotas en metros. Norte arriba.

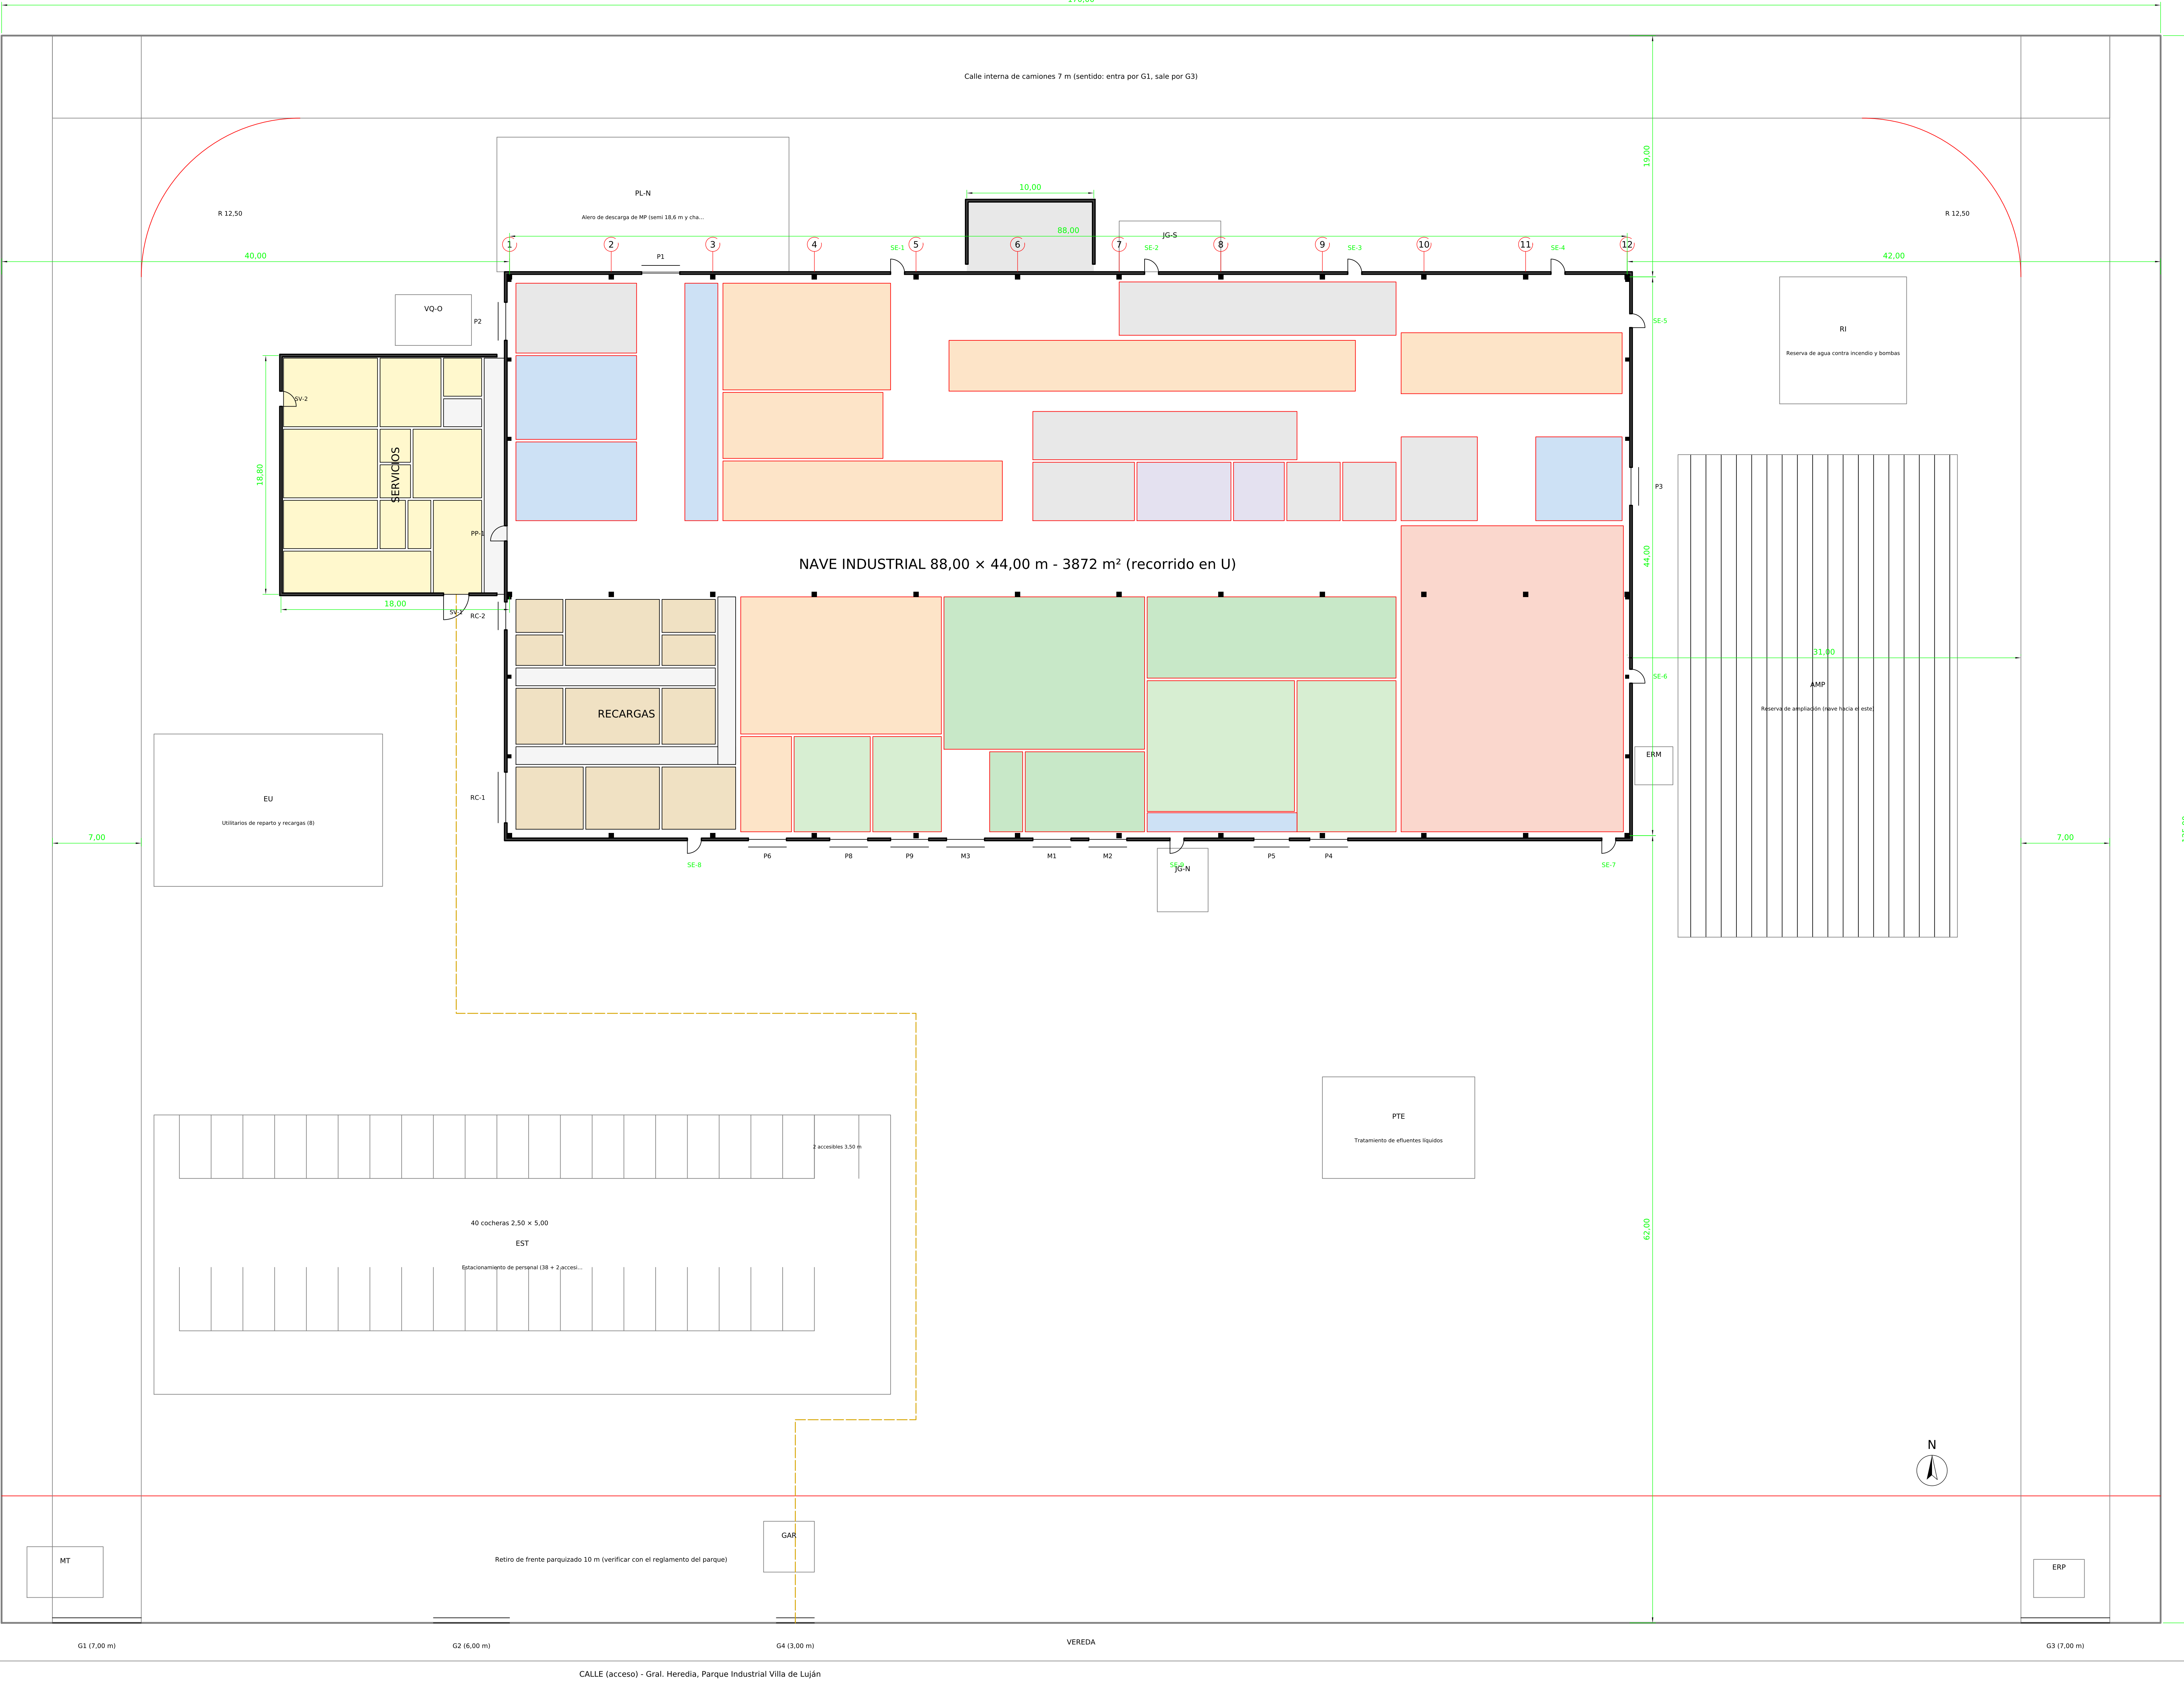

Cuadro de superficies

| Concepto                         | m²     | %     |
|----------------------------------|--------|-------|
| Terreno 170,00 x 125,00          | 21.250 | 100,0 |
| Nave industrial 88,00 x 44,00    | 3.872  | 18,2  |
| Incluye recargas (ángulo SO)     | 327    |       |
| Servicios al personal y oficinas | 338    | 1,6   |
| Sala técnica norte               | 58     | 0,3   |
| Alero de descarga de MP (norte)  | 244    | 1,1   |
| Superficie cubierta total        | 4.512  | 21,2  |
| FOS = cubierta / terreno         |        | 0,21  |
| Reserva de ampliación (este)     | 836    |       |

FOS, FOT, retiros y altura máxima: verificar con el reglamento del parque industrial y el código de Avellaneda (Ley 13.744 de parques industriales PBA, habilitación Ley 11.459).

Referencias de exteriores

| Código | Elemento exterior                                  |
|--------|----------------------------------------------------|
| PL-N   | Alero de descarga de MP (semi 18,6 m y chasis)     |
| VQ-O   | Volquete 6 m³ (scrap)                              |
| JG-S   | Jaula de gases de soldadura (Ar/CO₂)               |
| ERM    | Regulación de gas de hornos                        |
| JG-N   | Jaula de N₂ y CO (manifold)                        |
| RI     | Reserva de agua contra incendio y bombas           |
| AMP    | Reserva de ampliación (nave hacia el este)         |
| PTE    | Tratamiento de efluentes líquidos                  |
| EST    | Estacionamiento de personal (38 + 2 accesibles)    |
| EU     | Utilitarios de reparto y recargas (8)              |
| GAR    | Garita y control de acceso                         |
| MT     | Celda de medición de media tensión                 |
| ERP    | Estación reductora de gas                          |
| G1     | Portón de camiones de MP, scrap y pintor (entrada) |
| G2     | Portón de autos del personal                       |
| G3     | Portón de camiones de PT y carros (salida)         |
| G4     | Ingreso peatonal con garita                        |

Circulación de camiones en anillo de un sentido (G1 -> oeste -> norte -> este -> G3); los camiones de MP descargan en la playa norte o en la bahía interior oeste y los de PT en los muelles sur sin cruzarse. Autos y peatones entran por el frente, separados de los camiones. Radio de giro exterior del semi: 12,50 m. Pavimento de hormigón en calles, playas y patios; veredas perimetrales de 1,20 m. Naves: pórticos metálicos de dos luces (19,40 y 24,60 m) cada 8 m, columnas centrales en el eje B, al borde del pasillo central; altura libre bajo cerca 8,00 m; cerramiento de zócalo de bloque de 2,40 m y chapa; cubierta de chapa con aislación y lucernarios; anexos de mampostería.

|                       |  |                                                                                             |  |                      |  |                               |  |
|-----------------------|--|---------------------------------------------------------------------------------------------|--|----------------------|--|-------------------------------|--|
| Fecha                 |  | Nombre                                                                                      |  | Propietario          |  | Reemplaza a / Reemplazado por |  |
| Dibujó 02/10/26       |  | Claude Code                                                                                 |  | FLAMA S.A.           |  |                               |  |
| Revisó                |  |                                                                                             |  | Denominación         |  | Material                      |  |
| Aprobó                |  |                                                                                             |  | Implantación general |  | Estructura metálica           |  |
| Escala                |  | Método de proyección                                                                        |  | Edición              |  | Fecha de emisión              |  |
| 1:200                 |  |  ISO E |  | 0                    |  | 02/10/2026                    |  |
| Unidades              |  | Formato                                                                                     |  | Hoja                 |  | Idioma                        |  |
| Cotas en m            |  | A0                                                                                          |  | 1 / 4                |  | es                            |  |
| Tipo de documento     |  |                                                                                             |  | Nº de plano          |  |                               |  |
| Plano de implantación |  |                                                                                             |  | FL_PI_04             |  |                               |  |

FL PI\_04 - PLANO FORMAL NORMALIZADO - HOJA 2: PLANTA DE LA NAVE, SECTOR OESTE (x = -20 a 42 m)

Escala 1:100. Cotas en metros. Ejes estructurales 1 a 12 cada 8,00 m y A-B-C (luces de 19,40 y 24,60 m, columnas centrales en el eje B).



Continúa en hoja 3

Equipos por paso (entero = operación; .1, 2 = máquinas iguales)

| Paso  | Cód. | Equipo                                    | Medidas m    | kW   | Op. | Fuente                        |
|-------|------|-------------------------------------------|--------------|------|-----|-------------------------------|
| -     | H01  | Chapa en paquetes (reserva, 2 alturas)    | 8,80 x 5,40  | -    | -   | Estimado                      |
| -     | PH1  | Extintores del pañal                      | 1,00 x 5,90  | -    | -   | Estimado                      |
| -     | PH2  | Extintores del pañal                      | 1,00 x 5,90  | -    | -   | Estimado                      |
| -     | PH3  | Extintores del pañal                      | 1,00 x 5,90  | -    | -   | Estimado                      |
| -     | SC1  | Contenedores basculantes de scrap         | 6,60 x 1,40  | -    | -   | Estimado                      |
| -     | RH1  | Rack de chapa en uso                      | 2,20 x 4,40  | -    | -   | Estimado                      |
| -     | RT1  | Camión de caja 6 m                        | 2,20 x 5,00  | -    | -   | Estimado                      |
| -     | RF1  | Porta-flejes (27 rollos)                  | 2,20 x 8,20  | -    | -   | Estimado                      |
| -     | M02  | Mesa elevadora de trena 11                | 1,40 x 3,00  | 2,2  | -   | MP Manipulación               |
| -     | M03  | Mesa de tolas                             | 1,40 x 3,40  | -    | -   | MP Manipulación               |
| 1     | M04  | Guillete hidráulica 8 x 3200              | 2,30 x 4,20  | 15,0 | 1   | Cota: Cena E21                |
| -     | M05  | Mesa de salida                            | 1,40 x 3,40  | -    | -   | Estimado                      |
| 2.1   | B01  | Numero de cuerpo                          | 1,20 x 0,80  | 0,5  | 1   | Estimado                      |
| 2.2   | B01B | Numero de cuerpo                          | 1,20 x 0,80  | 0,5  | 1   | Estimado                      |
| 3     | B02  | Cilindrada                                | 1,70 x 0,90  | 1,1  | 1   | Cota: Baiden                  |
| 4     | B03  | Soldadura longitudinal                    | 2,20 x 1,60  | 12,0 | 1   | Cota: Misa G52H Ergo          |
| 5.1   | M16  | Láser de tubo 6012                        | 10,20 x 2,00 | 10,0 | 1   | Cota: Leapion 6012            |
| 5.2   | M15  | Láser de tubo 6012                        | 10,20 x 2,00 | 10,0 | -   | Cota: Leapion 6012            |
| 6.1   | M06  | Desdoblador y embudizador                 | 2,60 x 2,00  | 3,0  | -   | Cota: alimentador 900 mm      |
| 6.2   | M07  | Alimentador servo                         | 1,40 x 1,20  | 2,0  | -   | Cota: alimentador 900 mm      |
| 6.3   | M08  | Presión de corte y embudo 300 t           | 3,00 x 2,60  | 30,0 | 1   | Cota: PHM 300                 |
| 7.1   | M09  | Preparación de cuello                     | 1,20 x 1,00  | 3,0  | 1   | Estimado                      |
| 7.2   | M10  | Preparación de cuello                     | 1,20 x 1,00  | 3,0  | -   | Estimado                      |
| 8.1   | M11  | Soldadura circ. de cuello                 | 1,60 x 1,20  | 12,0 | 1   | Cota: FS-HFM1                 |
| 8.2   | M12  | Soldadura circ. de cuello                 | 1,60 x 1,20  | 12,0 | -   | Cota: FS-HFM1                 |
| 9.1   | E09a | Encastre de fondo                         | 1,20 x 1,00  | 1,0  | 1   | Estimado                      |
| 9.2   | E09b | Encastre de fondo                         | 1,20 x 1,00  | 1,0  | -   | Estimado                      |
| 9.3   | E09c | Encastre de fondo                         | 1,20 x 1,00  | 1,0  | 1   | Estimado                      |
| 10    | B04  | Bordenadores                              | 1,20 x 0,90  | 1,5  | 1   | Cota: SWM-400                 |
| -     | R01  | Rack de PT 1 de módulos x 2 x 4)          | 1,18 x 11,40 | -    | -   | Estimado                      |
| C1    | C01  | Cilindrada de 4 rodillos                  | 4,50 x 1,40  | 5,5  | 1   | Cota: Getwell                 |
| C2.1  | C02  | Puntos, refuerzo y estructura             | 2,50 x 1,50  | 10,0 | 1   | Estimado                      |
| C2.2  | C03  | Puntos, refuerzo y estructura             | 2,50 x 1,50  | 10,0 | 1   | Estimado                      |
| C3    | C04  | Soldadura longitudinal de caros           | 3,00 x 2,00  | 18,0 | 1   | Cota: Getwell ZF-1000         |
| C4    | C05  | Soldadura circ. de fondo y cúpula         | 3,00 x 1,80  | 18,0 | 1   | Estimado                      |
| C5    | C06  | Inspección de costuras                    | 2,20 x 1,20  | 0,5  | 1   | Estimado                      |
| C6    | C07  | PH 4,2 MPA con jaula                      | 3,60 x 2,60  | 2,0  | 1   | Cota: Vulkan M.000200 + jaula |
| C7    | C08  | Marcado del recipiente                    | 2,40 x 1,00  | 0,5  | -   | Estimado                      |
| -     | C09  | Probas de soldadura                       | 2,40 x 1,20  | 2,0  | -   | Estimado                      |
| -     | AL1C | Rack de casquetes de caros                | 1,20 x 3,20  | -    | -   | Estimado                      |
| C12   | C12  | Carro a pintura mecanizada                | 3,60 x 6,80  | -    | -   | Estimado                      |
| C8    | T02  | Carga de polvo de caros                   | 2,60 x 2,40  | 2,0  | 1   | Estimado                      |
| -     | Q01  | Cabina de descarga de muestras            | 2,60 x 3,00  | 3,0  | -   | Estimado                      |
| C9    | T12  | Almado de caros                           | 2,40 x 2,00  | 0,5  | 1   | Estimado                      |
| C10   | T13  | Presurización y etiquetado de caros       | 2,40 x 2,00  | 0,5  | 1   | Estimado                      |
| -     | T14  | Estructuras y ruedas de caros             | 4,80 x 0,90  | -    | -   | Estimado                      |
| R1    | R01  | Recepción y clasificación                 | 2,40 x 0,90  | 0,5  | 1   | Estimado                      |
| R2.1  | R19a | Inspección visual                         | 1,60 x 0,90  | 0,5  | 1   | Estimado                      |
| R2.2  | R19b | Inspección visual                         | 1,60 x 0,90  | 0,5  | 1   | Estimado                      |
| R3.1  | R04a | Desarme de malabaje (mona)                | 1,40 x 0,90  | 0,5  | 1   | Estimado                      |
| R3.2  | R04b | Desarme de malabaje (mona)                | 1,40 x 0,90  | 0,5  | 1   | Estimado                      |
| R3.3  | R04c | Desarme de malabaje (mona)                | 1,40 x 0,90  | 0,5  | 1   | Estimado                      |
| R4    | R05  | Lavado interior de cilindro               | 2,60 x 1,40  | 0,5  | 1   | Estimado                      |
| R5.1  | R02a | Descarga de polvo con recuperación        | 1,20 x 1,40  | 0,5  | 1   | Estimado                      |
| R5.2  | R02b | Descarga de polvo con recuperación        | 1,20 x 1,40  | 0,5  | 1   | Estimado                      |
| R5.3  | R02c | Descarga de polvo con recuperación        | 1,20 x 1,40  | 0,5  | -   | Estimado                      |
| R5.4  | R02d | Descarga de polvo con recuperación        | 1,20 x 1,40  | 0,5  | -   | Estimado                      |
| R6    | R26  | Descarga de flujos                        | 1,80 x 1,40  | 0,5  | -   | Estimado                      |
| R7    | R07  | Prueba hidráulica con jaula               | 3,20 x 2,40  | 0,5  | 1   | Estimado                      |
| R8    | R08  | Secado de cilindros                       | 2,40 x 1,00  | 0,5  | -   | Estimado                      |
| R9    | R23  | Prueba Puffer (IRAM 3572)                 | 1,20 x 1,20  | 0,5  | -   | Estimado                      |
| R10.1 | R02a | Carga de polvo por vacío                  | 1,60 x 1,80  | 0,5  | 1   | Estimado                      |
| R10.2 | R02b | Carga de polvo por vacío                  | 1,60 x 1,80  | 0,5  | 1   | Estimado                      |
| R10.3 | R02c | Carga de polvo por vacío                  | 1,60 x 1,80  | 0,5  | -   | Estimado                      |
| R11   | R16  | Caja D (descarga + carga manual)          | 1,00 x 1,60  | 0,5  | -   | Estimado                      |
| -     | R18  | Deshumidificador sala de polvo            | 2,00 x 1,00  | 0,5  | -   | Estimado                      |
| R12   | R24  | Descarga de CO <sub>2</sub> agente limpio | 1,20 x 1,40  | 0,5  | 1   | Estimado                      |
| R13   | R12  | Carga de CO <sub>2</sub> (transvase)      | 1,20 x 1,40  | 0,5  | -   | Estimado                      |
| R14   | R13  | Carga de agente limpio + N <sub>2</sub>   | 1,20 x 1,40  | 0,5  | -   | Estimado                      |
| R15   | R14  | Llenado de agente líquido                 | 1,60 x 1,20  | 0,5  | 1   | Estimado                      |
| R16.1 | R09a | Ensamblaje (anillo, pescante, rosca)      | 1,60 x 1,00  | 0,5  | 1   | Estimado                      |
| R16.2 | R09b | Ensamblaje (anillo, pescante, rosca)      | 1,60 x 1,00  | 0,5  | 1   | Estimado                      |
| R16.3 | R09c | Ensamblaje (anillo, pescante, rosca)      | 1,60 x 1,00  | 0,5  | -   | Estimado                      |
| R17.1 | R10a | Presurización N <sub>2</sub>              | 1,50 x 1,00  | 0,5  | 1   | Estimado                      |
| R17.2 | R10b | Presurización N <sub>2</sub>              | 1,50 x 1,00  | 0,5  | -   | Estimado                      |
| R18   | R27  | Empuje de peso                            | 1,20 x 1,00  | 0,5  | -   | Estimado                      |
| R19   | R31  | Hermeticidad (inmersión)                  | 1,60 x 1,00  | 0,5  | 1   | Estimado                      |
| R20   | R20  | Retenue de pintura                        | 1,60 x 1,00  | 0,5  | 1   | Estimado                      |
| R21   | R21  | Etiquetado (cable IRAM + martinet)        | 1,60 x 0,90  | 0,5  | 1   | Estimado                      |
| R22   | R17  | Despacho (precintos + remite)             | 2,40 x 0,90  | 0,5  | 1   | Estimado                      |


Referencias: cada equipo se dibuja en planta a escala con sus partes (basidor, rodillos, montañas, motores, tableros), resguardos en rojo y perrero en su puesto (magenta); en trazos, partes elevadas; óvalo = código del equipo; círculo rojo = barrido de pluma; líneas amarillas = demarcación de pasillos (IRAM 1000S); color = senda peatonal; punto rojo numerado = extintor ABC 10 kg (IRAM 3517-2; recorrido > 20 m); fecha verde = salida de emergencia 1,10 m con barril antipánico.

|            |                      |                         |                               |
|------------|----------------------|-------------------------|-------------------------------|
| Fecha      | Nombre               | Propietario             | Reemplaza a / Reemplazado por |
| 02/10/2026 | Claude Code          | FLAMA S.A.              | -                             |
| Revisó     |                      | Denominación            | Material                      |
| Aprobó     |                      | Planta de la nave oeste | Estructura metálica           |
| Escala     | Método de proyección | Edición                 | Fecha de emisión              |
| 1:100      | ISO E                | 0                       | 02/10/2026                    |
| Cotas en m | Formato              | Hoja                    | es                            |
| A0         | Tipo de documento    | 2 / 4                   | es                            |
|            |                      | Nº de plano             | FL_PI_04                      |

FL PI\_04 - PLANO FORMAL NORMALIZADO - HOJA 3: PLANTA DE LA NAVE, SECTOR ESTE (x = 42 a 104 m)

Escala 1:100. Cotas en metros. Ejes estructurales 1 a 12 cada 8,00 m y A-B-C (lucos de 19,40 y 24,60 m, columnas centrales en el eje B).

Continúa en hoja 2

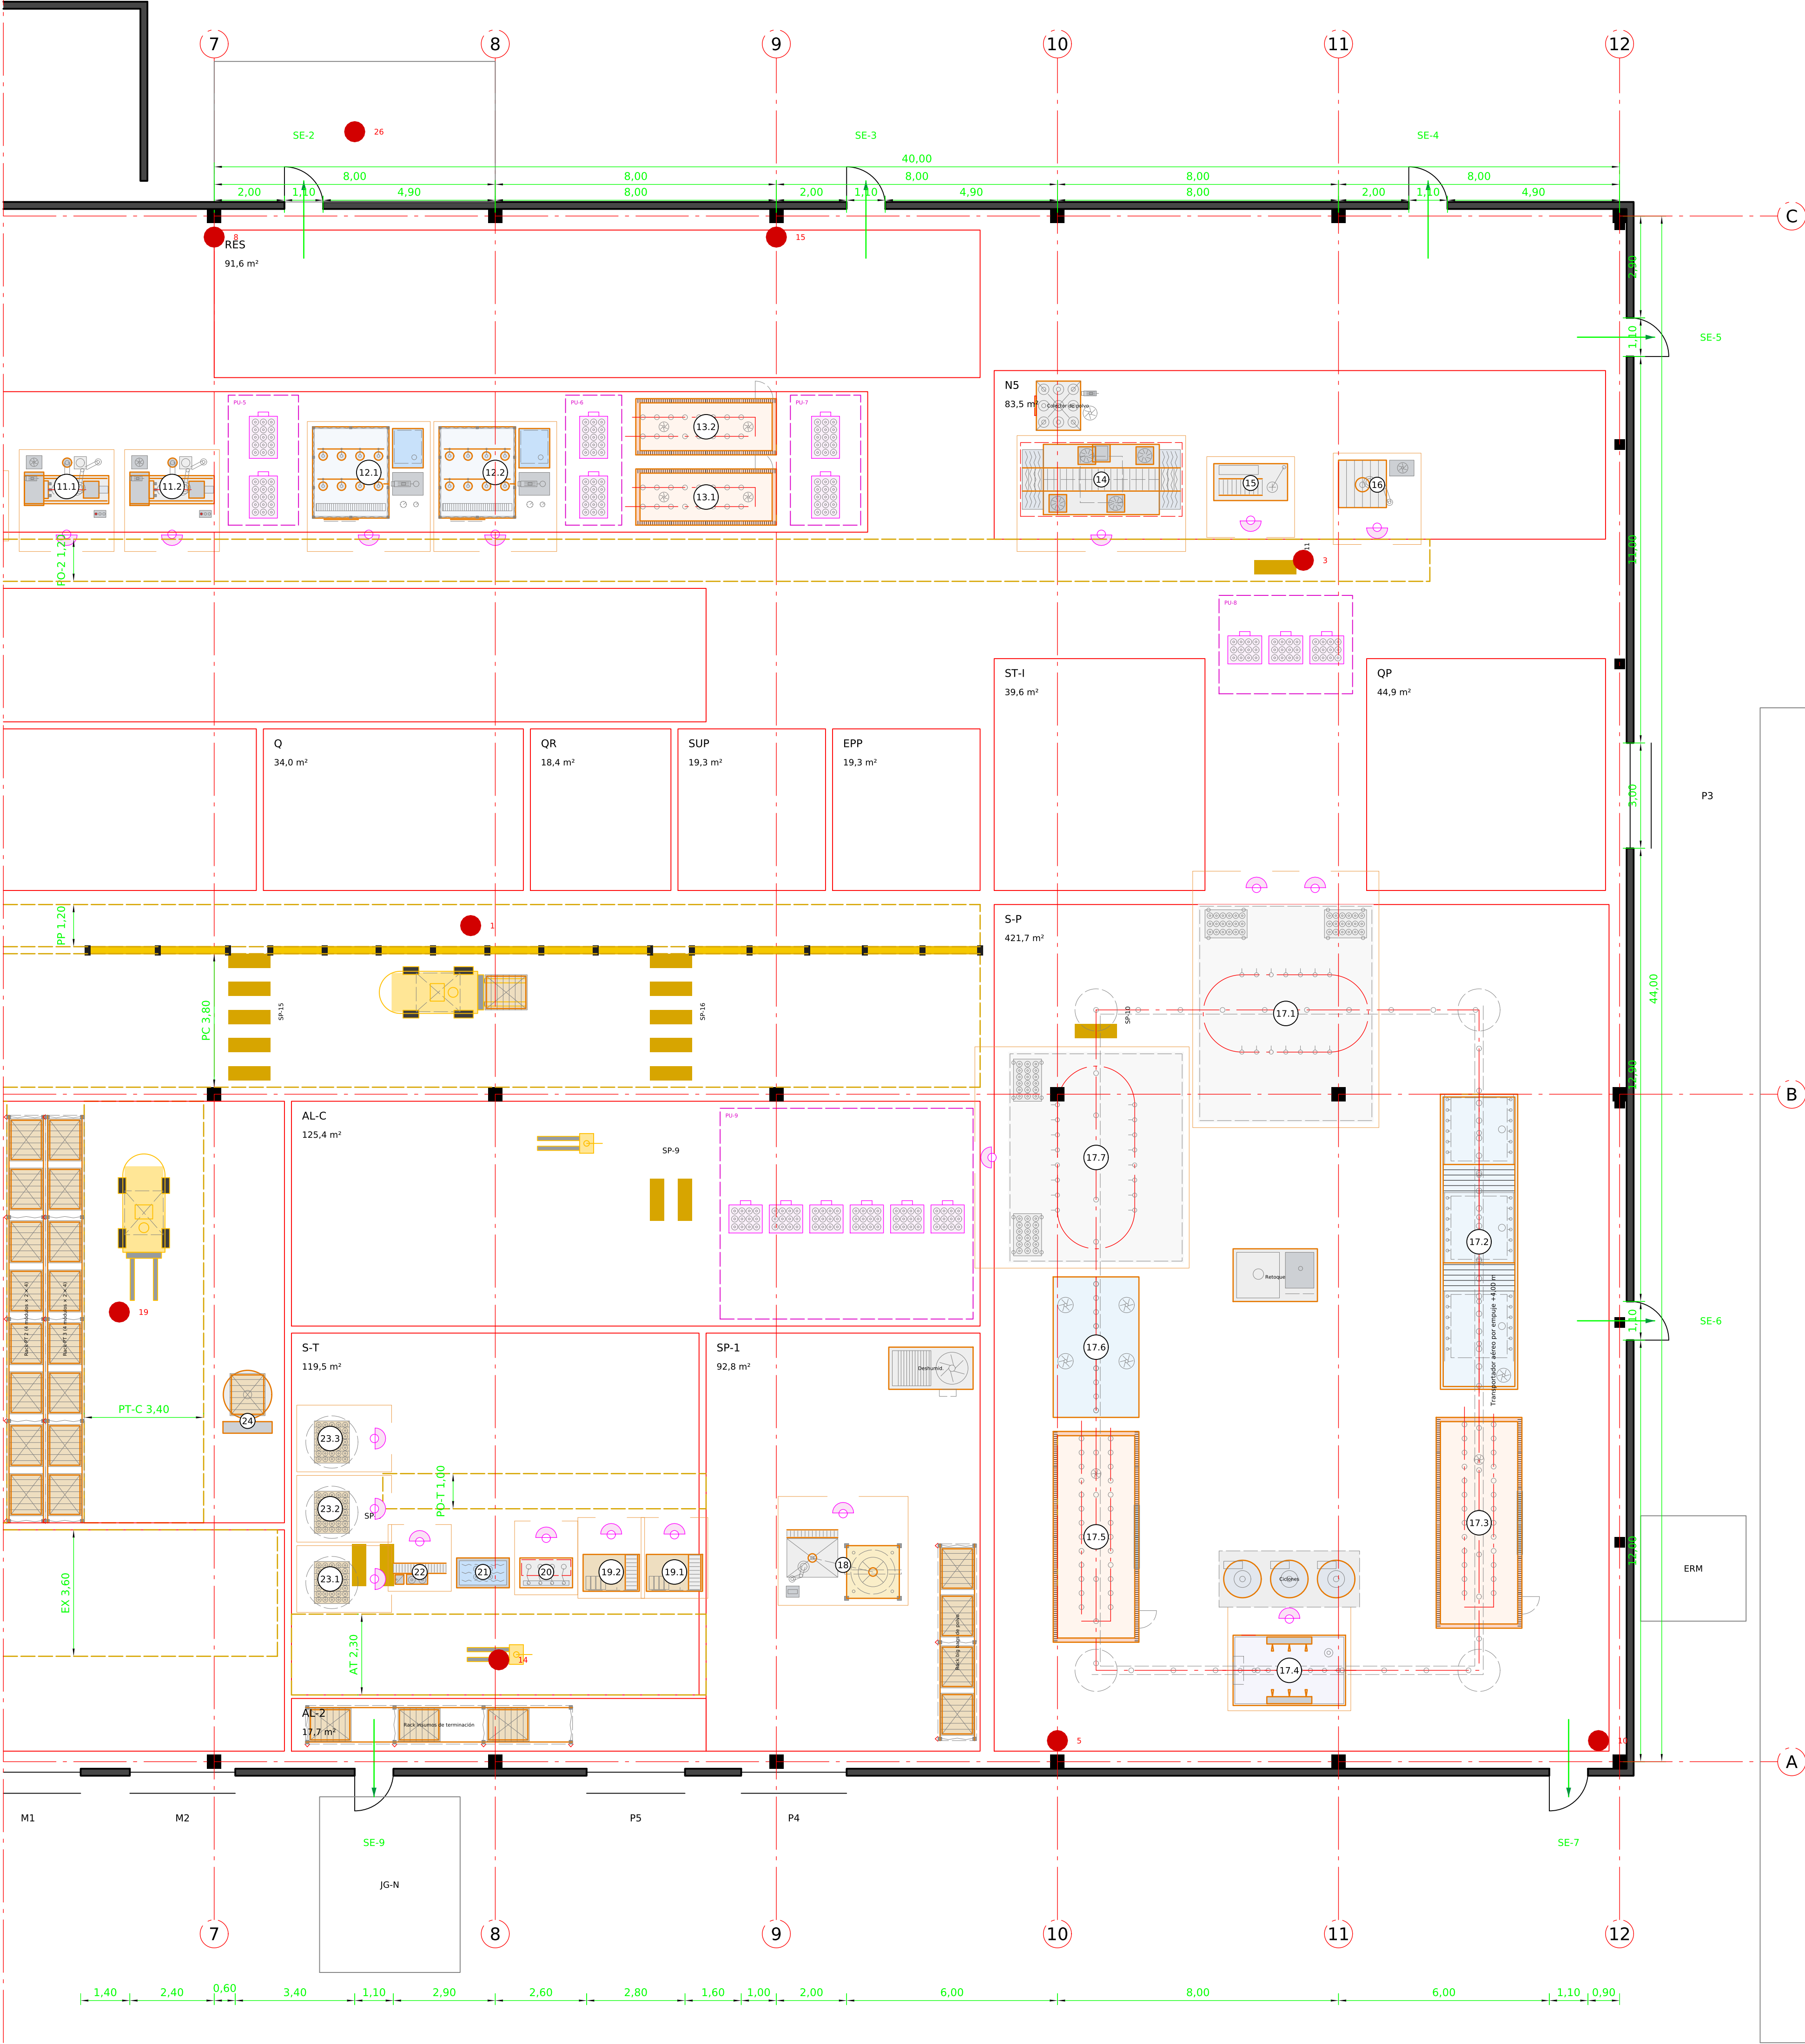

Equipos por paso (entero = operación; .1 .2 = máquinas iguales)

| Paso | Cód. | Equipo                            | Medidas m    | KW   | Op. | Fuente                                   |
|------|------|-----------------------------------|--------------|------|-----|------------------------------------------|
| 11.1 | A06  | Soldadura circ. copa y fondo      | 2,40 x 1,80  | 15,0 | 1   | Cota: Getwell                            |
| 11.2 | B06  | Soldadura circ. copa y fondo      | 2,40 x 1,80  | 15,0 | 1   | Cota: Schieding PRO WP130                |
| 12.1 | A07  | Puerta hidráulica automática      | 3,20 x 2,60  | 4,0  | 1   | Cota: Finesse PS-D12A                    |
| 12.2 | B07  | Puerta hidráulica automática      | 3,20 x 2,60  | 4,0  | 1   | Cota: Finesse PS-D12A                    |
| 13.1 | B14  | Secadora de cilindros             | 4,00 x 1,60  | 6,0  | -   | Estimado                                 |
| 13.2 | A11  | Secadora de cilindros             | 4,00 x 1,60  | 6,0  | -   | Estimado                                 |
| 14   | B08  | Granuladora de tonel              | 4,50 x 2,20  | 15,0 | 1   | Cota: Adhilet G-100                      |
| -    | B13  | Colector de polvo                 | 1,80 x 1,40  | 5,5  | -   | Estimado                                 |
| 15   | R09  | Detección de defectos             | 2,20 x 1,20  | 6,5  | 1   | Estimado                                 |
| 16   | B10  | Corrección de defectos            | 2,20 x 1,50  | 10,0 | 1   | Estimado                                 |
| 17.1 | P01  | Tren de carga                     | 5,00 x 6,20  | -    | 2   | Cota: Electrolor                         |
| 17.2 | P02  | Tonel de procesamiento (3 etapas) | 2,20 x 8,40  | 11,0 | -   | Estimado SP Ingeniería / Electrolor      |
| 17.3 | P03  | Horno de secado 6 x 2,44 m        | 2,44 x 6,00  | 3,0  | -   | Cota: Electrolor                         |
| 17.4 | P04  | Cabina de prueba y reciprocador   | 3,20 x 2,00  | 5,0  | 1   | Cota: Electrolor EC40-2000               |
| -    | P05  | Cilindros de recuperación         | 4,00 x 1,60  | 11,0 | -   | Cota: Electrolor                         |
| 17.5 | P06  | Horno de polimerizado 6 x 2,44 m  | 2,44 x 6,00  | 3,0  | -   | Cota: Electrolor                         |
| 17.6 | P07  | Enfriamiento                      | 2,44 x 4,00  | -    | -   | Estimado                                 |
| 17.7 | P08  | Tren de descarga                  | 5,00 x 6,00  | -    | 1   | Cota: Electrolor                         |
| -    | P09  | Retraje y control de espesor      | 2,40 x 1,60  | -    | -   | Estimado                                 |
| 18   | T01  | Carga de polvo 120 kg             | 3,40 x 2,00  | 3,0  | 1   | Cota: Ivam M000121 = estación de trabajo |
| -    | T15  | Desumidificador y extracción      | 2,40 x 1,20  | 6,0  | -   | Estimado                                 |
| -    | R05  | Rack de big bags de polvo         | 1,10 x 5,60  | -    | -   | Estimado                                 |
| 19.1 | T03  | Ensamblaje de válvula             | 1,60 x 1,20  | 0,5  | 1   | Estimado                                 |
| 19.2 | T04  | Ensamblaje de válvula             | 1,60 x 1,20  | 0,5  | 1   | Estimado                                 |
| 20   | T05  | Presurización con N <sub>2</sub>  | 1,50 x 1,00  | 0,5  | 1   | Cota: Valcon M000150                     |
| 21   | T06  | Hermeticidad                      | 1,50 x 1,00  | 0,5  | -   | Estimado                                 |
| 22   | T07  | Etiquetado y automatizada         | 1,50 x 0,80  | 0,5  | 1   | Cota: SISA                               |
| 23.1 | T08  | Embalaje y palletizado            | 1,60 x 1,60  | -    | 1   | Estimado                                 |
| 23.2 | T09  | Embalaje y palletizado            | 1,60 x 1,60  | -    | 1   | Estimado                                 |
| 23.3 | T10  | Palletizado de cilindros vendidos | 1,60 x 1,60  | -    | 1   | Estimado                                 |
| -    | R00  | Rack de insumos de terminación    | 7,60 x 1,10  | -    | -   | Estimado                                 |
| 24   | T11  | Envoltorio de pallets             | 1,50 x 2,00  | 1,5  | -   | Cota: EDOS P05                           |
| -    | R02  | Rack de PT 2 (4 módulos x 2 x 4)  | 1,10 x 11,60 | -    | -   | Estimado                                 |
| -    | R03  | Rack de PT 3 (4 módulos x 2 x 4)  | 1,10 x 11,60 | -    | -   | Estimado                                 |

Referencias: cada equipo se dibuja en planta a escala con sus partes (bastidor, rodillos, montajes, motores, tableros), resguardos en rojo y aperturas en su punto (magenta); en trazos, partes elevadas; óvalo = código del equipo; círculo rojo = barrido de pluma; líneas amarillas = demarcación de pasillos (IRAM 10005); color = senda peatonal; punto rojo numerado = extintor ABC 10 kg (IRAM 3517-2; recorrido ≤ 20 m); flecha verde = salida de emergencia 1.10 m con barril antipánico.

|          |            |             |                        |                               |
|----------|------------|-------------|------------------------|-------------------------------|
|          | Fecha      | Nombre      | Propietario            | Reemplaza a / Reemplazado por |
| Dibujó   | 02/10/2026 | Claude Code | FLAMA S.A.             | -                             |
| Revisó   |            |             | Denominación           | Material                      |
| Aprobó   |            |             | Planta de la nave este | Estructura metálica           |
| Escala   | 1:100      | Formato     | ISO E                  | Edición                       |
| Unidades | Cotas en m | A0          | Plano de planta        | 0                             |
|          |            |             |                        | Fecha de emisión              |
|          |            |             |                        | 02/10/2026                    |
|          |            |             |                        | Hoja                          |
|          |            |             |                        | 3 / 4                         |
|          |            |             |                        | es                            |
|          |            |             |                        | Nº de plano                   |
|          |            |             |                        | FL_PI_04                      |


FL\_PI\_04 - PLANO FORMAL NORMALIZADO - HOJA 4: SERVICIOS, SANITARIOS Y CORTE

Planta del bloque de servicios 1:50; sanitario accesible 1:20; corte transversal de la nave 1:100. Cotas en metros.


BLOQUE DE SERVICIOS AL PERSONAL Y OFICINAS - 1:50



Inodoro a 0,45-0,50 m de altura; eje a 0,45 m del muro con barra fija; espacio lateral libre  $\geq$  0,80 m del lado de transferencia con barra rebatible; lavatorio sin pie a 0,80-0,85 m; espejo inclinado; puerta de 0,90 m que abre hacia afuera; accionamiento de canilla por palanca; timbre de emergencia.

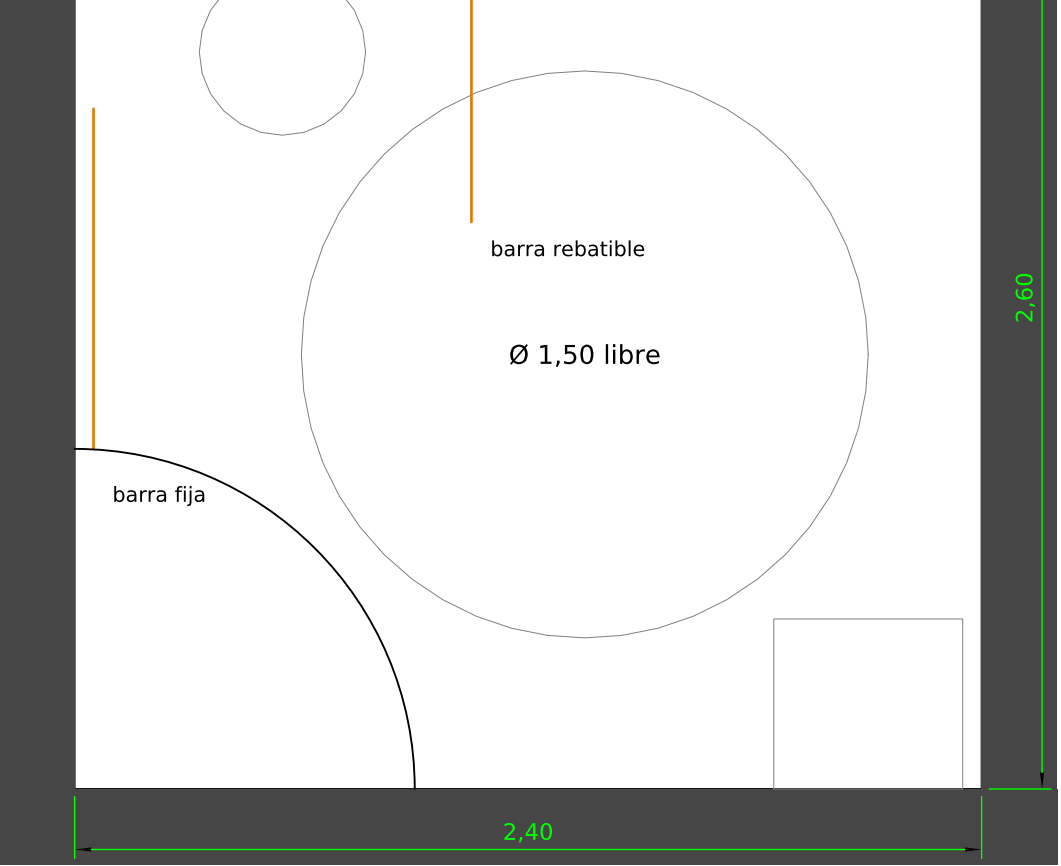

CORTE TRANSVERSAL A-A (por eje 4) - 1:100

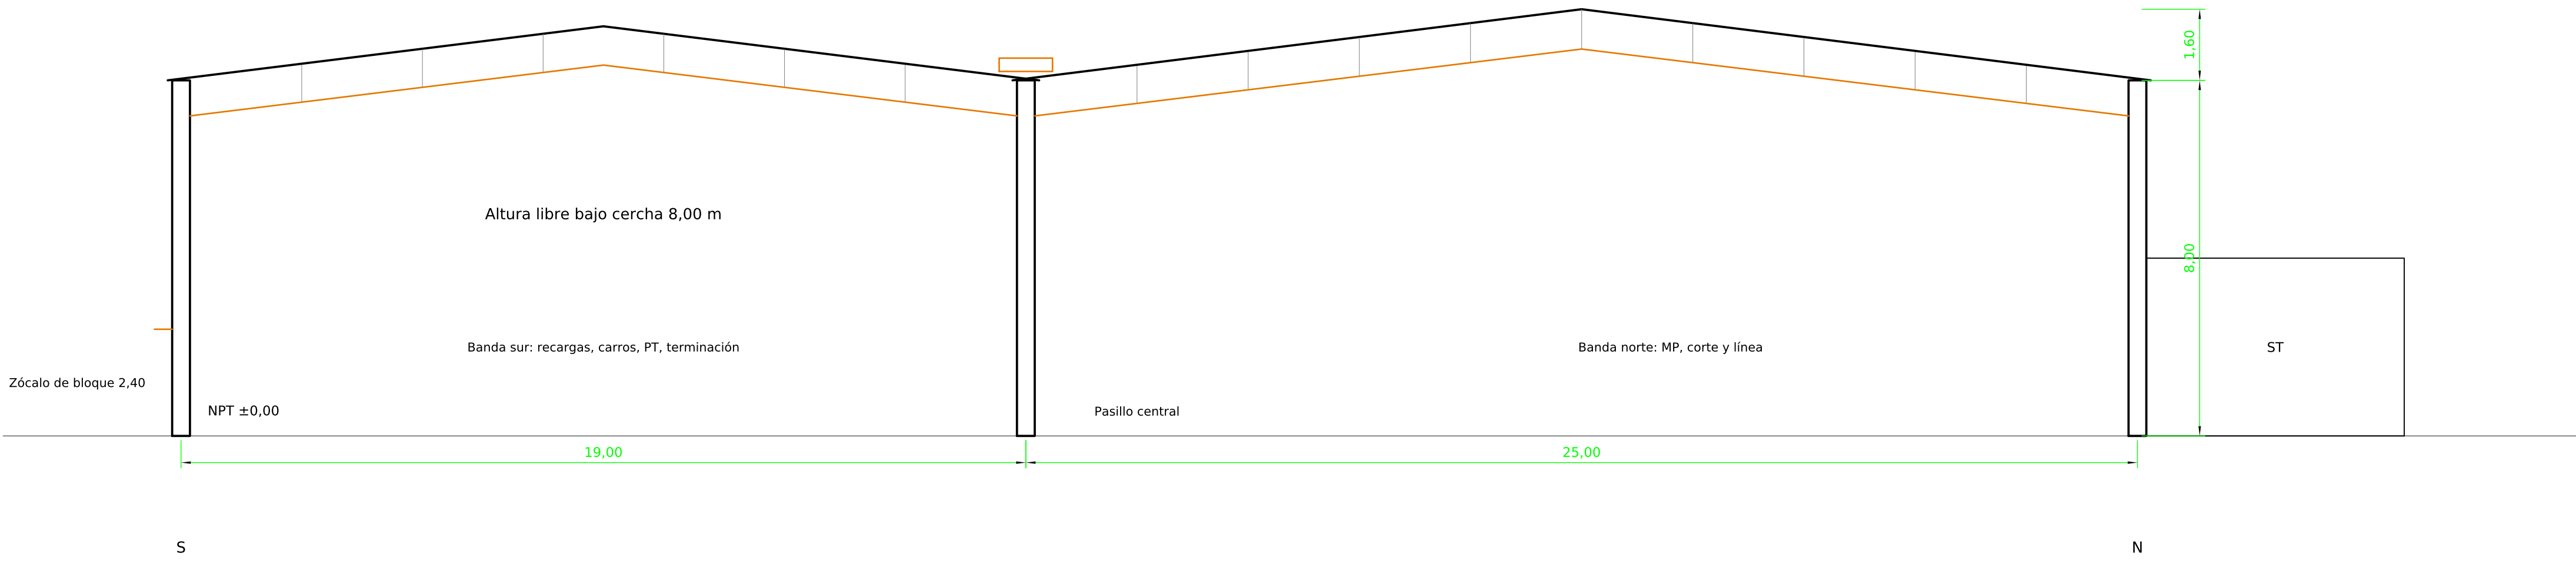

Locales de servicios y recargas

| Local                                                        | m²   | Equipamiento                                                                |
|--------------------------------------------------------------|------|-----------------------------------------------------------------------------|
| SV-VH Vestuario hombres (62 armarios)                        | 40,0 |                                                                             |
| SV-SH Sanitarios y duchas hombres                            | 29,8 | 1 Inodoros, 6 mingitorios, 6 lavabos, 4 duchas                              |
| SV-LU Limpieza                                               | 9,0  |                                                                             |
| SV-PS Paso a planta                                          | 6,6  |                                                                             |
| SV-VH Vestuario y sanitarios mujeres (14 armarios)           | 40,0 | 2 Inodoros, 2 lavabos, 2 duchas                                             |
| SV-AC Sanitario accesible                                    | 6,2  | Círculo libre Ø 1,50 m, barras, inodoro con 0,80 m libre later              |
| SV-LA Lactario                                               | 6,2  | Buena práctica (Ley 26.873)                                                 |
| SV-PA Primeros auxilios                                      | 29,2 |                                                                             |
| SV-CO Pasillo                                                | 33,5 |                                                                             |
| SV-HA Hall, recepción y fichado                              | 28,1 |                                                                             |
| SV-OF Oficinas (6 puestos)                                   | 28,1 |                                                                             |
| SV-JP Jefatura de planta                                     | 7,6  |                                                                             |
| SV-RE Reuniones                                              | 6,8  |                                                                             |
| SV-CN Comedor 30 plazas y office                             | 39,4 |                                                                             |
| RC-RE Recepción, clasificación y recibidos                   | 26,0 | Clasificación en 4 colas: polvo, CO <sub>2</sub> , agente limpio y líquidos |
| RC-DE Desarme y lavado                                       | 28,4 |                                                                             |
| RC-OC Odiscapa y ensayo de funcionamiento                    | 28,4 | Sala con extracción y recuperación de polvo                                 |
| RC-C1 Corredor de recargas (suri)                            | 24,2 |                                                                             |
| RC-GA CO <sub>2</sub> y agente limpio                        | 16,3 | Trasvasador y balanza                                                       |
| RC-PV Recinto de polvo (H <sub>2</sub> a 70 %)               | 32,6 | Carga ABC, BC y D; 8 renovaciones por hora; sin estufas                     |
| RC-PH PH con jaula, secado y Puffer                          | 18,5 |                                                                             |
| RC-C2 Corredor de recargas (centro)                          | 22,0 |                                                                             |
| RC-CN Conector al pasillo central                            | 18,5 |                                                                             |
| RC-IR Inutilizados y residuos                                | 8,9  |                                                                             |
| RC-OP Despacho y equipos para entregar                       | 9,6  |                                                                             |
| RC-EN Ensamblaje, presentación, peso, hermeticidad y retaque | 38,5 |                                                                             |
| RC-LO Líquidos                                               | 10,1 | Agua, AFFF y clase K                                                        |
| RC-NP Etiquetado y lista de intercambio                      | 10,9 |                                                                             |

Pisos lavables y antideslizantes; revestimiento sanitario hasta 2,30 m; ventilación natural o mecánica; agua caliente y fría en duchas y lavabos (Dec. 351/75 cap. 3); altura mínima de locales 3,00 m; separación por sexo con acceso independiente; vestuarios contiguos a los sanitarios (art. 20). Paso a planta PP-1, directo al pasillo central de personal.

|          |            |                      |                        |                                                    |
|----------|------------|----------------------|------------------------|----------------------------------------------------|
|          | Fecha      | Nombre               | Propietario            | Reemplaza a / Reemplazado por                      |
| Dibujó   | 02/10/26   | Claude Code          | FLAMA S.A.             | -                                                  |
| Revisó   |            |                      | Denominación           | Materia                                            |
| Aprobó   |            |                      | Servicios y sanitarios | Mampostería / estructura metálica                  |
| Escala   | 1:50       | Método de proyección | Formato                | Edición                                            |
| Unidades | Cotas en m | Formato              | A0                     | 0                                                  |
|          |            |                      |                        | 02/10/2026                                         |
|          |            |                      |                        | 4 / 4                                              |
|          |            |                      |                        | es                                                 |
|          |            |                      |                        | Planta 1:50, sanitario accesible 1:20, corte 1:100 |
|          |            |                      |                        | Plano de detalle                                   |
|          |            |                      |                        | FL_PI_04                                           |